


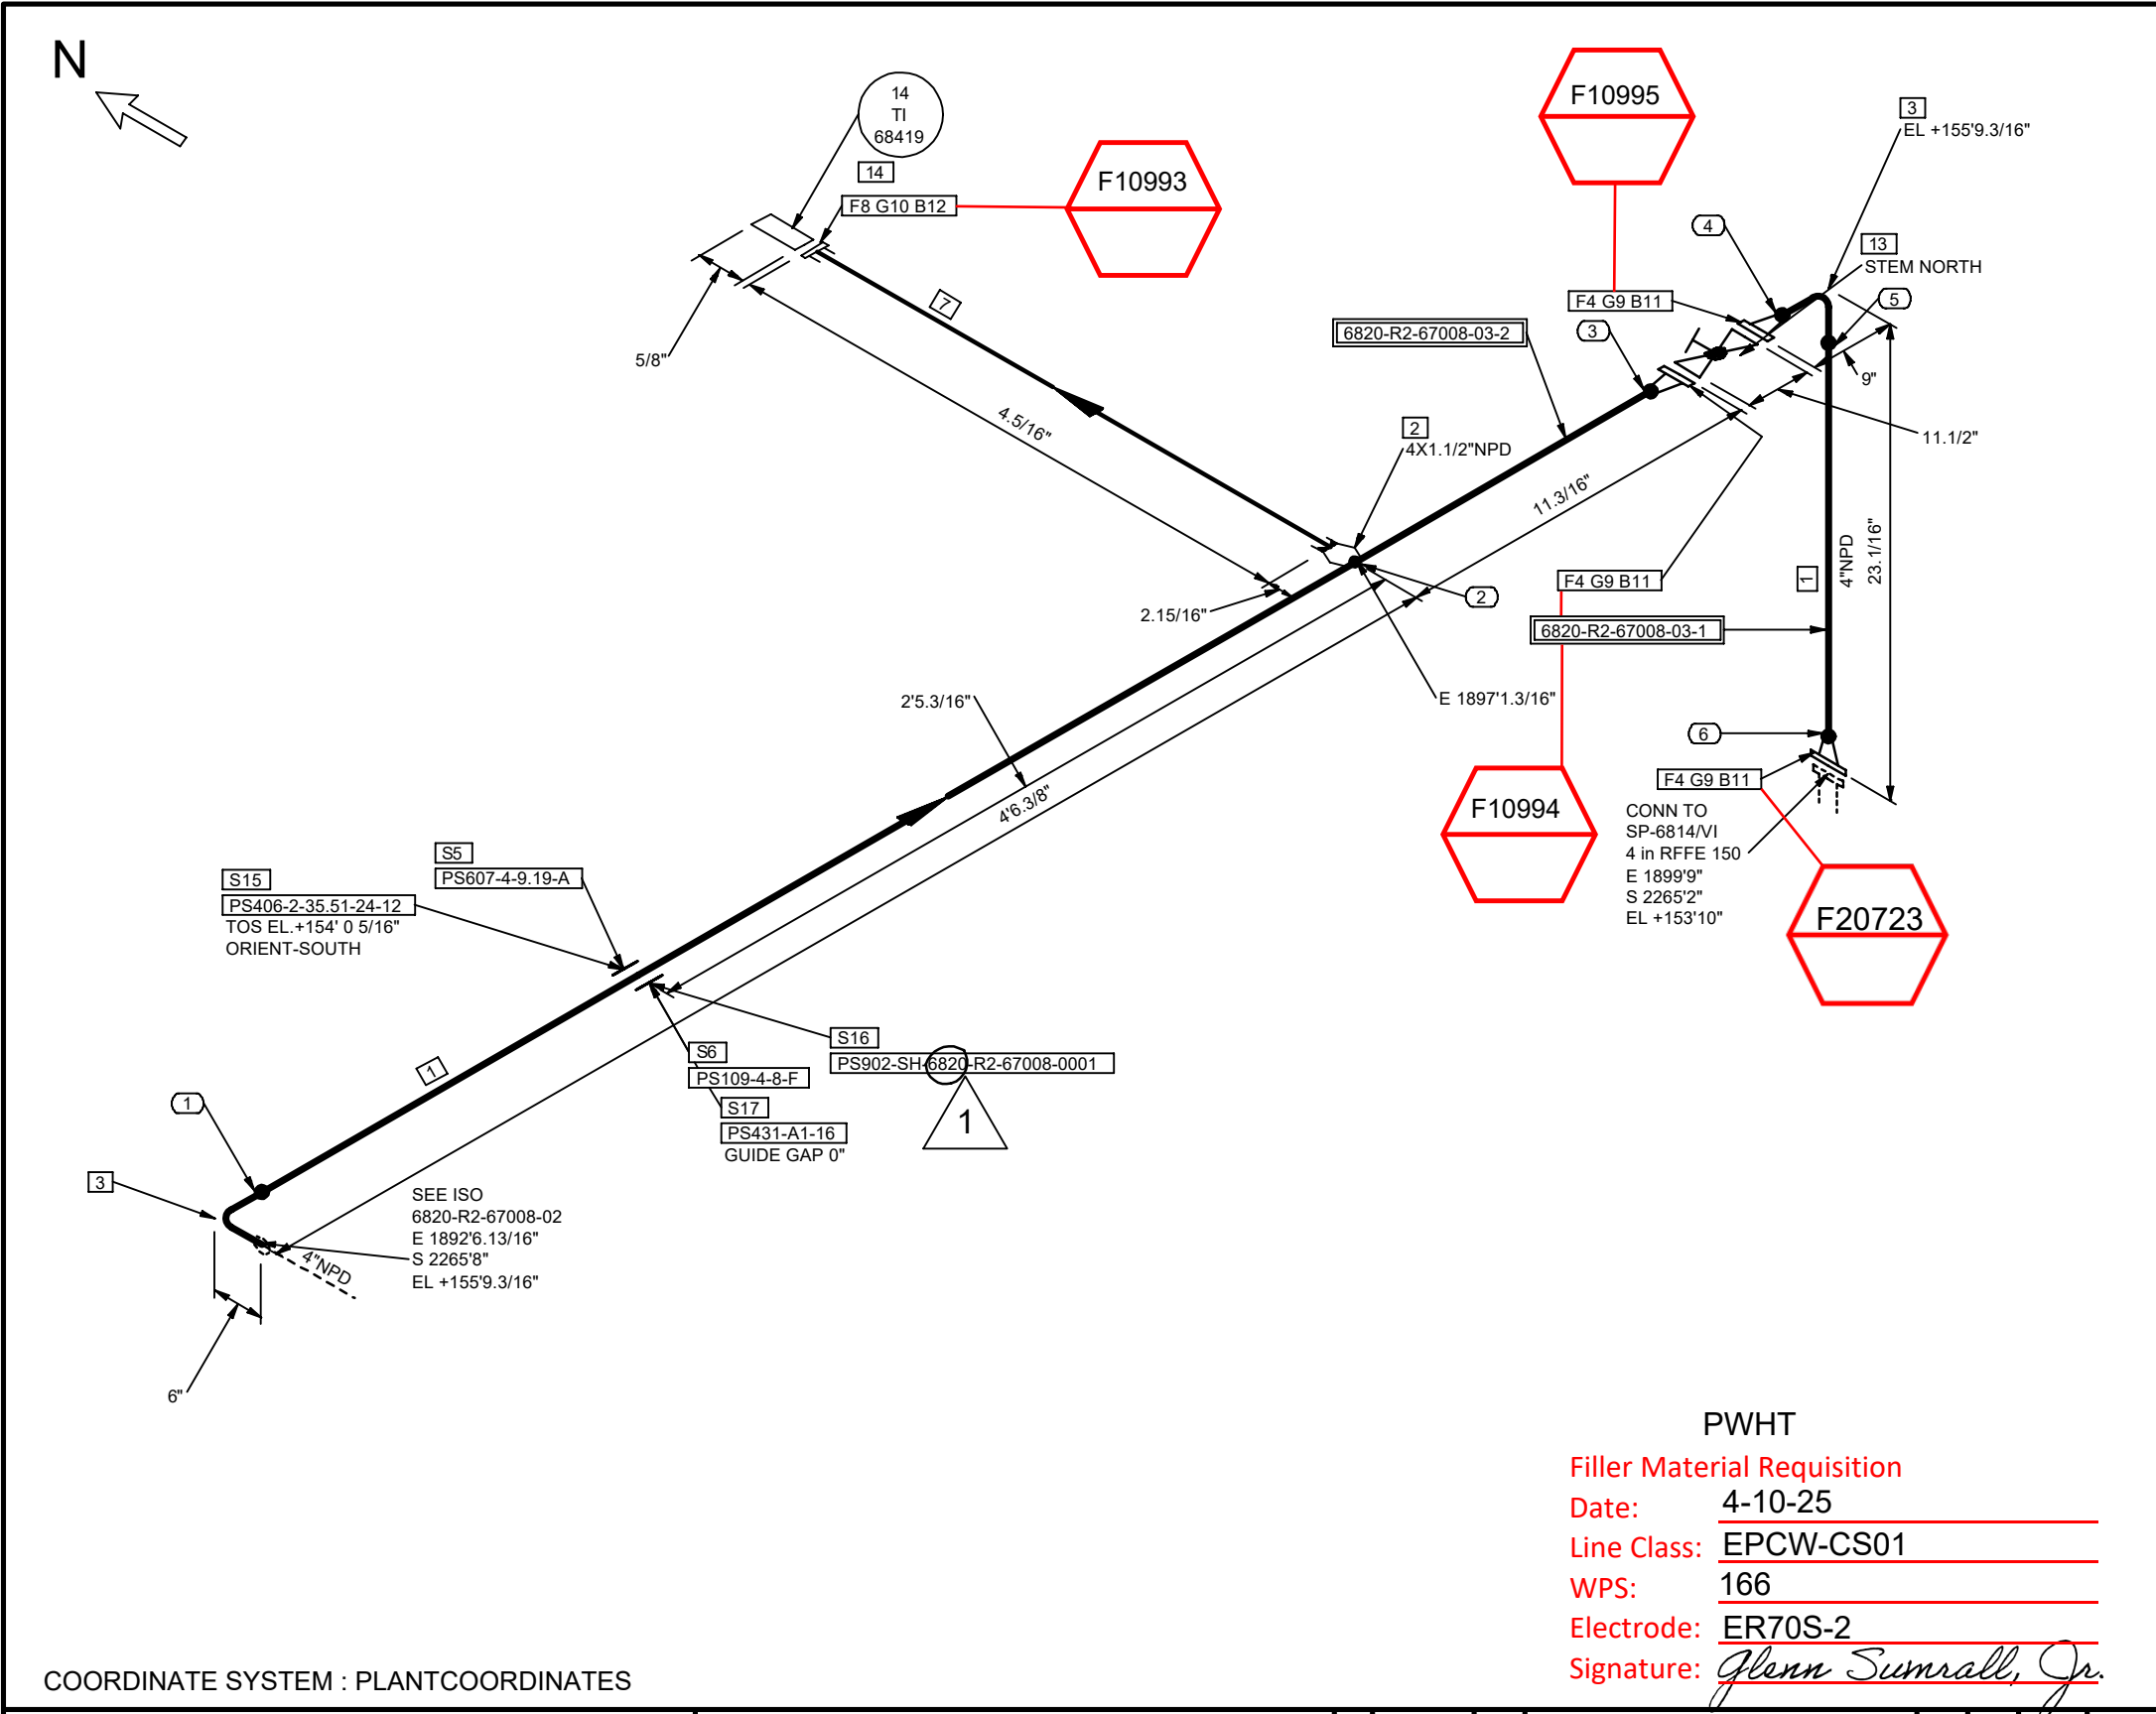

COORDINATE SYSTEM : PLANTCOORDINATES

PWHT
Filler Material Requisition
Date: 4-10-25
Line Class: EPCW-CS01
WPS: 166
Electrode: ER70S-2
Signature: *Glenn Sumrall, Jr.*

SHOP MATERIALS							
NO	NPD	DESCRIPTION	IDENT	QTY			
1	4	Pipes, Seamless, ASME B36.10, ASTM A106 Gr.B, BE, -, -, S-STD	CPP0AAXH	5.9 '			
2	4X1.1/2	Threadolet, ASTM A105N, 3000 Lbs, NPTF Ends, -, -,	CLT8TVLU	1			
3	4	90° Elb LR, Seamless, ASME B16.9, ASTM A234 Gr.WPB, BW Ends, -, -, S-STD	CDB66GLS	2			
4	4	WN Flg, ASME B16.5, ASTM A105N, 150 Lbs, RF/BW End, -, S-STD	CFG6WJF4	3			
PIPE SUPPORTS							
5	4	PS607-4-9.19-A	PS607	1			
6	4	PS109-4-8-F	PS109	1			
OTHER THAN SHOP MATERIALS							
NO	NPD	DESCRIPTION	IDENT	QTY			
7	1.1/2	Pipes, Seamless, ASME B36.10, ASTM A106 Gr.B, NPTM Ends, w/ coupling, -, S-XS	CEZCLVN	0.4 '			
8	1.1/2	THD Flg, ASME B16.5, ASTM A105N, 150 Lbs, RF/NPTF End, -,	CFG8U740	1			
9	4	NM Flat Gk, Barium Sulfate filled PTFE, 150 Lbs, RF as per ASME B16.5, Full Face, Thk=1/8in, -,	C7CT1ZFZ	3			
10	1.1/2	NM Flat Gk, Barium Sulfate filled PTFE, 150 Lbs, RF as per ASME B16.5, Full Face, Thk=1/8in, -,	C7CT1ZFK	1			
11	5/8	SBlt 2 HHx N, A193 Gr.B7/A194 Gr.2H, -, Xylan PTFE Coated, - 3.75 in. Length	C6S4K88S	24			
12	1/2	SBlt 2 HHx N, A193 Gr.B7/A194 Gr.2H, -, Xylan PTFE Coated, - 3 in. Length	C6S4K87V	4			
13	4	Glo Flg, API 623, ASTM A216 Gr.WCB, 150 Lbs, RF, Ends as per ASME B16.5, HO,-, Valve Tag: GL-0627	C84KV7D0	1			
INSTRUMENTS							
14	1.1/2	14-TI-68419	14-TI-68419	1			
PIPE SUPPORTS							
15	4	PS406-2-35.51-24-12	PS406	1			
16	4	PS902-SH-6820-R2-67008-0001	PS902	1			
17	4	PS431-A1-16	PS431	1			
PIECE MARKS							
6820-R2-67008-03-1 6820-R2-67008-03-2							
Turner Industries Group, LLC Received APRIL 10, 2025 DOCUMENT CONTROL							
SERVICE:	VAPOR/LIQUID:	INSUL TYPE:	INSUL THK:	SHOP:	FIELD:	PAINT CODE:	MODULE:
R2	V	Per LDT	Per LDT	Y	Y	Per LDT	-
 P&ID: 202998C-001-PID-0021-0320 UNIT#: 6800 EWIP AREA: 6820 SPEC: EPCW-CS01 STRESS CALC #: CN-0383 LINE No: 4"-R2-67008-EPCW-CS01-H DRAWING NUMBER 6820-R2-67008-03 REV. 1 OxyChem Redstone Battleground PROJECT							

NOTES:
1. FOR LINE PRESSURES, TEMPERATURES, INSULATION TYPE AND THICKNESS, ETC. REFER TO LATEST REVISION OF LDT.
2. FOR STANDARD PIPE SUPPORT DETAILS SEE PROJECT STANDARD.
3. FIELD SHIM TO SUIT UNLESS OTHERWISE NOTED.
4. FOR PWHT REQUIREMENTS REFER TO LINE CLASS SPECIFICATION.
5. ALL THREADED PIPE LINE SYSTEMS, FIELD SHALL VERIFY DIMENSION PRIOR TO ERECTION.
6. FFW DESIGNATION AT WELDS INDICATES FIELD FIT WELD, WHERE PIPE FABRICATOR IS TO ADD 9 INCH OF PIPE TO THE ISOMETRIC DIMENSION TO ENABLE THE FIELD TO CUT TO FIT AT SITE.
7. REFER TO 202998C-000-W1-1300-0001 FOR FRP AND DUAL-LAM FABRICATION.

T.EN

TECHNIP ENERGIES

Information contained in this document is the work product of one or more legal entities of Technip Energies N.V. and embodies confidential and proprietary information of the applicable entity and/or its client. Use of this information is restricted in accordance with conditions specified by the contract. Technip Energies N.V. and its affiliates disclaim any and all liabilities for any changes or modifications to this document which are made by any person other than the entity that issued the document under the applicable client contract.

THIS DOCUMENT IS UNCONTROLLED WHEN REPRODUCED

REV	DATE	BY	DESCRIPTION	CHKD	MTO	STRESS	APRVD
1	2025-04-04	RVA	ISSUED FOR CONSTRUCTION	SAD	KJK	SMR	GR
0	2024-11-15	RVA	ISSUED FOR CONSTRUCTION	SAD	KJK	SMR	GR

