


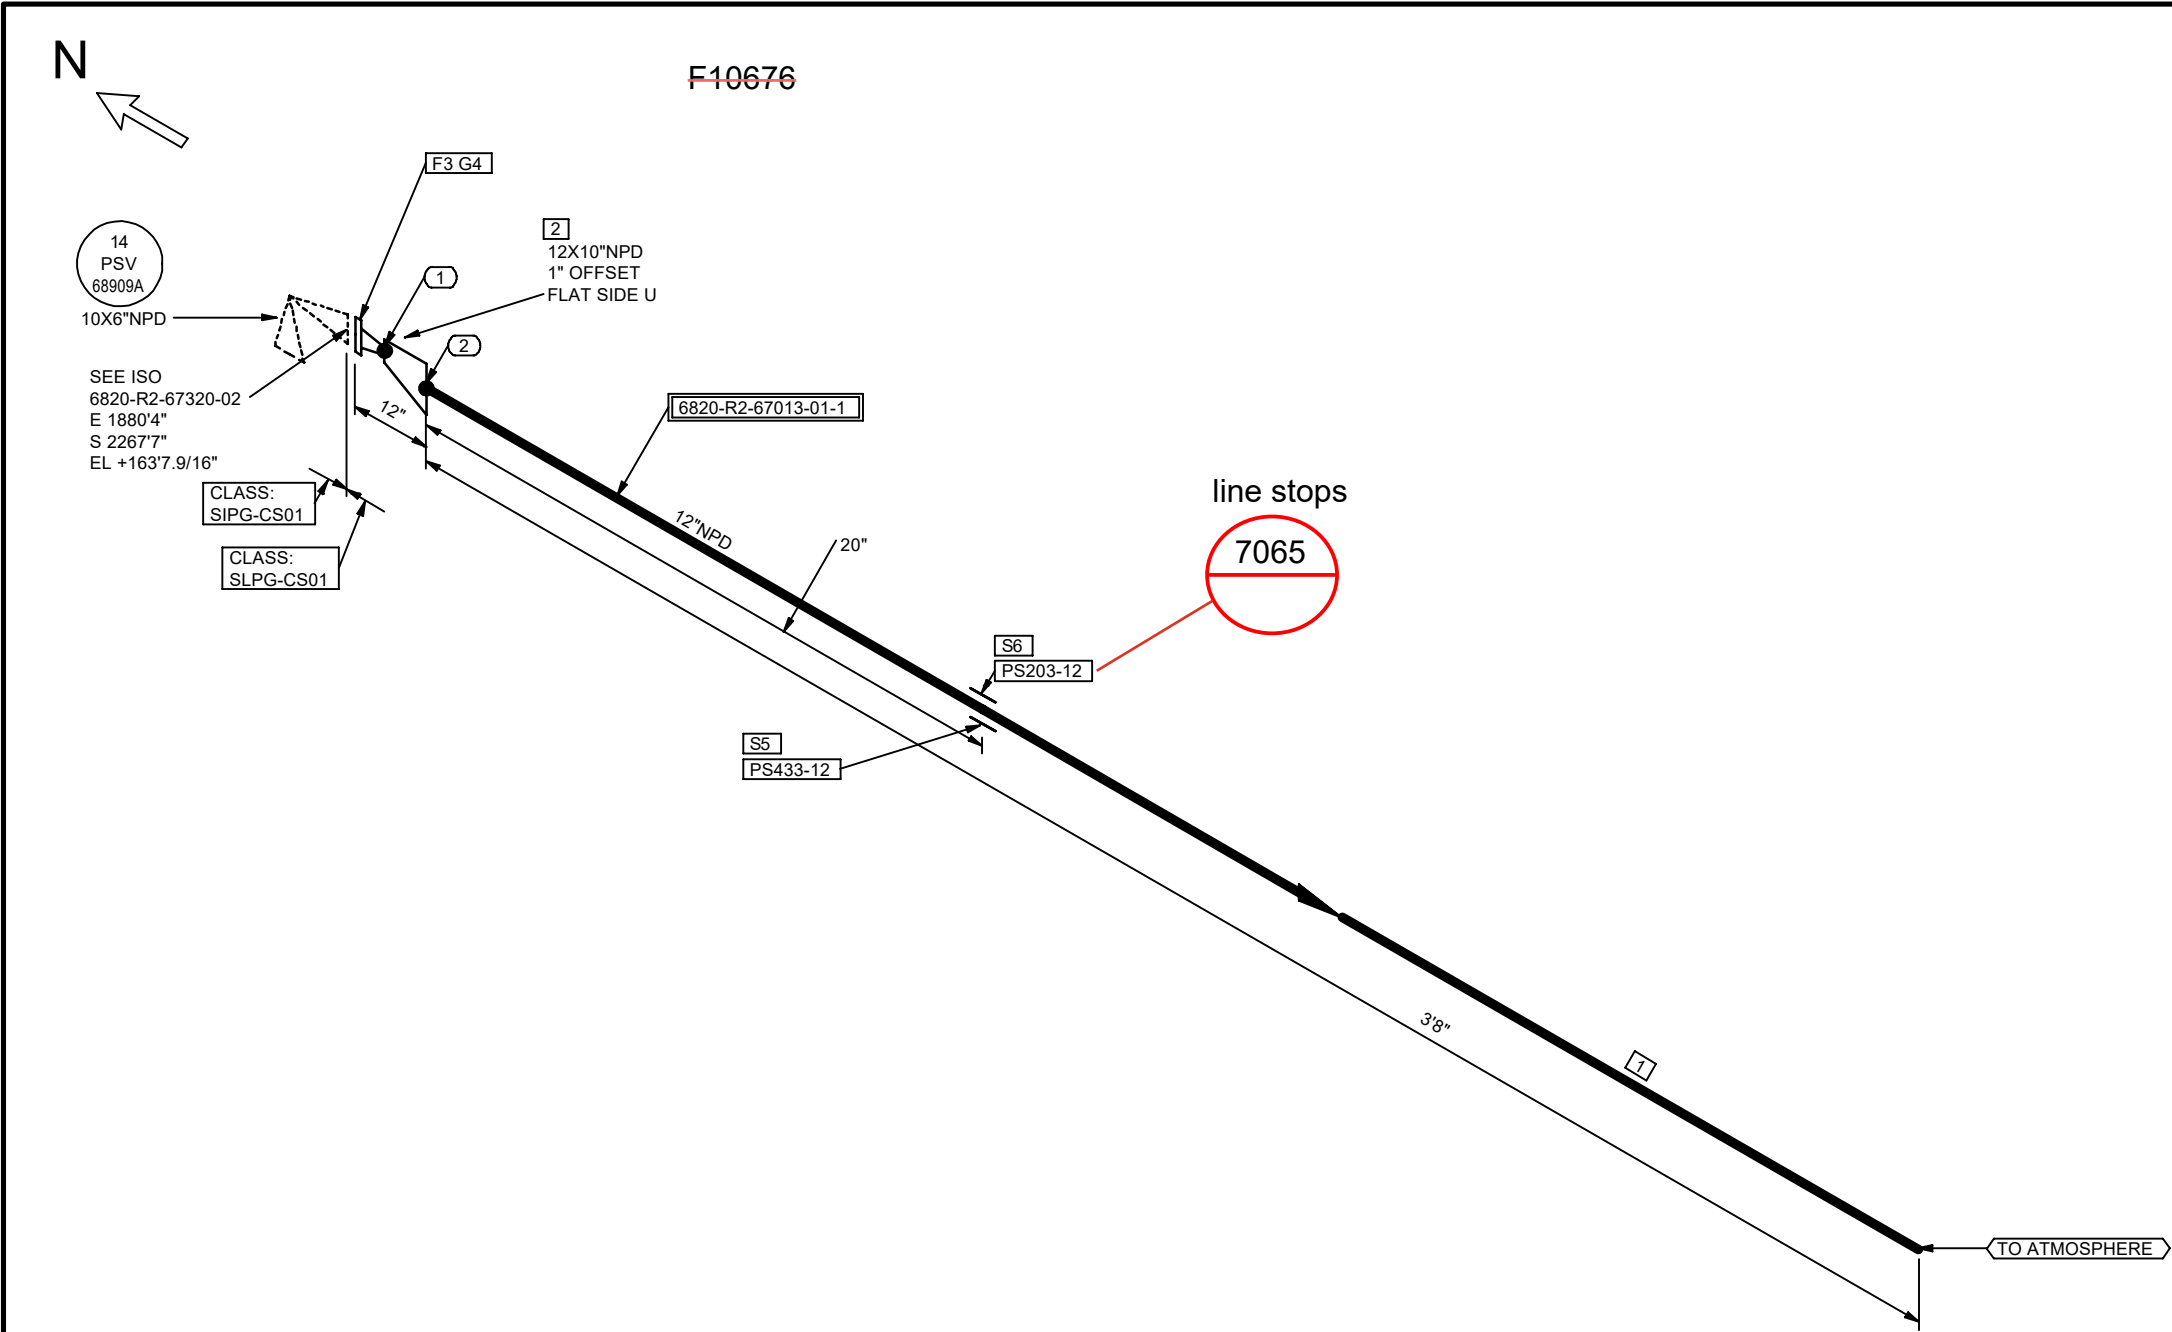

SHOP MATERIALS				
NO	NPD	DESCRIPTION	IDENT	QTY
1	12	Pipes, Seamless, ASME B36.10, ASTM A106 Gr.B, BE, -, -, S-STD	CPP0AATK	3.7 '
2	12X10	Ecc Reducer, Seamless, ASME B16.9, ASTM A234 Gr.WPB, BW Ends, -, -, S-STD	CDB6BF3G	1
3	10	WN Flg, ASME B16.5, ASTM A105N, 150 Lbs, RF/BW End, -, S-STD	CFG6WJ2C	1
OTHER THAN SHOP MATERIALS				
NO	NPD	DESCRIPTION	IDENT	QTY
4	10	NM Flat Gk, Aramid Fiber Reinforced SBR, 150 Lbs, RF as per ASME B16.5, -, Thk=1/8in, -,	C7SMNYW4	1
PIPE SUPPORTS				
5	12	PS433-12	PS433	1
6	12	PS203-12	PS203	1
PIECE MARKS				
6820-R2-67013-01-1				

COORDINATE SYSTEM : PLANTCOORDINATES

Filler Material Requisition

Date: 12-3-24

Line Class: SLPG-CS01

WPS: 10245

Electrode: ER70S-2

Signature: *Glenn Sumrall Jr*

NOTES:

1. FOR LINE PRESSURES, TEMPERATURES, INSULATION TYPE AND THICKNESS, ETC. REFER TO LATEST REVISION OF LDT.

2. FOR STANDARD PIPE SUPPORT DETAILS SEE PROJECT STANDARD.

3. FIELD SHIM TO SUIT UNLESS OTHERWISE NOTED.

4. FOR PWHT REQUIREMENTS REFER TO LINE CLASS SPECIFICATION.

5. ALL THREADED PIPE LINE SYSTEMS, FIELD SHALL VERIFY DIMENSION PRIOR TO ERECTION.

6. FFW DESIGNATION AT WELDS INDICATES FIELD FIT WELD, WHERE PIPE FABRICATOR IS TO ADD 9 INCH OF PIPE TO THE ISOMETRIC DIMENSION TO ENABLE THE FIELD TO CUT TO FIT AT SITE.

7. REFER TO 202998C-000-W1-1300-0001 FOR FRP AND DUAL-LAM FABRICATION.

T.EN

TECHNIP ENERGIES

Information contained in this document is the work product of one or more legal entities of Technip Energies N.V. and embodies confidential and proprietary information of the applicable entity and/or its client. Use of this information is restricted in accordance with conditions specified by the contract. Technip Energies N.V. and its affiliates disclaim any and all liabilities for any changes or modifications to this document which are made by any person other than the entity that issued the document under the applicable client contract.

THIS DOCUMENT IS UNCONTROLLED WHEN REPRODUCED

REV	DATE	BY	DESCRIPTION	CHKD	MTO	STRESS	APRVD
0	2024-11-15	RVA	ISSUED FOR CONSTRUCTION	SAD	KJK	SMR	GR

OXY

OxyChem Redstone Battleground PROJECT

P&ID:

202998C-001-PID-0021-0320

UNIT#:

6800

EWPA AREA:

6820

SPEC:

SLPG-CS01

STRESS CALC #:

CN-0413

LINE No.

12"-R2-67013-SLPG-CS01-P

DRAWING NUMBER

6820-R2-67013-01

REV.

0

23 NOV 2024 06:43