


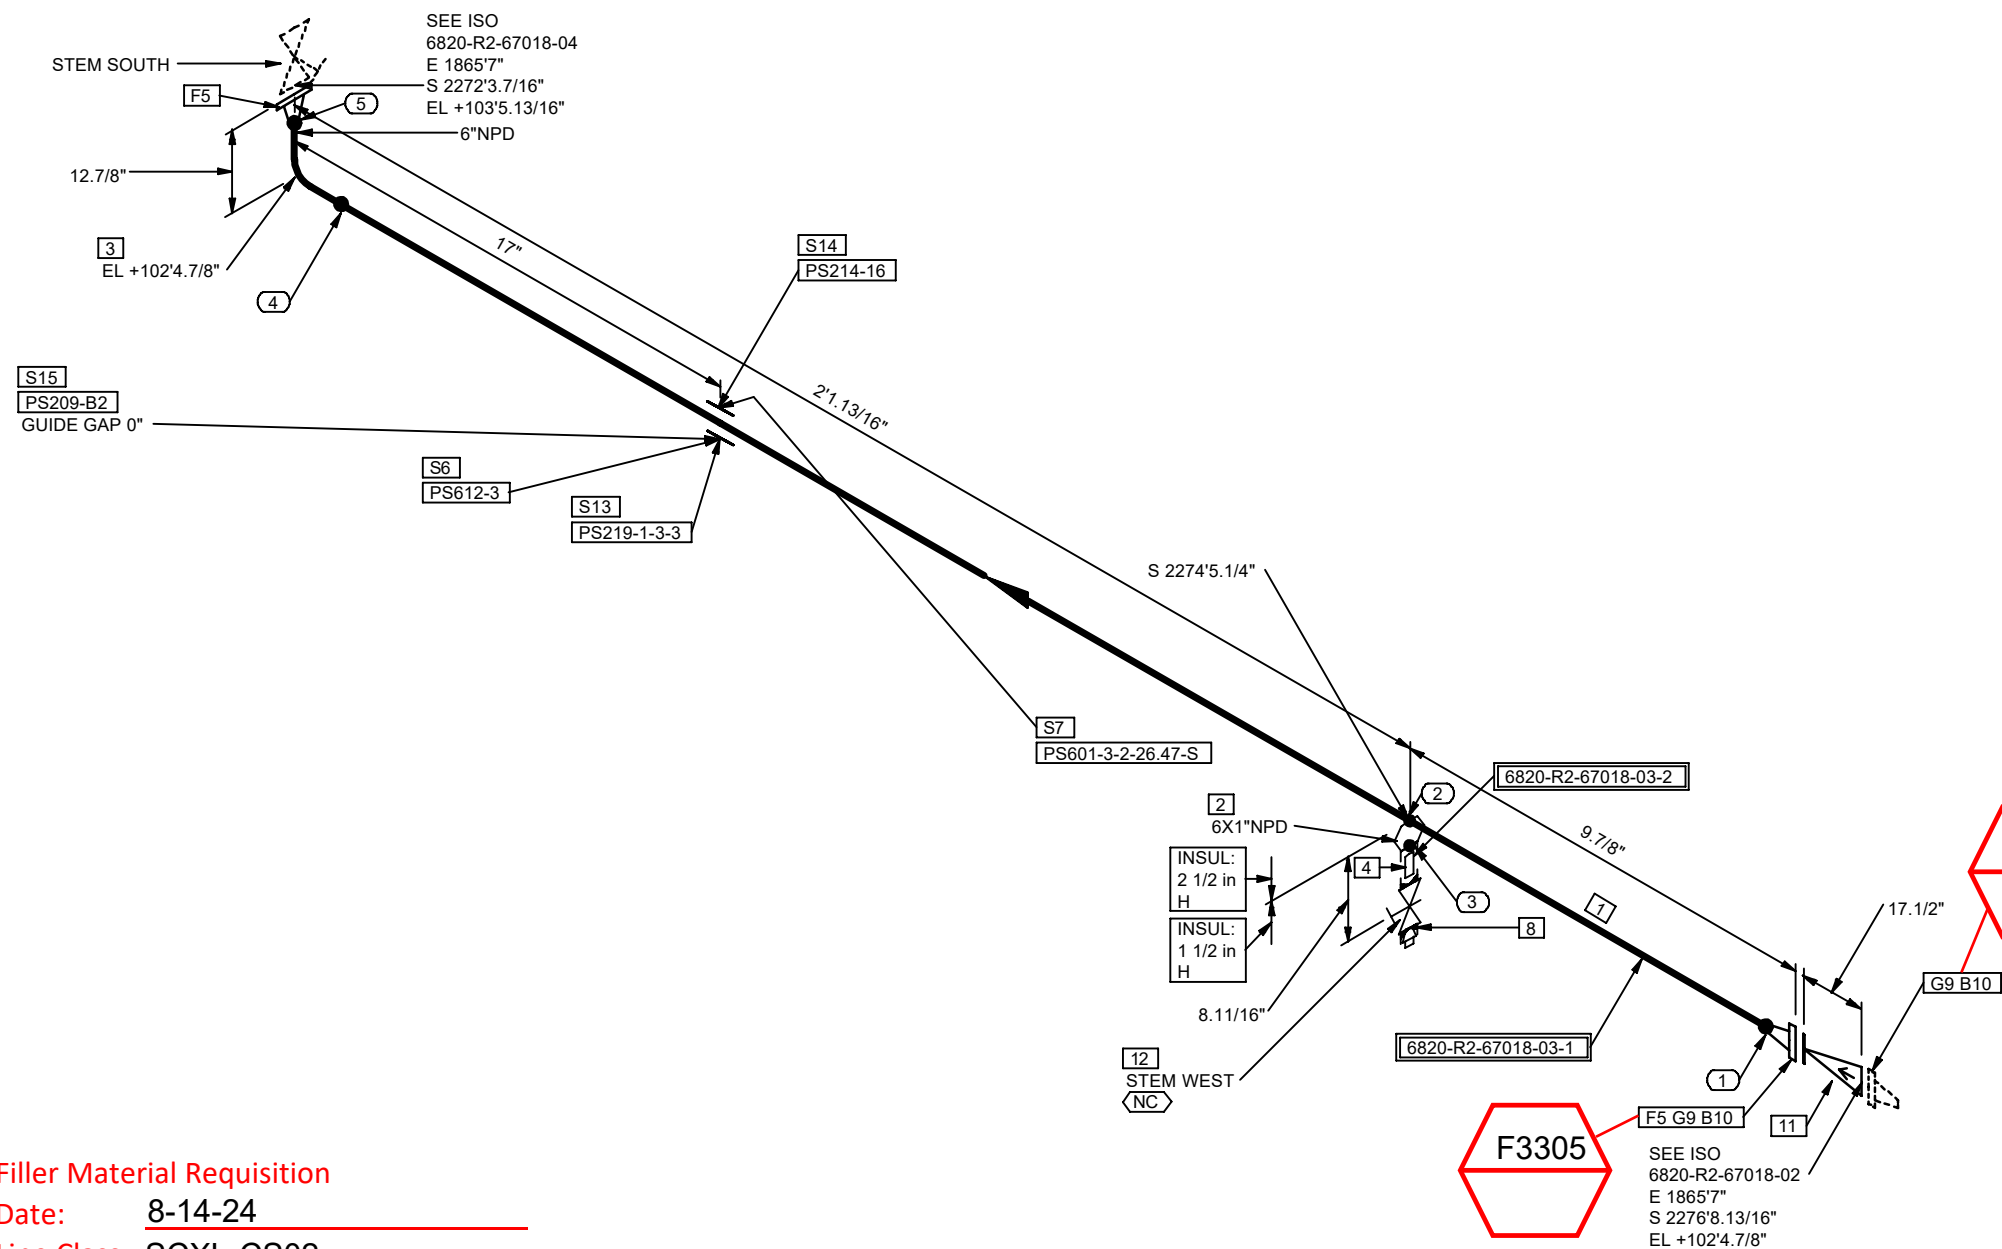

Date: 8-14-24

Line Class: SCXL-CS02

WPS: 10245

Electrode: ER70S-2

Signature: Glenn Sumrall Jr.

COORDINATE SYSTEM : PLANTCOORDINATES



Information contained in this document is the work product of one or more legal entities of Technip Energies N.V. and embodies confidential and proprietary information of the applicable entity and/or its client(s) to whom this information is restricted in accordance with conditions specified by the contract. Technip Energies N.V. and its affiliates disclaim any and all liabilities for any changes or modifications to this document which are made by any person other than the entity that issued the document under the applicable client contract.

THIS DOCUMENT IS UNCONTROLLED WHEN REPRODUCED

0	2024-08-09	RVA	ISSUED FOR CONSTRUCTION	SAD	KJK	SMR	GR
REV	DATE	BY	DESCRIPTION	CHKD	MTO	STRESS	APRVD

SERVICE: R2	VAPOR/LIQUID: L	INSUL TYPE: Per LDT	INSUL THK: Per LDT	SHOP: Y	FIELD: Y	PAINT CODE: Per LDT	MODULE: -	
 OxyChem Redstone Battleground PROJECT				P&ID: 202998C-001-PID-0021-0321				
				UNIT#: 6800	SWP AREA: 6820	SPEC: SCXL-CS02	STRESS CALC #: CN-0385	
				LINE No. 6"-R2-67018-SCXL-CS02-H				
				DRAWING NUMBER 6820-R2-67018-03				REV. 0

09 AUG 2024 08:05

