


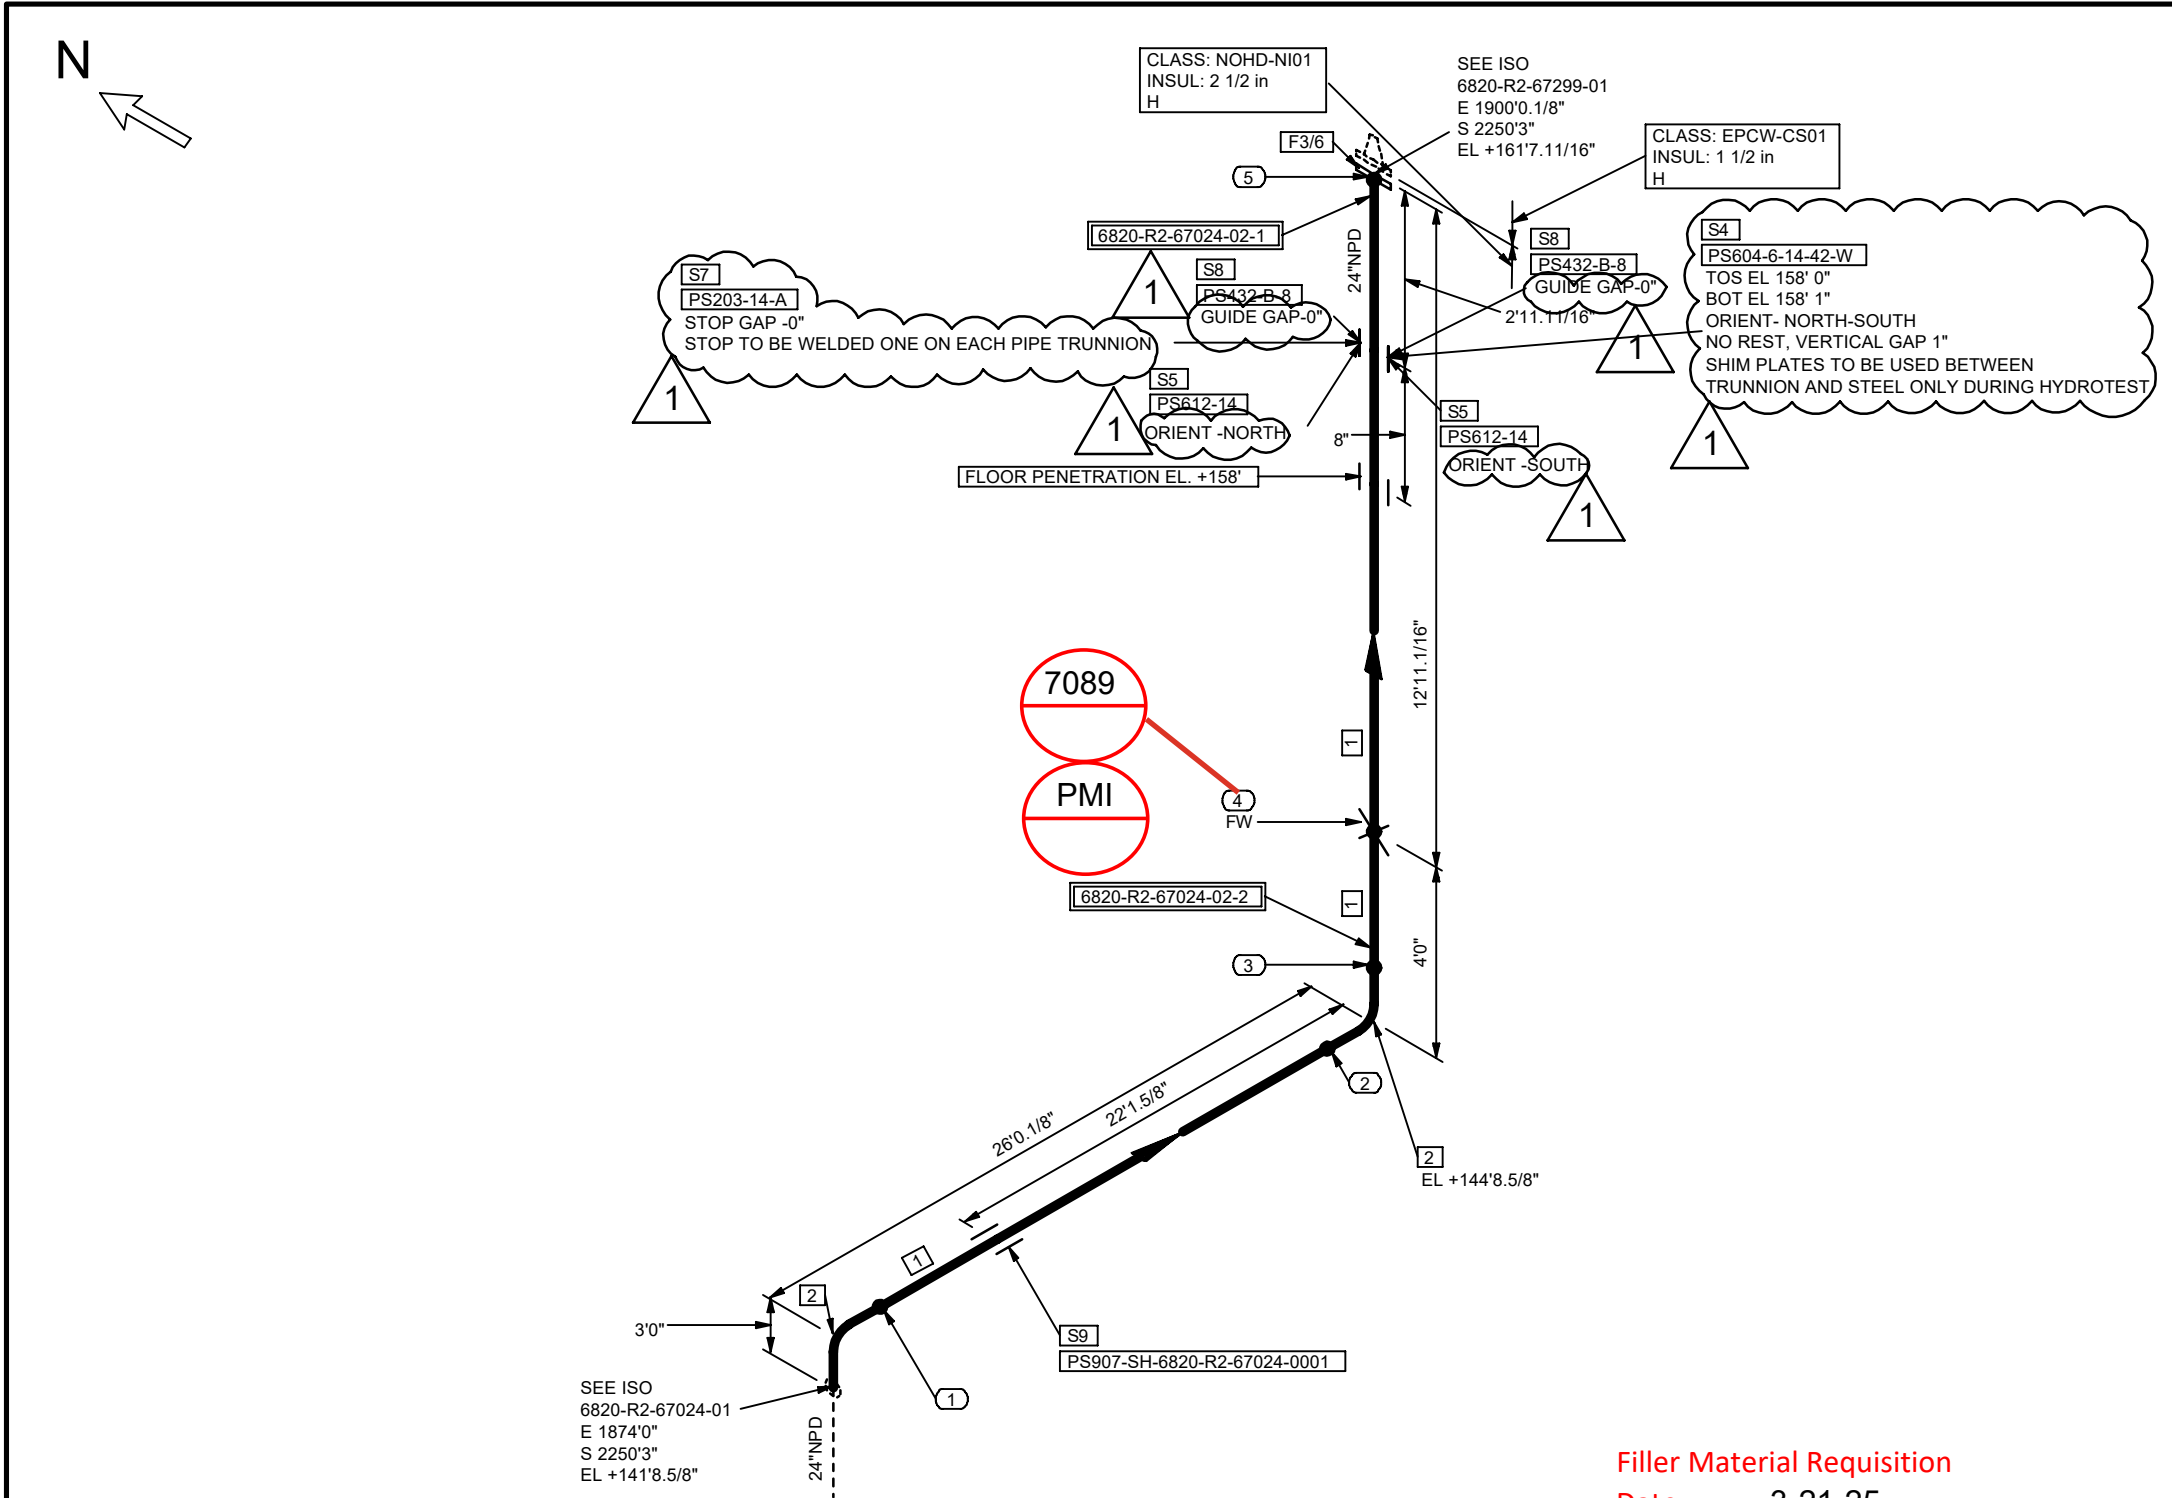

Filler Material Requisition

Date: 3-21-25
Line Class: NOHD-NI01
WPS: 4130
Electrode: ERNi-1
Signature: Glenn Sumrall Jr

SHOP MATERIALS				
NO	NPD	DESCRIPTION	IDENT	QTY
1	24	Pipes, EFW, ASME B36.19/B36.10, ASTM B725 UNS N02200 annealed, BE, -, -, S-10S	C8D8FVD5	33.5 '
2	24	90° Elb LR, Seamless, ASME B16.9, ASTM B366 Gr.WPN, BW Ends, -,Annealed, S-10S	C8D8FXC2	2
3	24	LJ Flg, ASME B16.5, ASTM A105 Galv. as per ASTM A153, 150 Lbs, FF, -,	C26WFFFJ	1
PIPE SUPPORTS PS604-6-14-42-W PS612-14 MISCELLANEOUS COMPONENTS				
4	24	Stub SP, Seamless, ASME B16.9, ASTM B366 Gr.WPN, BW Ends, -,Annealed, x S-10S	C8D8JBNE	1
5	24		PS612	2
OTHER THAN SHOP MATERIALS				
NO	NPD	DESCRIPTION	IDENT	QTY
PIPE SUPPORTS PS203-14-A PS432-B-8 PS907-SH-6820-R2-67024-0001				
7	24		PS203	1
8	24		PS432	2
9	24		PS907	1
PIECE MARKS 6820-R2-67024-02-1 6820-R2-67024-02-2				

Turner Industries Group, LLC
Received
MARCH 20, 2025
DOCUMENT CONTROL

SERVICE:	VAPOR/LIQUID:	INSUL TYPE:	INSUL THK:	SHOP:	FIELD:	PAINT CODE:	MODULE:
R2	V	Per LDT	Per LDT	Y	Y	Per LDT	-

OXY

OxyChem Redstone Battleground PROJECT

P&ID:
202998C-001-PID-0021-0322

UNIT#: 6800

EWPA AREA: 6820

SPEC: NOHD-NI01

STRESS CALC #: CN-0386

LINE No:
24"-R2-67024-NOHD-NI01-H

DRAWING NUMBER
6820-R2-67024-02

REV.
1

COORDINATE SYSTEM : PLANTCOORDINATES

NOTES:	
1.	FOR LINE PRESSURES, TEMPERATURES, INSULATION TYPE AND THICKNESS, ETC. REFER TO LATEST REVISION OF LDT.
2.	FOR STANDARD PIPE SUPPORT DETAILS SEE PROJECT STANDARD.
3.	FIELD SHIM TO SUIT UNLESS OTHERWISE NOTED.
4.	FOR PWHT REQUIREMENTS REFER TO LINE CLASS SPECIFICATION.
5.	ALL THREADED PIPE LINE SYSTEMS, FIELD SHALL VERIFY DIMENSION PRIOR TO ERECTION.
6.	FFW DESIGNATION AT WELDS INDICATES FIELD FIT WELD, WHERE PIPE FABRICATOR IS TO ADD 9 INCH OF PIPE TO THE ISOMETRIC DIMENSION TO ENABLE THE FIELD TO CUT TO FIT AT SITE.
7.	REFER TO 202998C-000-W1-1300-0001 FOR FRP AND DUAL-LAM FABRICATION.

T.EN TECHNIP ENERGIES		Information contained in this document is the work product of one or more legal entities of Technip Energies N.V. and embodies confidential and proprietary information of the applicable entity and/or its client. Use of this information is restricted in accordance with conditions specified by the contract. Technip Energies N.V. and its affiliates disclaim any and all liabilities for any changes or modifications to this document which are made by any person other than the entity that issued the document under the applicable client contract.		THIS DOCUMENT IS UNCONTROLLED WHEN REPRODUCED	
1	2025-03-14	RVA	ISSUED FOR CONSTRUCTION	SAD	KJK
0	2024-11-08	RVA	ISSUED FOR CONSTRUCTION	SAD	KJK
REV	DATE	BY	DESCRIPTION	CHKD	MTO
				STRESS	APRVD

