


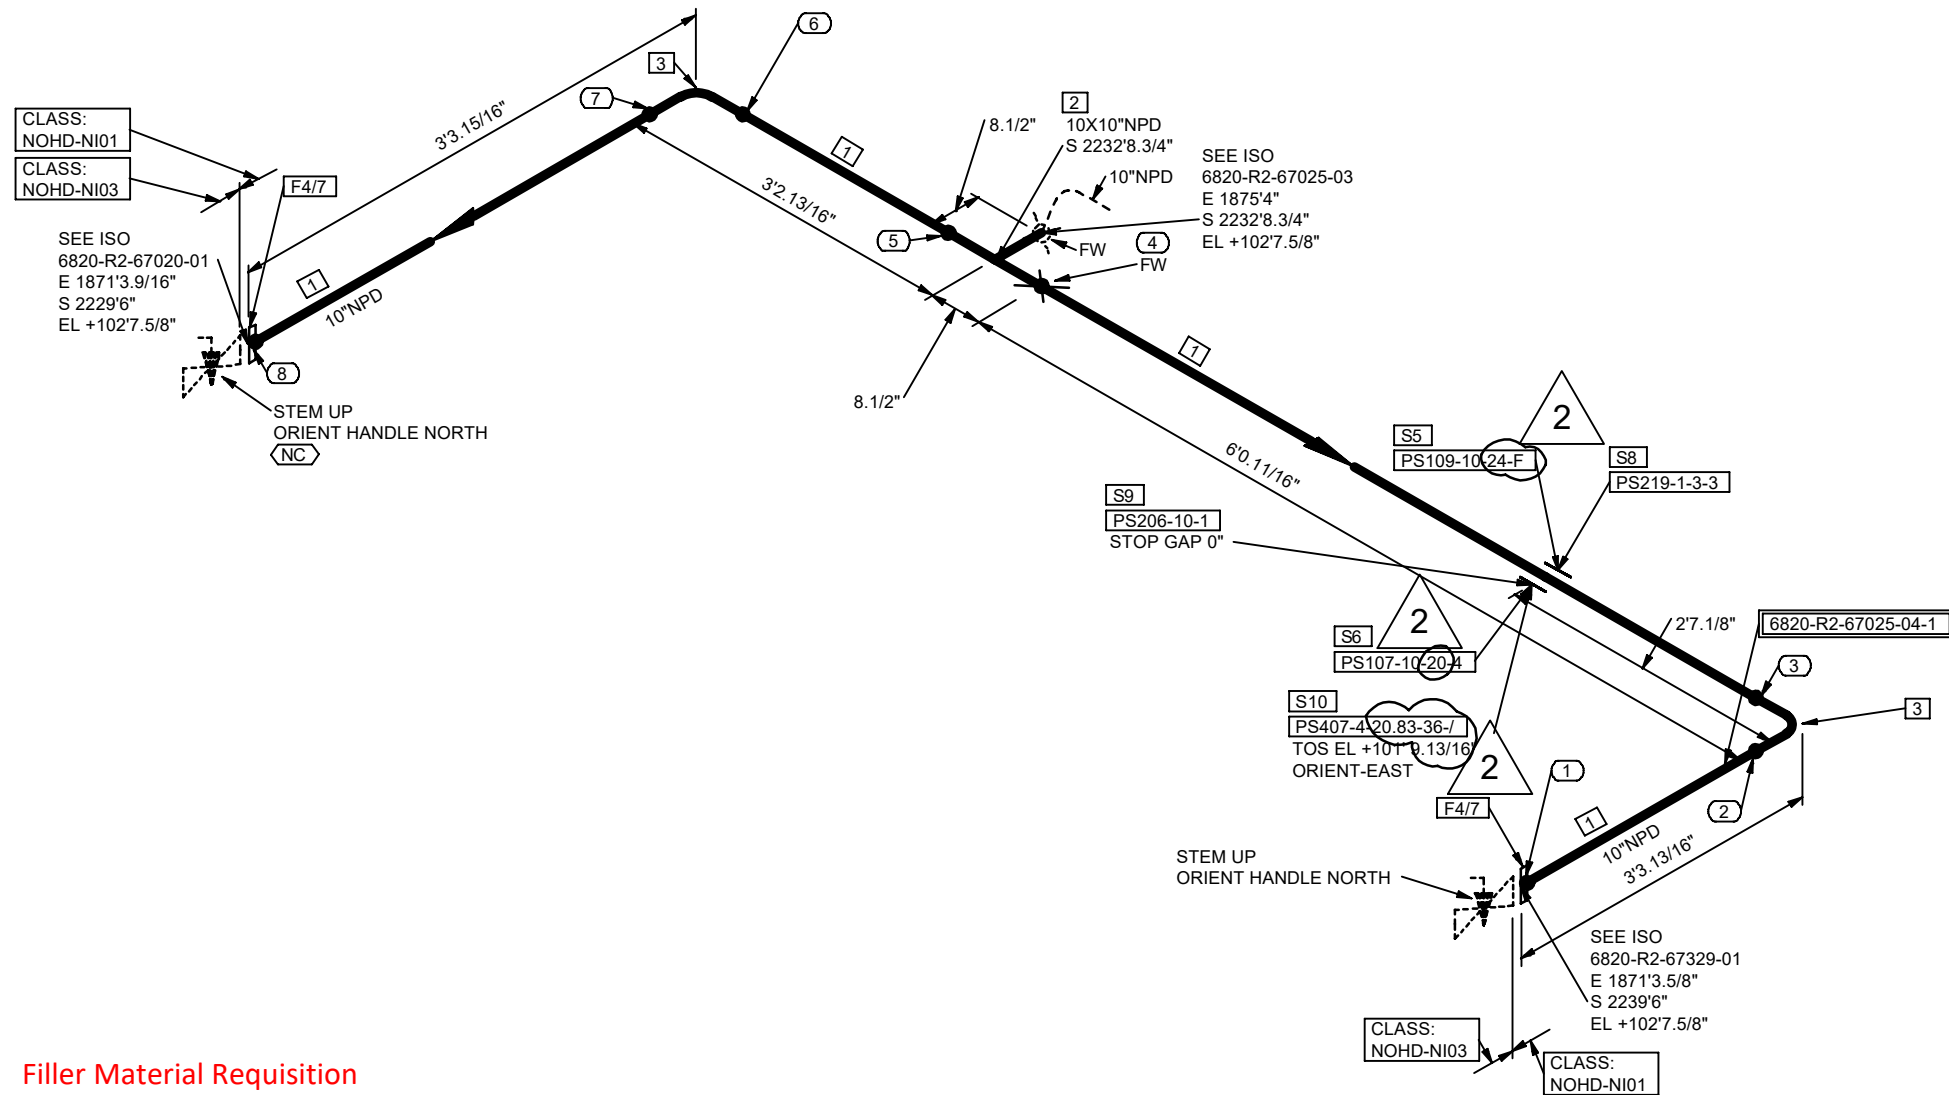

Filler Material Requisition

Date: 3-21-25
Line Class: NOHD-NI01
WPS: 4130
Electrode: ERNi-1
Signature: Glenn Sumrall Jr

COORDINATE SYSTEM : PLANTCOORDINATES

NOTES:

- FOR LINE PRESSURES, TEMPERATURES, INSULATION TYPE AND THICKNESS, ETC. REFER TO LATEST REVISION OF LDT.
- FOR STANDARD PIPE SUPPORT DETAILS SEE PROJECT STANDARD.
- FIELD SHIM TO SUIT UNLESS OTHERWISE NOTED.
- FOR PWHT REQUIREMENTS REFER TO LINE CLASS SPECIFICATION.
- ALL THREADED PIPE LINE SYSTEMS, FIELD SHALL VERIFY DIMENSION PRIOR TO ERECTION.
- FFW DESIGNATION AT WELDS INDICATES FIELD FIT WELD, WHERE PIPE FABRICATOR IS TO ADD 9 INCH OF PIPE TO THE ISOMETRIC DIMENSION TO ENABLE THE FIELD TO CUT TO FIT AT SITE.
- REFER TO 202998C-000-W1-1300-0001 FOR FRP AND DUAL-LAM FABRICATION.



Information contained in this document is the work product of one or more legal entities of Technip Energies N.V. and embodies confidential and proprietary information of the applicable entity and/or its client. Use of this information is restricted in accordance with conditions specified by the contract. Technip Energies N.V. and its affiliates disclaim any and all liabilities for any changes or modifications to this document which are made by any person other than the entity that issued the document under the applicable client contract.

THIS DOCUMENT IS UNCONTROLLED WHEN REPRODUCED

REV	DATE	BY	DESCRIPTION	CHKD	MTD	STRESS	APRVD
2	2025-03-14	RVA	ISSUED FOR CONSTRUCTION	SAD	KJK	SMR	GR
1	2025-01-31	RVA	ISSUED FOR CONSTRUCTION	SAD	KJK	SMR	GR
0	2024-11-08	RVA	ISSUED FOR CONSTRUCTION	SAD	KJK	SMR	GR

SERVICE: R2	VAPOR/LIQUID: L	INSUL TYPE: Per LDT	INSUL THK: Per LDT	SHOP: Y	FIELD: Y	PAINT CODE: Per LDT	MODULE: -
				P&ID: 202998C-001-PID-0021-0322			
				UNIT#: 6800	EWPA AREA: 6820	SPEC: NOHD-NI01	STRESS CALC #: CN-0387
				LINE No: 10"-R2-67025-NOHD-NI01-H			
OxyChem Redstone Battleground PROJECT				DRAWING NUMBER 6820-R2-67025-04			REV. 2

SHOP MATERIALS

NO	NPD	DESCRIPTION	IDENT	QTY
1	10	Pipes, EFW, ASME B36.19/B36.10, ASTM B725 UNS N02200 annealed, BE, -, -, S-10S	C7ZWWMEP	9.4'
2	10X10	Eq Te, Seamless, ASME B16.9, ASTM B366 Gr.WPN, BW Ends, -, Annealed, S-10S	C7ZWWT4M	1
3	10	90° Elb LR, Seamless, ASME B16.9, ASTM B366 Gr.WPN, BW Ends, -, Annealed, S-10S	C7ZWWZN1	2
4	10	LJ Flg, ASME B16.5, ASTM A105 Galv. as per ASTM A153, 150 Lbs, FF, -,	C26WFFFA	2

PIPE SUPPORTS

5	10	PS109-10-24-F	PS109	1
6	10	PS107-10-20-4	PS107	1

MISCELLANEOUS COMPONENTS

7	10	Stub SP, Seamless, ASME B16.9, ASTM B366 Gr.WPN, BW Ends, -, Annealed, x S-10S	C8A5GXS2	2
---	----	--	----------	---

OTHER THAN SHOP MATERIALS

NO	NPD	DESCRIPTION	IDENT	QTY
8	10	PS219-1-3-3	PS219	1
9	10	PS206-10-1	PS206	1
10	10	PS407-4-20.83-36-/	PS407	1

PIECE MARKS

6820-R2-67025-04-1

