


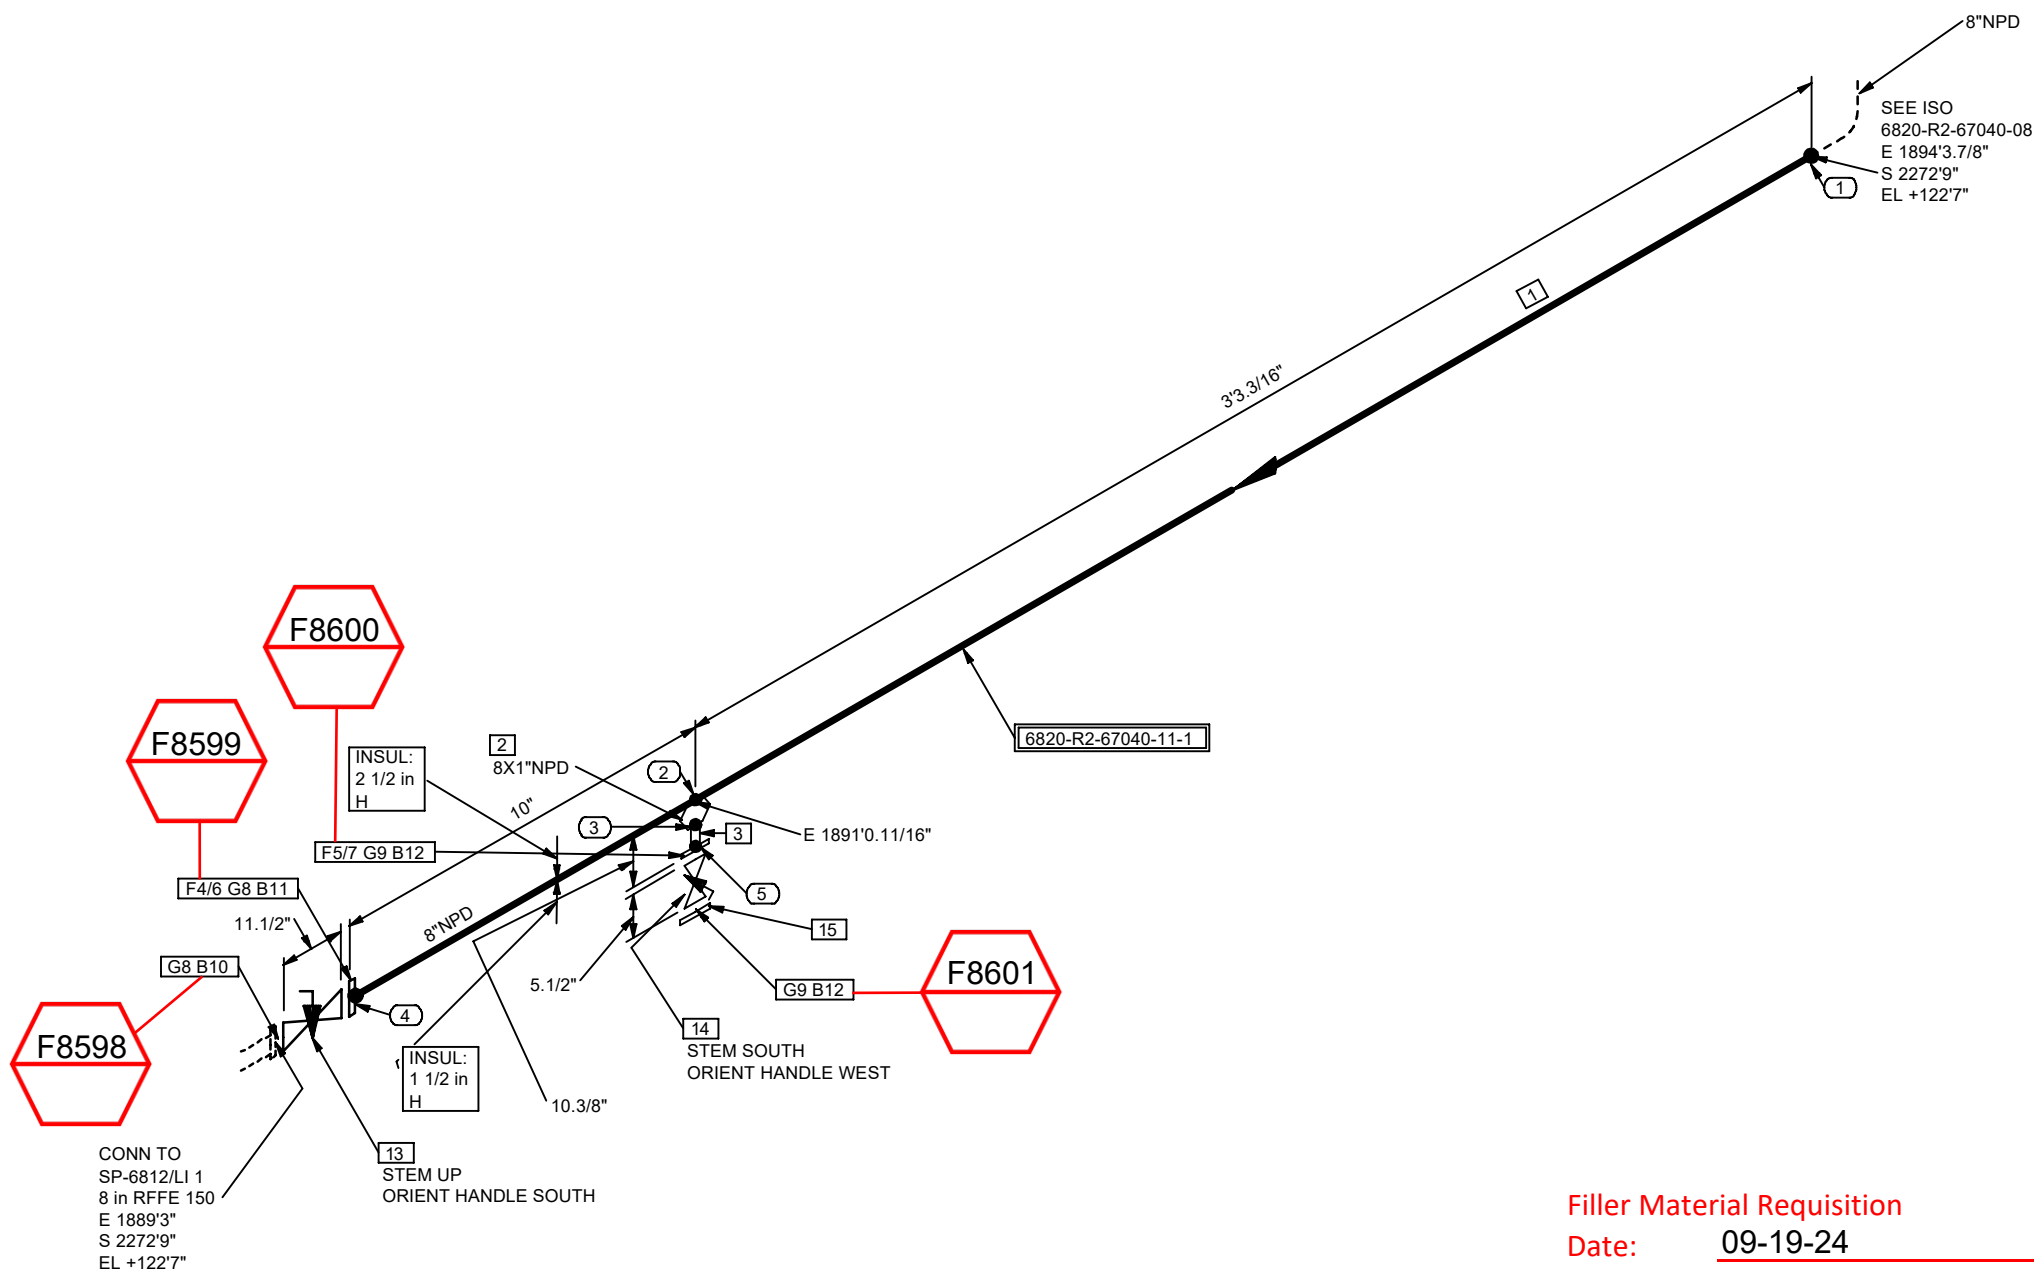

NOTES:

FOR LINE PRESSURES, TEMPERATURES, INSULATION TYPE AND THICKNESS, ETC.  
REFER TO LATEST REVISION OF LDT.

FOR STANDARD PIPE SUPPORT DETAILS SEE PROJECT STANDARD.


FIELD SHIM TO SUIT UNLESS OTHERWISE NOTED.

FOR PWHT REQUIREMENTS REFER TO LINE CLASS SPECIFICATION.

ALL THREADED PIPE LINE SYSTEMS, FIELD SHALL VERIFY DIMENSION PRIOR TO ERECTION.

FFW DESIGNATION AT WELDS INDICATES FIELD FIT WELD, WHERE PIPE FABRICATOR IS TO ADD  
9 INCH OF PIPE TO THE ISOMETRIC DIMENSION TO ENABLE THE FIELD TO CUT TO FIT AT SITE.

REFER TO 202998C-000-W1-1300-0001 FOR FRP AND DUAL-LAM FABRICATION.

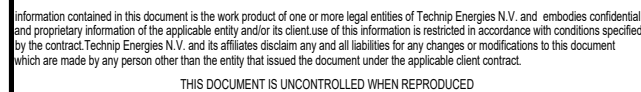

Date: 09-19-24

Line Class: NOHD-NI01

WPS: 4130

Electrode: ERNi-1

Signature: Glenn Sumrall Jr

| OTHER THAN SHOP MATERIALS |     |   |          |     |
|---------------------------|-----|---|----------|-----|
| NO                        | NPD | DESCRIPTION   | IDENT    | QTY |
| 8                         | 8   | NM Flat Gk, Barium Sulfate filled<br>PTFE, 150 Lbs, RF as per ASME<br>B16.5, -, Thk=1/8in, -,                                                                         | C6SBWZF4 | 2   |
| 9                         | 1   | NM Flat Gk, Barium Sulfate filled<br>PTFE, 150 Lbs, RF as per ASME<br>B16.5, -, Thk=1/8in, -,                                                                         | C6S4K87F | 2   |
| 10                        | 3/4 | SBlt 2 HHx N, A193 Gr.B7/A194<br>Gr.2H, -, Xylan PTFE Coated, -<br>4.5 in. Length                                                                                     | C6S4K8BD | 8   |
| 11                        | 3/4 | SBlt 2 HHx N, A193 Gr.B7/A194<br>Gr.2H, -, Xylan PTFE Coated, -<br>4.75 in. Length                                                                                    | C6S4K8BE | 8   |
| 12                        | 1/2 | SBlt 2 HHx N, A193 Gr.B7/A194<br>Gr.2H, -, Xylan PTFE Coated, -<br>2.75 in. Length                                                                                    | C6S4K87U | 8   |
| 13                        | 8   | Plug Flg.SP, Inverted Tapered<br>Plug, Non Lubricated, API 599,<br>ASTM A494 Gr.CZ100, 150 Lbs,<br>RF, Ends as per ASME B16.5, -,<br>GO,-, -, Valve Tag: PL-0503      | C8P7NJK0 | 1   |
| 14                        | 1   | Plug Flg.SP, Inverted Tapered<br>Plug, Non Lubricated, API 599,<br>ASTM B564 UNS N02200, 150 Lbs,<br>RF, Ends as per ASME B16.5, -,<br>LO,-, -, Valve Tag: PL-0503_LO | C8RR9V37 | 1   |
| 15                        | 1   | Bld Flg, ASME B16.5, ASTM B564 UNS<br>N02200, 150 Lbs. RF, -,   | C7T63YAU | 1   |

Turner Industries Group, LLC  
Received  
SEPTEMBER 18, 2024  
DOCUMENT CONTROL

|                                                                                       |                    |                        |                       |                                          |                   |                        |                           |           |
|---------------------------------------------------------------------------------------|--------------------|------------------------|-----------------------|------------------------------------------|-------------------|------------------------|---------------------------|-----------|
| SERVICE:<br>R2                                                                        | VAPOR/LIQUID:<br>L | INSUL TYPE:<br>Per LDT | INSUL THK:<br>Per LDT | SHOP:<br>Y                               | FIELD:<br>Y       | PAINT CODE:<br>Per LDT | MODULE:<br>-              |           |
|  |                    |                        |                       | PID:<br>202998C-001-PID-0021-0323        |                   |                        |                           |           |
|                                                                                       |                    |                        |                       | UNIT#:<br>6800                           | SWP AREA:<br>6820 | SPEC:<br>NOHD-NI01     | STRESS CALC #:<br>CN-0379 |           |
|                                                                                       |                    |                        |                       | LINE No.<br>8"-R2-67040-NOHD-NI01-H      |                   |                        |                           |           |
|                                                                                       |                    |                        |                       | DRAWING NUMBER<br>6820-R2-67040-11       |                   |                        |                           | REV.<br>0 |
|                                                                                       |                    |                        |                       | OxyChem Redstone Battleground<br>PROJECT |                   |                        |                           |           |