


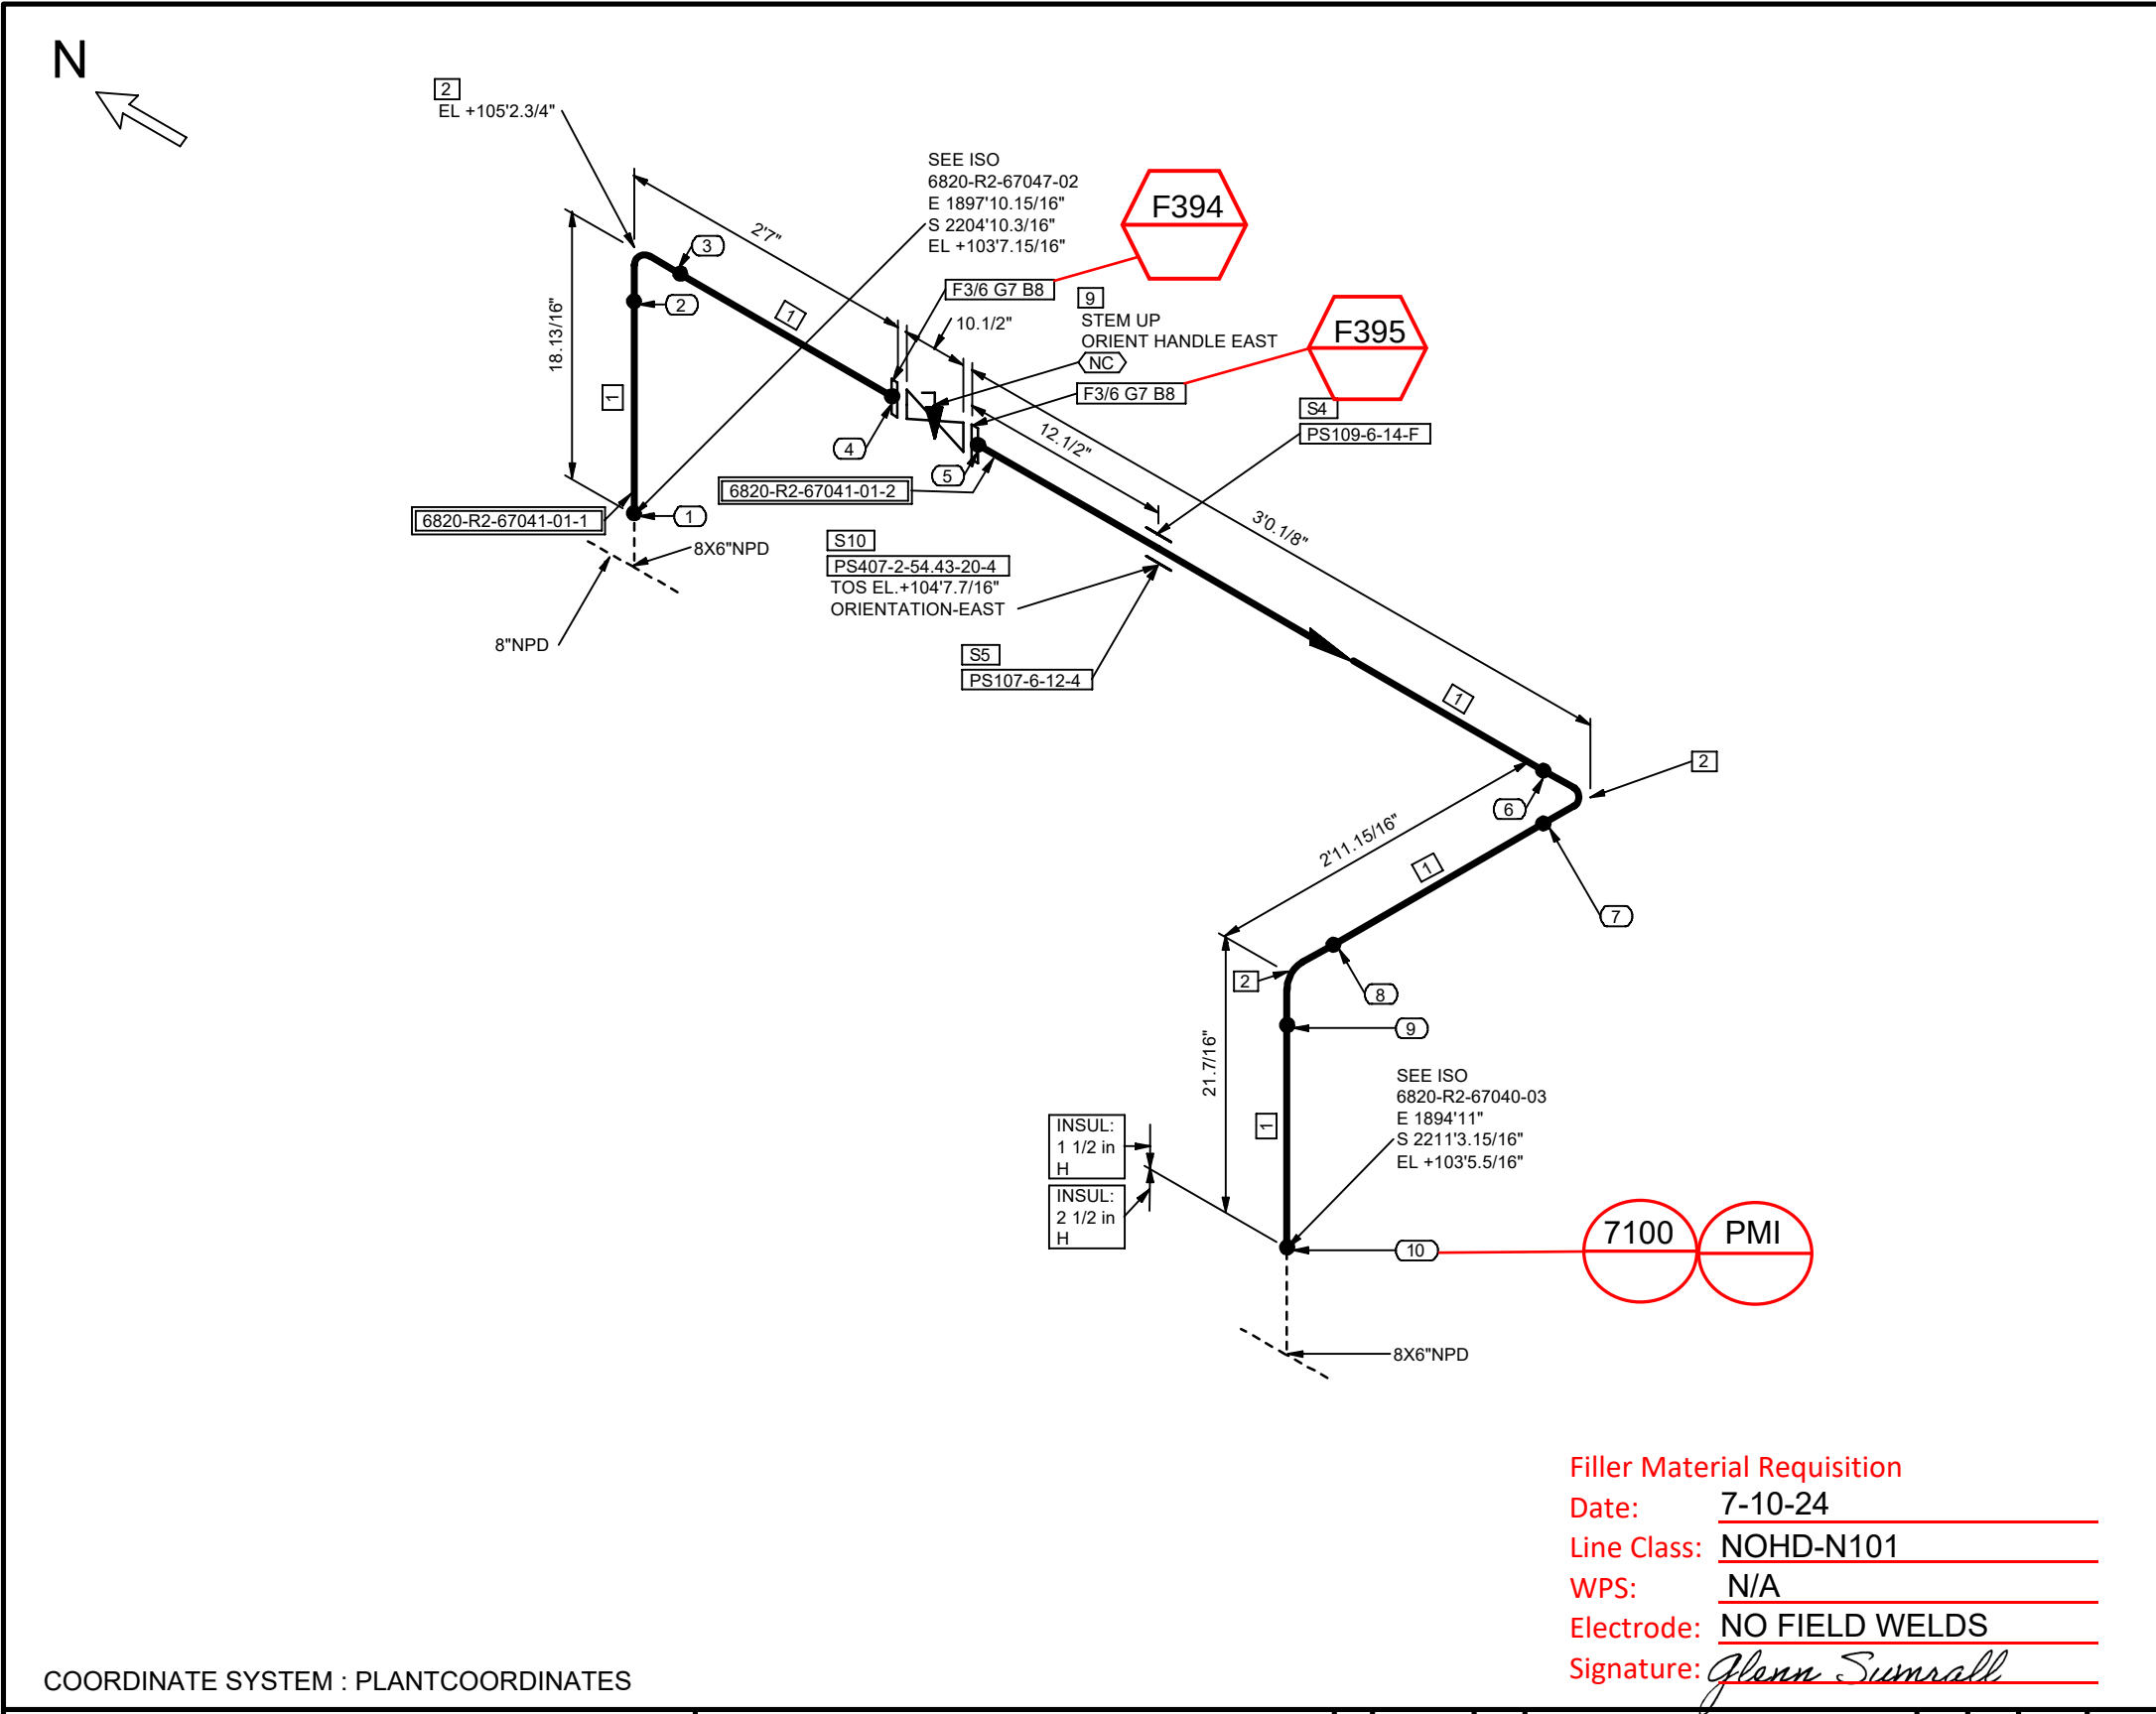

Filler Material Requisition

Date: 7-10-24
Line Class: NOHD-N101
WPS: N/A
Electrode: NO FIELD WELDS
Signature: *Glenn Sumrall*

SHOP MATERIALS

NO	NPD	DESCRIPTION	IDENT	QTY
1	6	Pipes, Seamless, ASME B36.19/B36.10, ASTM B161 UNS N02200, BE, -, -, S-10S	C7ZWWN1D	6.9
2	6	90° Elb LR, Seamless, ASME B16.9, ASTM B366 Gr.WPN, BW Ends, -, Annealed, S-10S	C7ZWX022	3
3	6	LJ Flg, ASME B16.5, ASTM A105 Galv. as per ASTM A153, 150 Lbs, FF, -,	C26WFFFP	2

PIPE SUPPORTS

4	6	PS109-6-14-F	PS109	1
5	6	PS107-6-12-4	PS107	1

MISCELLANEOUS COMPONENTS

6	6	Stub SP, Seamless, ASME B16.9, ASTM B366 Gr.WPN, BW Ends, -, Annealed, x S-10S	C8A5GY30	2
---	---	--	----------	---

OTHER THAN SHOP MATERIALS

NO	NPD	DESCRIPTION	IDENT	QTY
7	6	NM Flat Gk, Barium Sulfate filled PTFE, 150 Lbs, RF as per ASME B16.5, -, Thk=1/8in, -,	C6S4K87R	2
8	3/4	SBlt 2 HHx N, A193 Gr.B7/A194 Gr.2H, -, Xylan PTFE Coated, - 4.25 in. Length	C6S4K8BC	16
9	6	Plug Flg, SP, Inverted Tapered Plug, Non Lubricated, API 599, ASTM A494 Gr.CZ100, 150 Lbs, RF, Ends as per ASME B16.5, -, GO, -, -, Valve Tag: PL-0503	C8P7NJJZ	1

PIPE SUPPORTS

10	6	PS407-2-54.43-20-4	PS407	1
----	---	--------------------	-------	---

PIECE MARKS

6820-R2-67041-01-1 6820-R2-67041-01-2



COORDINATE SYSTEM : PLANTCOORDINATES

NOTES:

- FOR LINE PRESSURES, TEMPERATURES, INSULATION TYPE AND THICKNESS, ETC. REFER TO LATEST REVISION OF LDT.
- FOR STANDARD PIPE SUPPORT DETAILS SEE PROJECT STANDARD.
- FIELD SHIM TO SUIT UNLESS OTHERWISE NOTED.
- FOR PWHT REQUIREMENTS REFER TO LINE CLASS SPECIFICATION.
- ALL THREADED PIPE LINE SYSTEMS, FIELD SHALL VERIFY DIMENSION PRIOR TO ERECTION.
- FFW DESIGNATION AT WELDS INDICATES FIELD FIT WELD, WHERE PIPE FABRICATOR IS TO ADD 9 INCH OF PIPE TO THE ISOMETRIC DIMENSION TO ENABLE THE FIELD TO CUT TO FIT AT SITE.



Information contained in this document is the work product of one or more legal entities of Technip Energies N.V. and embodies confidential and proprietary information of the applicable entity and/or its client. Use of this information is restricted in accordance with conditions specified by the contract. Technip Energies N.V. and its affiliates disclaim any and all liabilities for any changes or modifications to this document which are made by any person other than the entity that issued the document under the applicable client contract.

THIS DOCUMENT IS UNCONTROLLED WHEN REPRODUCED

REV	DATE	BY	DESCRIPTION	CHKD	MTO	STRESS	APRVD
0	2024-07-05	RVA	ISSUED FOR CONSTRUCTION	SAD	KJK	BRD	GR

SERVICE: R2	VAPOR/LIQUID: L	INSUL TYPE: Per LDT	INSUL THK: Per LDT	SHOP: Y	FIELD: Y	PAINT CODE: Per LDT	MODULE: -	
 OxyChem Redstone Battleground PROJECT				P&ID: 202998C-001-PID-0021-0323				
				UNIT#:	EWPA AREA:	SPEC:	STRESS CALC #:	
				6800	6820	NOHD-NI01	CN-0379	
				LINE No: 6"-R2-67041-NOHD-NI01-H				
				DRAWING NUMBER 6820-R2-67041-01				
				REV. 0				

