


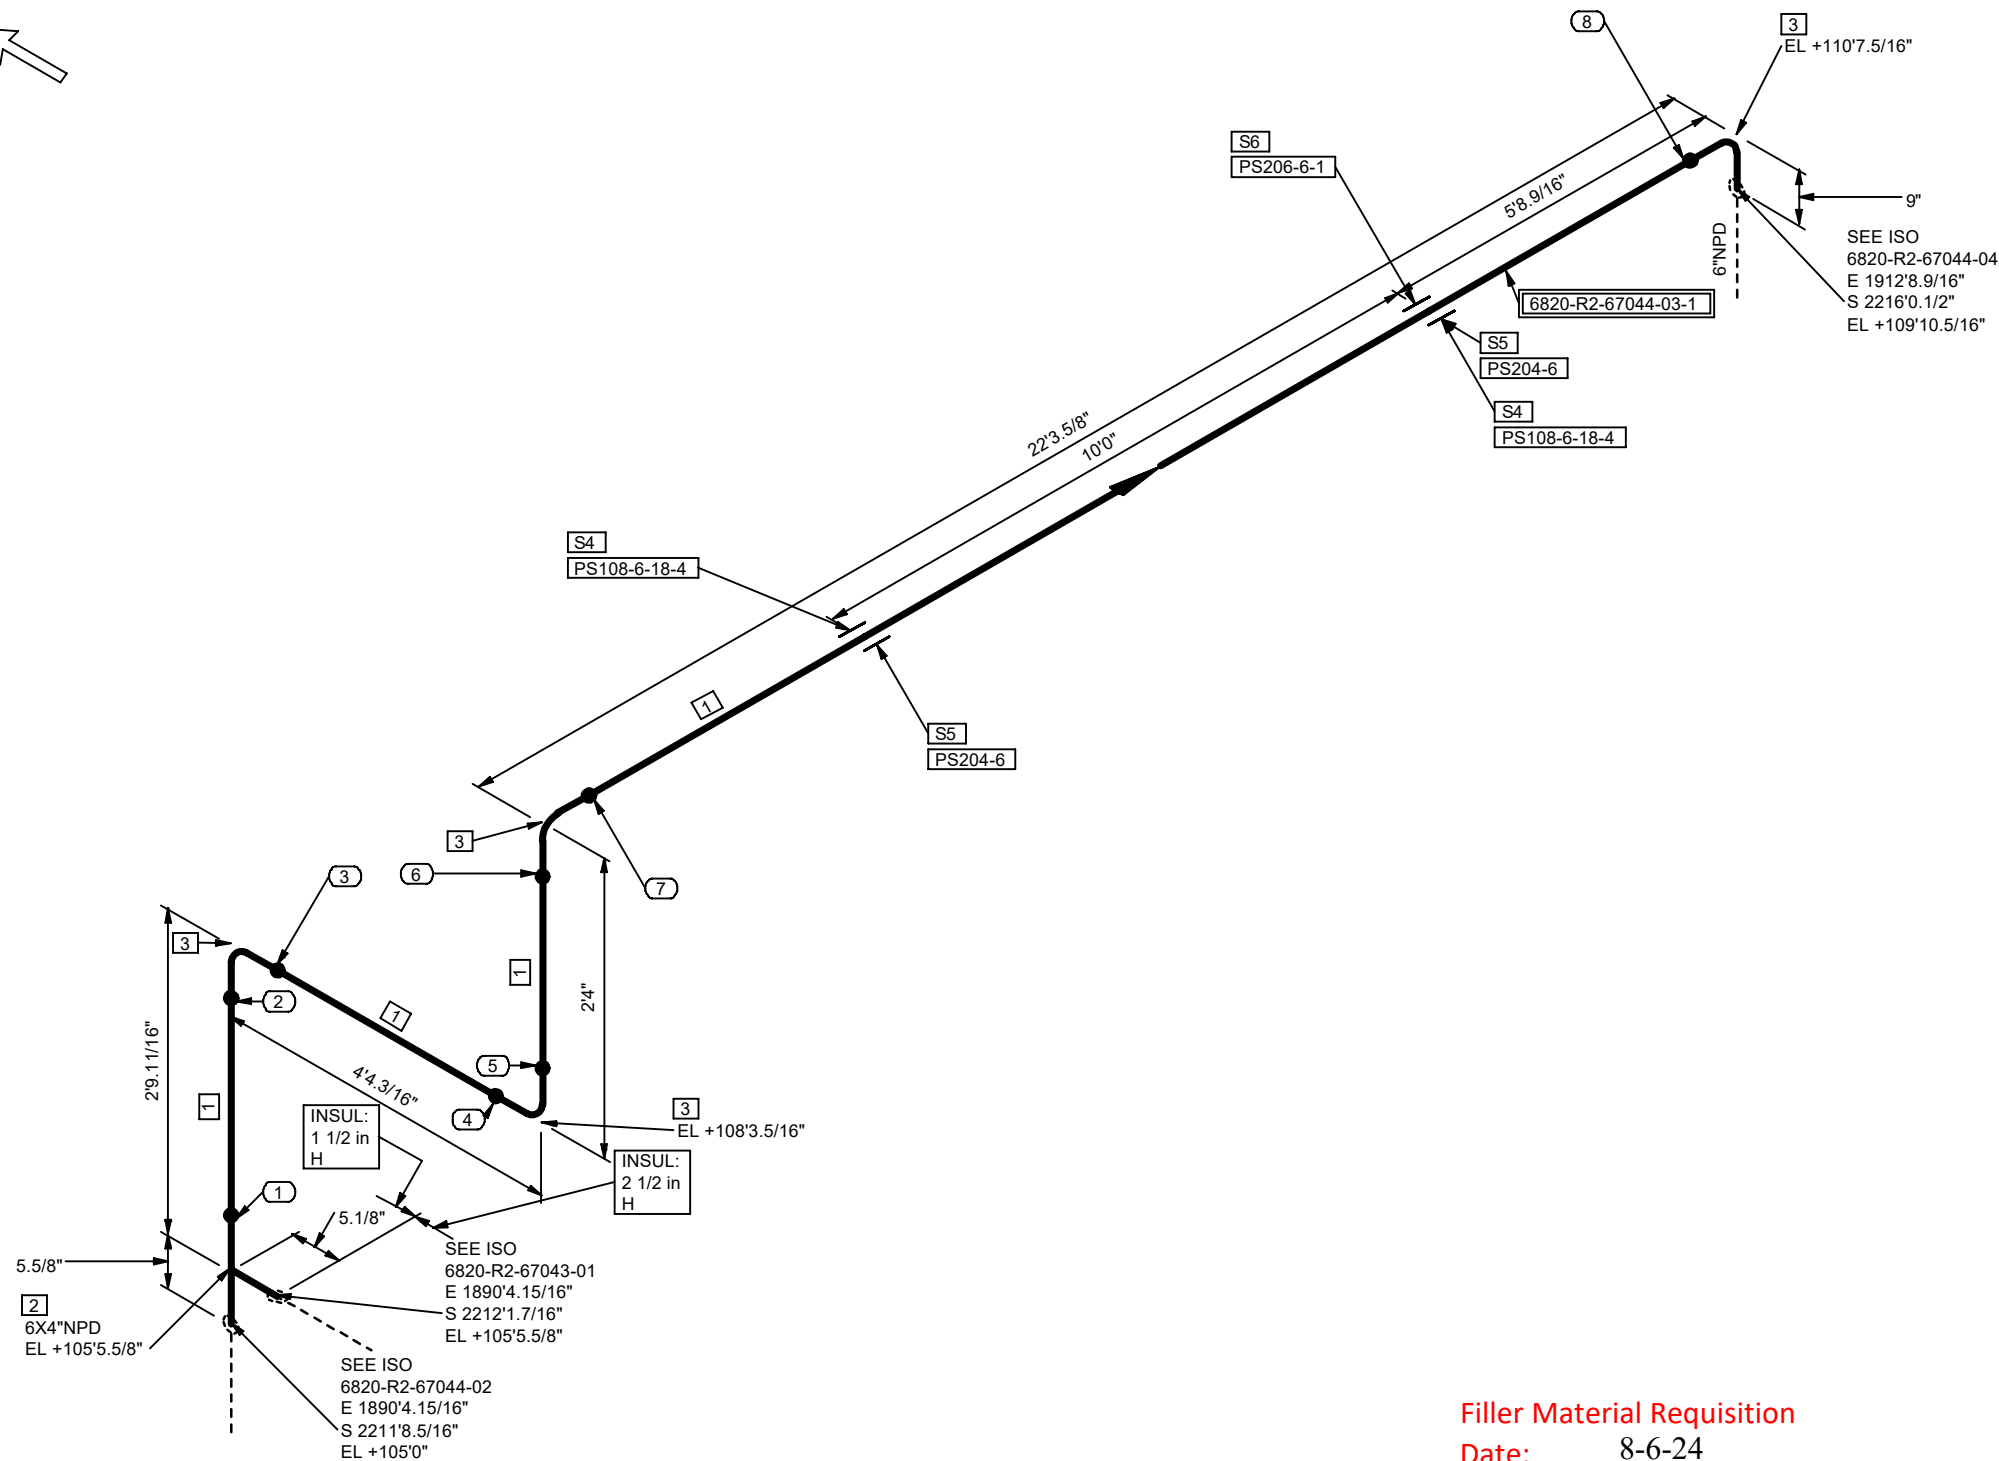

Filler Material Requisition

Date: 8-6-24
Line Class: SCXL-CS02
WPS: 10245
Electrode: ER70S-2
Signature: Pedro Morin

SHOP MATERIALS

NO	NPD	DESCRIPTION	IDENT	QTY
1	6	Pipes, Seamless, ASME B36.10, ASTM A106 Gr.B, BE, -, -, S-STD	CPP00336	26.1'
2	6X4	Red Te, Seamless, ASME B16.9, ASTM A234 Gr.WPB, BW Ends, -, -, S-STD	CDB0DGGR	1
3	6	90° Elb LR, Seamless, ASME B16.9, ASTM A234 Gr.WPB, BW Ends, -, -, S-STD	CDB66GNP	4

PIPE SUPPORTS

4	6	PS108-6-18-4	PS108	2
---	---	--------------	-------	---

OTHER THAN SHOP MATERIALS

NO	NPD	DESCRIPTION	IDENT	QTY
----	-----	-------------	-------	-----

PIPE SUPPORTS

5	6	PS204-6	PS204	2
6	6	PS206-6-1	PS206	1

PIECE MARKS

6820-R2-67044-03-1

COORDINATE SYSTEM : PLANTCOORDINATES

NOTES:


- 1. FOR LINE PRESSURES, TEMPERATURES, INSULATION TYPE AND THICKNESS, ETC. REFER TO LATEST REVISION OF LDT.
- 2. FOR STANDARD PIPE SUPPORT DETAILS SEE PROJECT STANDARD.
- 3. FIELD SHIM TO SUIT UNLESS OTHERWISE NOTED.
- 4. FOR PWHT REQUIREMENTS REFER TO LINE CLASS SPECIFICATION.
- 5. ALL THREADED PIPE LINE SYSTEMS, FIELD SHALL VERIFY DIMENSION PRIOR TO ERECTION.
- 6. FFWD DESIGNATION AT WELDS INDICATES FIELD FIT WELD, WHERE PIPE FABRICATOR IS TO ADD 9 INCH OF PIPE TO THE ISOMETRIC DIMENSION TO ENABLE THE FIELD TO CUT TO FIT AT SITE.
- 7. REFER TO 202998C-000-W1-1300-0001 FOR FRP AND DUAL-LAM FABRICATION.



Information contained in this document is the work product of one or more legal entities of Technip Energies N.V. and embodies confidential and proprietary information of the applicable entity and/or its client. Use of this information is restricted in accordance with conditions specified by the contract. Technip Energies N.V. and its affiliates disclaim any and all liabilities for any changes or modifications to this document which are made by any person other than the entity that issued the document under the applicable client contract.

THIS DOCUMENT IS UNCONTROLLED WHEN REPRODUCED

0	2024-08-02	RVA	ISSUED FOR CONSTRUCTION	SAD	KJK	BRD	GR		
REV	DATE	BY	DESCRIPTION	CHKD	MTO	STRESS	APRVD		

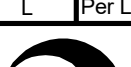SERVICE: R2	VAPOR/LIQUID: L	INSUL TYPE: Per LDT	INSUL THK: Per LDT	SHOP: Y	FIELD: Y	PAINT CODE: Per LDT	MODULE: -	
 OxyChem Redstone Battleground PROJECT				P&ID: 202998C-001-PID-0021-0323				
				UNIT#: 6800	EWPA AREA: 6820	SPEC: SCXL-CS02	STRESS CALC #: CN-0385/CN-0394	
				LINE No: 6"-R2-67044-SCXL-CS02-H				
				DRAWING NUMBER 6820-R2-67044-03				
				REV. 0				



OxyChem Redstone Battleground PROJECT

