


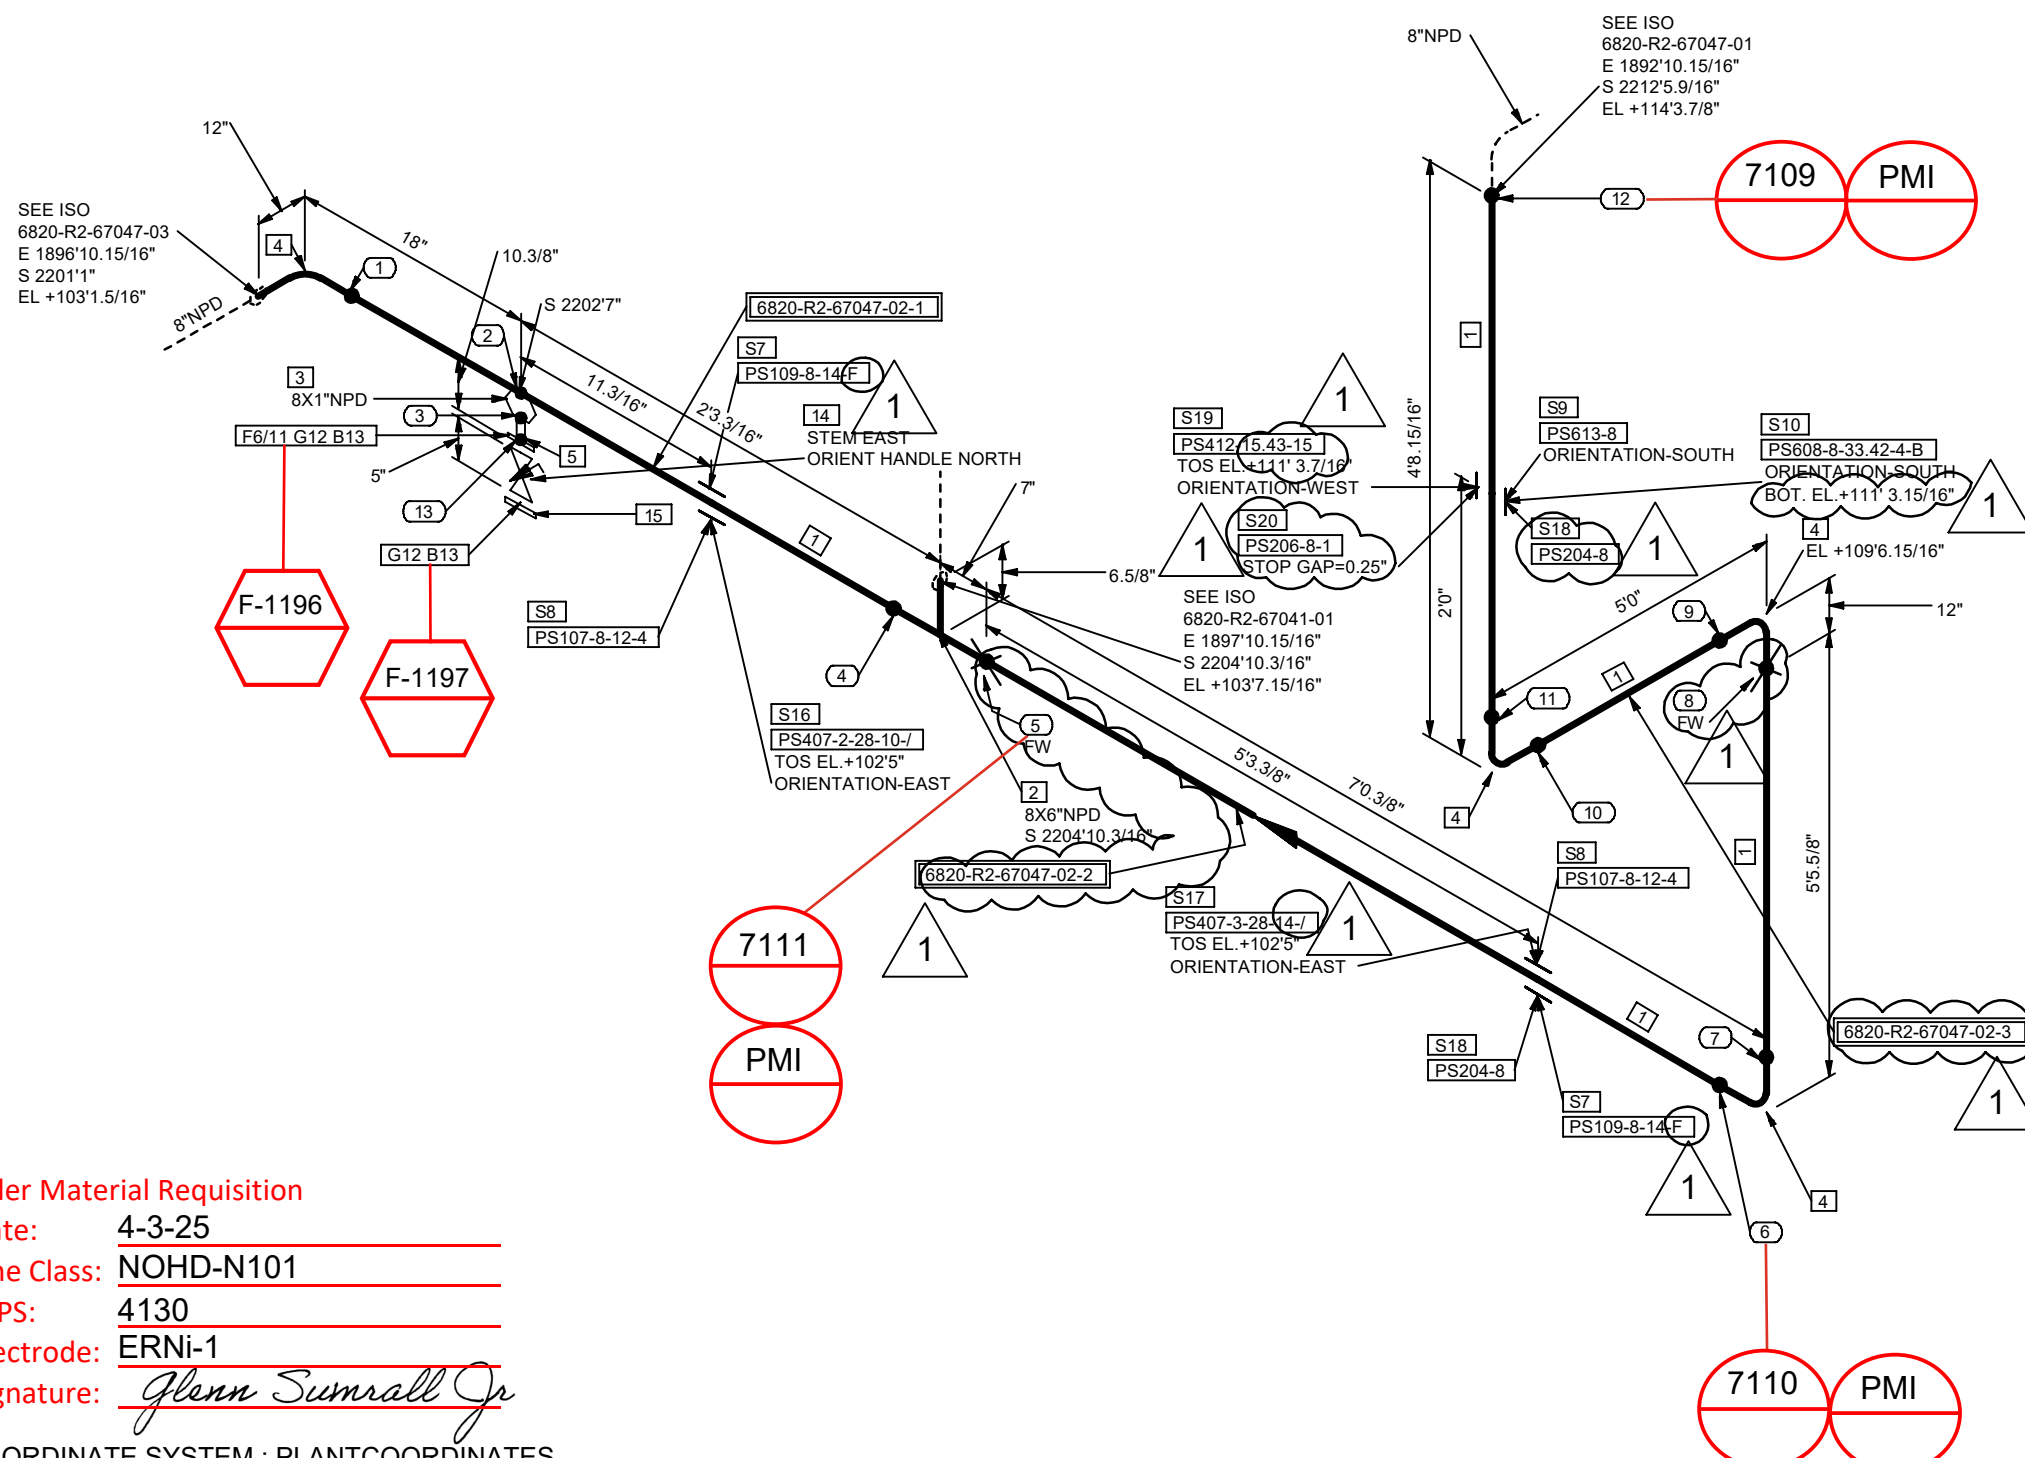

Date: 4-3-25

Line Class: NOHD-N101

WPS: 4130

Electrode: ERNi-1

Signature: *Glenn Sumrall Jr*

NOTES:

- 

Information contained in this document is the work product of one or more legal entities of Technip Energies N.V. and embodies confidential and proprietary information of the applicable entity and/or its client; use of this information is restricted in accordance with conditions specified by the contract. Technip Energies N.V. and its affiliates disclaim any and all liabilities for any changes or modifications to this document which are made by any person other than the entity that issued the document under the applicable client contract.

THIS DOCUMENT IS UNCONTROLLED WHEN REPRODUCED

1	2025-03-28	RVA	ISSUED FOR CONSTRUCTION	SAD	KJK	SMR	GR
0	2024-07-18	RVA	ISSUED FOR CONSTRUCTION	SAD	KJK	BRD	GR
REV	DATE	BY	DESCRIPTION	CHKD	MTD	STRESS	APRV

PIPE SUPPORTS

MISCELLANEOUS COMPONENTS

OTHER THAN SHOP MATERIALS

PIPE SUPPORTS

16	8	PS407-2-28-10-/	PS407	1
17	8	PS407-3-28-14-/	PS407	1
18	8	PS204-8	PS204	2
19	8	PS412-15.43/15	PS412	1
20	8	PS206-8-1	PS206	1

PIECE MARKS

6820-R2-67047-02-1 6820-R2-67047-02-2 6820-R2-67047-02-3 / 1



SERVICE: R2	VAPOR/LIQUID: L	INSUL TYPE: Per LDT	INSUL THK: Per LDT	SHOP: Y	FIELD: Y	PAINT CODE: Per LDT	MODULE: -	
				P&ID: 202998C-001-PID-0021-0324				
				UNIT#: 6800	LEW AREA: 6820	SPEC: NOHD-NI01	STRESS CALC #: CN-0379	
				LINE No. 8"-R2-67047-NOHD-NI01-H				
				DRAWING NUMBER 6820-R2-67047-02				REV. 1
				OxyChem Redstone Battleground PROJECT				

