


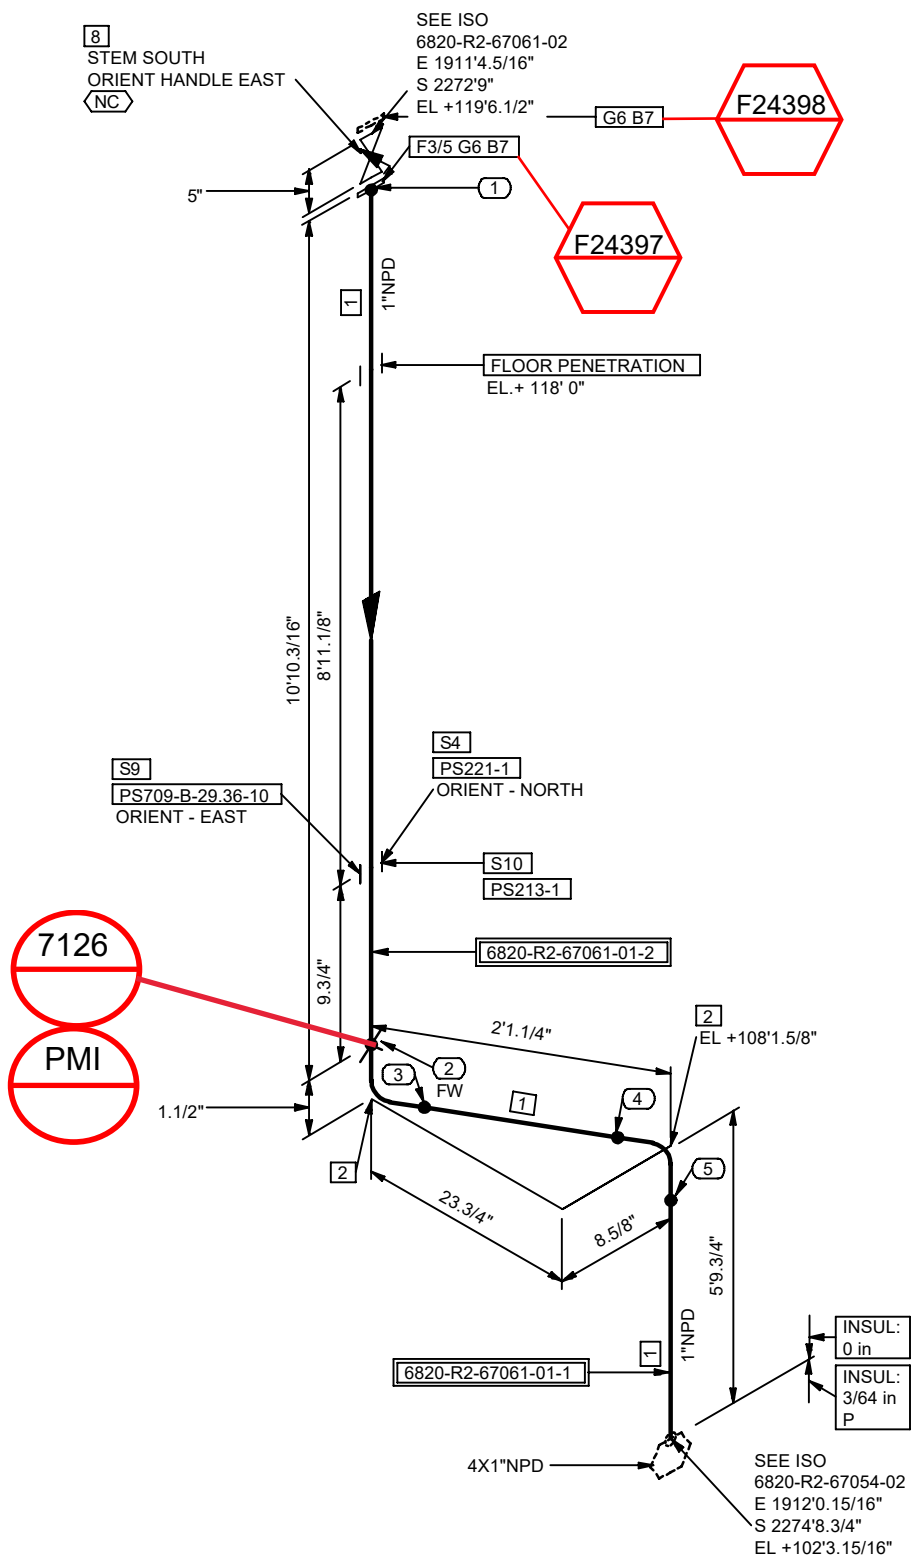

Filler Material Requisition  
Date: 1-7-25  
Line Class: NOHD-SS03  
WPS: 802  
Electrode: ER308L  
Signature: *Pedro Morin*

COORDINATE SYSTEM : PLANTCOORDINATES

NOTES:

- FOR LINE PRESSURES, TEMPERATURES, INSULATION TYPE AND THICKNESS, ETC. REFER TO LATEST REVISION OF LDT.
- FOR STANDARD PIPE SUPPORT DETAILS SEE PROJECT STANDARD.
- FIELD SHIM TO SUIT UNLESS OTHERWISE NOTED.
- FOR PWHT REQUIREMENTS REFER TO LINE CLASS SPECIFICATION.
- ALL THREADED PIPE LINE SYSTEMS, FIELD SHALL VERIFY DIMENSION PRIOR TO ERECTION.
- FFW DESIGNATION AT WELDS INDICATES FIELD FIT WELD, WHERE PIPE FABRICATOR IS TO ADD 9 INCH OF PIPE TO THE ISOMETRIC DIMENSION TO ENABLE THE FIELD TO CUT TO FIT AT SITE.
- REFER TO 202998C-000-W1-1300-0001 FOR FRP AND DUAL-LAM FABRICATION.



Information contained in this document is the work product of one or more legal entities of Technip Energies N.V. and embodies confidential and proprietary information of the applicable entity and/or its client. Use of this information is restricted in accordance with conditions specified by the contract. Technip Energies N.V. and its affiliates disclaim any and all liabilities for any changes or modifications to this document which are made by any person other than the entity that issued the document under the applicable client contract.

THIS DOCUMENT IS UNCONTROLLED WHEN REPRODUCED

|     |            |     |                         |      |     |        |       |
|-----|------------|-----|-------------------------|------|-----|--------|-------|
|     |            |     |                         |      |     |        |       |
|     |            |     |                         |      |     |        |       |
|     |            |     |                         |      |     |        |       |
|     |            |     |                         |      |     |        |       |
| 0   | 2024-12-27 | RVA | ISSUED FOR CONSTRUCTION | SAD  | KJK | SMR    | GR    |
| REV | DATE       | BY  | DESCRIPTION             | CHKD | MTD | STRESS | APRVD |

SHOP MATERIALS

| NO | NPD | DESCRIPTION                                                                        | IDENT    | QTY  |
|----|-----|------------------------------------------------------------------------------------|----------|------|
| 1  | 1   | Pipes, Seamless, ASME B36.19/B36.10, ASTM A312 Gr.TP304L, BE, -, -, S-40S          | C275NB8F | 18.3 |
| 2  | 1   | 90° Elb LR, Seamless, ASME B16.9, ASTM A403 Gr.WP304L, BW Ends, -, Annealed, S-40S | C80RG22P | 2    |
| 3  | 1   | LJ Flg, ASME B16.5, ASTM A105 Galv. as per ASTM A153, 150 Lbs, FF, -,              | C26WFFF7 | 1    |

PIPE SUPPORTS

|   |   |         |       |   |
|---|---|---------|-------|---|
| 4 | 1 | PS221-1 | PS221 | 1 |
|---|---|---------|-------|---|

MISCELLANEOUS COMPONENTS

|   |   |                                                                                   |          |   |
|---|---|-----------------------------------------------------------------------------------|----------|---|
| 5 | 1 | Stub SP, Seamless, ASME B16.9, ASTM A403 Gr.WP304L, BW Ends, -, Annealed, x S-40S | C8A5BKT4 | 1 |
|---|---|-----------------------------------------------------------------------------------|----------|---|

OTHER THAN SHOP MATERIALS

| NO | NPD | DESCRIPTION   | IDENT    | QTY |
|----|-----|---|----------|-----|
| 6  | 1   | NM Flat Gk, Barium Sulfate filled PTFE, 150 Lbs, RF as per ASME B16.5, -, Thk=1/8in, -,                                                      | C6S4K87F | 2   |
| 7  | 1/2 | SBlt 2 HHx N, A193 Gr.B7/A194 Gr.2H, -, Xylan PTFE Coated, - 2.75 in. Length                                                                 | C6S4K87U | 8   |
| 8  | 1   | Plug Flg, SP, Tapered Plug, Non Lubricated, API 599, ASTM A351 Gr.CF8M, 150 Lbs, RF, Ends as per ASME B16.5, -, LO, -, -, Valve Tag: PL-0548 | C76KHSRR | 1   |

PIPE SUPPORTS

|    |   |                  |       |   |
|----|---|------------------|-------|---|
| 9  | 1 | PS709-B-29.36-10 | PS709 | 1 |
| 10 | 1 | PS213-1          | PS213 | 1 |

PIECE MARKS

6820-R2-67061-01-1 6820-R2-67061-01-2



|                                                                                       |               |             |            |                           |            |             |                |  |
|---------------------------------------------------------------------------------------|---------------|-------------|------------|---------------------------|------------|-------------|----------------|--|
| SERVICE:                                                                              | VAPOR/LIQUID: | INSUL TYPE: | INSUL THK: | SHOP:                     | FIELD:     | PAINT CODE: | MODULE:        |  |
| R2                                                                                    | L             | Per LDT     | Per LDT    | Y                         | Y          | Per LDT     | -              |  |
|  |               |             |            | P&ID:                     |            |             |                |  |
|                                                                                       |               |             |            | 202998C-001-PID-0021-0324 |            |             |                |  |
|                                                                                       |               |             |            | UNIT#:                    | EW P AREA: | SPEC:       | STRESS CALC #: |  |
|                                                                                       |               |             |            | 6800                      | 6820       | NOHD-SS03   | -              |  |
|                                                                                       |               |             |            | LINE No.                  |            |             |                |  |
| OxyChem Redstone Battleground PROJECT                                                 |               |             |            | 1"-R2-67061-NOHD-SS03-N   |            |             |                |  |
|                                                                                       |               |             |            | DRAWING NUMBER            |            |             |                |  |
|                                                                                       |               |             |            | 6820-R2-67061-01          |            |             |                |  |
|                                                                                       |               |             |            |                           |            | REV.        |                |  |
|                                                                                       |               |             |            |                           |            | 0           |                |  |

