


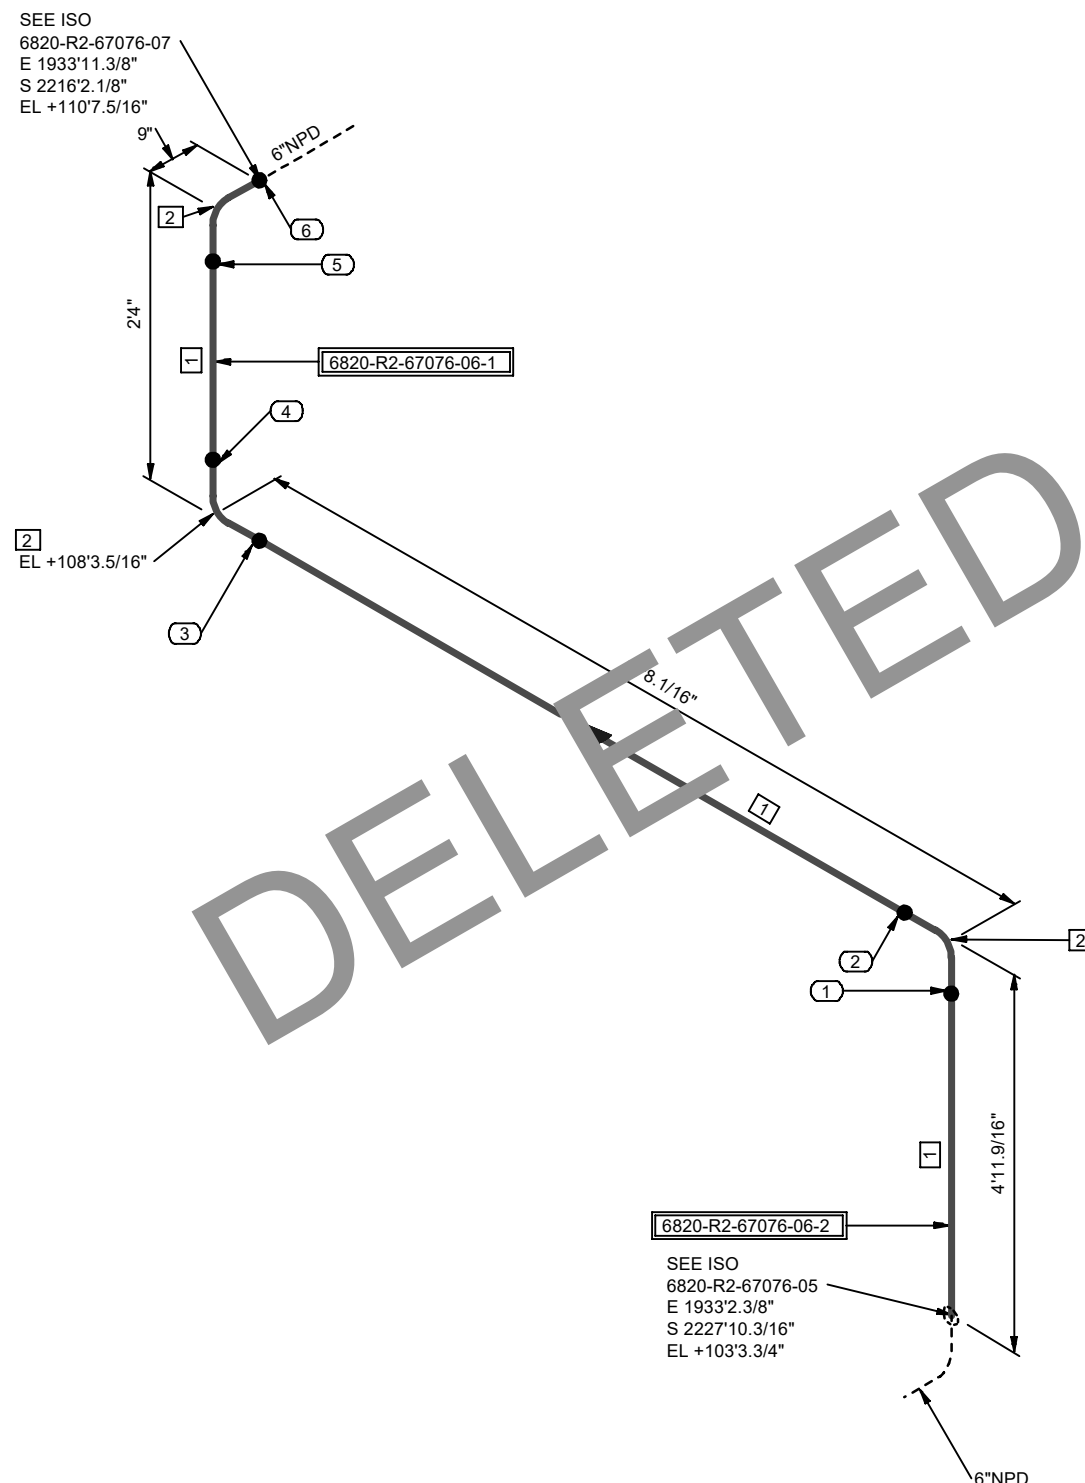


PIECE MARKS

6820-R2-67076-06-1 6820-R2-67076-06-2

COORDINATE SYSTEM : PLANTCOORDINATES

NOTES

1. FOR LINE PRESSURES, TEMPERATURES, INSULATION TYPE AND THICKNESS, ETC.
REFER TO LATEST REVISION OF LDT.
2. FOR STANDARD PIPE SUPPORT DETAILS SEE PROJECT STANDARD.
3. FIELD SHIM TO SUIT UNLESS OTHERWISE NOTED.
4. FOR PWHT REQUIREMENTS REFER TO LINE CLASS SPECIFICATION.
5. ALL THREADED PIPE LINE SYSTEMS, FIELD SHALL VERIFY DIMENSION PRIOR TO ERECTION.
6. FFW DESIGNATION AT WELDS INDICATES FIELD FIT WELD, WHERE PIPE FABRICATOR IS TO ADD
9 INCH OF PIPE TO THE ISOMETRIC DIMENSION TO ENABLE THE FIELD TO CUT TO FIT AT SITE.
7. REFER TO 202998C-000-W1-1300-0001 FOR FRP AND DUAL-LAM FABRICATION.

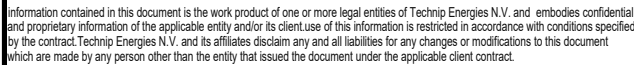

THIS DOCUMENT IS UNCONTROLLED WHEN REPRODUCED

1	2025-01-17	RVA	ISSUED FOR DELETION	SAD	KJK	SMR	GR
0	2024-07-26	RVA	ISSUED FOR CONSTRUCTION	SAD	KJK	BRD	GR
REV	DATE	BY	DESCRIPTION	CHKD	MTD	STRESS	APRVD

SERVICE: R2	VAPOR/LIQUID: L	INSUL TYPE: Per LDT	INSUL THK: Per LDT	SHOP: Y	FIELD: N	PAINT CODE: Per LDT	MODULE: -	
				P&ID: 202998C-001-PID-0021-0325				
				UNIT#: 6800	EWP AREA: 6820	SPEC: SCXL-CS02	STRESS CALC #: CN-0394	
				LINE No. 6"-R2-67076-SCXL-CS02-H				
				DRAWING NUMBER 6820-R2-67076-06				REV. 1
				OxyChem Redstone Battleground PROJECT				

26 JUL 2024 02:03

