


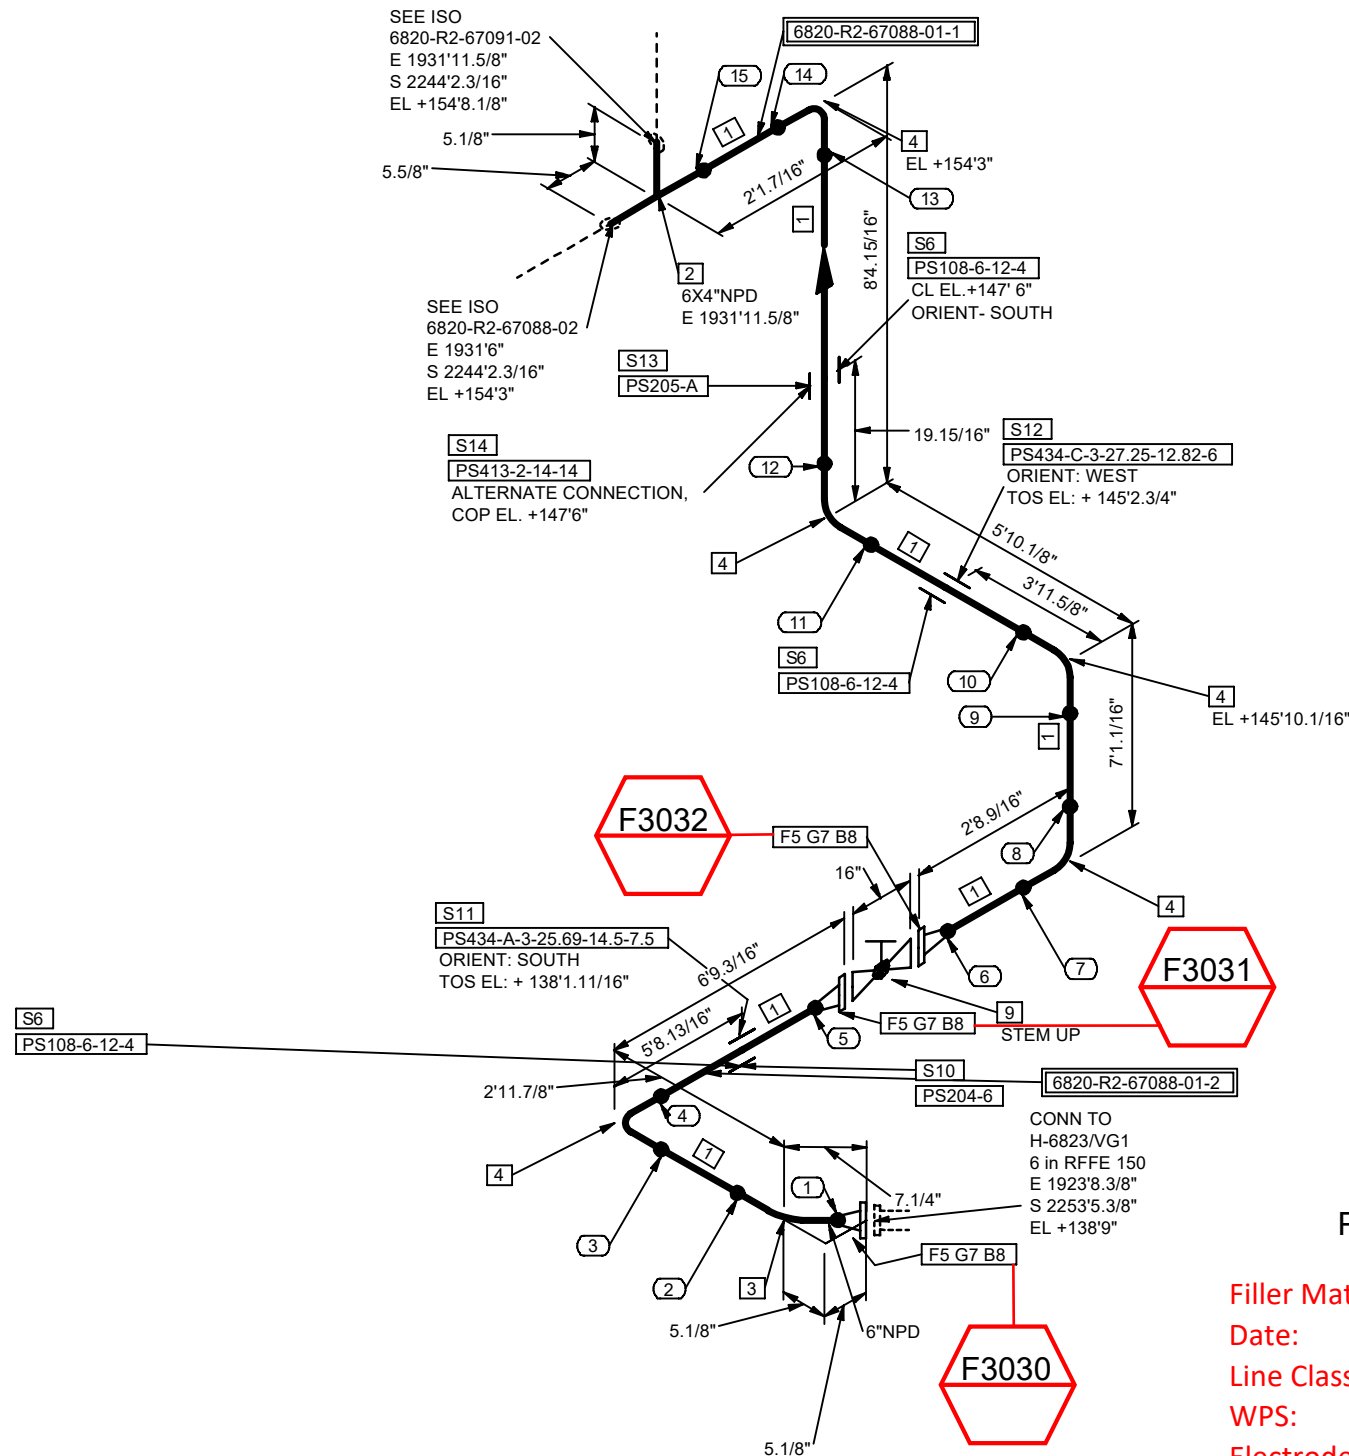

PWHT

Filler Material Requisition

Date: 8/23/24
Line Class: EPCW-CS01
WPS: 166
Electrode: ER70S-2
Signature: *Glenn Sumrall Jr*

SHOP MATERIALS

NO	NPD	DESCRIPTION	IDENT	QTY
1	6	Pipes, Seamless, ASME B36.10, ASTM A106 Gr.B, BE, -, -, S-STD	CPP00336	27.1
2	6X4	Red Te, Seamless, ASME B16.9, ASTM A234 Gr.WPB, BW Ends, -, -, S-STD	CDB0DGGR	1
3	6	45° Elb LR, Seamless, ASME B16.9, ASTM A234 Gr.WPB, BW Ends, -, -, S-STD	CDB66FSS	1
4	6	90° Elb LR, Seamless, ASME B16.9, ASTM A234 Gr.WPB, BW Ends, -, -, S-STD	CDB66GNP	5
5	6	WN Flg, ASME B16.5, ASTM A105N, 150 Lbs, RF/BW End, -, S-STD	CFG6WJH2	3

PIPE SUPPORTS

6	6	PS108-6-12-4	PS108	3
---	---	--------------	-------	---

OTHER THAN SHOP MATERIALS

NO	NPD	DESCRIPTION	IDENT	QTY
7	6	NM Flat Gk, Barium Sulfate filled PTFE, 150 Lbs, RF as per ASME B16.5, Full Face, Thk=1/8in, -, SBlt 2 HHx N, A193 Gr.B7/A194 Gr.2H, -, Xylan PTFE Coated, - 4.25 in. Length	C7CT1ZG1	3
8	3/4	Glo Flg, API 623, ASTM A216 Gr.WCB, 150 Lbs, RF, Ends as per ASME B16.5, HO, -, Valve Tag: GL-0627	C6S4K8BC	24
9	6		C84KV7D1	1

PIPE SUPPORTS

10	6	PS204-6	PS204	1
11	6	PS434-A-3-25.69-14.5-7.5	PS434	1
12	6	PS434-C-3-27.25-12.82-6	PS434	1
13	6	PS205-A	PS205	1
14	6	PS413-2-14-14	PS413	1

PIECE MARKS

6820-R2-67088-01-1 6820-R2-67088-01-2

COORDINATE SYSTEM : PLANTCOORDINATES

NOTES:

- FOR LINE PRESSURES, TEMPERATURES, INSULATION TYPE AND THICKNESS, ETC. REFER TO LATEST REVISION OF LDT.
- FOR STANDARD PIPE SUPPORT DETAILS SEE PROJECT STANDARD.
- FIELD SHIM TO SUIT UNLESS OTHERWISE NOTED.
- FOR PWHT REQUIREMENTS REFER TO LINE CLASS SPECIFICATION.
- ALL THREADED PIPE LINE SYSTEMS, FIELD SHALL VERIFY DIMENSION PRIOR TO ERECTION.
- FFW DESIGNATION AT WELDS INDICATES FIELD FIT WELD, WHERE PIPE FABRICATOR IS TO ADD 9 INCH OF PIPE TO THE ISOMETRIC DIMENSION TO ENABLE THE FIELD TO CUT TO FIT AT SITE.
- REFER TO 202998C-000-W1-1300-0001 FOR FRP AND DUAL-LAM FABRICATION.



Information contained in this document is the work product of one or more legal entities of Technip Energies N.V. and embodies confidential and proprietary information of the applicable entity and/or its client. Use of this information is restricted in accordance with conditions specified by the contract. Technip Energies N.V. and its affiliates disclaim any and all liabilities for any changes or modifications to this document which are made by any person other than the entity that issued the document under the applicable client contract.

THIS DOCUMENT IS UNCONTROLLED WHEN REPRODUCED

REV	DATE	BY	DESCRIPTION	CHKD	MTO	STRESS	APRVD
0	2024-08-17	RVA	ISSUED FOR CONSTRUCTION	SAD	KJK	SMR	GR

SERVICE:	VAPOR/LIQUID:	INSUL TYPE:	INSUL THK:	SHOP:	FIELD:	PAINT CODE:	MODULE:	
R2	L	Per LDT	Per LDT	Y	Y	Per LDT	-	
				P&ID:				
				202998C-001-PID-0021-0326				
				UNIT#:	EWPA AREA:	SPEC:	STRESS CALC #:	
				6800	6820	EPCW-CS01	CN-0398	
				LINE No:				
OxyChem Redstone Battleground PROJECT				6"-R2-67088-EPCW-CS01-H				
				DRAWING NUMBER				
				6820-R2-67088-01				



OxyChem Redstone Battleground PROJECT

