


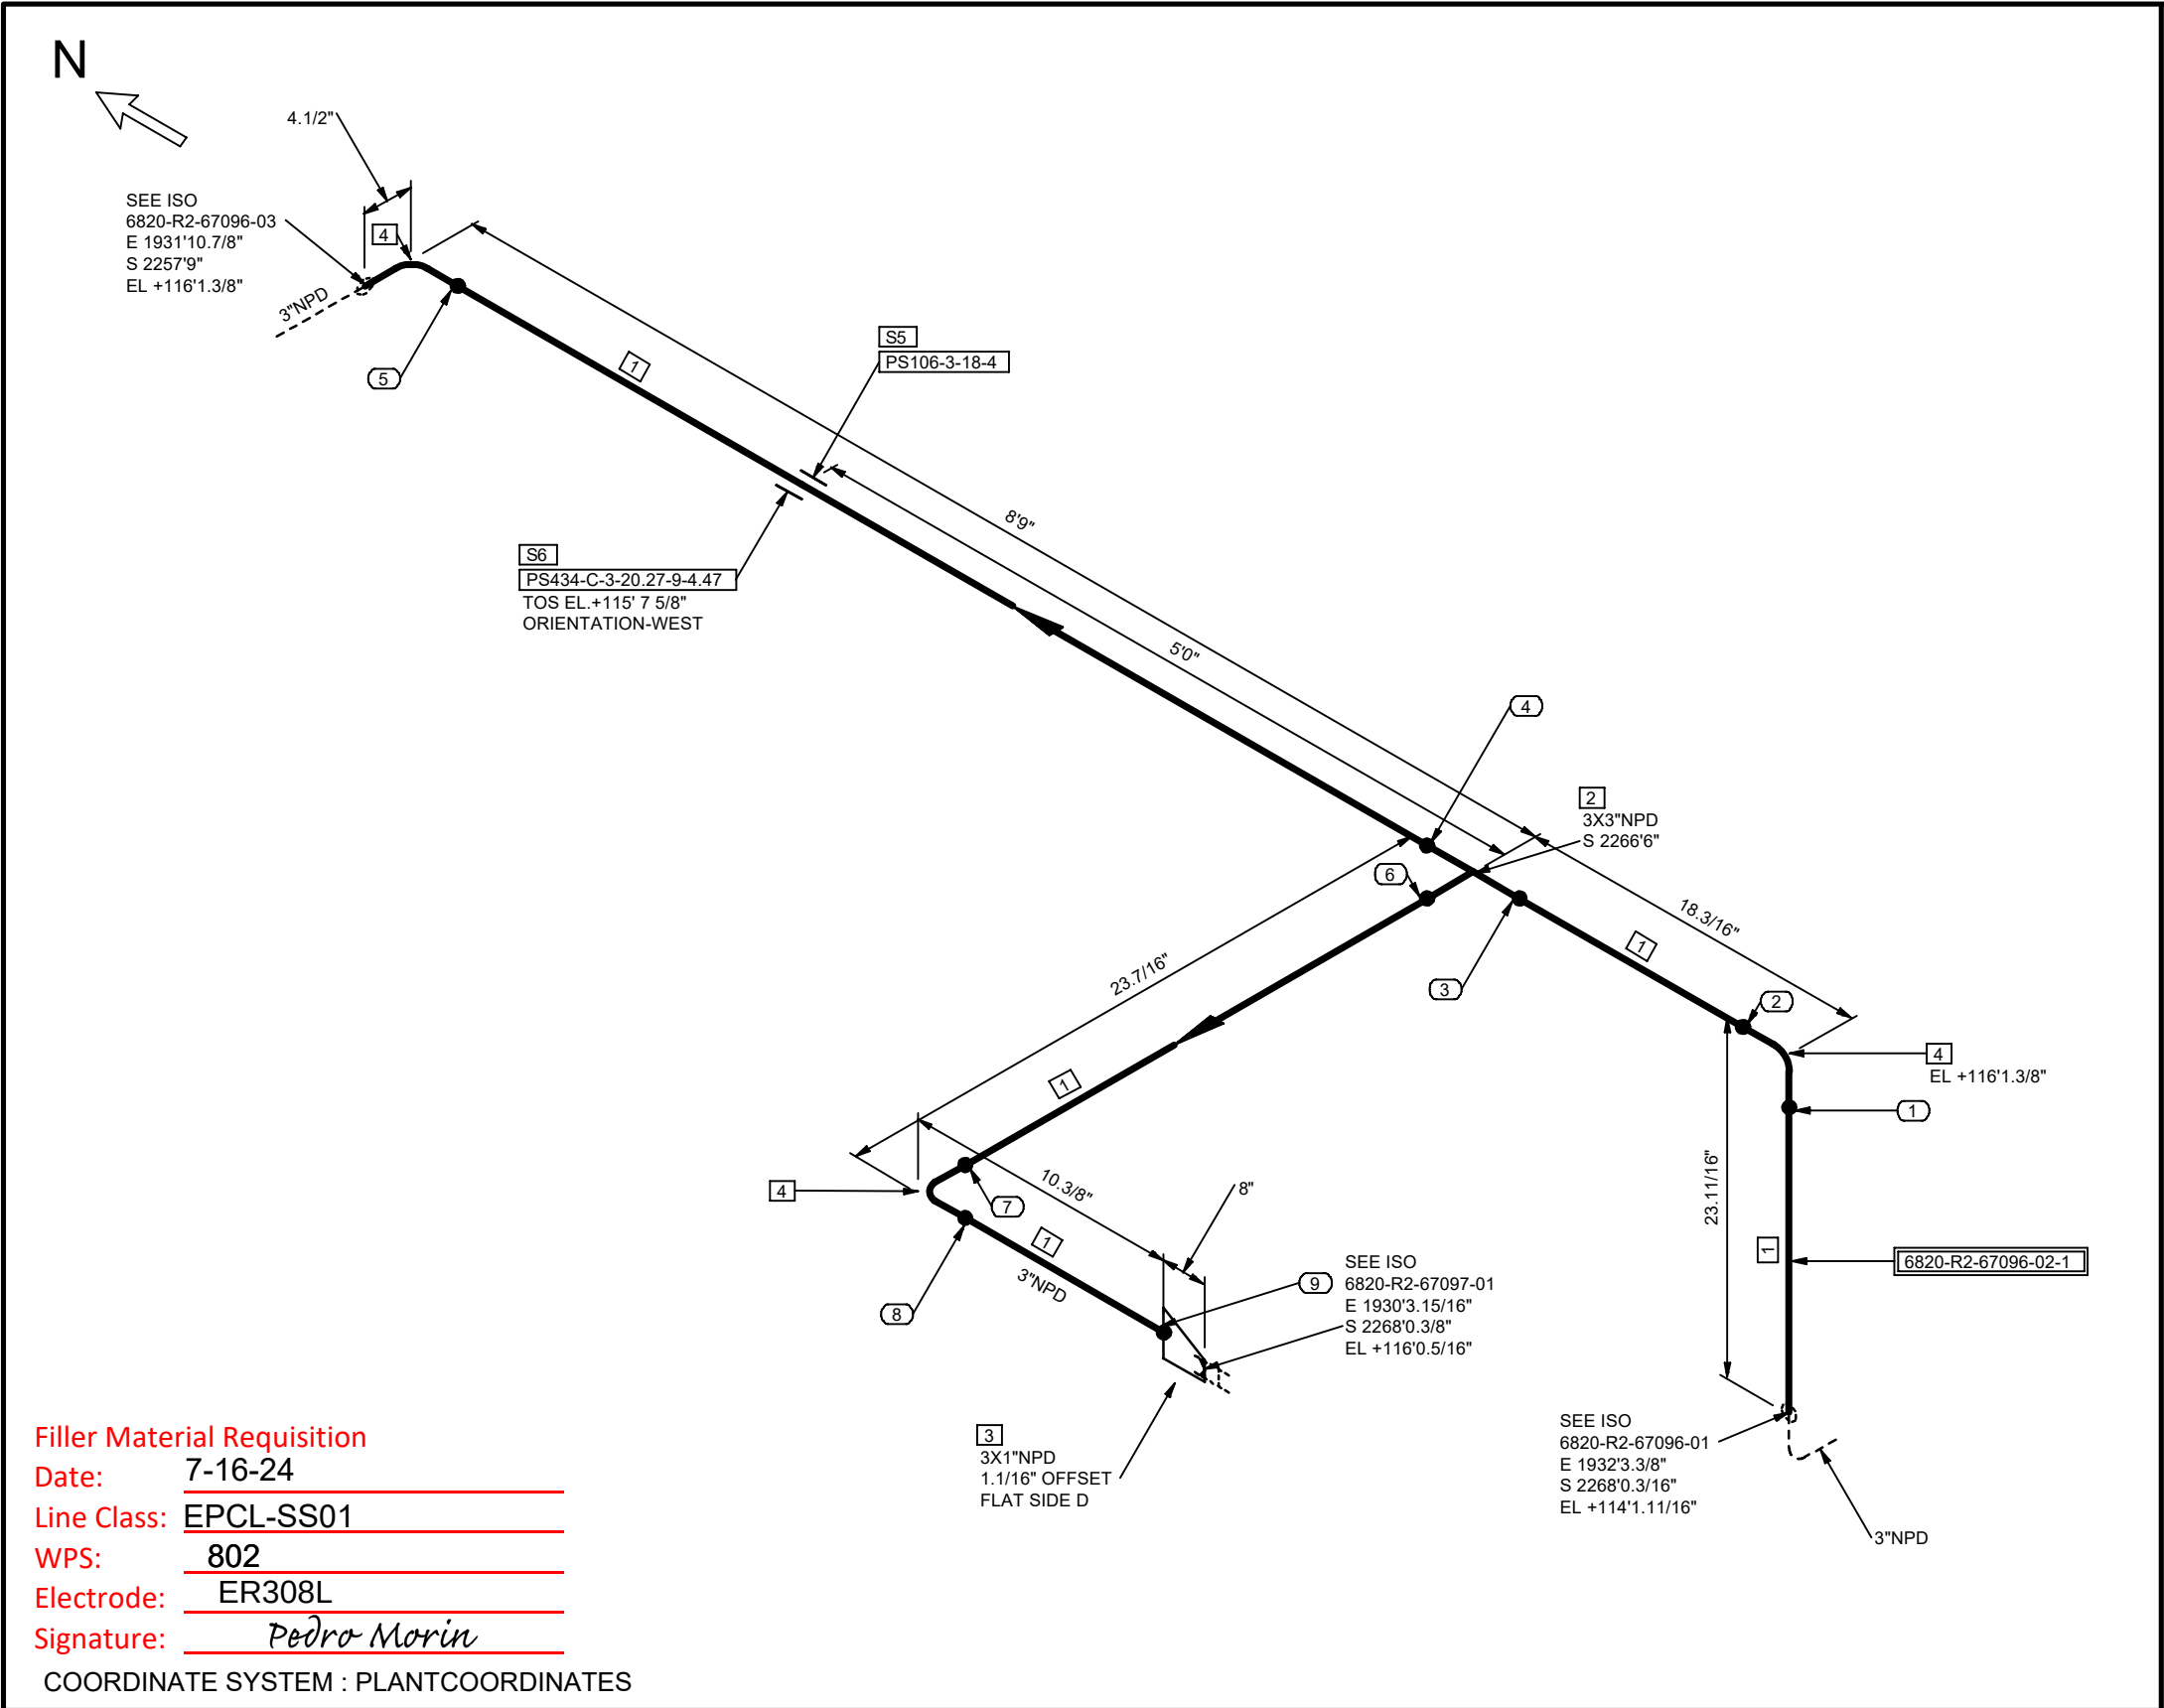

Filler Material Requisition
Date: 7-16-24
Line Class: EPCL-SS01
WPS: 802
Electrode: ER308L
Signature: Pedro Morin

COORDINATE SYSTEM : PLANTCOORDINATES

- NOTES:
- FOR LINE PRESSURES, TEMPERATURES, INSULATION TYPE AND THICKNESS, ETC. REFER TO LATEST REVISION OF LDT.
 - FOR STANDARD PIPE SUPPORT DETAILS SEE PROJECT STANDARD.
 - FIELD SHIM TO SUIT UNLESS OTHERWISE NOTED.
 - FOR PWHT REQUIREMENTS REFER TO LINE CLASS SPECIFICATION.
 - ALL THREADED PIPE LINE SYSTEMS, FIELD SHALL VERIFY DIMENSION PRIOR TO ERECTION.
 - FFW DESIGNATION AT WELDS INDICATES FIELD FIT WELD, WHERE PIPE FABRICATOR IS TO ADD 9 INCH OF PIPE TO THE ISOMETRIC DIMENSION TO ENABLE THE FIELD TO CUT TO FIT AT SITE.
 - REFER TO 202998C-000-W1-1300-0001 FOR FRP AND DUAL-LAM FABRICATION.



TECHNIP ENERGIES

Information contained in this document is the work product of one or more legal entities of Technip Energies N.V. and embodies confidential and proprietary information of the applicable entity and/or its client. Use of this information is restricted in accordance with conditions specified by the contract. Technip Energies N.V. and its affiliates disclaim any and all liabilities for any changes or modifications to this document which are made by any person other than the entity that issued the document under the applicable client contract.

THIS DOCUMENT IS UNCONTROLLED WHEN REPRODUCED

0	2024-07-12	RVA	ISSUED FOR CONSTRUCTION			SAD	KJK	BRD	GR
REV	DATE	BY	DESCRIPTION			CHKD	MTO	STRESS	APRVD

SHOP MATERIALS

NO	NPD	DESCRIPTION	IDENT	QTY
1	3	Pipes, Seamless, ASME B36.19/B36.10, ASTM A312 Gr.TP304L, BE, -, -, S-10S	CPP6WN1S	12.4
2	3X3	Eq Te, Seamless, ASME B16.9, ASTM A403 Gr.WP304L, BW Ends, -, Annealed, S-10S	C6SEUHT5	1
3	3X1	Eccentric swage, MSS SP-95, ASTM A403 Gr.WP304L, BE/NPTM End, -, Annealed, S-10S x S-80S	C7BP5PBR	1
4	3	90° Elb LR, Seamless, ASME B16.9, ASTM A403 Gr.WP304L, BW Ends, -, Annealed, S-10S	C6SEUJG7	3

PIPE SUPPORTS

5	3	PS106-3-18-4	PS106	1
---	---	--------------	-------	---

OTHER THAN SHOP MATERIALS

PIPE SUPPORTS

6	3	PS434-C-3-20.27-9-4.47	PS434	1
---	---	------------------------	-------	---

PIECE MARKS

6820-R2-67096-02-1

Turner Industries Group, LLC
Received
July 16, 2024
DOCUMENT CONTROL

SERVICE:	VAPOR/LIQUID:	INSUL TYPE:	INSUL THK:	SHOP:	FIELD:	PAINT CODE:	MODULE:
R2	L	Per LDT	Per LDT	Y	Y	Per LDT	-



OxyChem Redstone Battleground PROJECT

P&ID:
202998C-001-PID-0021-0326

UNIT#:	EWPA AREA:	SPEC:	STRESS CALC #:
6800	6820	EPCL-SS01	-

LINE No:
3"-R2-67096-EPCL-SS01-H

DRAWING NUMBER 6820-R2-67096-02			REV. 0
------------------------------------	--	--	-----------

