


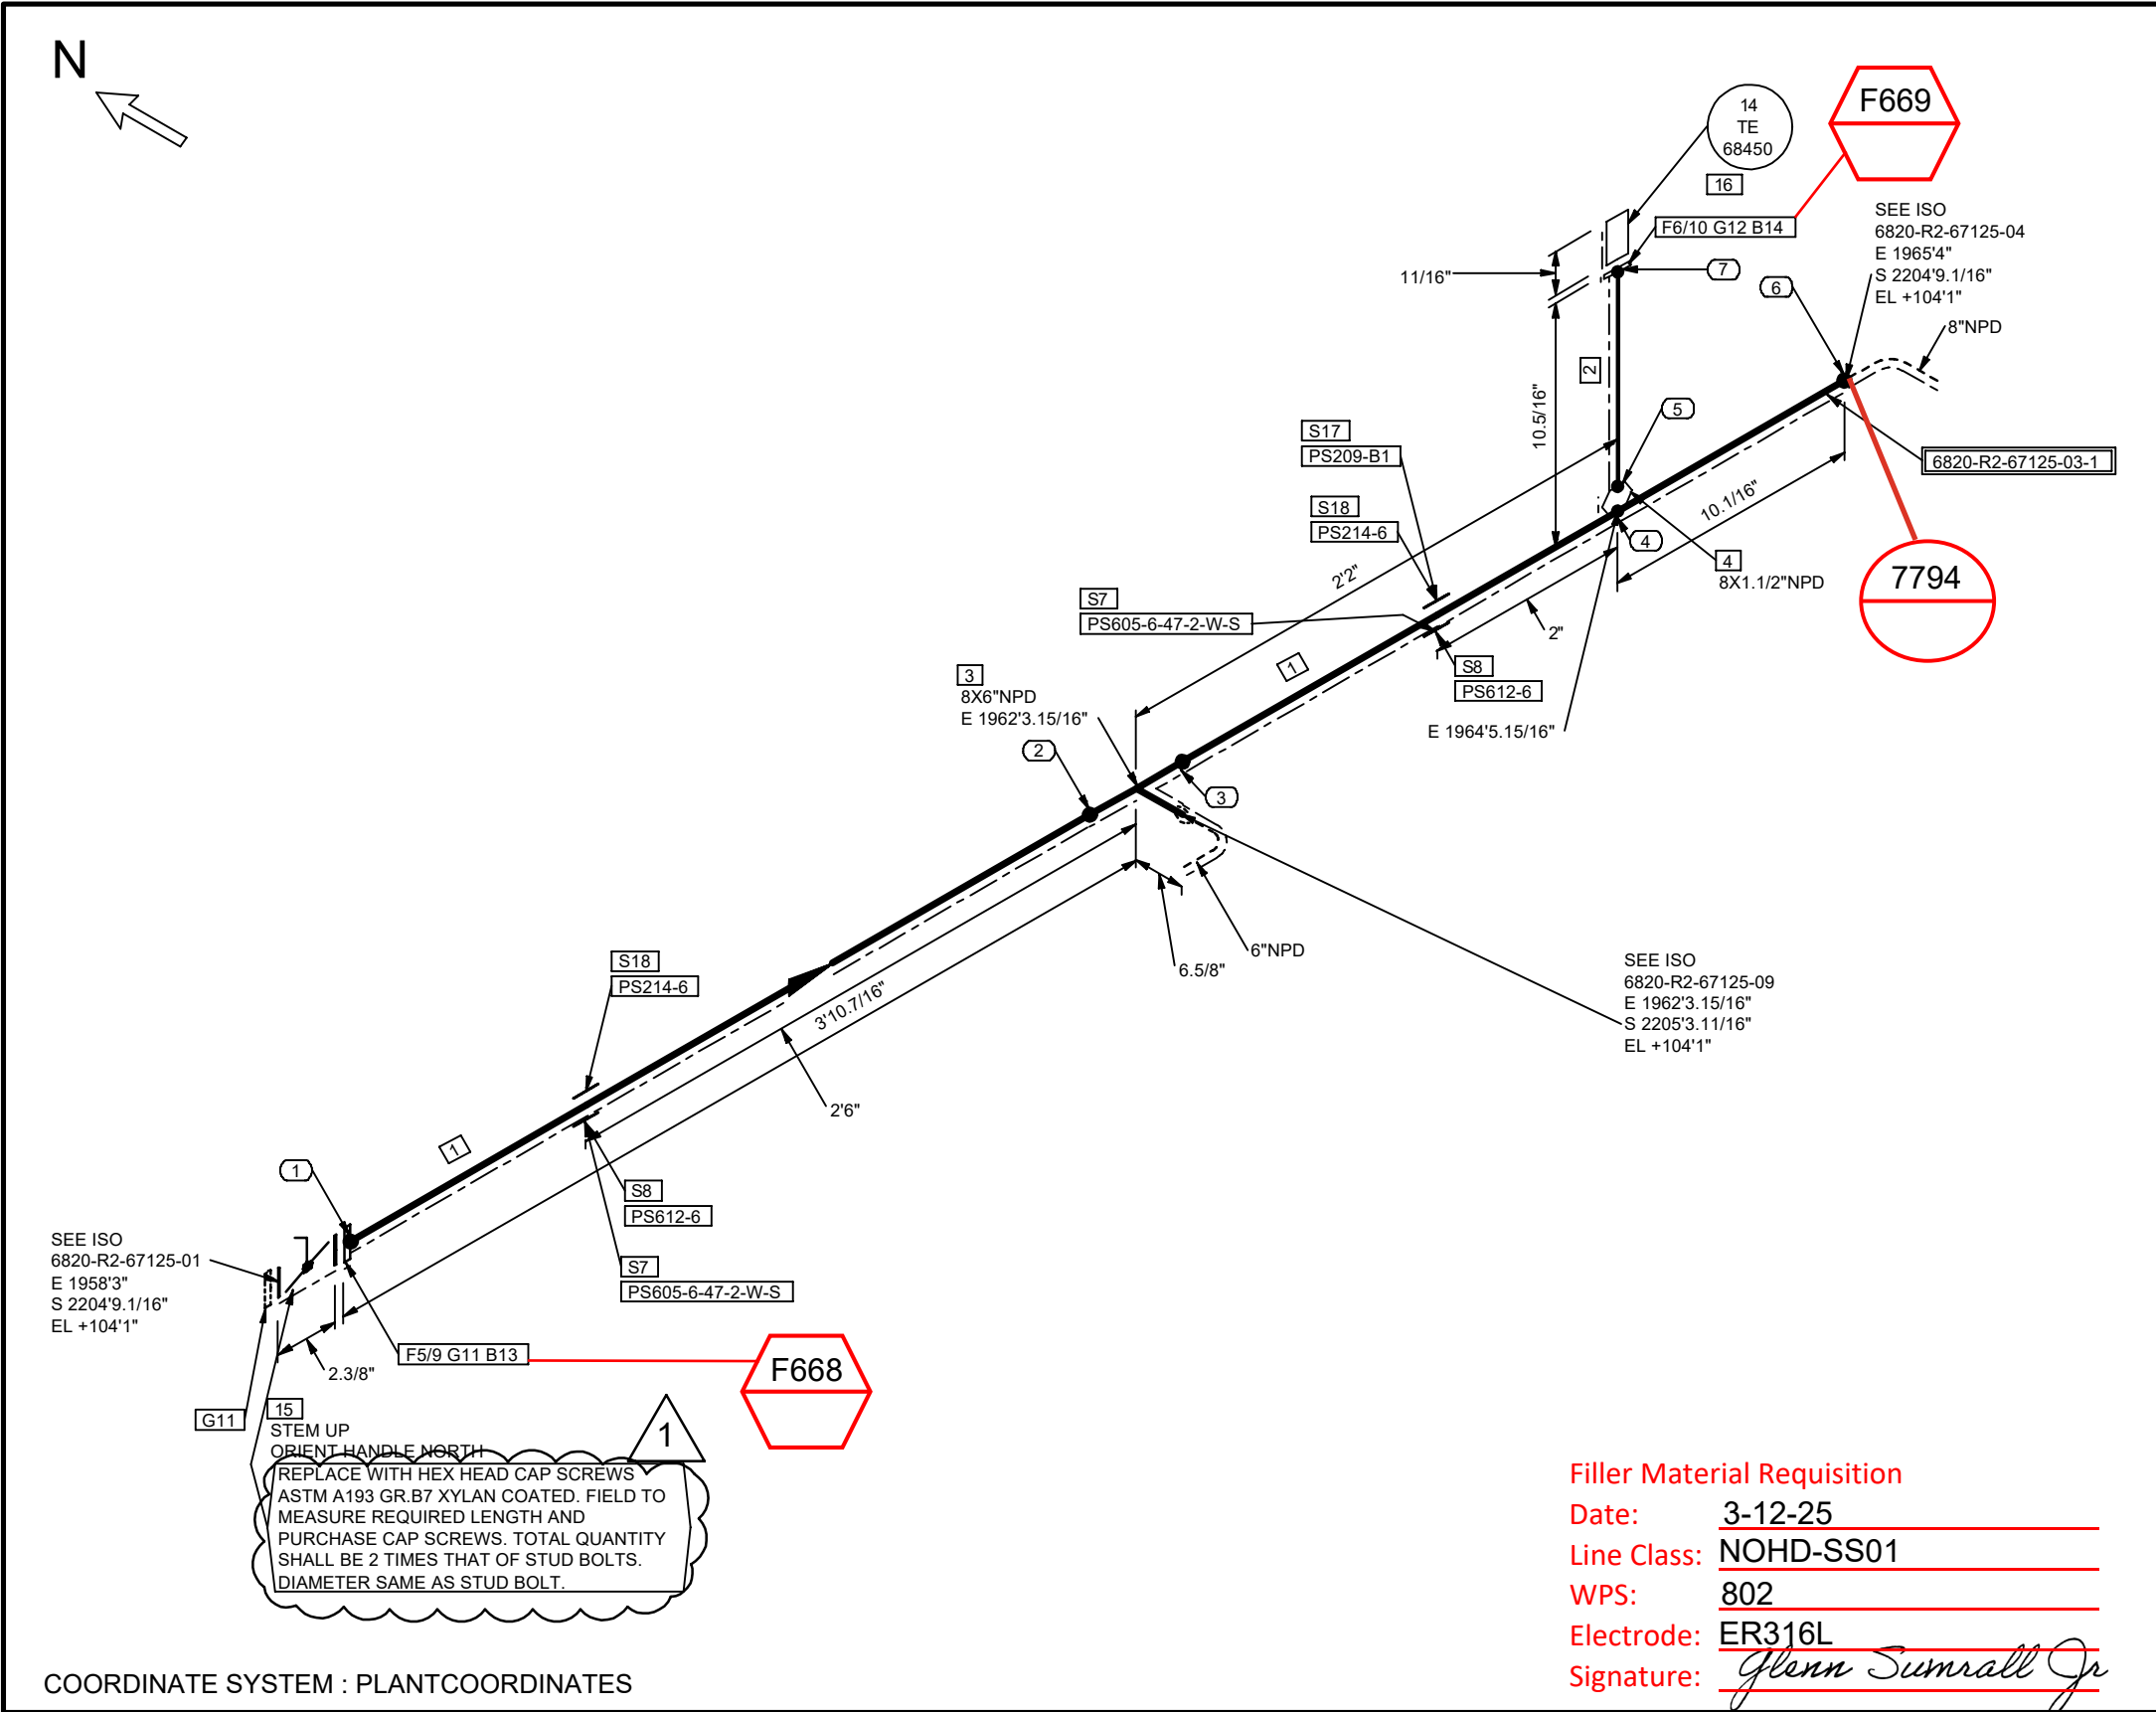

SHOP MATERIALS								
NO	NPD	DESCRIPTION	IDENT	QTY				
1	8	Pipes, Seamless, ASME B36.19/B36.10, ASTM A312 Gr.TP316L, BE, -, -, S-10S	CPPFEGLE	5.4 '				
2	1.1/2	Pipes, Seamless, ASME B36.19/B36.10, ASTM A312 Gr.TP316L, BE, -, -, S-40S	CYLECR2	0.3 '				
3	8X6	Red Te, Seamless, ASME B16.9, ASTM A403 Gr.WP316L, BW Ends, -,Annealed, S-10S	C6SDNT84	1				
4	8X1.1/2	Weldolet, MSS SP-97, ASTM A182 Gr.F316L, BW Ends, Annealed, S-10S x S-40S	C80R6C3P	1				
5	8	LJ Flg, ASME B16.5, ASTM A105 Galv. as per ASTM A153, 150 Lbs, FF, -,	C26WFFFR	1				
6	1.1/2	LJ Flg, ASME B16.5, ASTM A105 Galv. as per ASTM A153, 150 Lbs, FF, -,	C26WFFF9	1				
PIPE SUPPORTS								
7	8	PS605-6-47-2-W-S	PS605	2				
8	8	PS612-6	PS612	2				
MISCELLANEOUS COMPONENTS								
9	8	Stub SP, Seamless, ASME B16.9, ASTM A403 Gr.WP316L, BW Ends, -,Annealed, x S-10S	C8A57S3L	1				
10	1.1/2	Stub SP, Seamless, ASME B16.9, ASTM A403 Gr.WP316L, BW Ends, -,Annealed, x S-40S	C8A57RPB	1				
OTHER THAN SHOP MATERIALS								
NO	NPD	DESCRIPTION	IDENT	QTY				
11	8	NM Flat Gk, Barium Sulfate filled PTFE, 150 Lbs, RF as per ASME B16.5, -, Thk=1/8in, -,	C6SBWZF4	2				
12	1.1/2	NM Flat Gk, Barium Sulfate filled PTFE, 150 Lbs, RF as per ASME B16.5, -, Thk=1/8in, -,	C6S4K87H	1				
13	3/4	SBlt 2 HHx N, A193 Gr.B7/A194 Gr.2H, -, Xylan PTFE Coated, - 7.25 in. Length	C6S4K8BR	8				
14	1/2	SBlt 2 HHx N, A193 Gr.B7/A194 Gr.2H, -, Xylan PTFE Coated, - 2.75 in. Length	C6S4K87U	4				
15	8	But Waf, API 609 Cat.A, ASTM A395 Gr.60-40-18 PFA Lined and Epoxy Coated,150 Lbs, Lug-type RF, Ends as per ASME B16.5, GO,-, Valve Tag: BU-0808	C7CT0BXY	1				
INSTRUMENTS								
16	1.1/2	14-TE-68450	14-TE-68450	1				
PIPE SUPPORTS								
17	8	PS209-B1	PS209	1				
18	8	PS214-6	PS214	2				
PIECE MARKS								
6820-R2-67125-03-1								
Turner Industries Group, LLC Received MARCH 12, 2025 DOCUMENT CONTROL								
SERVICE:	VAPOR/LIQUID:	INSUL TYPE:	INSUL THK:	SHOP:	FIELD:	PAINT CODE:	MODULE:	
R2	L	Per LDT	Per LDT	Y	Y	Per LDT	-	
 OxyChem Redstone Battleground PROJECT					P&ID: 202998C-001-PID-0021-0328			
					UNIT#: 6800	EW P AREA: 6820	SPEC: NOHD-SS01	STRESS CALC #: CN-0392
					LINE No. 8"-R2-67125-NOHD-SS01-HET			
DRAWING NUMBER 6820-R2-67125-03					REV. 1			

NOTES:

- FOR LINE PRESSURES, TEMPERATURES, INSULATION TYPE AND THICKNESS, ETC. REFER TO LATEST REVISION OF LDT.
- FOR STANDARD PIPE SUPPORT DETAILS SEE PROJECT STANDARD.
- FIELD SHIM TO SUIT UNLESS OTHERWISE NOTED.
- FOR PWHT REQUIREMENTS REFER TO LINE CLASS SPECIFICATION.
- ALL THREADED PIPE LINE SYSTEMS, FIELD SHALL VERIFY DIMENSION PRIOR TO ERECTION.
- FFW DESIGNATION AT WELDS INDICATES FIELD FIT WELD, WHERE PIPE FABRICATOR IS TO ADD 9 INCH OF PIPE TO THE ISOMETRIC DIMENSION TO ENABLE THE FIELD TO CUT TO FIT AT SITE.
- REFER TO 202998C-000-W1-1300-0001 FOR FRP AND DUAL-LAM FABRICATION.

T.EN

TECHNIP ENERGIES

Information contained in this document is the work product of one or more legal entities of Technip Energies N.V. and embodies confidential and proprietary information of the applicable entity and/or its client. Use of this information is restricted in accordance with conditions specified by the contract. Technip Energies N.V. and its affiliates disclaim any and all liabilities for any changes or modifications to this document which are made by any person other than the entity that issued the document under the applicable client contract.

THIS DOCUMENT IS UNCONTROLLED WHEN REPRODUCED

REV	DATE	BY	DESCRIPTION	CHKD	MTO	STRESS	APRVD
1	2025-03-07	RVA	ISSUED FOR CONSTRUCTION	SAD	KJK	SMR	GR
0	2024-07-13	RVA	ISSUED FOR CONSTRUCTION	SAD	KJK	BRD	GR

