


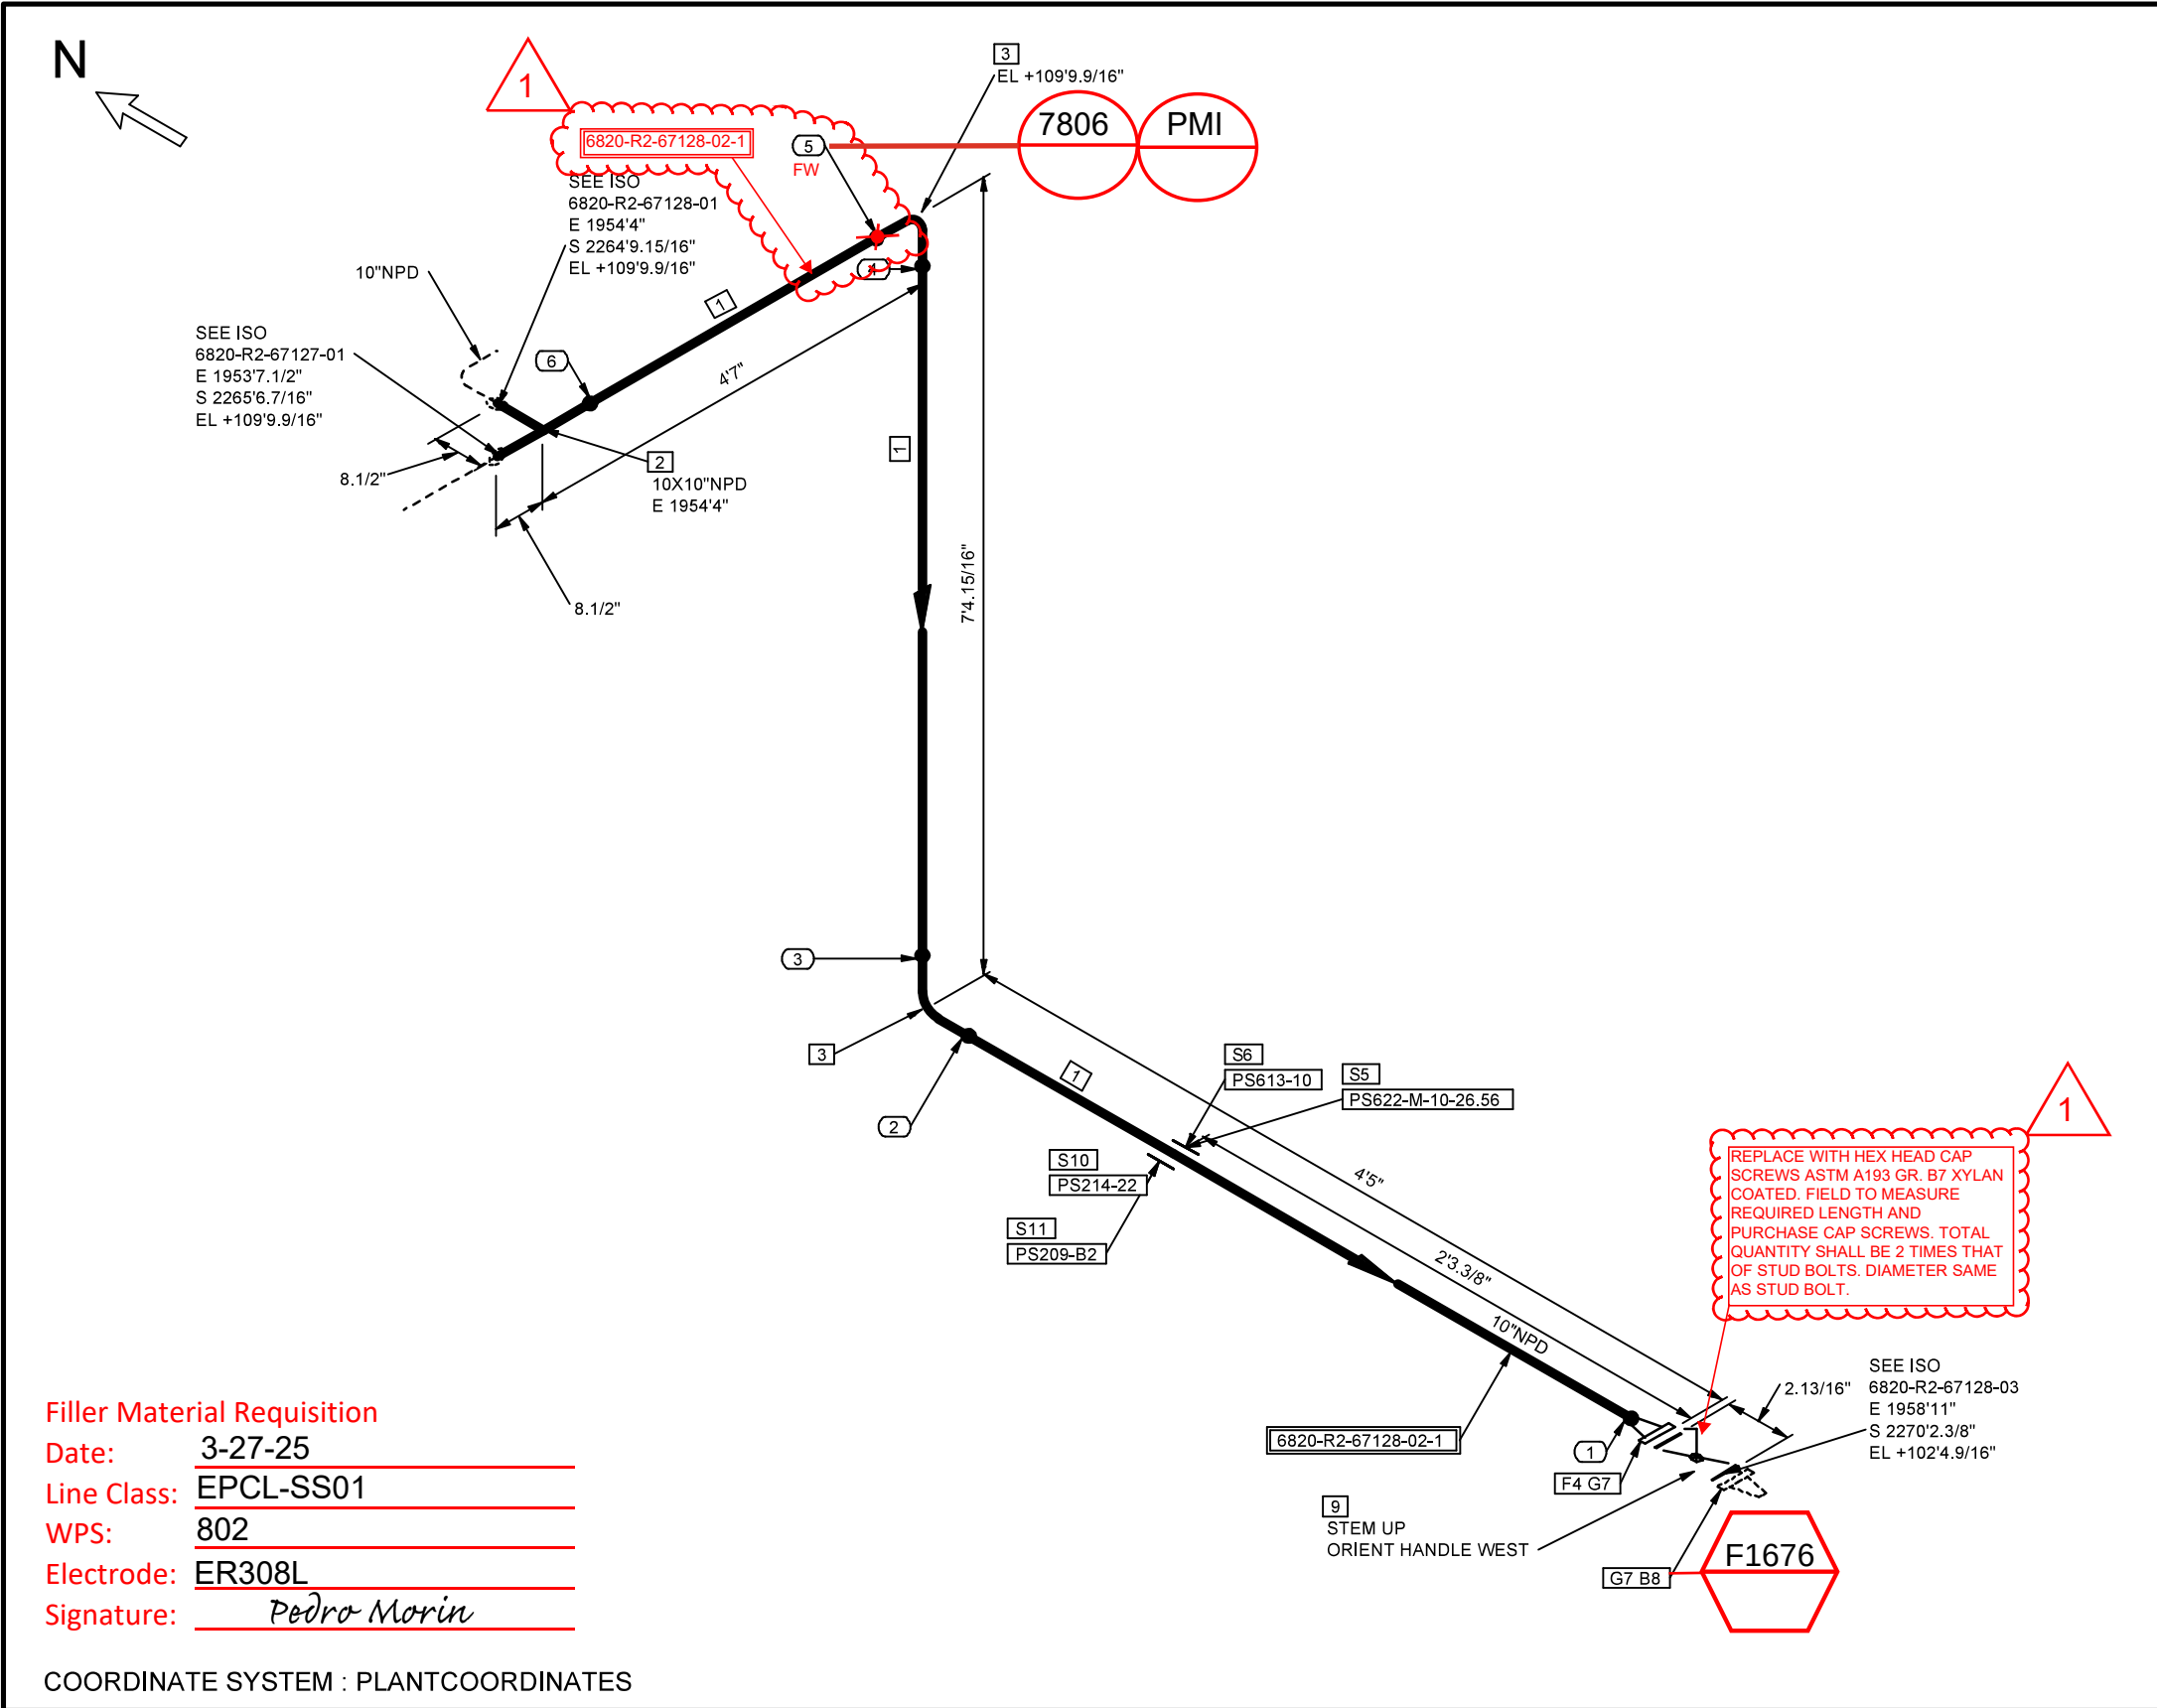

Filler Material Requisition  
Date: 3-27-25  
Line Class: EPCL-SS01  
WPS: 802  
Electrode: ER308L  
Signature: Pedro Morin

COORDINATE SYSTEM : PLANTCOORDINATES

NOTES:  
1. FOR LINE PRESSURES, TEMPERATURES, INSULATION TYPE AND THICKNESS, ETC. REFER TO LATEST REVISION OF LDT.  
2. FOR STANDARD PIPE SUPPORT DETAILS SEE PROJECT STANDARD.  
3. FIELD SHIM TO SUIT UNLESS OTHERWISE NOTED.  
4. FOR PWHT REQUIREMENTS REFER TO LINE CLASS SPECIFICATION.  
5. ALL THREADED PIPE LINE SYSTEMS, FIELD SHALL VERIFY DIMENSION PRIOR TO ERECTION.  
6. FFWD DESIGNATION AT WELDS INDICATES FIELD FIT WELD, WHERE PIPE FABRICATOR IS TO ADD 9 INCH OF PIPE TO THE ISOMETRIC DIMENSION TO ENABLE THE FIELD TO CUT TO FIT AT SITE.  
7. REFER TO 202998C-000-W1-1300-0001 FOR FRP AND DUAL-LAM FABRICATION.

T.EN

TECHNIP ENERGIES

Information contained in this document is the work product of one or more legal entities of Technip Energies N.V. and embodies confidential and proprietary information of the applicable entity and/or its client. Use of this information is restricted in accordance with conditions specified by the contract. Technip Energies N.V. and its affiliates disclaim any and all liabilities for any changes or modifications to this document which are made by any person other than the entity that issued the document under the applicable client contract.

THIS DOCUMENT IS UNCONTROLLED WHEN REPRODUCED

|     |            |     |                         |      |     |        |       |  |  |
|-----|------------|-----|-------------------------|------|-----|--------|-------|--|--|
|     |            |     |                         |      |     |        |       |  |  |
|     |            |     |                         |      |     |        |       |  |  |
|     |            |     |                         |      |     |        |       |  |  |
| 1   | 2025-03-21 | RVA | ISSUED FOR CONSTRUCTION | SAD  | KJK | SMR    | GR    |  |  |
| 0   | 2024-08-01 | RVA | ISSUED FOR CONSTRUCTION | SAD  | KJK | BRD    | GR    |  |  |
| REV | DATE       | BY  | DESCRIPTION             | CHKD | MTO | STRESS | APRVD |  |  |

| SHOP MATERIALS   |       |   |          |      |   |
|---|-------|---|----------|------|---|
| NO   | NPD   | DESCRIPTION   | IDENT    | QTY  |   |
| 1   | 10    | Pipes, Seamless, ASME B36.19/B36.10, ASTM A312 Gr.TP304L, BE, -, -, S-10S                                          | C7FCSP3  | 10.4 | ' |
| 2   | 10X10 | Eq Te, Seamless, ASME B16.9, ASTM A403 Gr.WP304L, BW Ends, -, Annealed, S-10S                                      | C6SEUHDU | 1    |   |
| 3   | 10    | 90° Elb LR, Seamless, ASME B16.9, ASTM A403 Gr.WP304L, BW Ends, -, Annealed, S-10S                                 | C6SEUJ3X | 2    |   |
| 4   | 10    | WN Flg, ASME B16.5, ASTM A182 Gr.F304L, 150 Lbs, RF/BW End, Annealed, S-10S                                        | C7W2U6KT | 1    |   |
| PIPE SUPPORTS   |       |   |          |      |   |
| 5   | 10    | PS622-M-10-26.56                                                                                                   | PS622    | 1    |   |
| 6   | 10    | PS613-10   | PS613    | 1    |   |
| OTHER THAN SHOP MATERIALS   |       |   |          |      |   |
| NO   | NPD   | DESCRIPTION   | IDENT    | QTY  |   |
| 7   | 10    | NM Flat Gk, Barium Sulfate filled PTFE, 150 Lbs, RF as per ASME B16.5, Full Face, Thk=1/8in, -,                    | C7CT1ZFL | 2    |   |
| 8   | 7/8   | SBlt 2 HHx N, A193 Gr.B7/A194 Gr.2H, -, Xylan PTFE Coated, - 7.5 in. Length                                        | C6S4K8D4 | 12   |   |
| 9   | 10    | But Waf, API 609 Cat.B, ASTM A351 Gr.CF8M, 150 Lbs, Lug-type RF, Ends as per ASME B16.5, GO, -, Valve Tag: BU-1191 | C8PLE43X | 1    |   |
| PIPE SUPPORTS   |       |   |          |      |   |
| 10   | 10    | PS214-22   | PS214    | 1    |   |
| 11   | 10    | PS209-B2   | PS209    | 1    |   |
| PIECE MARKS   |       |   |          |      |   |
| 6820-R2-67128-02-1 <span>6820-R2-67108-01-2</span>   |       |   |          |      |   |
| 1   |       |   |          |      |   |
| REPLACE WITH HEX HEAD CAP SCREWS ASTM A193 GR. B7 XYLAN COATED. FIELD TO MEASURE REQUIRED LENGTH AND PURCHASE CAP SCREWS. TOTAL QUANTITY SHALL BE 2 TIMES THAT OF STUD BOLTS. DIAMETER SAME AS STUD BOLT. |       |   |          |      |   |
| 1   |       |   |          |      |   |
| SEE ISO 6820-R2-67128-03 E 1958'11" S 2270'2.3/8" EL +102'4.9/16"   |       |   |          |      |   |
| F1676   |       |   |          |      |   |
| 9 STEM UP ORIENT HANDLE WEST   |       |   |          |      |   |
| 6820-R2-67128-02-1   |       |   |          |      |   |
| PS613-10, PS622-M-10-26.56, PS214-22, PS209-B2   |       |   |          |      |   |
| 4'5", 2'3.3/8", 10"NPD   |       |   |          |      |   |
| F4 G7, G7 B8   |       |   |          |      |   |
| 10X10"NPD, E 1954'4"   |       |   |          |      |   |
| SEE ISO 6820-R2-67127-01, E 1953'7.1/2", S 2265'6.7/16", EL +109'9.9/16"   |       |   |          |      |   |
| 10"NPD, 8.1/2"   |       |   |          |      |   |
| SEE ISO 6820-R2-67128-01, E 1954'4", S 2264'9.15/16", EL +109'9.9/16"   |       |   |          |      |   |
| FW   |       |   |          |      |   |
| 7806 PMI   |       |   |          |      |   |
| 1   |       |   |          |      |   |
| 7'4.15/16", 4'7"   |       |   |          |      |   |
| 1   |       |   |          |      |   |
| N   |       |   |          |      |   |

Turner Industries Group, LLC  
Received  
MARCH 27, 2025  
DOCUMENT CONTROL

|                                       |                 |                     |                    |                                 |                 |                     |                        |
|---------------------------------------|-----------------|---------------------|--------------------|---------------------------------|-----------------|---------------------|------------------------|
| SERVICE: R2                           | VAPOR/LIQUID: L | INSUL TYPE: Per LDT | INSUL THK: Per LDT | SHOP: Y                         | FIELD: Y        | PAINT CODE: Per LDT | MODULE: -              |
| P&ID: 202998C-001-PID-0021-0329       |                 |                     |                    | UNIT#: 6800                     | EWPA AREA: 6820 | SPEC: EPCL-SS01     | STRESS CALC #: CN-0401 |
| LINE No. 10"-R2-67128-EPCL-SS01-H     |                 |                     |                    | DRAWING NUMBER 6820-R2-67128-02 |                 |                     |                        |
| OxyChem Redstone Battleground PROJECT |                 |                     |                    | REV. 1                          |                 |                     |                        |

