



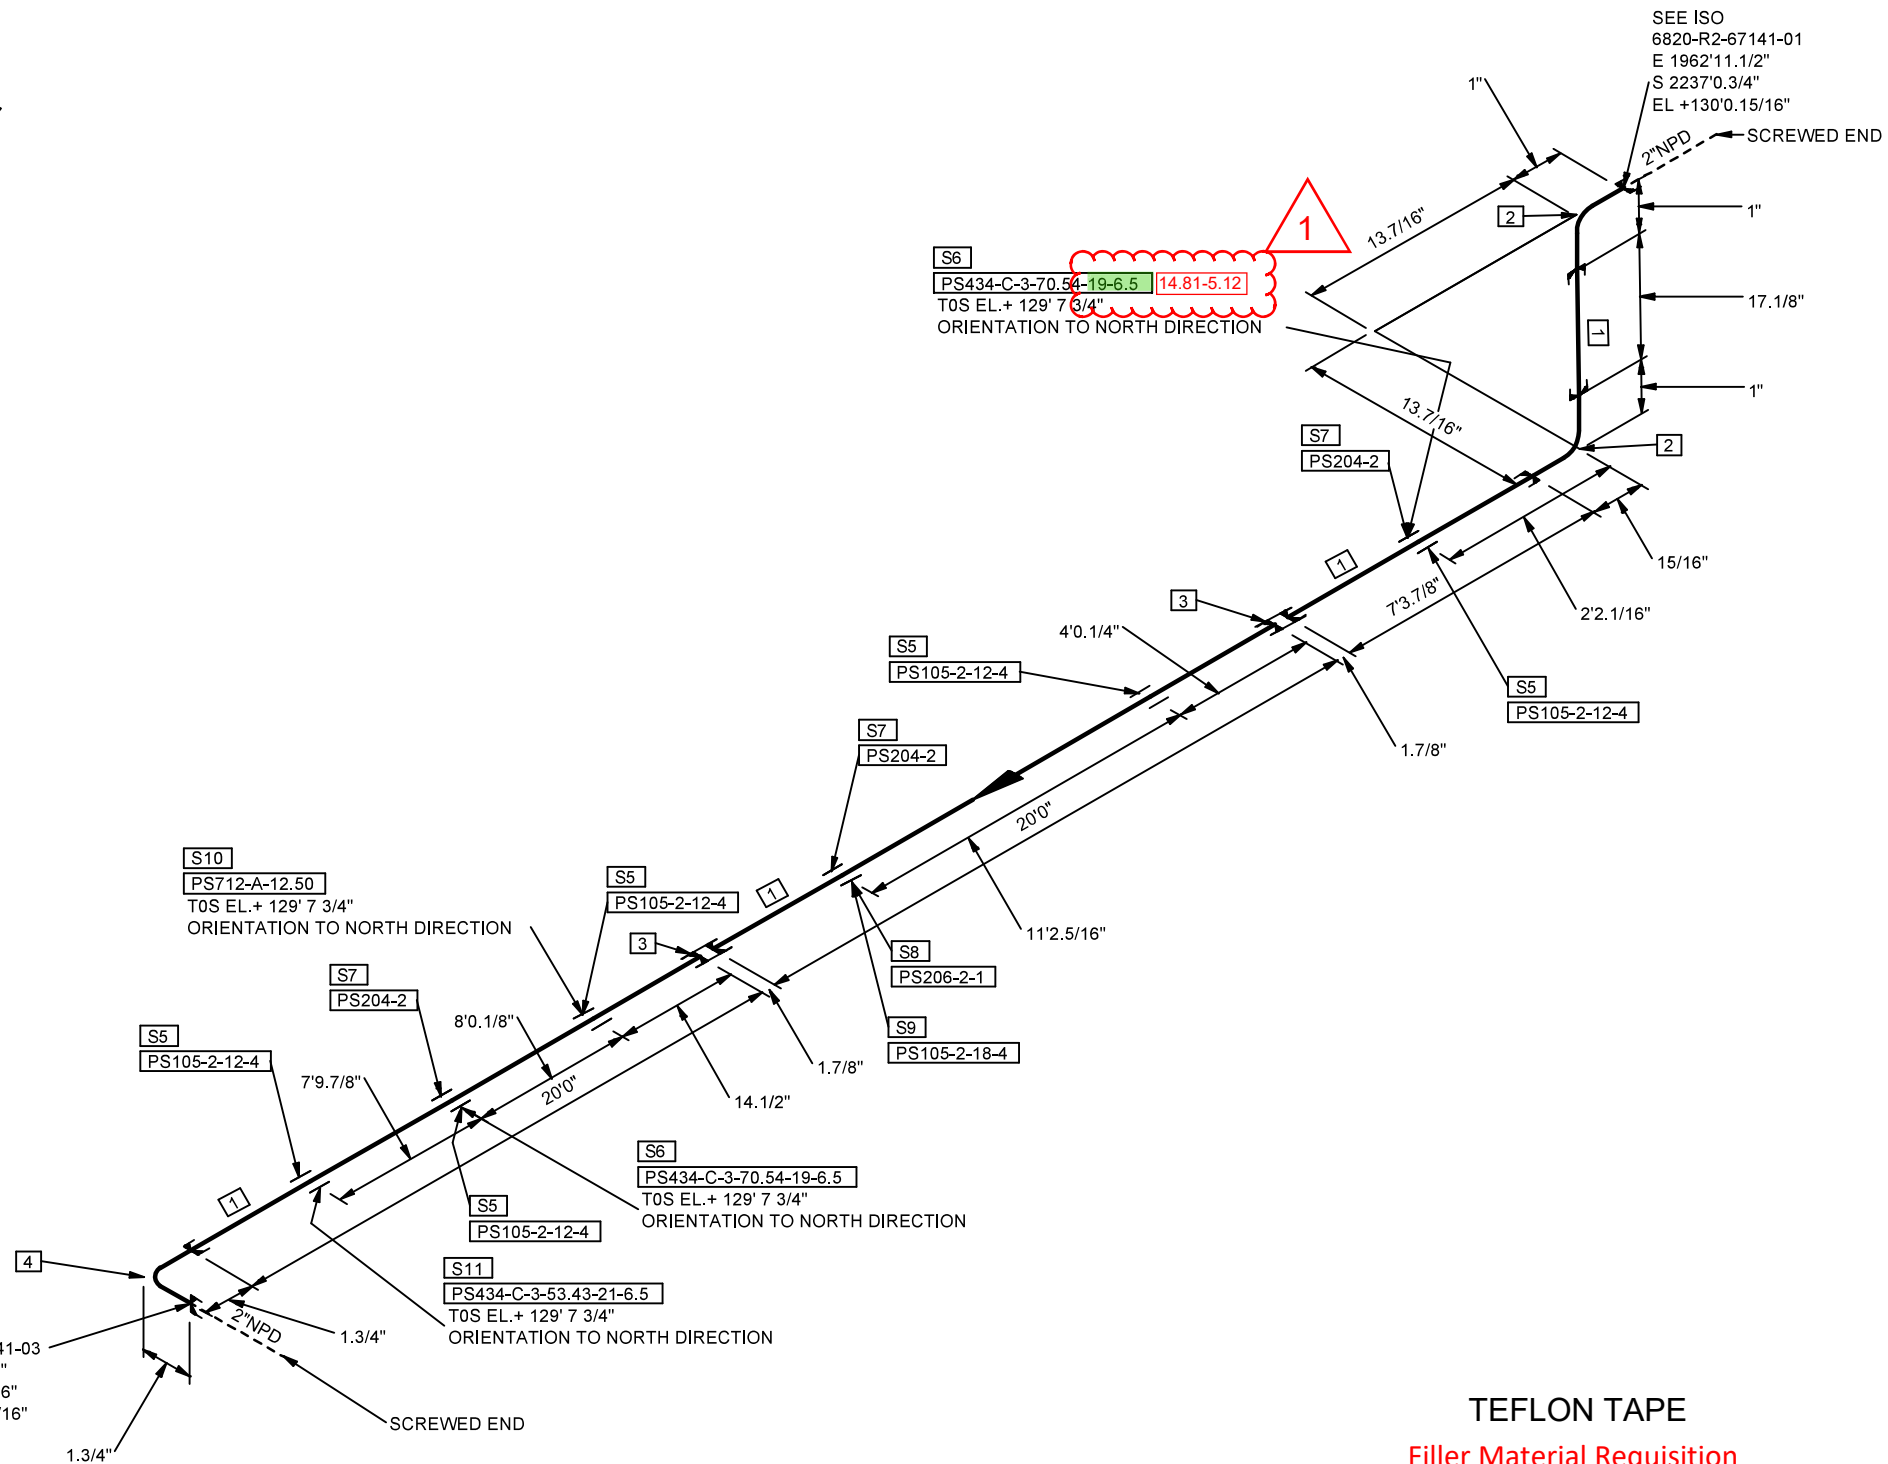

NOTES:

1. FOR LINE PRESSURES, TEMPERATURES, INSULATION TYPE AND THICKNESS, ETC. REFER TO LATEST REVISION OF LDT.
2. FOR STANDARD PIPE SUPPORT DETAILS SEE PROJECT STANDARD.
3. FIELD SHIM TO SUIT UNLESS OTHERWISE NOTED.
4. FOR PWHT REQUIREMENTS REFER TO LINE CLASS SPECIFICATION.
5. ALL THREADED PIPE LINE SYSTEMS, FIELD SHALL VERIFY DIMENSION PRIOR TO ERECTION.
6. FFW DESIGNATION AT WELDS INDICATES FIELD FIT WELD, WHERE PIPE FABRICATOR IS TO ADD 9 INCH OF PIPE TO THE ISOMETRIC DIMENSION TO ENABLE THE FIELD TO CUT TO FIT AT SITE.

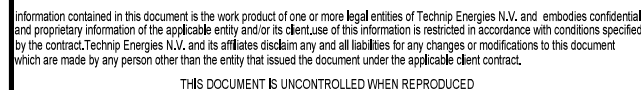

|     |            |     |                         |      |     |        |       |
|-----|------------|-----|-------------------------|------|-----|--------|-------|
|     |            |     |                         |      |     |        |       |
|     |            |     |                         |      |     |        |       |
|     |            |     |                         |      |     |        |       |
|     |            |     |                         |      |     |        |       |
| 1   | 2025-03-21 | RVA | ISSUED FOR CONSTRUCTION | SAD  | KJK | SMR    | GR    |
| 0   | 2024-06-28 | RVA | ISSUED FOR CONSTRUCTION | SAD  | KJK | BRD    | GR    |
| REV | DATE       | BY  | DESCRIPTION             | CHKD | MTO | STRESS | APRVD |

Turner Industries Group, LLC  
Received  
MARCH 27, 2025  
DOCUMENT CONTROL

Signature: Pedro Morin

|                                                                                       |                    |                        |                       |                                     |                    |                        |                     |
|---------------------------------------------------------------------------------------|--------------------|------------------------|-----------------------|-------------------------------------|--------------------|------------------------|---------------------|
| SERVICE:<br>R2                                                                        | VAPOR/LIQUID:<br>L | INSUL TYPE:<br>Per LDT | INSUL THK:<br>Per LDT | SHOP:<br>N                          | FIELD:<br>Y        | PAINT CODE:<br>Per LDT | MODULE:<br>-        |
|  |                    |                        |                       | PID:<br>202998C-001-PID-0021-0329   |                    |                        |                     |
|                                                                                       |                    |                        |                       | UNIT#:<br>6800                      | EQIP AREA:<br>6820 | SPEC:<br>EPCL-SS01     | STRESS CALC #:<br>- |
|                                                                                       |                    |                        |                       | LINE No.<br>2"-R2-67141-EPCL-SS01-H |                    |                        |                     |
|                                                                                       |                    |                        |                       | DRAWING NUMBER<br>6820-R2-67141-02  |                    |                        |                     |
| OxyChem Redstone Battleground PROJECT                                                 |                    |                        |                       | REV.<br>1                           |                    |                        |                     |