


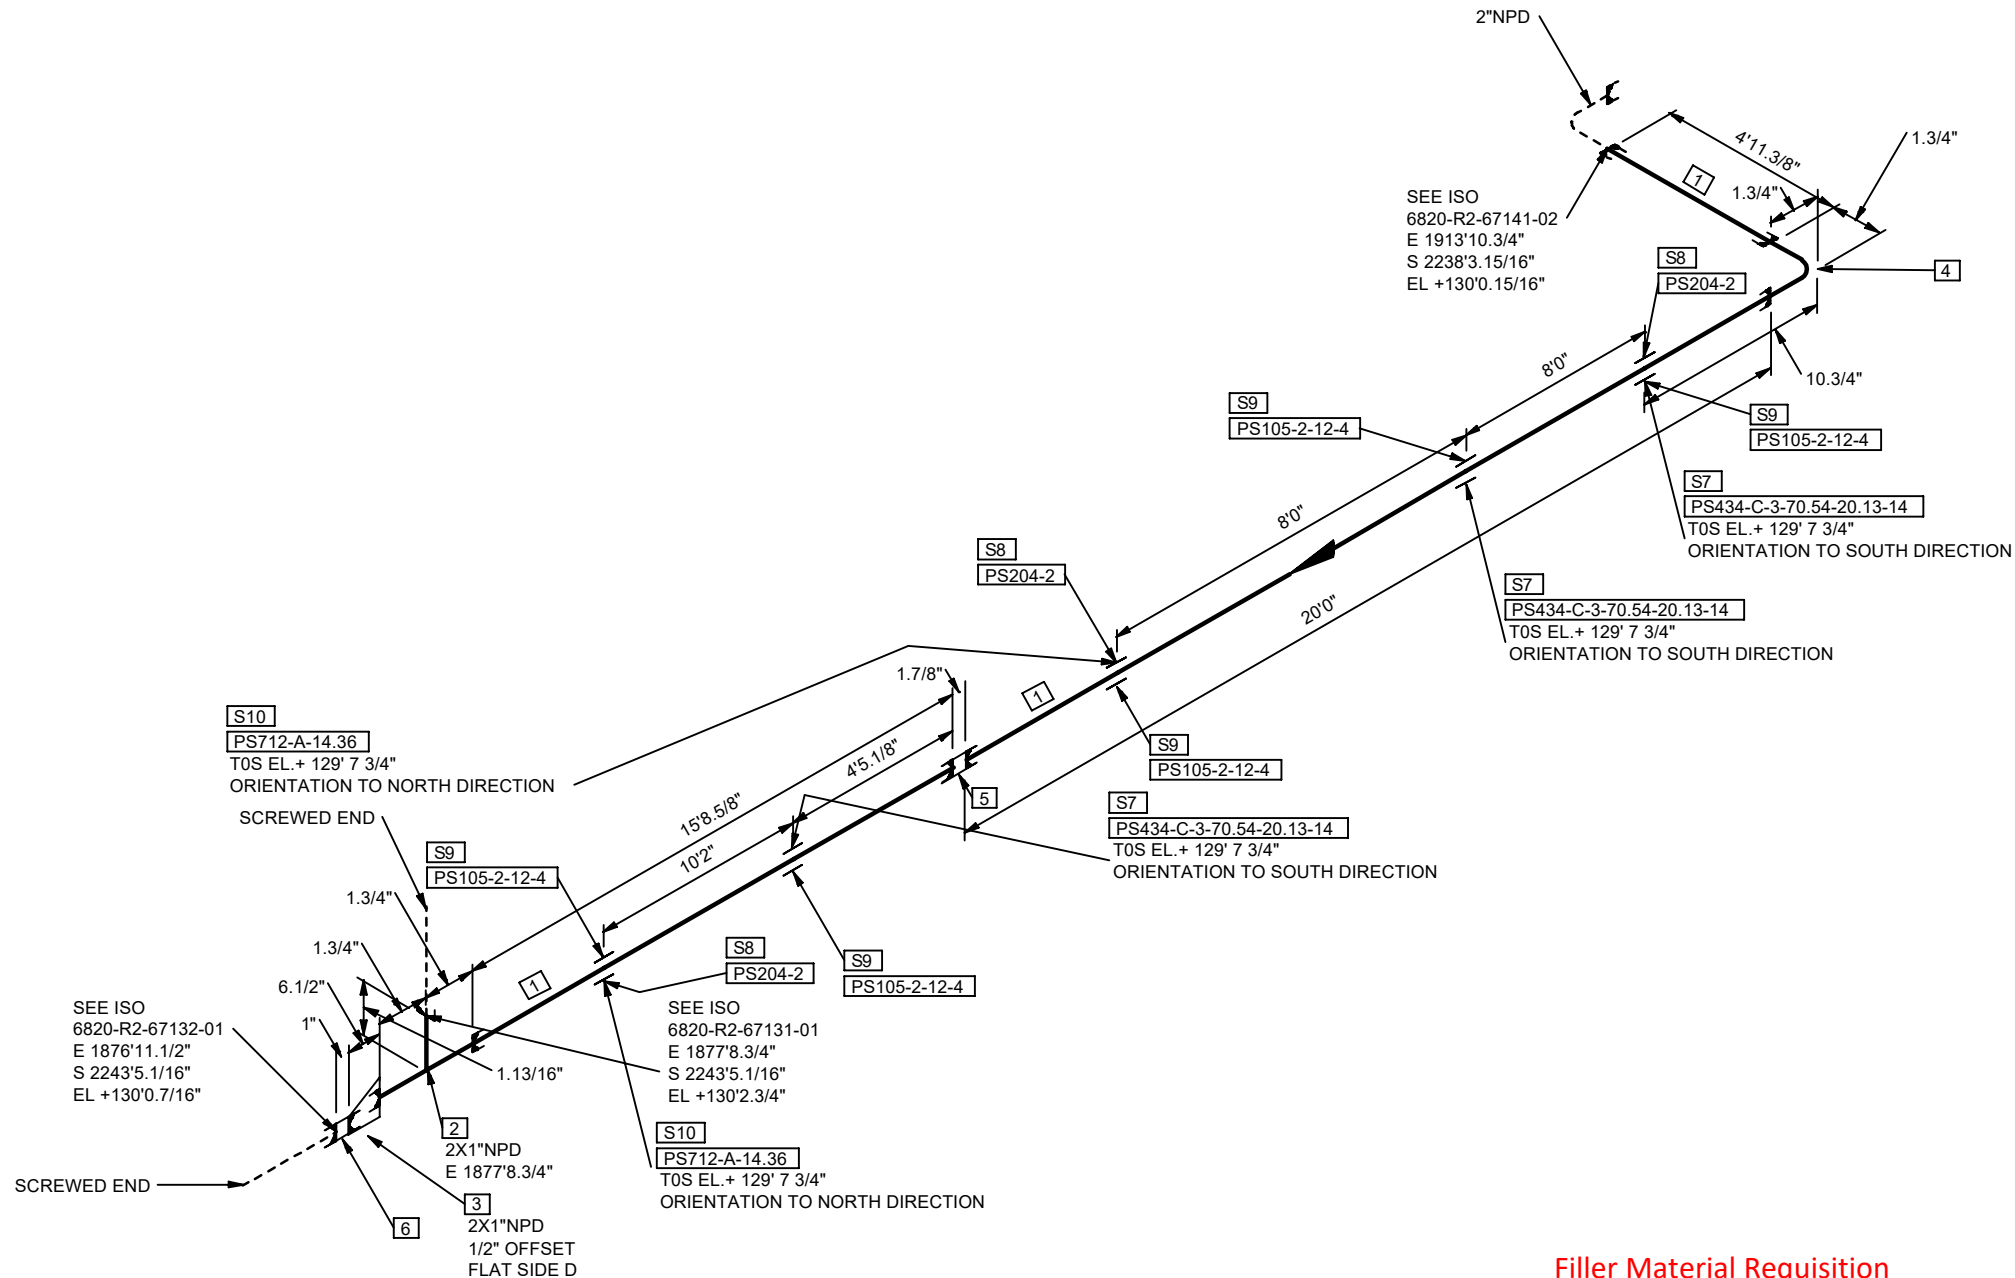

Filler Material Requisition
Date: 7-1-24
Line Class: EPCL-SS01
WPS: 802
Electrode: NO FIELD
Signature: *Pedro Morin*

COORDINATE SYSTEM : PLANTCOORDINATES

NOTES:

- FOR LINE PRESSURES, TEMPERATURES, INSULATION TYPE AND THICKNESS, ETC. REFER TO LATEST REVISION OF LDT.
- FOR STANDARD PIPE SUPPORT DETAILS SEE PROJECT STANDARD.
- FIELD SHIM TO SUIT UNLESS OTHERWISE NOTED.
- FOR PWHT REQUIREMENTS REFER TO LINE CLASS SPECIFICATION.
- ALL THREADED PIPE LINE SYSTEMS, FIELD SHALL VERIFY DIMENSION PRIOR TO ERECTION.
- FFW DESIGNATION AT WELDS INDICATES FIELD FIT WELD, WHERE PIPE FABRICATOR IS TO ADD 9 INCH OF PIPE TO THE ISOMETRIC DIMENSION TO ENABLE THE FIELD TO CUT TO FIT AT SITE.



Information contained in this document is the work product of one or more legal entities of Technip Energies N.V. and embodies confidential and proprietary information of the applicable entity and/or its client. Use of this information is restricted in accordance with conditions specified by the contract. Technip Energies N.V. and its affiliates disclaim any and all liabilities for any changes or modifications to this document which are made by any person other than the entity that issued the document under the applicable client contract.

THIS DOCUMENT IS UNCONTROLLED WHEN REPRODUCED

0	2024-06-28	RVA	ISSUED FOR CONSTRUCTION	SAD	KJK	BRD	GR		
REV	DATE	BY	DESCRIPTION	CHKD	MTO	STRESS	APRVD		

OTHER THAN SHOP MATERIALS

NO	NPD	DESCRIPTION	IDENT	QTY
1	2	Pipes, Seamless, ASME B36.19/B36.10, ASTM A312 Gr.TP304L, NPTM Ends, w/ coupling, -, S-80S	C76KFFWK	40.7
2	2X1	Red Te, ASME B16.11, ASTM A182 Gr.F304L, 3000 Lbs, NPTF Ends, Annealed,	C7BP5GZ7	1
3	2X1	Eccentric swage, MSS SP-95, ASTM A403 Gr.WP304L,NPTM Ends,-, Annealed, S-80S	C7BP5N1K	1
4	2	90° Elb, ASME B16.11, ASTM A182 Gr.F304L, 3000 Lbs, NPTF Ends, Annealed,	C7BP5GGZ	1
5	2	Full Coup, ASME B16.11, ASTM A182 Gr.F304L, 3000 Lbs, NPTF Ends, Annealed,	C7BP51NY	1
6	1	Full Coup, ASME B16.11, ASTM A182 Gr.F304L, 3000 Lbs, NPTF Ends, Annealed,	C7BP51NV	1

PIPE SUPPORTS

7	2	PS434-C-3-70.54-20.13-14	PS434	3
8	2	PS204-2	PS204	3
9	2	PS105-2-12-4	PS105	5
10	2	PS712-A-14.36	PS712	2



SERVICE:	VAPOR/LIQUID:	INSUL TYPE:	INSUL THK:	SHOP:	FIELD:	PAINT CODE:	MODULE:	
R2	L	Per LDT	Per LDT	N	Y	Per LDT	-	
 OxyChem Redstone Battleground PROJECT				P&ID: 202998C-001-PID-0021-0329				
				UNIT#:	EWPA AREA:	SPEC:	STRESS CALC #:	
				6800	6820	EPCL-SS01	NC	
				LINE No.				
				2"-R2-67141-EPCL-SS01-H				
OxyChem Redstone Battleground PROJECT				DRAWING NUMBER 6820-R2-67141-03			REV. 0	

