


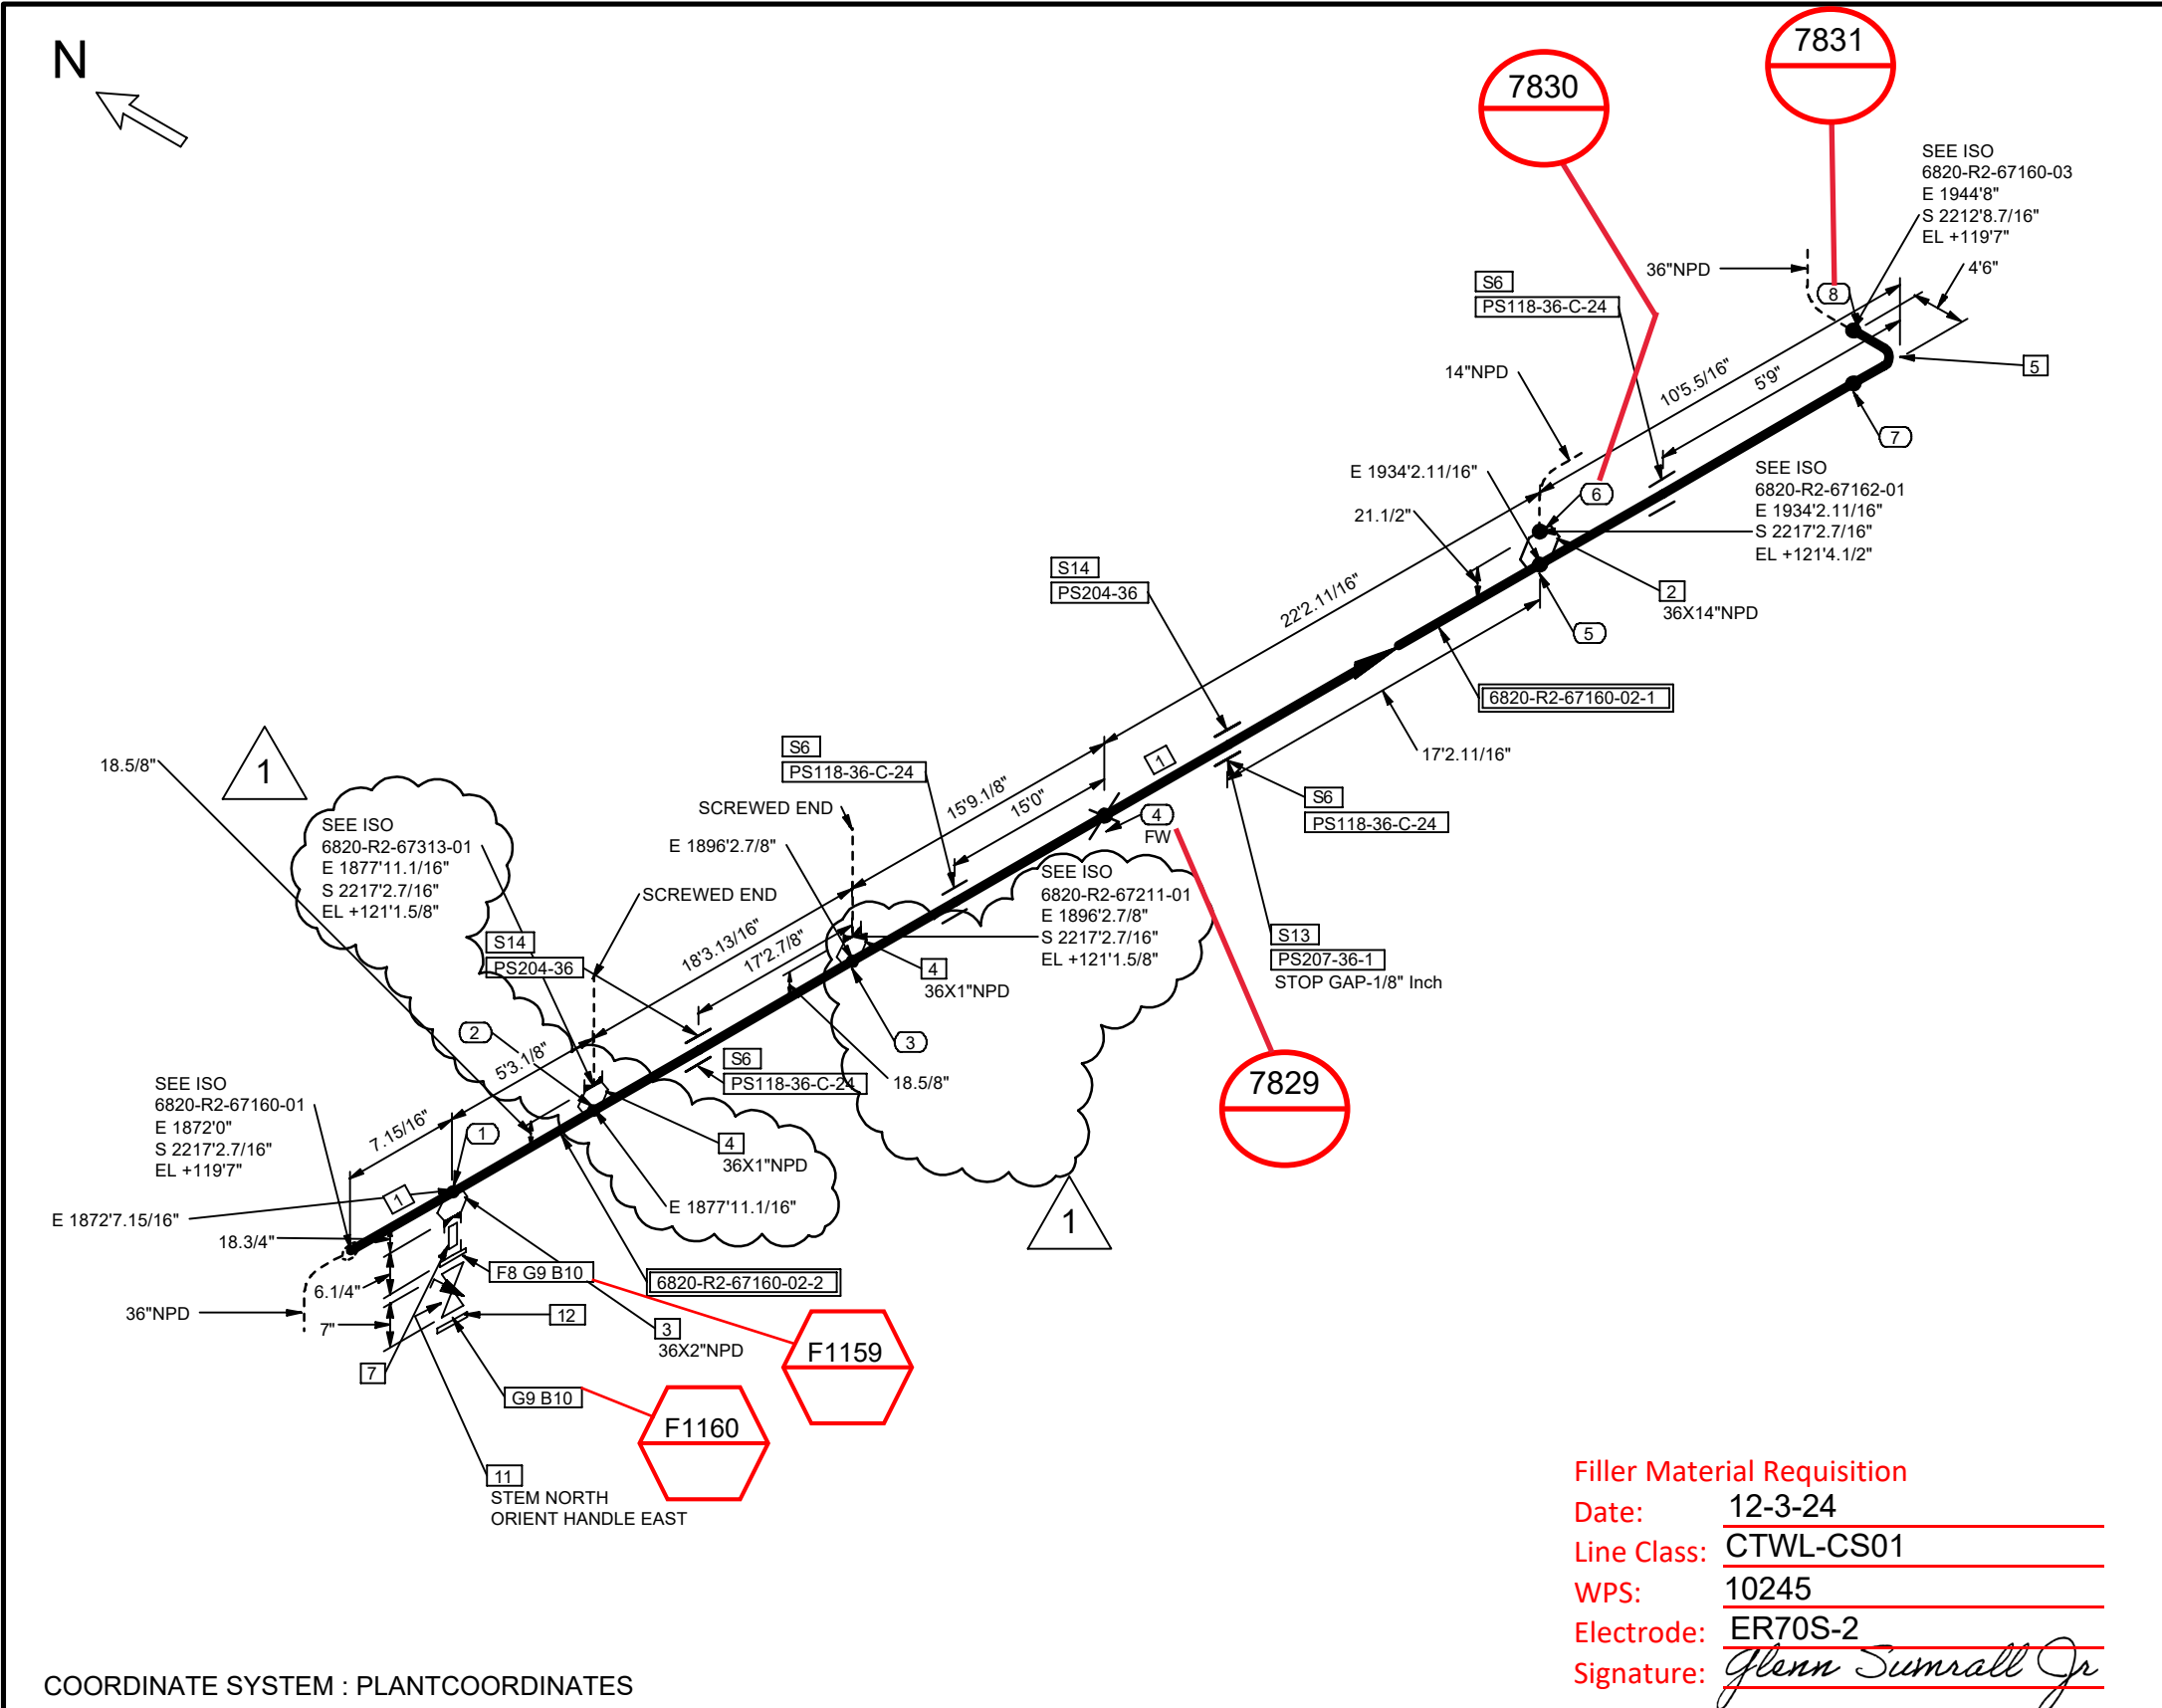

Filler Material Requisition  
Date: 12-3-24  
Line Class: CTWL-CS01  
WPS: 10245  
Electrode: ER70S-2  
Signature: *Glenn Sumrall Jr*

| SHOP MATERIALS   |               |   |            |       |                                    |             |           |
|---|---------------|---|------------|-------|------------------------------------|-------------|-----------|
| NO   | NPD           | DESCRIPTION   | IDENT      | QTY   |                                    |             |           |
| 1   | 36            | Pipes, DSAW, ASME B36.10, API 5L Gr.B PSL1, BE, -, -, .375"                                                                                             | C7SN25MV   | 68.2  |                                    |             |           |
| 2   | 36X14         | Weldolet, MSS SP-97, ASTM A105N, BW Ends, -, .375" x S-STD                                                                                              | C56W17FS   | 1     |                                    |             |           |
| 3   | 36X2          | Thredolet, ASTM A105N Galv. as per ASTM A153, 3000 Lbs, NPTF Ends, -, -,                                                                                | C5N67YV5   | 1     |                                    |             |           |
| 4   | 36X1          | Thredolet, ASTM A105N Galv. as per ASTM A153, 3000 Lbs, NPTF Ends, -, -,                                                                                | C5MYLG8B   | 2     |                                    |             |           |
| 5   | 36            | 90° Elb LR, Welded + 100% RT, ASME B16.9, ASTM A234 Gr.WPB, BW Ends, -, -, .375"                                                                        | CE79U10    | 1     |                                    |             |           |
| PIPE SUPPORTS   |               |   |            |       |                                    |             |           |
| 6   | 36            | PS118-36-C-24   | PS118      | 4     |                                    |             |           |
| OTHER THAN SHOP MATERIALS   |               |   |            |       |                                    |             |           |
| NO   | NPD           | DESCRIPTION   | IDENT      | QTY   |                                    |             |           |
| 7   | 2             | Nipple, ASTM A106 Gr.B Galv. as per ASTM A153, NPTM Ends, L = 6in, -, S-XS                                                                              | C76KHZKZ   | 1     |                                    |             |           |
| 8   | 2             | THD Flg, ASME B16.5, ASTM A105N Galv. as per ASTM A153, 150 Lbs, RF/NPTF End, -,                                                                        | C1DR2JR    | 1     |                                    |             |           |
| 9   | 2             | NM Flat Gk, Aramid Fiber Reinforced SBR, 150 Lbs, RF as per ASME B16.5, Full Face, Thk=1/8in, -,                                                        | C76KHSS3   | 2     |                                    |             |           |
| 10   | 5/8           | SBlT 2 HHx N, A193 Gr.B7/A194 Gr.2H, -, Xylan PTFE Coated, - 3.5 in. Length                                                                             | C6S4K88R   | 8     |                                    |             |           |
| 11   | 2             | Plug Flg,SP, Inverted Tapered Plug, Non Lubricated, API 599, ASTM A395 Gr.60-40-18, 150 Lbs, RF, Ends as per ASME B16.5, -, LO,-, -, Valve Tag: PL-0546 | C76RJXHX   | 1     |                                    |             |           |
| 12   | 2             | Bld Flg, ASME B16.5, ASTM A105N Galv. as per ASTM A153, 150 Lbs, RF, -,                                                                                 | C1DR2JY    | 1     |                                    |             |           |
| PIPE SUPPORTS   |               |   |            |       |                                    |             |           |
| 13   | 36            | PS207-36-1   | PS207      | 1     |                                    |             |           |
| 14   | 36            | PS204-36   | PS204      | 2     |                                    |             |           |
| PIECE MARKS   |               |   |            |       |                                    |             |           |
| 6820-R2-67160-02-1 6820-R2-67160-02-2   |               |   |            |       |                                    |             |           |
| <div>Turner Industries Group, LLC<br/>Received<br/>DECEMBER 03,2024<br/>DOCUMENT CONTROL</div>   |               |   |            |       |                                    |             |           |
| SERVICE:   | VAPOR/LIQUID: | INSUL TYPE:   | INSUL THK: | SHOP: | FIELD:                             | PAINT CODE: | MODULE:   |
| R2   | L             | Per LDT   | Per LDT    | Y     | Y                                  | Per LDT     | -         |
| <div><div>P&amp;ID:<br/>202998C-001-PID-0021-0333</div><div>UNIT#: 6800 EWP AREA: 6820 SPEC: CTWL-CS01 STRESS CALC #: CN-0407</div><div>LINE No:<br/>36"-R2-67160-CTWL-CS01-N</div></div> |               |   |            |       | DRAWING NUMBER<br>6820-R2-67160-02 |             | REV.<br>1 |
| OxyChem Redstone Battleground PROJECT   |               |   |            |       |                                    |             |           |

NOTES:

1. FOR LINE PRESSURES, TEMPERATURES, INSULATION TYPE AND THICKNESS, ETC. REFER TO LATEST REVISION OF LDT.

2. FOR STANDARD PIPE SUPPORT DETAILS SEE PROJECT STANDARD.

3. FIELD SHIM TO SUIT UNLESS OTHERWISE NOTED.

4. FOR PWHT REQUIREMENTS REFER TO LINE CLASS SPECIFICATION.

5. ALL THREADED PIPE LINE SYSTEMS, FIELD SHALL VERIFY DIMENSION PRIOR TO ERECTION.

6. FFW DESIGNATION AT WELDS INDICATES FIELD FIT WELD, WHERE PIPE FABRICATOR IS TO ADD 9 INCH OF PIPE TO THE ISOMETRIC DIMENSION TO ENABLE THE FIELD TO CUT TO FIT AT SITE.

7. REFER TO 202998C-000-W1-1300-0001 FOR FRP AND DUAL-LAM FABRICATION.

T.EN

TECHNIP  
ENERGIES

Information contained in this document is the work product of one or more legal entities of Technip Energies N.V. and embodies confidential and proprietary information of the applicable entity and/or its client. Use of this information is restricted in accordance with conditions specified by the contract. Technip Energies N.V. and its affiliates disclaim any and all liabilities for any changes or modifications to this document which are made by any person other than the entity that issued the document under the applicable client contract.

THIS DOCUMENT IS UNCONTROLLED WHEN REPRODUCED

|     |            |     |                         |      |     |        |       |
|-----|------------|-----|-------------------------|------|-----|--------|-------|
|     |            |     |                         |      |     |        |       |
|     |            |     |                         |      |     |        |       |
|     |            |     |                         |      |     |        |       |
|     |            |     |                         |      |     |        |       |
| 1   | 2024-11-19 | RVA | ISSUED FOR CONSTRUCTION | SAD  | KJK | SMR    | GR    |
| 0   | 2024-07-26 | RVA | ISSUED FOR CONSTRUCTION | SAD  | KJK | BRD    | GR    |
| REV | DATE       | BY  | DESCRIPTION             | CHKD | MTO | STRESS | APRVD |

