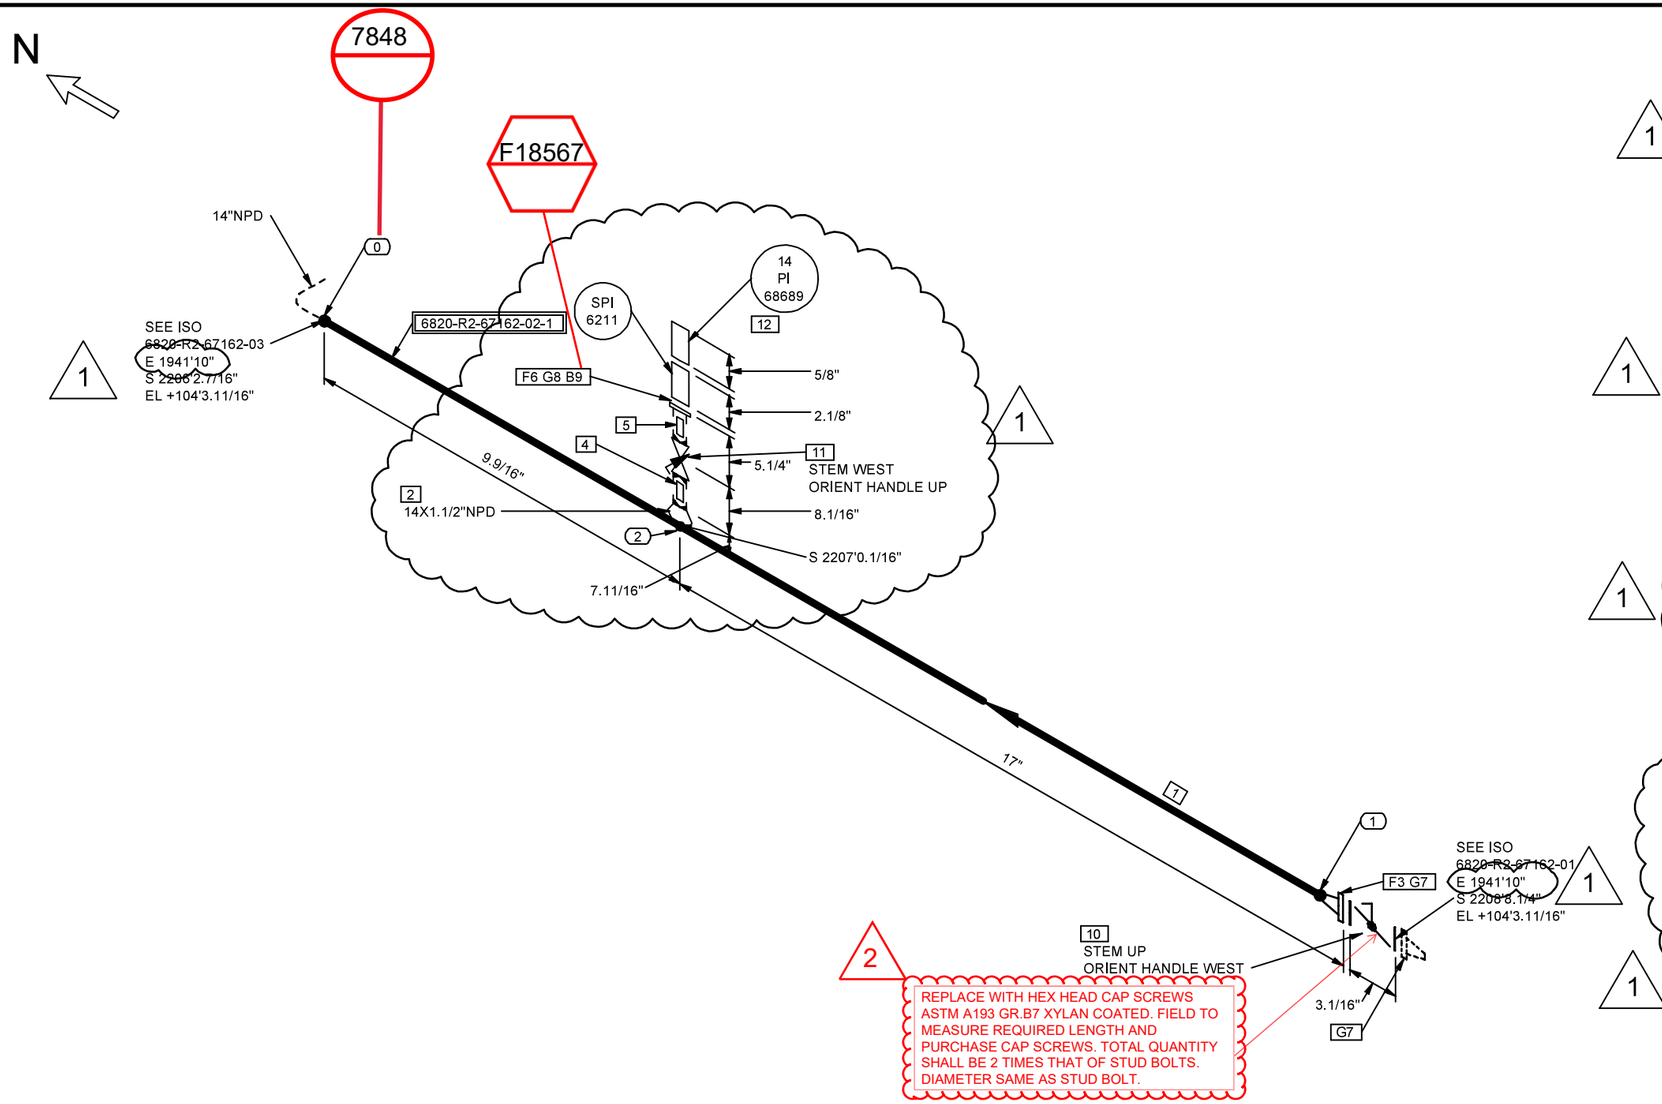

SHOP MATERIALS

NO	NPD	DESCRIPTION	IDENT	QTY
1	14	Pipes, Seamless, ASME B36.10, ASTM A106 Gr.B, BE, -, -, S-STD	CPP0AMRT	1.8 '
2	14X1.1/2	Threadolet, ASTM A105N Galv. as per ASTM A153, 3000 Lbs, NPTF Ends, -, -	C1Y177MR	1
3	14	WN Flg, ASME B16.5, ASTM A105N, 150 Lbs, RF/BW End, -, S-STD	CFG6WJ59	1

OTHER THAN SHOP MATERIALS

NO	NPD	DESCRIPTION	IDENT	QTY
4	1.1/2	Nipple, ASTM A106 Gr.B Galv. as per ASTM A153, NPTM Ends, L = 6in, -, S-XS	C41B2D92	1
5	1.1/2	Nipple, ASTM A106 Gr.B Galv. as per ASTM A153, NPTM Ends, L = 3in, -, S-XS	C41B2D95	1
6	1.1/2	THD Flg, ASME B16.5, ASTM A105N Galv. as per ASTM A153, 150 Lbs, RF/NPTF End, -,	C1DR2JP	1
7	14	NM Flat Gk, Aramid Fiber Reinforced SBR, 150 Lbs, RF as per ASME B16.5, Full Face, Thk=1/8in, -	C76KJLFJ	2
8	1.1/2	NM Flat Gk, Aramid Fiber Reinforced SBR, 150 Lbs, RF as per ASME B16.5, Full Face, Thk=1/8in, -	C76KHSS1	1
9	1/2	SBlt 2 HHx N, A193 Gr.B7/A194 Gr.2H, -, Xylan PTFE Coated, - 3 in. Length	C6S4K87V	4
10	14	But Waf, API 609 Cat.A, ASTM A395 Gr.60-40-18 EPDM Lined,150 Lbs, Lug-type RF, Ends as per ASME B16.5, GO,232 psig, Valve Tag: BU-0543	C76KJLEF	1
11	1.1/2	Plug Fem,RgP, Tapered Plug, Non Lubricated, API 599, ASTM A395 Gr.60-40-18, 300 Lbs, NPTF Ends, Ends as per ASME B16.11,-, LO, -, Valve Tag: PL-0545	C76N9VBH	1

INSTRUMENTS

12	1.1/2	14-PI-68689	14-PI-68689	1

PIECE MARKS

6820-R2-67162-02-1

Filler Material Requisition

Date: 3-27-25
Line Class: CTWL-CS01
WPS: 10245
Electrode: ER70S-2
Signature: Pedro Morin

Turner Industries Group, LLC
Received
MARCH 27, 2025
DOCUMENT CONTROL

COORDINATE SYSTEM : PLANTCOORDINATES

NOTES:
1. FOR LINE PRESSURES, TEMPERATURES, INSULATION TYPE AND THICKNESS, ETC. REFER TO LATEST REVISION OF LDT.
2. FOR STANDARD PIPE SUPPORT DETAILS SEE PROJECT STANDARD.
3. FIELD SHIM TO SUIT UNLESS OTHERWISE NOTED.
4. FOR PWHT REQUIREMENTS REFER TO LINE CLASS SPECIFICATION.
5. ALL THREADED PIPE LINE SYSTEMS, FIELD SHALL VERIFY DIMENSION PRIOR TO ERECTION.
6. FFW DESIGNATION AT WELDS INDICATES FIELD FIT WELD, WHERE PIPE FABRICATOR IS TO ADD 9 INCH OF PIPE TO THE ISOMETRIC DIMENSION TO ENABLE THE FIELD TO CUT TO FIT AT SITE.
7. REFER TO 202998C-000-W1-1300-0001 FOR FRP AND DUAL-LAM FABRICATION.

T.EN TECHNIP ENERGIES

Information contained in this document is the work product of one or more legal entities of Technip Energies N.V. and embodies confidential and proprietary information of the applicable entity and/or its client.use of this information is restricted in accordance with conditions specified by the contract.Technip Energies N.V. and its affiliates disclaim any and all liabilities for any changes or modifications to this document which are made by any person other than the entity that issued the document under the applicable client contract.

THIS DOCUMENT IS UNCONTROLLED WHEN REPRODUCED

REV	DATE	BY	DESCRIPTION	CHKD	MTO	STRESS	APRVD
2	2025-03-21	RVA	ISSUED FOR CONSTRUCTION	SAD	KJK	SMR	GR
1	2024-11-19	RVA	ISSUED FOR CONSTRUCTION	SAD	KJK	SMR	GR
0	2024-07-18	RVA	ISSUED FOR CONSTRUCTION	SAD	KJK	BRD	GR

SERVICE:	VAPOR/LIQUID:	INSUL TYPE:	INSUL THK:	SHOP:	FIELD:	PAINT CODE:	MODULE:
R2	L	Per LDT	Per LDT	Y	Y	Per LDT	-

OXY
OxyChem Redstone Battleground PROJECT

P&ID: 202998C-001-PID-0021-0333

UNIT#:	EWP AREA:	SPEC:	STRESS CALC #:
6800	6820	CTWL-CS01	CN-0403

LINE No. 14"-R2-67162-CTWL-CS01-N

DRAWING NUMBER: 6820-R2-67162-02 REV. 2

18 NOV 2024 23:29