
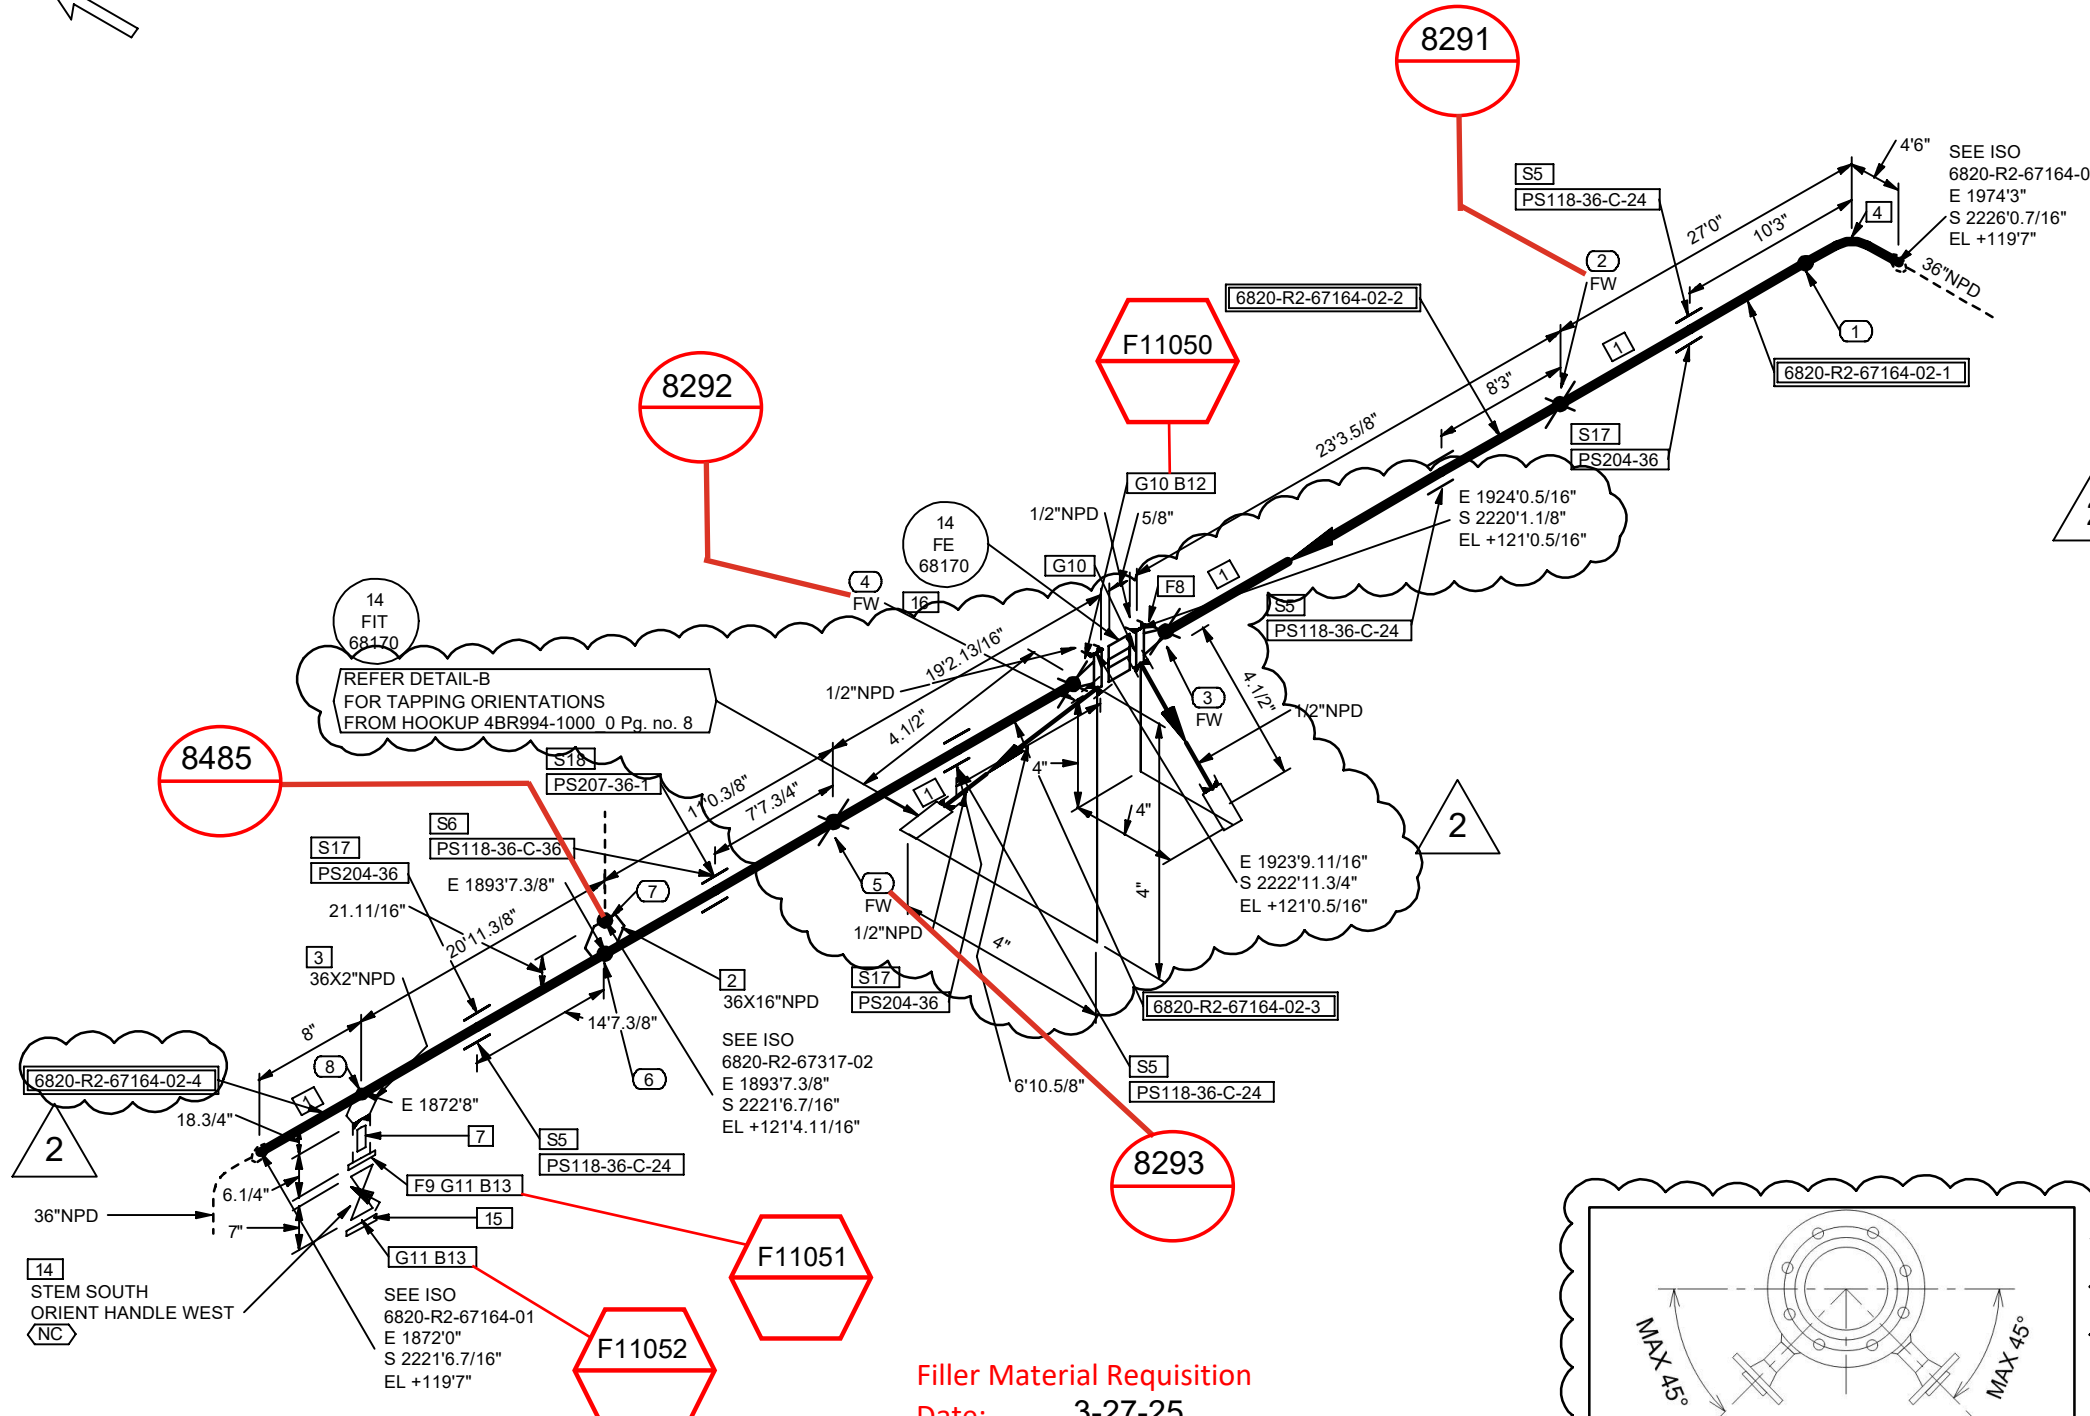


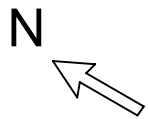

Filler Material Requisition
Date: 3-27-25
Line Class: CTWL-CS01
WPS: 10245
Electrode: ER70S-2
Signature: *Pedro Morin*

SHOP MATERIALS

NO	NPD	DESCRIPTION	IDENT	QTY
1	36	Pipes, DSAW, ASME B36.10, API 5L Gr.B PSL1, BE, -, -, .375"	C7SN25MV	96.1
2	36X16	Weldolet, MSS SP-97, ASTM A105N, BW Ends, -, .375" x S-STD	C7SN69PM	1
3	36X2	Thredolet, ASTM A105N Galv. as per ASTM A153, 3000 Lbs, NPTF Ends, -, -	C5N67YV5	1
4	36	90° Elb LR, Welded + 100% RT, ASME B16.9, ASTM A234 Gr.WPB, BW Ends, -, -, .375"	CE79U10	1

PIPE SUPPORTS

5	36	PS118-36-C-24	PS118	4
6	36	PS118-36-C-36	PS118	1

OTHER THAN SHOP MATERIALS

NO	NPD	DESCRIPTION	IDENT	QTY
7	2	Nipple, ASTM A106 Gr.B Galv. as per ASTM A153, NPTM Ends, L = 6in, -, 8-XS	C76KHZKZ	1
8	36	SP-6854	SP-6854	1
9	2	THD Flg, ASME B16.5, ASTM A105N Galv. as per ASTM A153, 150 Lbs, RF/NPTF End, -, 13.5 in. Length	C1DR2JR	1
10	36	NM Flat Gk, Aramid Fiber Reinforced SBR, 300 Lbs, RF as per ASME B16.47 Series A, Full Face, Thk=1/8in, -	C9YZMJSH	2
11	2	NM Flat Gk, Aramid Fiber Reinforced SBR, 150 Lbs, RF as per ASME B16.5, Full Face, Thk=1/8in, -	C76KHSS3	2
12	2	SBlT 2 HHx N, A193 Gr.B7/A194 Gr.2H, -, Xylan PTFE Coated, -	C6SDEV8M	32
13	5/8	SBlT 2 HHx N, A193 Gr.B7/A194 Gr.2H, -, Xylan PTFE Coated, - 3.5 in. Length	C6S4K88R	8
14	2	Plug Flg, SP, Inverted Tapered Plug, Non Lubricated, API 599, ASTM A395 Gr.60-40-18, 150 Lbs, RF, Ends as per ASME B16.5, -, LO, -, -, Valve Tag: PL-0546	C76RJXHX	1
15	2	Bld Flg, ASME B16.5, ASTM A105N Galv. as per ASTM A153, 150 Lbs, RF, -	C1DR2JY	1

INSTRUMENTS

16	36	14-FE-68170	14-FE-68170	1
----	----	-------------	-------------	---

PIPE SUPPORTS

17	36	PS204-36	PS204	3
18	36	PS207-36-1	PS207	1

PIECE MARKS

6820-R2-67164-02-1 6820-R2-67164-02-2 6820-R2-67164-02-3
6820-R2-67164-02-4

COORDINATE SYSTEM : PLANTCOORDINATES

NOTES:

- FOR LINE PRESSURES, TEMPERATURES, INSULATION TYPE AND THICKNESS, ETC. REFER TO LATEST REVISION OF LDT.
- FOR STANDARD PIPE SUPPORT DETAILS SEE PROJECT STANDARD.
- FIELD SHIM TO SUIT UNLESS OTHERWISE NOTED.
- FOR PWHT REQUIREMENTS REFER TO LINE CLASS SPECIFICATION.
- ALL THREADED PIPE LINE SYSTEMS, FIELD SHALL VERIFY DIMENSION PRIOR TO ERECTION.
- FFW DESIGNATION AT WELDS INDICATES FIELD FIT WELD, WHERE PIPE FABRICATOR IS TO ADD 9 INCH OF PIPE TO THE ISOMETRIC DIMENSION TO ENABLE THE FIELD TO CUT TO FIT AT SITE.
- REFER TO 202998C-000-W1-1300-0001 FOR FRP AND DUAL-LAM FABRICATION.



Information contained in this document is the work product of one or more legal entities of Technip Energies N.V. and embodies confidential and proprietary information of the applicable entity and/or its client. Use of this information is restricted in accordance with conditions specified by the contract. Technip Energies N.V. and its affiliates disclaim any and all liabilities for any changes or modifications to this document which are made by any person other than the entity that issued the document under the applicable client contract.

THIS DOCUMENT IS UNCONTROLLED WHEN REPRODUCED

REV	DATE	BY	DESCRIPTION	CHKD	MTD	STRESS	APRVD
2	2025-03-21	RVA	ISSUED FOR CONSTRUCTION	SAD	KJK	SMR	GR
1	2025-03-07	RVA	ISSUED FOR CONSTRUCTION	SAD	KJK	SMR	GR
0	2024-11-22	RVA	ISSUED FOR CONSTRUCTION	SAD	KJK	SMR	GR

SERVICE:	R2	VAPOR/LIQUID:	L	INSUL TYPE:	Per LDT	INSUL THK:	Per LDT	SHOP:	Y	FIELD:	Y	PAINT CODE:	Per LDT	MODULE:	-
								P&ID:							
								202998C-001-PID-0021-0327							
								UNIT#:	EWP AREA:		SPEC:		STRESS CALC #:		
								6800	6820		CTWL-CS01		CN-0408		
								LINE No.							
OxyChem Redstone Battleground PROJECT								36"-R2-67164-CTWL-CS01-N							
								DRAWING NUMBER							
								6820-R2-67164-02							



OxyChem Redstone Battleground PROJECT

