


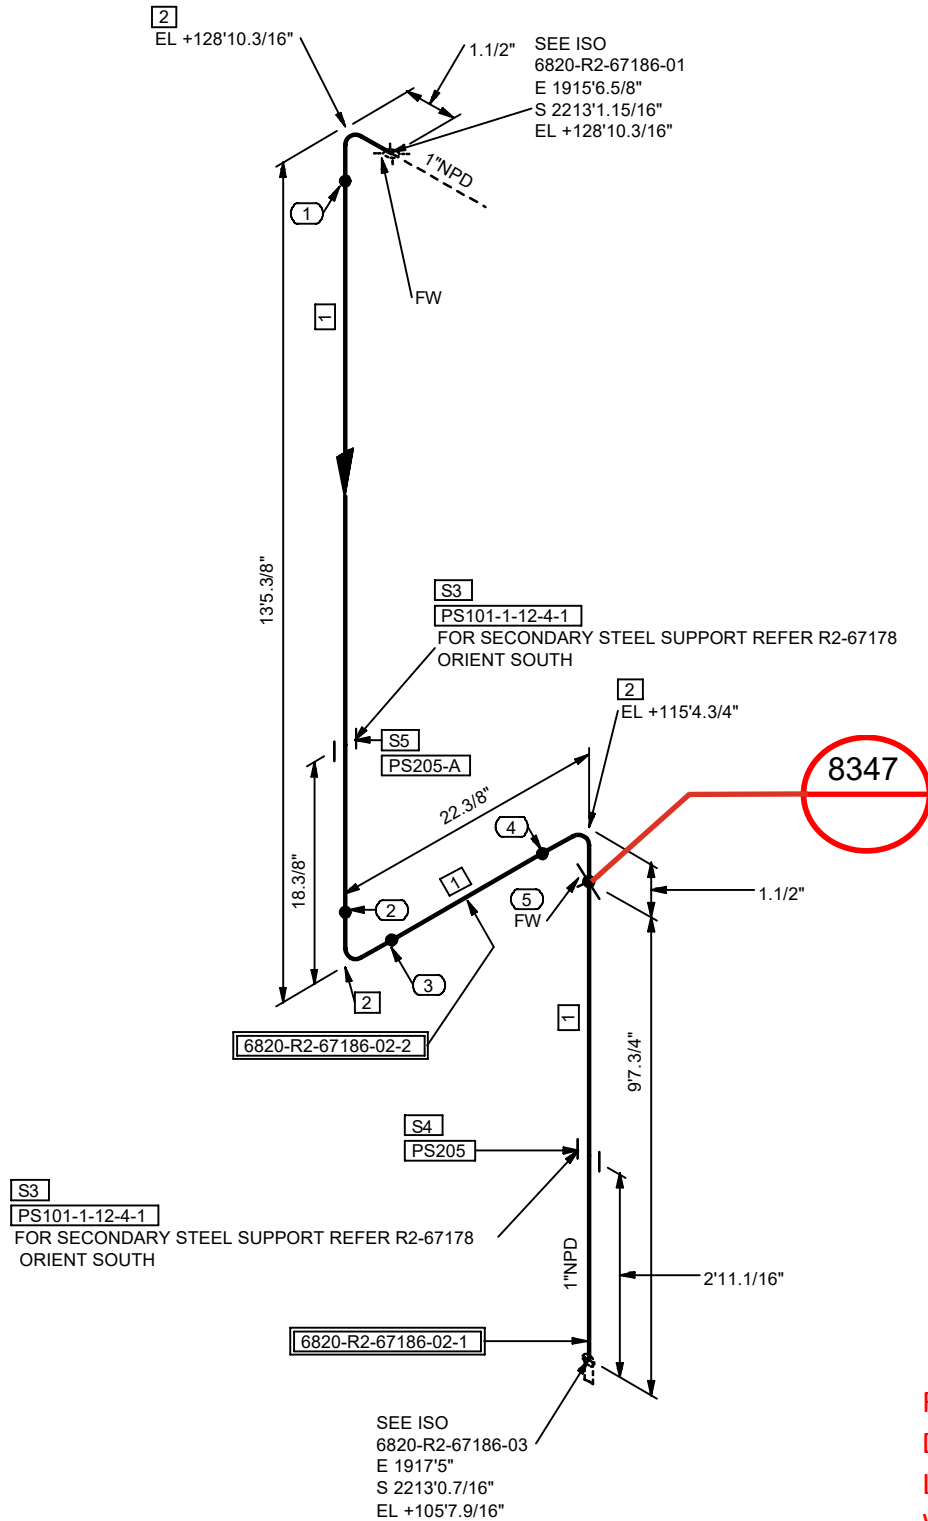

Filler Material Requisition
Date: 1-3-25
Line Class: SLPG-CS01
WPS: 10245
Electrode: ER70S-2
Signature: Pedro Morin

SHOP MATERIALS

NO	NPD	DESCRIPTION	IDENT	QTY
1	1	Pipes, Seamless, ASME B36.10, ASTM A106 Gr.B, BE, -, -, S-XS	C2UE2BC	24.5 '
2	1	90° Elb LR, Seamless, ASME B16.9, ASTM A234 Gr.WPB, BW Ends, -, -, S-XS	C2UE473	3

PIPE SUPPORTS

3	1	PS101-1-12-4-1	PS101	2
---	---	----------------	-------	---

OTHER THAN SHOP MATERIALS


NO	NPD	DESCRIPTION	IDENT	QTY
PIPE SUPPORTS				
4	1	PS205	PS205	1
5	1	PS205-A	PS205	1

PIECE MARKS

6820-R2-67186-02-1 6820-R2-67186-02-2

COORDINATE SYSTEM : PLANTCOORDINATES

- NOTES:
- FOR LINE PRESSURES, TEMPERATURES, INSULATION TYPE AND THICKNESS, ETC. REFER TO LATEST REVISION OF LDT.
 - FOR STANDARD PIPE SUPPORT DETAILS SEE PROJECT STANDARD.
 - FIELD SHIM TO SUIT UNLESS OTHERWISE NOTED.
 - FOR PWHT REQUIREMENTS REFER TO LINE CLASS SPECIFICATION.
 - ALL THREADED PIPE LINE SYSTEMS, FIELD SHALL VERIFY DIMENSION PRIOR TO ERECTION.
 - FFW DESIGNATION AT WELDS INDICATES FIELD FIT WELD, WHERE PIPE FABRICATOR IS TO ADD 9 INCH OF PIPE TO THE ISOMETRIC DIMENSION TO ENABLE THE FIELD TO CUT TO FIT AT SITE.
 - REFER TO 202998C-000-W1-1300-0001 FOR FRP AND DUAL-LAM FABRICATION.

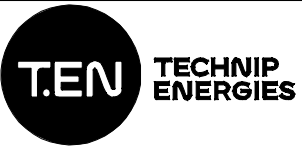

Information contained in this document is the work product of one or more legal entities of Technip Energies N.V. and embodies confidential and proprietary information of the applicable entity and/or its client. Use of this information is restricted in accordance with conditions specified by the contract. Technip Energies N.V. and its affiliates disclaim any and all liabilities for any changes or modifications to this document which are made by any person other than the entity that issued the document under the applicable client contract.

THIS DOCUMENT IS UNCONTROLLED WHEN REPRODUCED

0	2024-12-20	RVA	ISSUED FOR CONSTRUCTION	SAD	KJK	SMR	GR		
REV	DATE	BY	DESCRIPTION	CHKD	MTO	STRESS	APRVD		

SERVICE: R2

VAPOR/LIQUID: V

INSUL TYPE: Per LDT

INSUL THK: Per LDT

SHOP: Y

FIELD: Y

PAINT CODE: Per LDT

MODULE: -



OxyChem Redstone Battleground PROJECT

P&ID: 202998C-001-PID-0021-0335

UNIT#: 6800

EWPA AREA: 6820

SPEC: SLPG-CS01

STRESS CALC #: -

LINE No: 1"-R2-67186-SLPG-CS01-H

DRAWING NUMBER: 6820-R2-67186-02

REV: 0

