


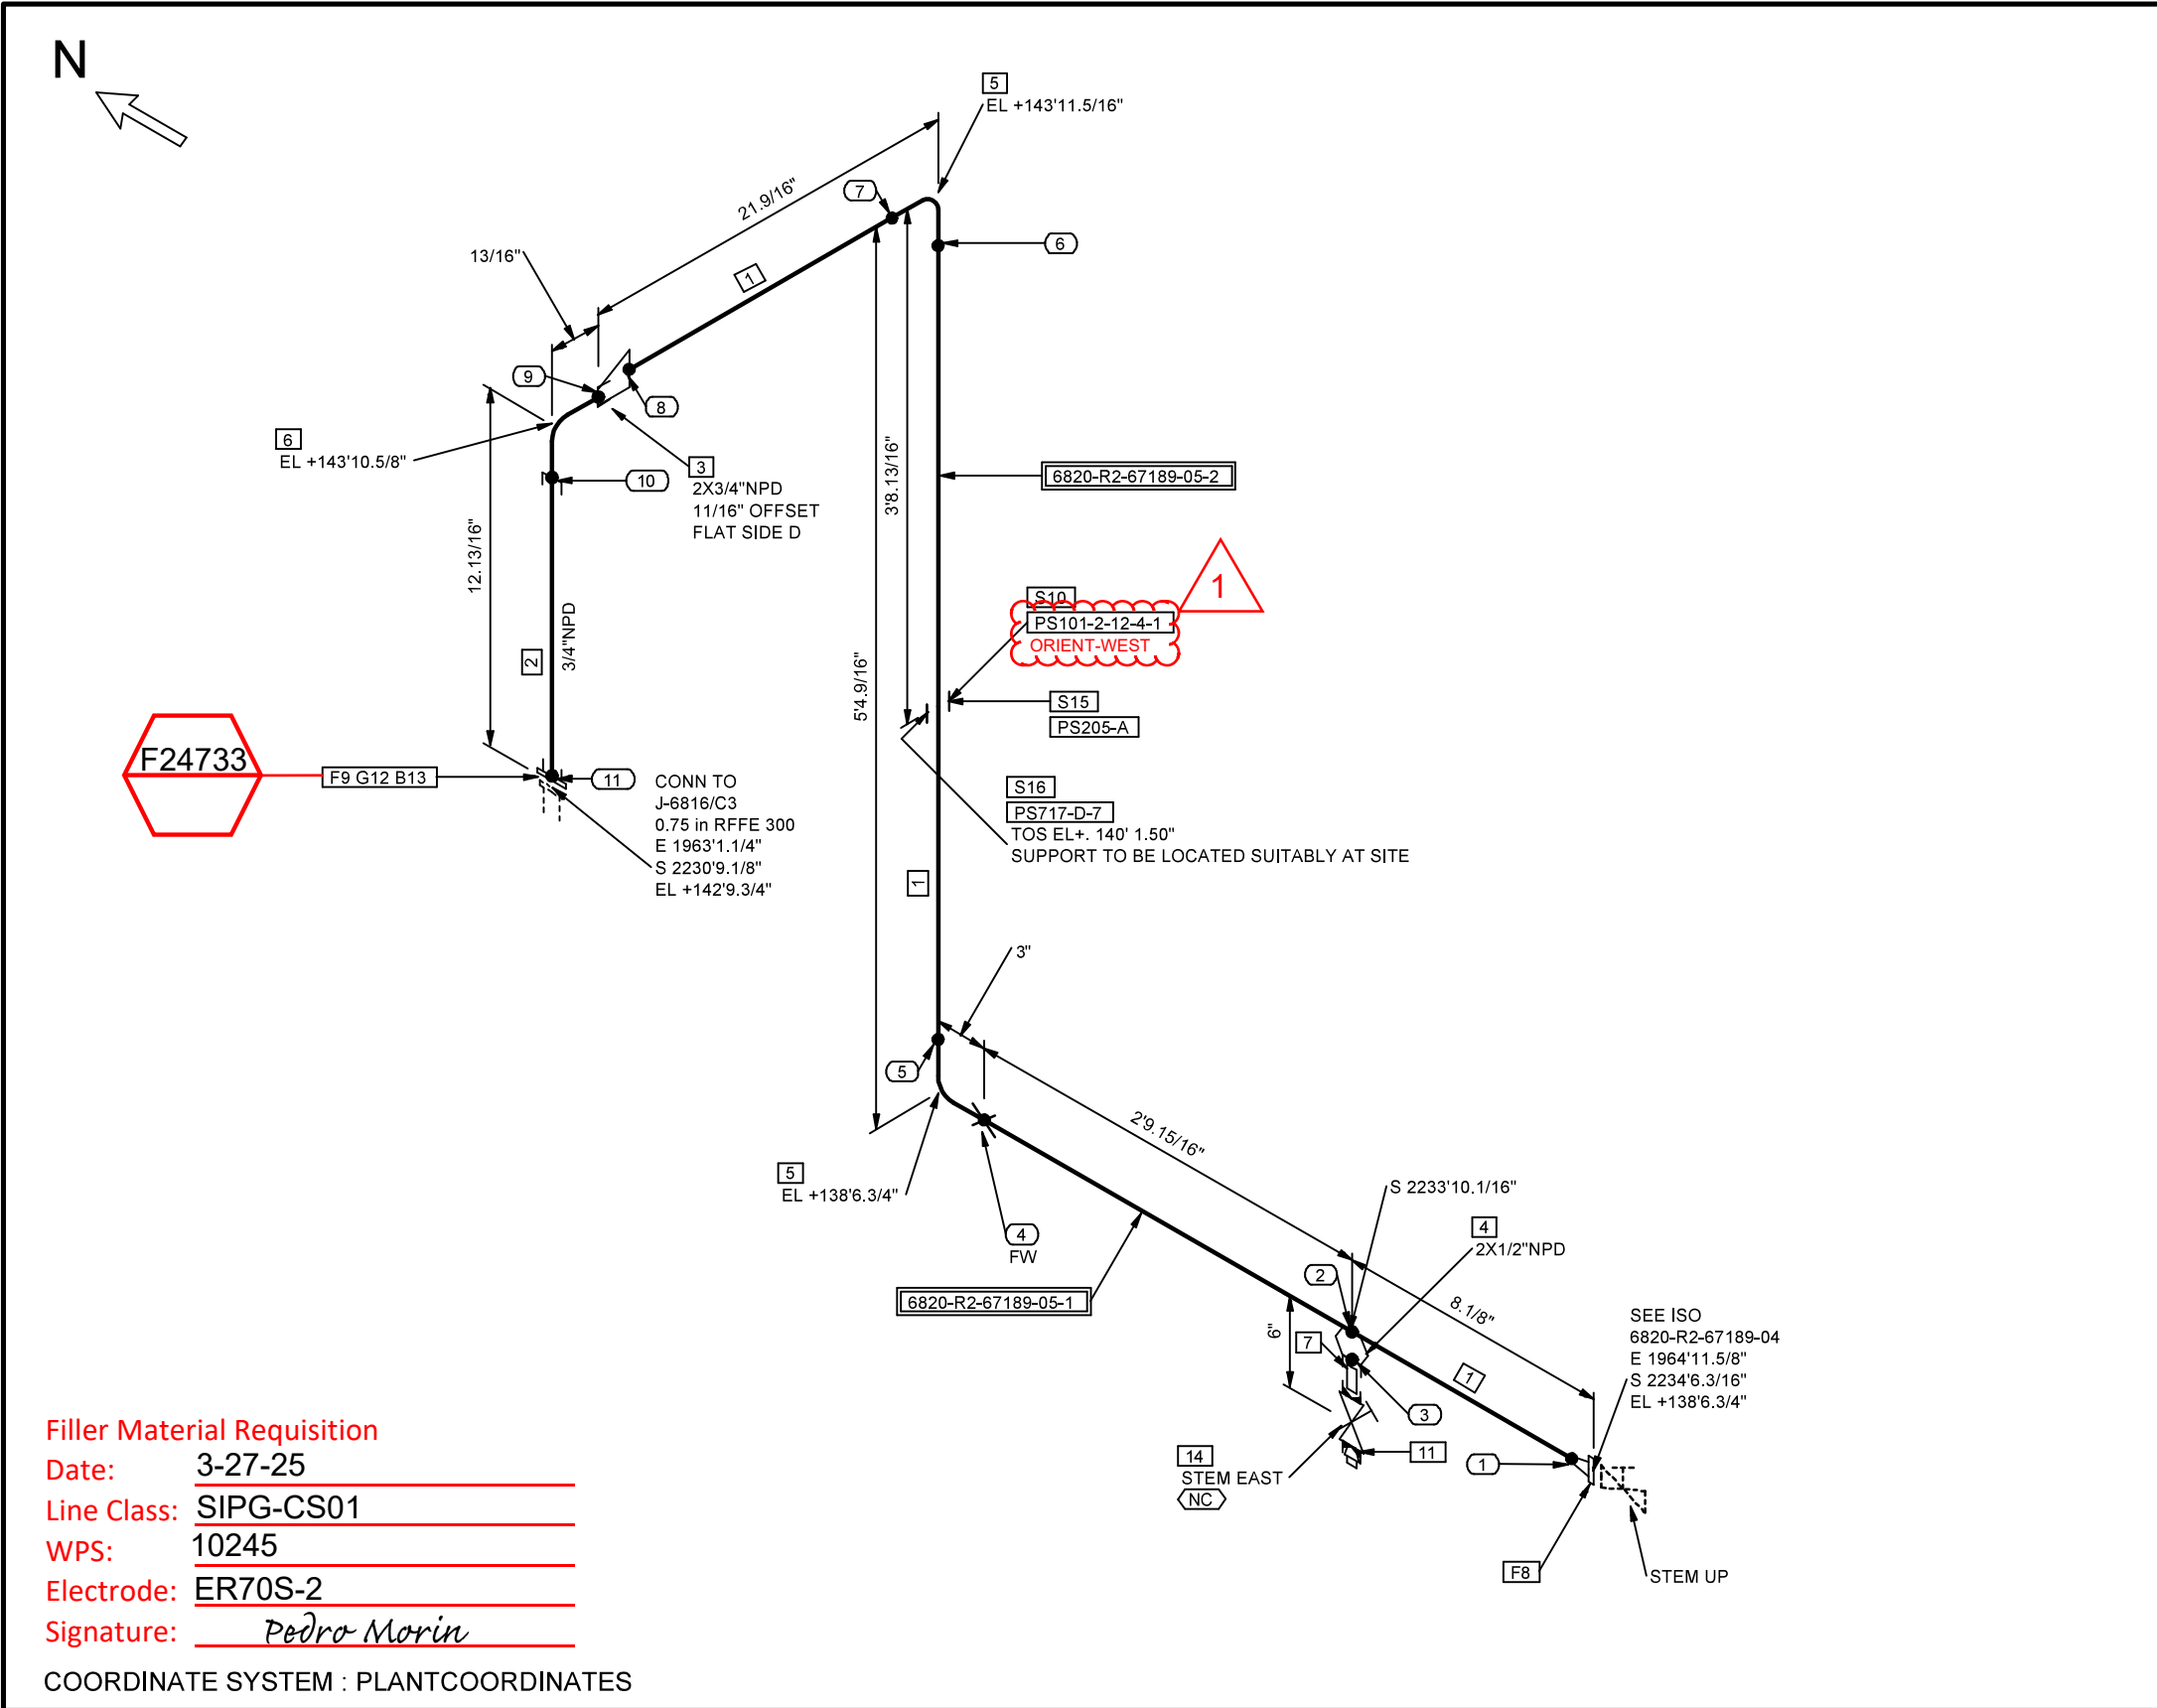

Filler Material Requisition
Date: 3-27-25
Line Class: SIPG-CS01
WPS: 10245
Electrode: ER70S-2
Signature: Pedro Morin

COORDINATE SYSTEM : PLANTCOORDINATES

- NOTES:**
1. FOR LINE PRESSURES, TEMPERATURES, INSULATION TYPE AND THICKNESS, ETC. REFER TO LATEST REVISION OF LDT.
 2. FOR STANDARD PIPE SUPPORT DETAILS SEE PROJECT STANDARD.
 3. FIELD SHIM TO SUIT UNLESS OTHERWISE NOTED.
 4. FOR PWHT REQUIREMENTS REFER TO LINE CLASS SPECIFICATION.
 5. ALL THREADED PIPE LINE SYSTEMS, FIELD SHALL VERIFY DIMENSION PRIOR TO ERECTION.
 6. FFW DESIGNATION AT WELDS INDICATES FIELD FIT WELD, WHERE PIPE FABRICATOR IS TO ADD 9 INCH OF PIPE TO THE ISOMETRIC DIMENSION TO ENABLE THE FIELD TO CUT TO FIT AT SITE.
 7. REFER TO 202998C-000-W1-1300-0001 FOR FRP AND DUAL-LAM FABRICATION.



**TECHNIP
ENERGIES**

Information contained in this document is the work product of one or more legal entities of Technip Energies N.V. and embodies confidential and proprietary information of the applicable entity and/or its client. Use of this information is restricted in accordance with conditions specified by the contract. Technip Energies N.V. and its affiliates disclaim any and all liabilities for any changes or modifications to this document which are made by any person other than the entity that issued the document under the applicable client contract.

THIS DOCUMENT IS UNCONTROLLED WHEN REPRODUCED

REV	DATE	BY	DESCRIPTION	CHKD	MTO	STRESS	APRVD
1	2025-03-21	RVA	ISSUED FOR CONSTRUCTION	SAD	KJK	SMR	GR
0	2024-12-13	RVA	ISSUED FOR CONSTRUCTION	SAD	KJK	SMR	GR

SHOP MATERIALS							
NO	NPD	DESCRIPTION	IDENT	QTY			
1	2	Pipes, Seamless, ASME B36.10, ASTM A106 Gr.B, BE, -, -, S-XS	CPP0AAUB	9.2 '			
2	3/4	Pipes, Seamless, ASME B36.10, ASTM A106 Gr.B, PE, -, -, S-XS	CPP0AMK2	1.0 '			
3	2X3/4	Eccentric swage, MSS SP-95, ASTM A234 Gr.WPB,BE/PE,-, -, S-XS	CRNZ6B	1			
4	2X1/2	Socketlet, ASTM A105N, 3000 Lbs, SW Ends, -, -,	C2JYR45	1			
5	2	90° Elb LR, Seamless, ASME B16.9, ASTM A234 Gr.WPB, BW Ends, -, -, S-XS	CDB66GD6	2			
6	3/4	90° Elb, ASME B16.11, ASTM A105N, 3000 Lbs, SW Ends, -,	CDF6ZSP5	1			
7	1/2	Nipple, ASTM A106 Gr.B, PE, L = 3in, -, S-XS	C246122	1			
8	2	WN Flg, ASME B16.5, ASTM A105N, 300 Lbs, RF/BW End, -, S-XS	CFG6WKK1	1			
9	3/4	SW Flg, ASME B16.5, ASTM A105N, 300 Lbs, RF/SW End, -, x S-XS	CFG70GLP	1			
PIPE SUPPORTS							
10	2	PS101-2-12-4-1	PS101	1			
OTHER THAN SHOP MATERIALS							
NO	NPD	DESCRIPTION	IDENT	QTY			
11	1/2	Plug, Solid Round Head Type, ASME B16.11, ASTM A105N, NPTM End, -,	CBBPLK2	1			
12	3/4	SW Gk, AISI 304/Graphite, 300 Lbs, RF as per ASME B16.5, Thk=1/8in, -, -,	CGKFEG5U	1			
13	5/8	SBlt 2 HHx N, A193 Gr.B7/A194 Gr.2H, -, Xylan PTFE Coated, - 3 in. Length	C6S4K88N	4			
14	1/2	Gat Fem, API 602, ASTM A105N,800 Lbs, NPTF Ends, HO,-, Valve Tag: VG-7	C80U8UAY	1			
PIPE SUPPORTS							
15	2	PS205-A	PS205	1			
16	2	PS717-D-7	PS717	1			
PIECE MARKS							
6820-R2-67189-05-1 6820-R2-67189-05-2							
Turner Industries Group, LLC Received MARCH 27, 2025 DOCUMENT CONTROL							
SERVICE:	VAPOR/LIQUID:	INSUL TYPE:	INSUL THK:	SHOP:	FIELD:	PAIN CODE:	MODULE:
R2	V	Per LDT	Per LDT	Y	Y	Per LDT	-
		P&ID: 202998C-001-PID-0021-0335					
UNIT#:		LEWP AREA:		SPEC:		STRESS CALC #:	
6800		6820		SIPG-CS01		-	
LINE No. 2"-R2-67189-SIPG-CS01-H							
OxyChem Redstone Battleground PROJECT						DRAWING NUMBER 6820-R2-67189-05	
						REV. 1	

