


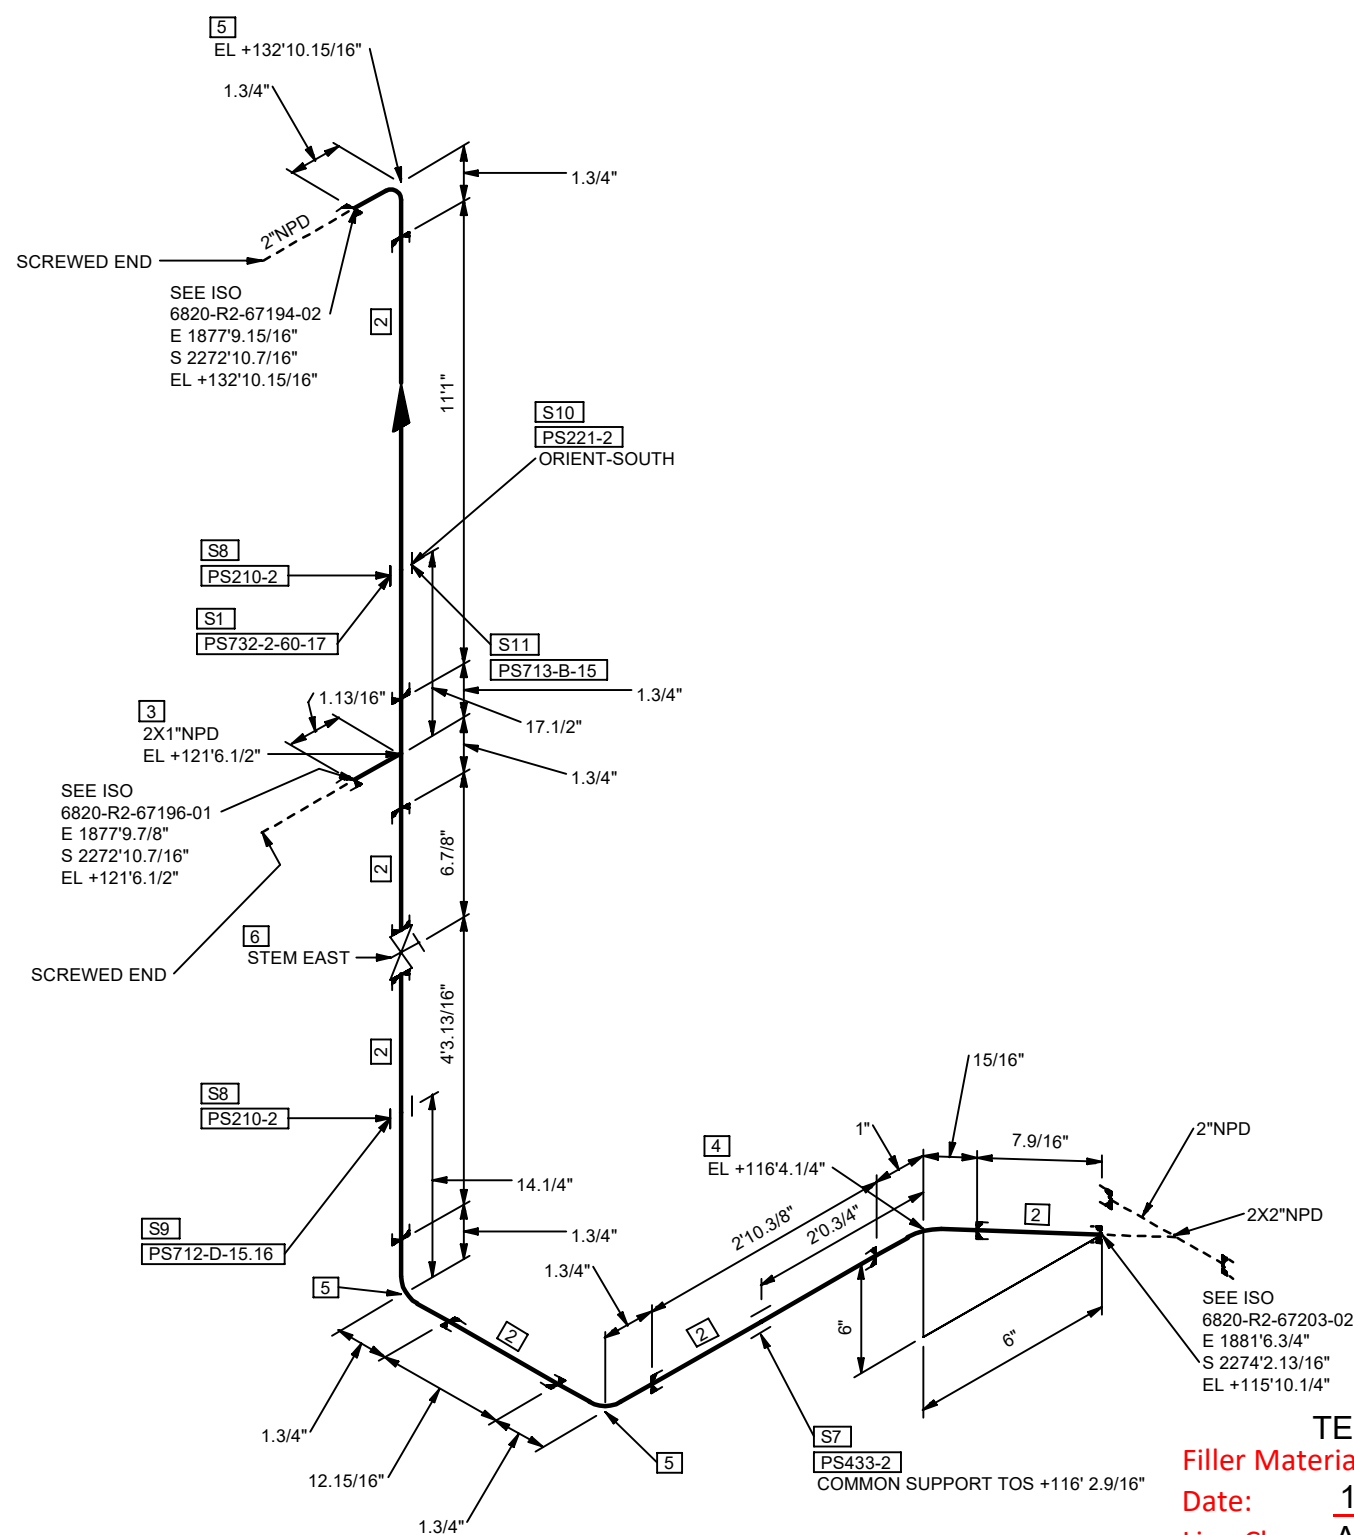


S7
PS433-2
COMMON SUPPORT TOS +116' 2.9/16"

TEFLON TAPE
Filler Material Requisition
Date: 1-16-25
Line Class: ARDG-XX01
WPS: N/A
Electrode: N/A
Signature: *Glenn Summalls*

SHOP MATERIALS				
NO	NPD	DESCRIPTION	IDENT	QTY
<u>PIPE SUPPORTS</u>				
1	2	PS732-2-60-17	PS732	1
<u>OTHER THAN SHOP MATERIALS</u>				
NO	NPD	DESCRIPTION	IDENT	QTY
2	2	Pipes, Seamless, ASME B36.10, ASTM A53 Gr.B Galv. as per ASTM A153, NPTM Ends, w/ coupling, -, S-XS	C8GWJY7T	20.5
3	2X1	Red Te, ASME B16.11, ASTM A105N Galv. as per ASTM A153, 3000 Lbs, NPTF Ends, -	C1DR2J7	1
4	2	45° Elb, ASME B16.11, ASTM A105N Galv. as per ASTM A153, 3000 Lbs, NPTF Ends, -	C1DMWEF	1
5	2	90° Elb, ASME B16.11, ASTM A105N Galv. as per ASTM A153, 3000 Lbs, NPTF Ends, -	C1DMWEN	3
6	2	Gat Fem, MSS SP-80, ASTM B62 UNS C83600, 125 Lbs, NPTF Ends, HO-, Valve Tag: GA-0110	C76KHVWW	1
<u>PIPE SUPPORTS</u>				
7	2	PS433-2	PS433	1
8	2	PS210-2	PS210	2
9	2	PS712-D-15.16	PS712	1
10	2	PS221-2	PS221	1
11	2	PS713-B-15	PS713	1

NOTES:

1. FOR LINE PRESSURES, TEMPERATURES, INSULATION TYPE AND THICKNESS, ETC. REFER TO LATEST REVISION OF LDT.
2. FOR STANDARD PIPE SUPPORT DETAILS SEE PROJECT STANDARD.
3. FIELD SHIM TO SUIT UNLESS OTHERWISE NOTED.
4. FOR PWHT REQUIREMENTS REFER TO LINE CLASS SPECIFICATION.
5. ALL THREADED PIPE LINE SYSTEMS, FIELD SHALL VERIFY DIMENSION PRIOR TO ERECTION.
6. FFW DESIGNATION AT WELDS INDICATES FIELD FIT WELD, WHERE PIPE FABRICATOR IS TO ADD 9 INCH OF PIPE TO THE ISOMETRIC DIMENSION TO ENABLE THE FIELD TO CUT TO FIT AT SITE.
7. REFER TO 202998C-000-W1-1300-0001 FOR FRP AND DUAL-LAM FABRICATION.

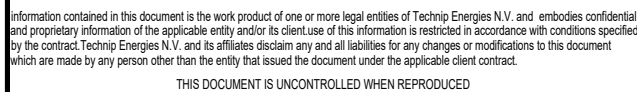

0	2025-01-10	RVA	ISSUED FOR CONSTRUCTION	SAD	KJK	SMR	GR
REV	DATE	BY	DESCRIPTION	CHKD	MTO	STRESS	APRVD

SERVICE: R2	VAPOR/LIQUID: V	INSUL TYPE: Per LDT	INSUL THK: Per LDT	SHOP: N	FIELD: Y	PAINT CODE: Per LDT	MODULE: -
 OxyChem Redstone Battleground PROJECT				P&ID: 202998C-001-PID-0021-0336			
				UNIT#: 6800	EWP AREA: 6820	SPEC: ARDG-XX01	STRESS CALC #: -
				LINE No. 2"-R2-67194-ARDG-XX01-N			
				DRAWING NUMBER 6820-R2-67194-01			
				REV. 0			

