


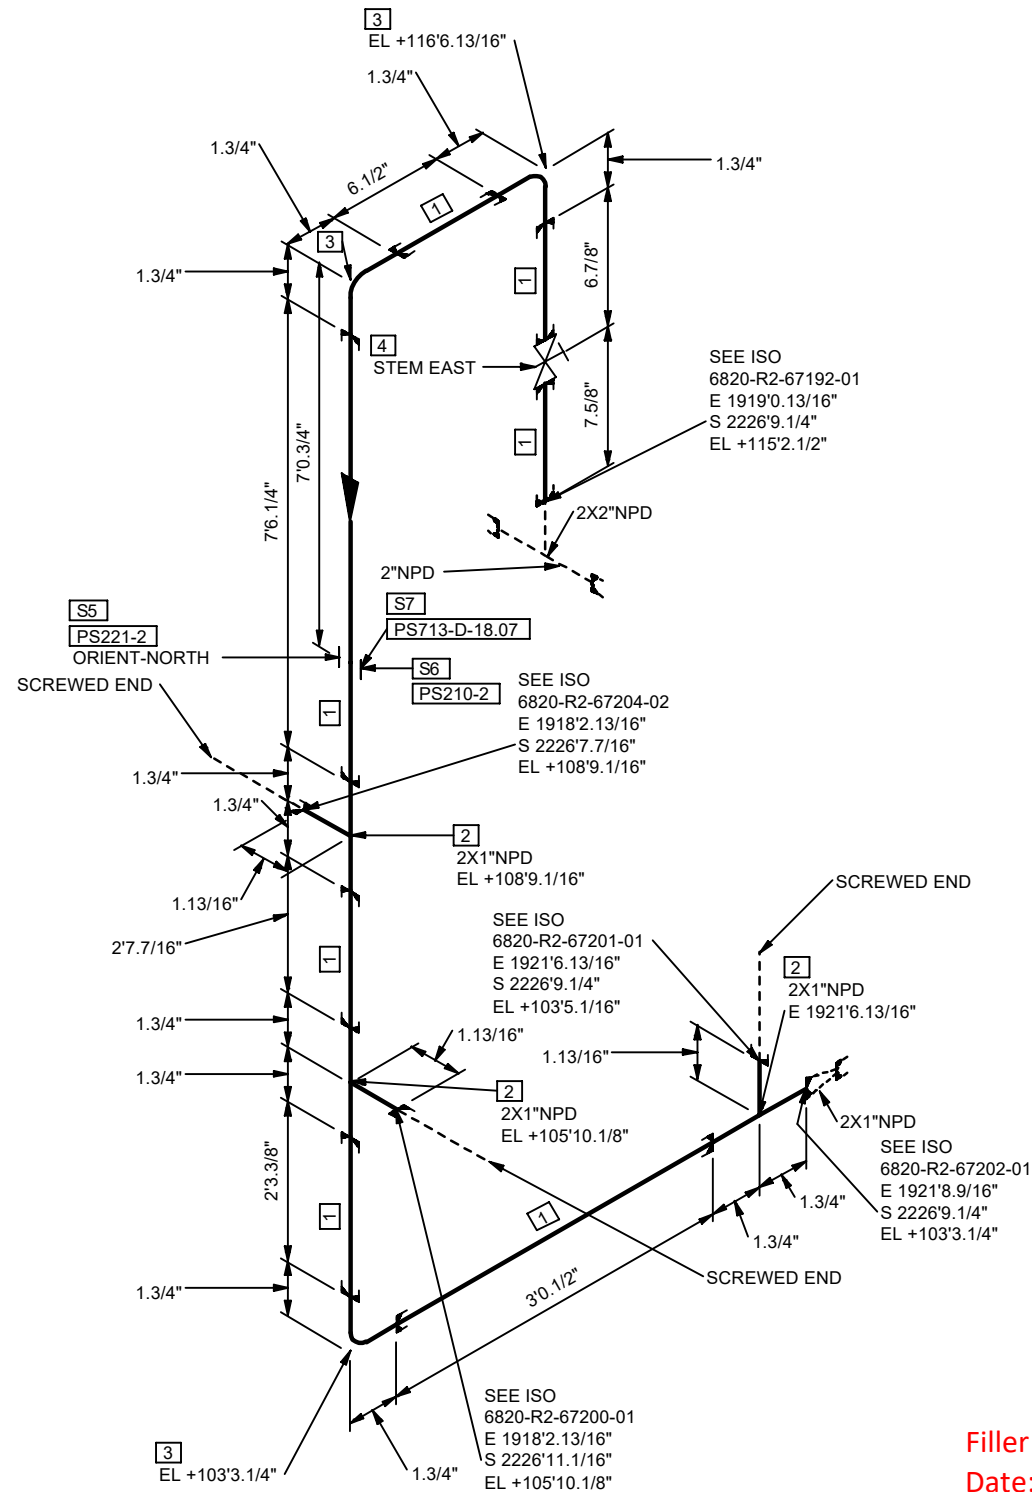

TEFLON TAPE  
Filler Material Requisition  
Date: 1-25-25  
Line Class: ARDG-XX01  
WPS: N/A  
Electrode: N/A  
Signature: *Glenn Sumrall Jr*

OTHER THAN SHOP MATERIALS

| NO            | NPD | DESCRIPTION                                                                                         | IDENT    | QTY  |
|---------------|-----|---|----------|------|
| 1             | 2   | Pipes, Seamless, ASME B36.10, ASTM A53 Gr.B Galv. as per ASTM A153, NPTM Ends, w/ coupling, -, S-XS | C8GWJY7T | 17.1 |
| 2             | 2X1 | Red Te, ASME B16.11, ASTM A105N Galv. as per ASTM A153, 3000 Lbs, NPTF Ends, -,                     | C1DR2J7  | 3    |
| 3             | 2   | 90° Elb, ASME B16.11, ASTM A105N Galv. as per ASTM A153, 3000 Lbs, NPTF Ends, -,                    | C1DMWEN  | 3    |
| 4             | 2   | Gat Fem, MSS SP-80, ASTM B62 UNS C83600, 125 Lbs, NPTF Ends, HO, -, Valve Tag: GA-0110              | C76KHVWW | 1    |
| PIPE SUPPORTS |     |   |          |      |
| 5             | 2   | PS221-2                                                                                             | PS221    | 1    |
| 6             | 2   | PS210-2                                                                                             | PS210    | 1    |
| 7             | 2   | PS713-D-18.07                                                                                       | PS713    | 1    |

COORDINATE SYSTEM : PLANTCOORDINATES

- NOTES:
- FOR LINE PRESSURES, TEMPERATURES, INSULATION TYPE AND THICKNESS, ETC. REFER TO LATEST REVISION OF LDT.
  - FOR STANDARD PIPE SUPPORT DETAILS SEE PROJECT STANDARD.
  - FIELD SHIM TO SUIT UNLESS OTHERWISE NOTED.
  - FOR PWHT REQUIREMENTS REFER TO LINE CLASS SPECIFICATION.
  - ALL THREADED PIPE LINE SYSTEMS, FIELD SHALL VERIFY DIMENSION PRIOR TO ERECTION.
  - FFW DESIGNATION AT WELDS INDICATES FIELD FIT WELD, WHERE PIPE FABRICATOR IS TO ADD 9 INCH OF PIPE TO THE ISOMETRIC DIMENSION TO ENABLE THE FIELD TO CUT TO FIT AT SITE.
  - REFER TO 202998C-000-W1-1300-0001 FOR FRP AND DUAL-LAM FABRICATION.



Information contained in this document is the work product of one or more legal entities of Technip Energies N.V. and embodies confidential and proprietary information of the applicable entity and/or its client. Use of this information is restricted in accordance with conditions specified by the contract. Technip Energies N.V. and its affiliates disclaim any and all liabilities for any changes or modifications to this document which are made by any person other than the entity that issued the document under the applicable client contract.

THIS DOCUMENT IS UNCONTROLLED WHEN REPRODUCED

| 0   | 2025-01-17 | RVA | ISSUED FOR CONSTRUCTION | SAD  | KJK | SMR    | GR    |
|-----|------------|-----|-------------------------|------|-----|--------|-------|
| REV | DATE       | BY  | DESCRIPTION             | CHKD | MTO | STRESS | APRVD |

|   |               |             |            |                                    |           |             |                |  |
|---|---------------|-------------|------------|------------------------------------|-----------|-------------|----------------|--|
| SERVICE:   | VAPOR/LIQUID: | INSUL TYPE: | INSUL THK: | SHOP:                              | FIELD:    | PAINT CODE: | MODULE:        |  |
| R2   | V             | Per LDT     | Per LDT    | N                                  | Y         | Per LDT     | -              |  |
| <div></div> <div>OxyChem Redstone Battleground PROJECT</div> |               |             |            | P&ID:<br>202998C-001-PID-0021-0336 |           |             |                |  |
|   |               |             |            | UNIT#:                             | EWP AREA: | SPEC:       | STRESS CALC #: |  |
|   |               |             |            | 6800                               | 6820      | ARDG-XX01   | -              |  |
|   |               |             |            | LINE No.                           |           |             |                |  |
|   |               |             |            | 2"-R2-67204-ARDG-XX01-N            |           |             |                |  |
| DRAWING NUMBER<br>6820-R2-67204-01   |               |             |            | REV.                               |           |             |                |  |
|   |               |             |            | 0                                  |           |             |                |  |



OxyChem Redstone Battleground PROJECT

