


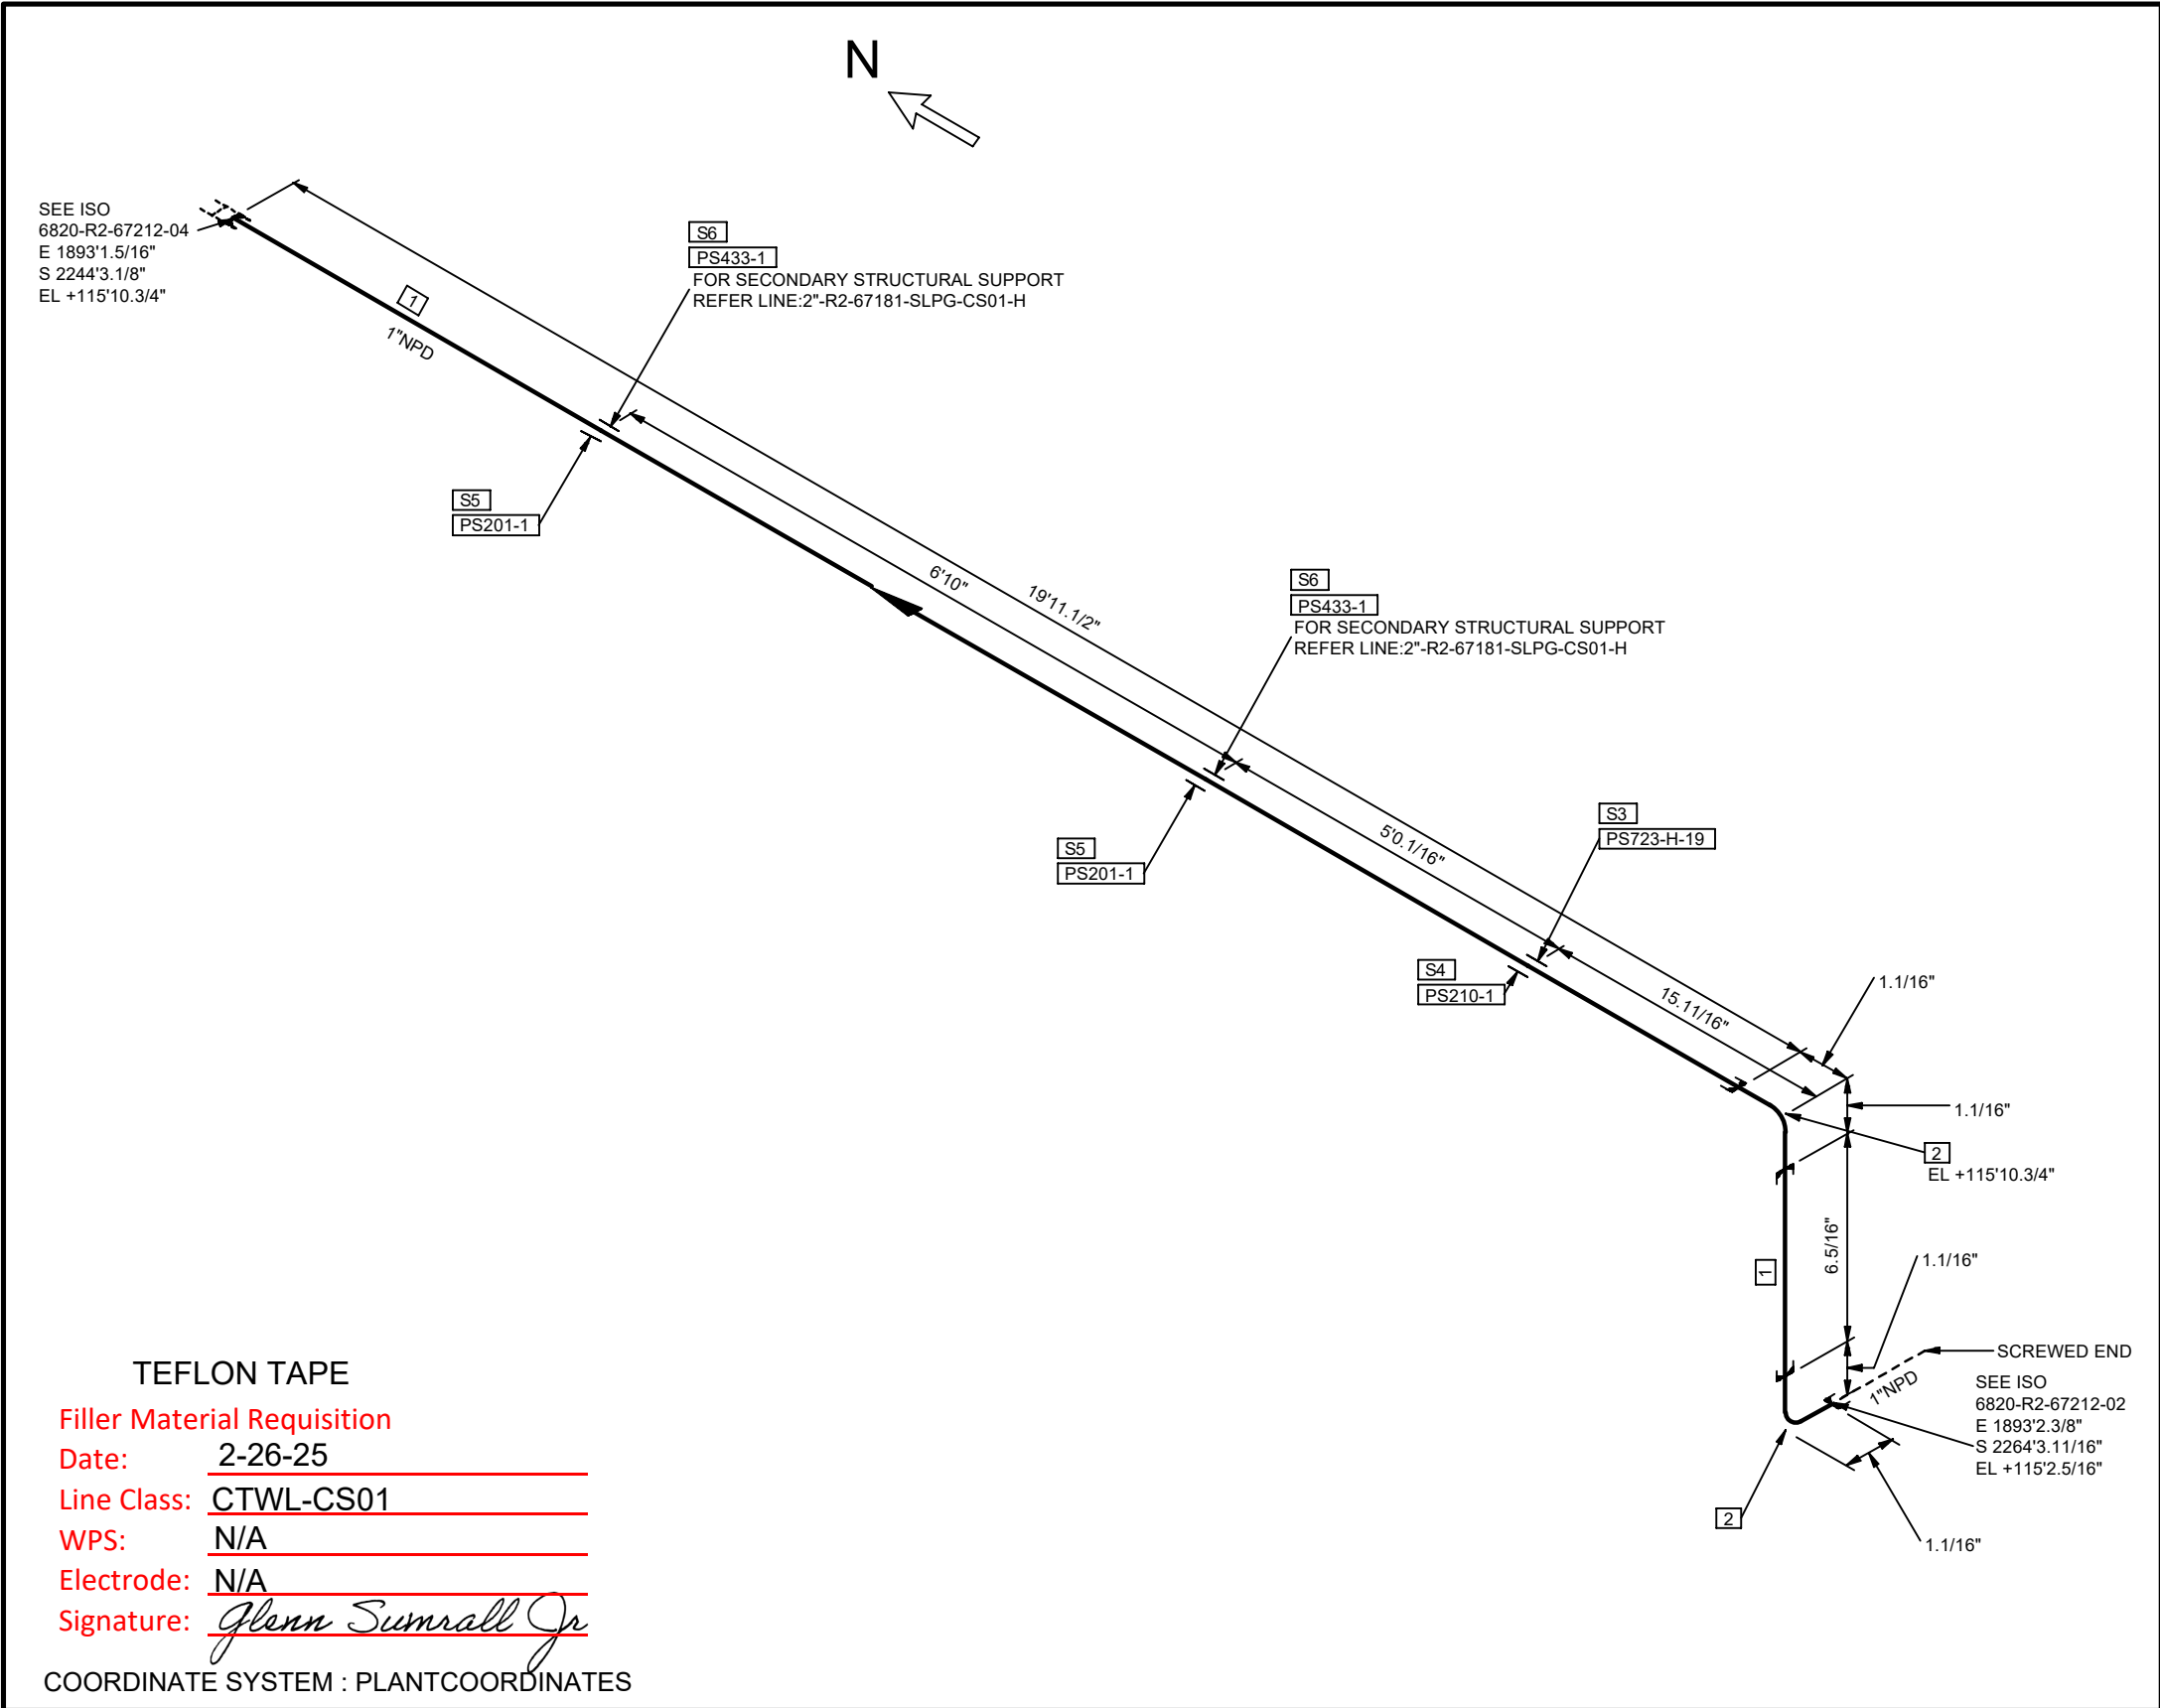

TEFLON TAPE

Filler Material Requisition

Date: 2-26-25

Line Class: CTWL-CS01

WPS: N/A

Electrode: N/A

Signature: *Glenn Sumrall Jr*

COORDINATE SYSTEM : PLANTCOORDINATES

OTHER THAN SHOP MATERIALS				
NO	NPD	DESCRIPTION	IDENT	QTY
1	1	Pipes, Seamless, ASME B36.10, ASTM A106 Gr.B Galv. as per ASTM A153, NPTM Ends, w/ coupling, -, S-XS	CPPD3S28	20.5
2	1	90° Elb, ASME B16.11, ASTM A105N Galv. as per ASTM A153, 3000 Lbs, NPTF Ends, -,	C1DMWEK	2
PIPE SUPPORTS				
3	1	PS723-H-19	PS723	1
4	1	PS210-1	PS210	1
5	1	PS201-1	PS201	2
6	1	PS433-1	PS433	2

NOTES: 1. FOR LINE PRESSURES, TEMPERATURES, INSULATION TYPE AND THICKNESS, ETC. REFER TO LATEST REVISION OF LDT. 2. FOR STANDARD PIPE SUPPORT DETAILS SEE PROJECT STANDARD. 3. FIELD SHIM TO SUIT UNLESS OTHERWISE NOTED. 4. FOR PWHT REQUIREMENTS REFER TO LINE CLASS SPECIFICATION. 5. ALL THREADED PIPE LINE SYSTEMS, FIELD SHALL VERIFY DIMENSION PRIOR TO ERECTION. 6. FFW DESIGNATION AT WELDS INDICATES FIELD FIT WELD, WHERE PIPE FABRICATOR IS TO ADD 9 INCH OF PIPE TO THE ISOMETRIC DIMENSION TO ENABLE THE FIELD TO CUT TO FIT AT SITE. 7. REFER TO 202998C-000-W1-1300-0001 FOR FRP AND DUAL-LAM FABRICATION.	T.EN TECHNIP ENERGIES Information contained in this document is the work product of one or more legal entities of Technip Energies N.V. and embodies confidential and proprietary information of the applicable entity and/or its client use of this information is restricted in accordance with conditions specified by the contract. Technip Energies N.V. and its affiliates disclaim any and all liabilities for any changes or modifications to this document which are made by any person other than the entity that issued the document under the applicable client contract. THIS DOCUMENT IS UNCONTROLLED WHEN REPRODUCED							SERVICE: R2 VAPOR/LIQUID: L INSUL TYPE: Per LDT INSUL THK: Per LDT SHOP: N FIELD: Y PAINT CODE: Per LDT MODULE: -	OXY OxyChem Redstone Battleground PROJECT P&ID: 202998C-001-PID-0021-0332 UNIT#: 6800 LEWP AREA: 6820 SPEC: CTWL-CS01 STRESS CALC #: LINE No. 1"-R2-67212-CTWL-CS01-N DRAWING NUMBER 6820-R2-67212-03 REV. 0		
										0 2025-02-21 RVA ISSUED FOR CONSTRUCTION SAD KJK SMR GR	
											REV DATE BY DESCRIPTION CHKD MTO STRESS APRVD

