


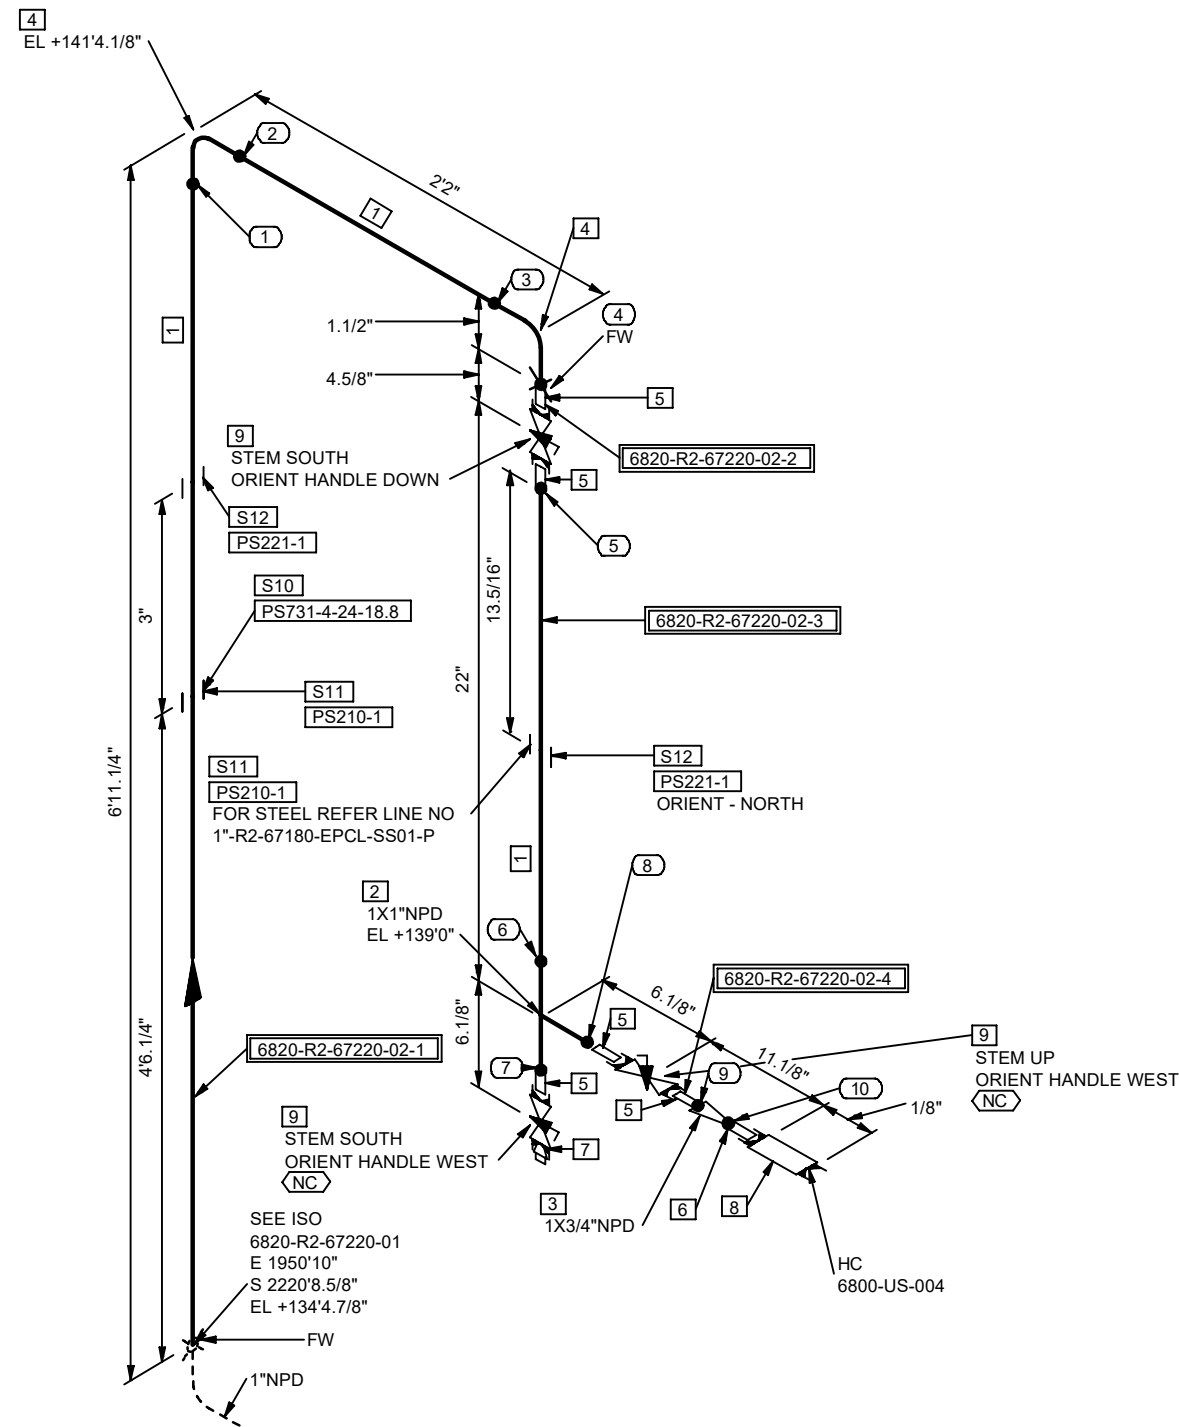

NOTES

- 

Information contained in this document is the work product of one or more legal entities of Technip Energies N.V. and embodies confidential and proprietary information of the applicable entity and/or its client. Use of this information is restricted in accordance with conditions specified by the contract. Technip Energies N.V. and its affiliates disclaim any and all liabilities for any changes or modifications to this document which are made by any person other than the entity that issued the document under the applicable client contract.

THIS DOCUMENT IS UNCONTROLLED WHEN REPRODUCED

0	2025-01-28	RVA	ISSUED FOR CONSTRUCTION	SAD	KJK	SMR	GR
REV	DATE	BY	DESCRIPTION	CHKD	MTO	STRESS	APRVD

Signature: Glenn Sumrall, Jr.

6820-R2-67220-02-1 6820-R2-67220-02-2 6820-R2-67220-02-3
6820-R2-67220-02-4



SERVICE:	VAPOR/LIQUID:	INSUL TYPE:	INSUL THK:	SHOP:	FIELD:	PAINT CODE:	MODULE:
R2	V	Per LDT	Per LDT	Y	Y	Per LDT	-
 OxyChem Redstone Battleground PROJECT				P&ID: 202998C-001-PID-0021-0337			
				UNIT#:	SWP AREA:	SPEC:	STRESS CALC #:
				6800	6820	ARWW-CS01	
				LINE No.			
				1"-R2-67220-ARWW-CS01-N			
				DRAWING NUMBER		REV.	
				6820-R2-67220-02		0	