


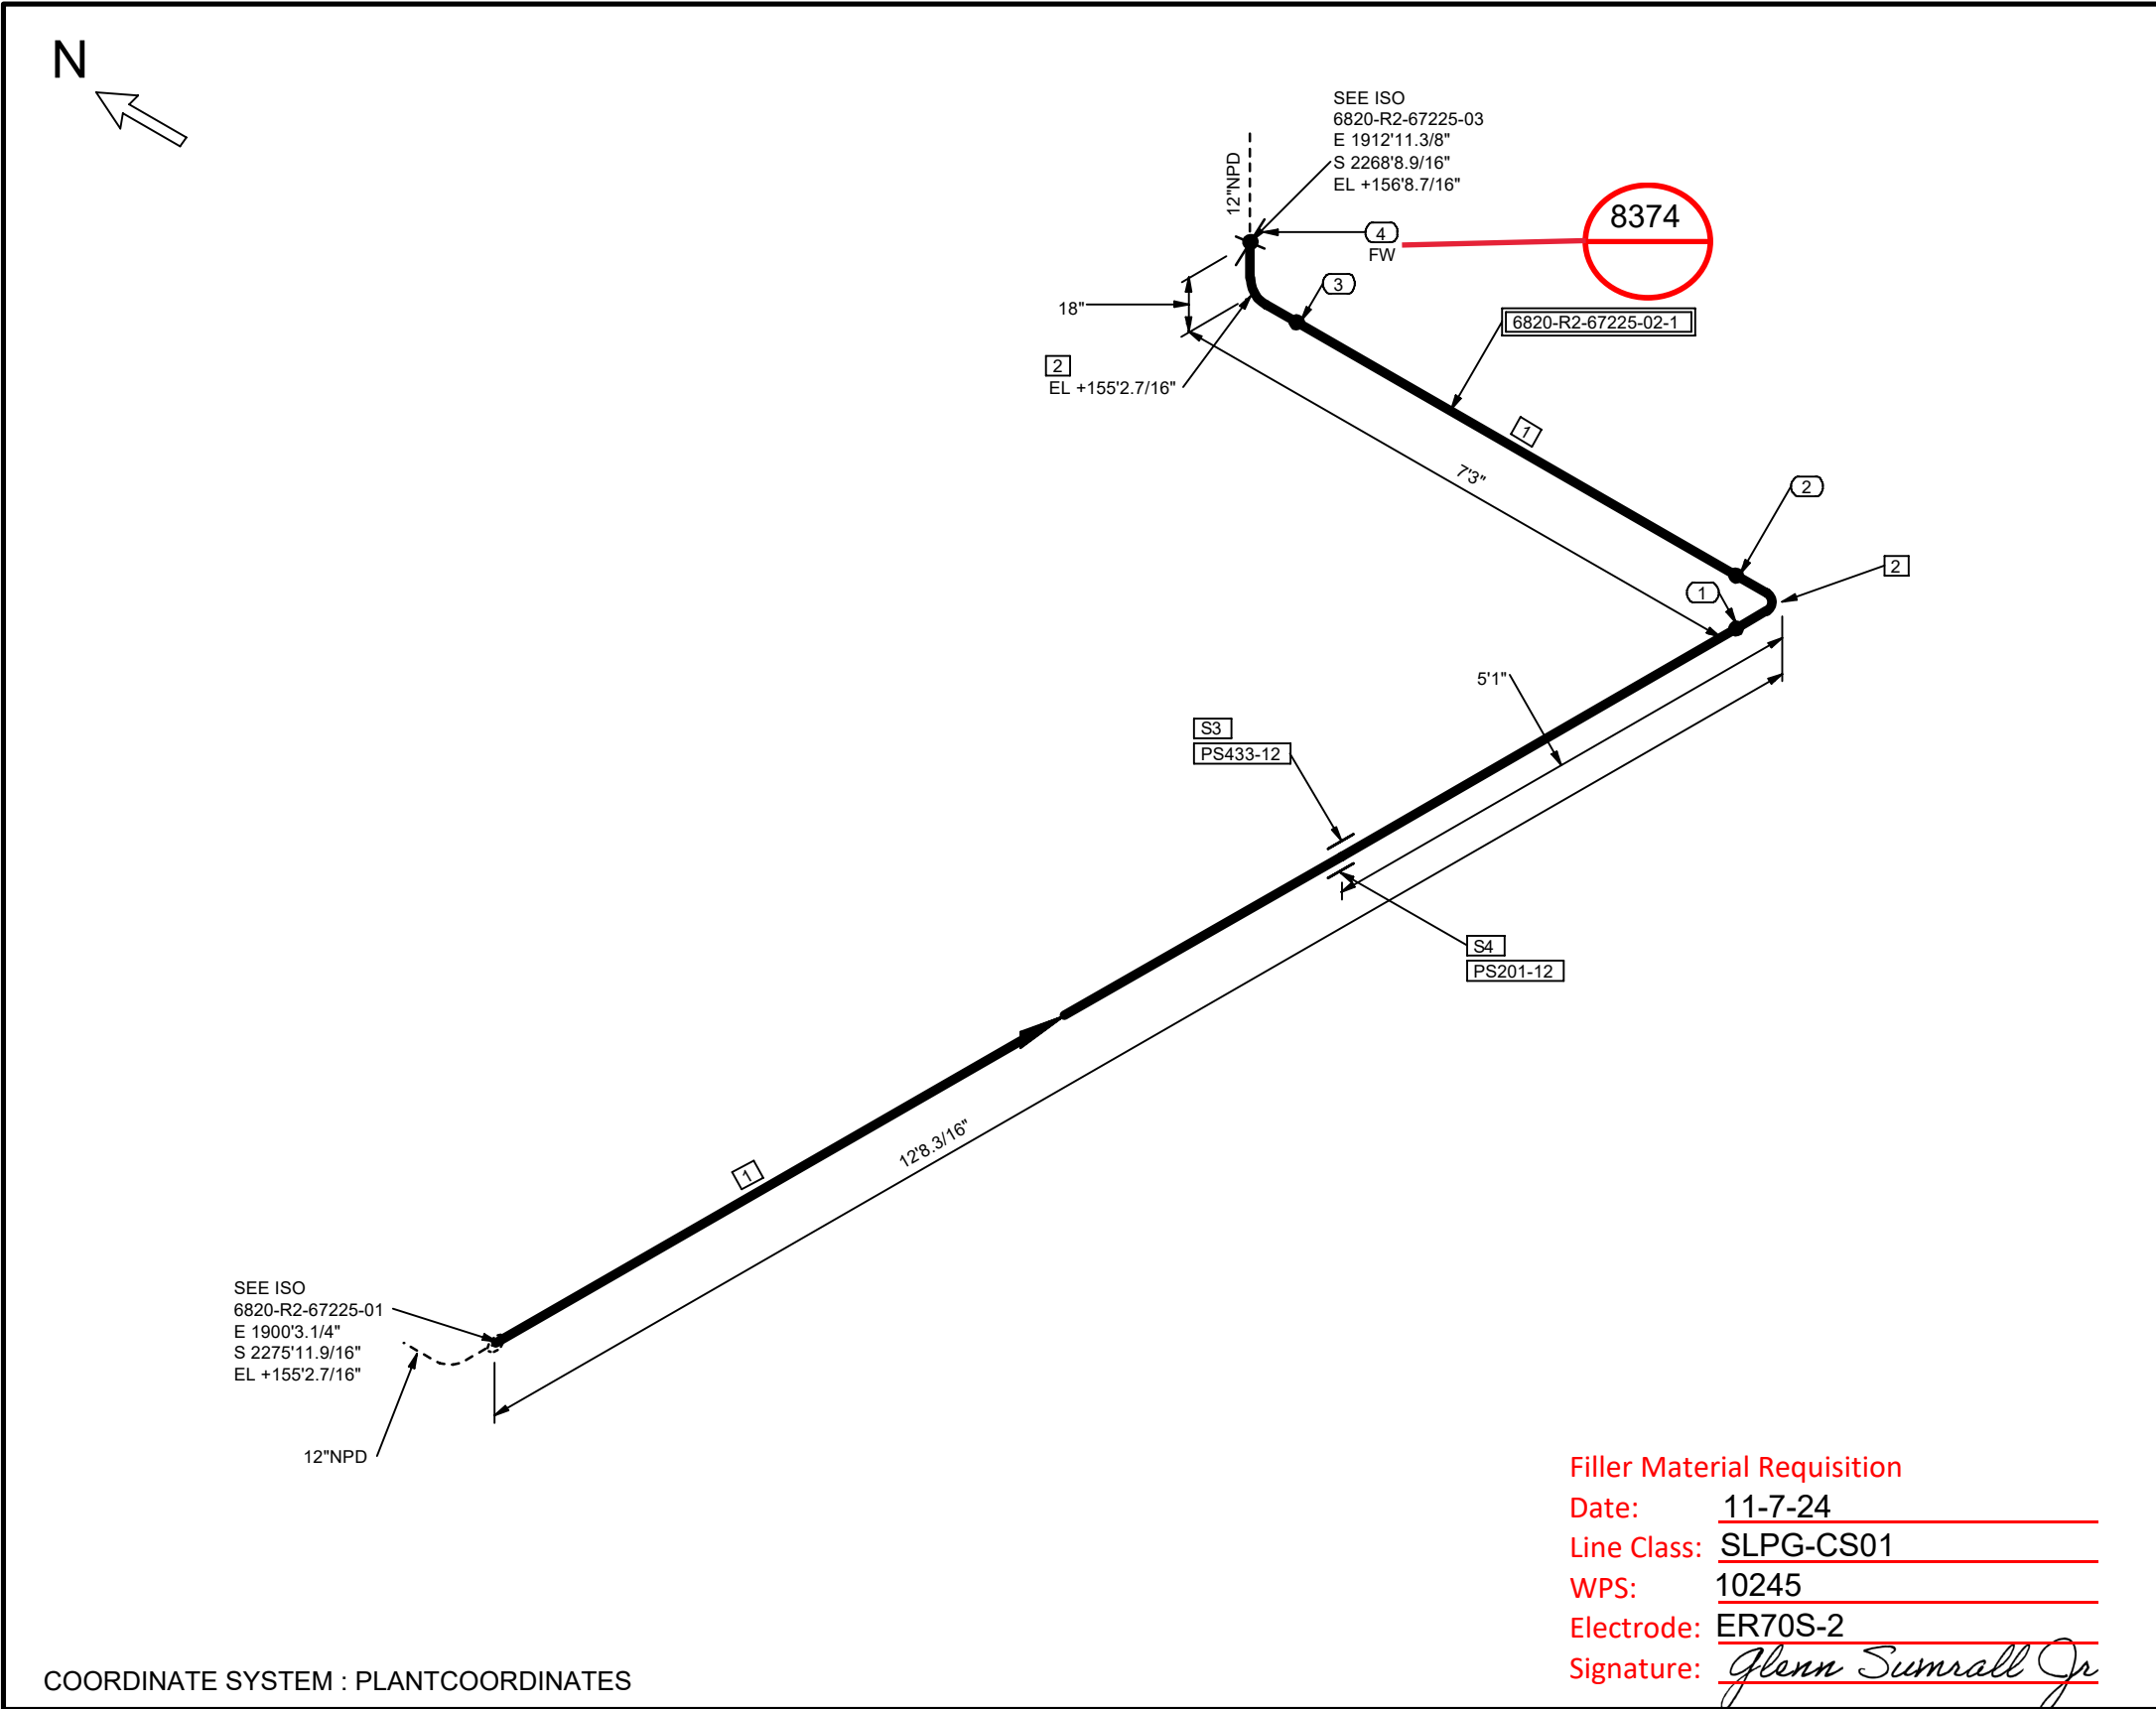

SHOP MATERIALS				
NO	NPD	DESCRIPTION	IDENT	QTY
1	12	Pipes, Seamless, ASME B36.10, ASTM A106 Gr.B, BE, -, -, S-STD	CPP0AATK	15.5 '
2	12	90° Elb LR, Seamless, ASME B16.9, ASTM A234 Gr.WPB, BW Ends, -, -, S-STD	CDB66G82	2
OTHER THAN SHOP MATERIALS				
NO	NPD	DESCRIPTION	IDENT	QTY
PIPE SUPPORTS				
3	12	PS433-12	PS433	1
4	12	PS201-12	PS201	1
PIECE MARKS				
6820-R2-67225-02-1				

Turner Industries Group, LLC
Received
November 7, 2024
DOCUMENT CONTROL

NOTES:		T.EN TECHNIP ENERGIES Information contained in this document is the work product of one or more legal entities of Technip Energies N.V. and embodies confidential and proprietary information of the applicable entity and/or its client. Use of this information is restricted in accordance with conditions specified by the contract. Technip Energies N.V. and its affiliates disclaim any and all liabilities for any changes or modifications to this document which are made by any person other than the entity that issued the document under the applicable client contract. THIS DOCUMENT IS UNCONTROLLED WHEN REPRODUCED										SERVICE: R2		VAPOR/LIQUID: V		INSUL TYPE: Per LDT		INSUL THK: Per LDT		SHOP: Y		FIELD: Y		PAINT CODE: Per LDT		MODULE: -	
1. FOR LINE PRESSURES, TEMPERATURES, INSULATION TYPE AND THICKNESS, ETC. REFER TO LATEST REVISION OF LDT.																											
2. FOR STANDARD PIPE SUPPORT DETAILS SEE PROJECT STANDARD.																											
3. FIELD SHIM TO SUIT UNLESS OTHERWISE NOTED.																											
4. FOR PWHT REQUIREMENTS REFER TO LINE CLASS SPECIFICATION.																											
5. ALL THREADED PIPE LINE SYSTEMS, FIELD SHALL VERIFY DIMENSION PRIOR TO ERECTION.																											
6. FFW DESIGNATION AT WELDS INDICATES FIELD FIT WELD, WHERE PIPE FABRICATOR IS TO ADD 9 INCH OF PIPE TO THE ISOMETRIC DIMENSION TO ENABLE THE FIELD TO CUT TO FIT AT SITE.																											
7. REFER TO 202998C-000-W1-1300-0001 FOR FRP AND DUAL-LAM FABRICATION.																											

