


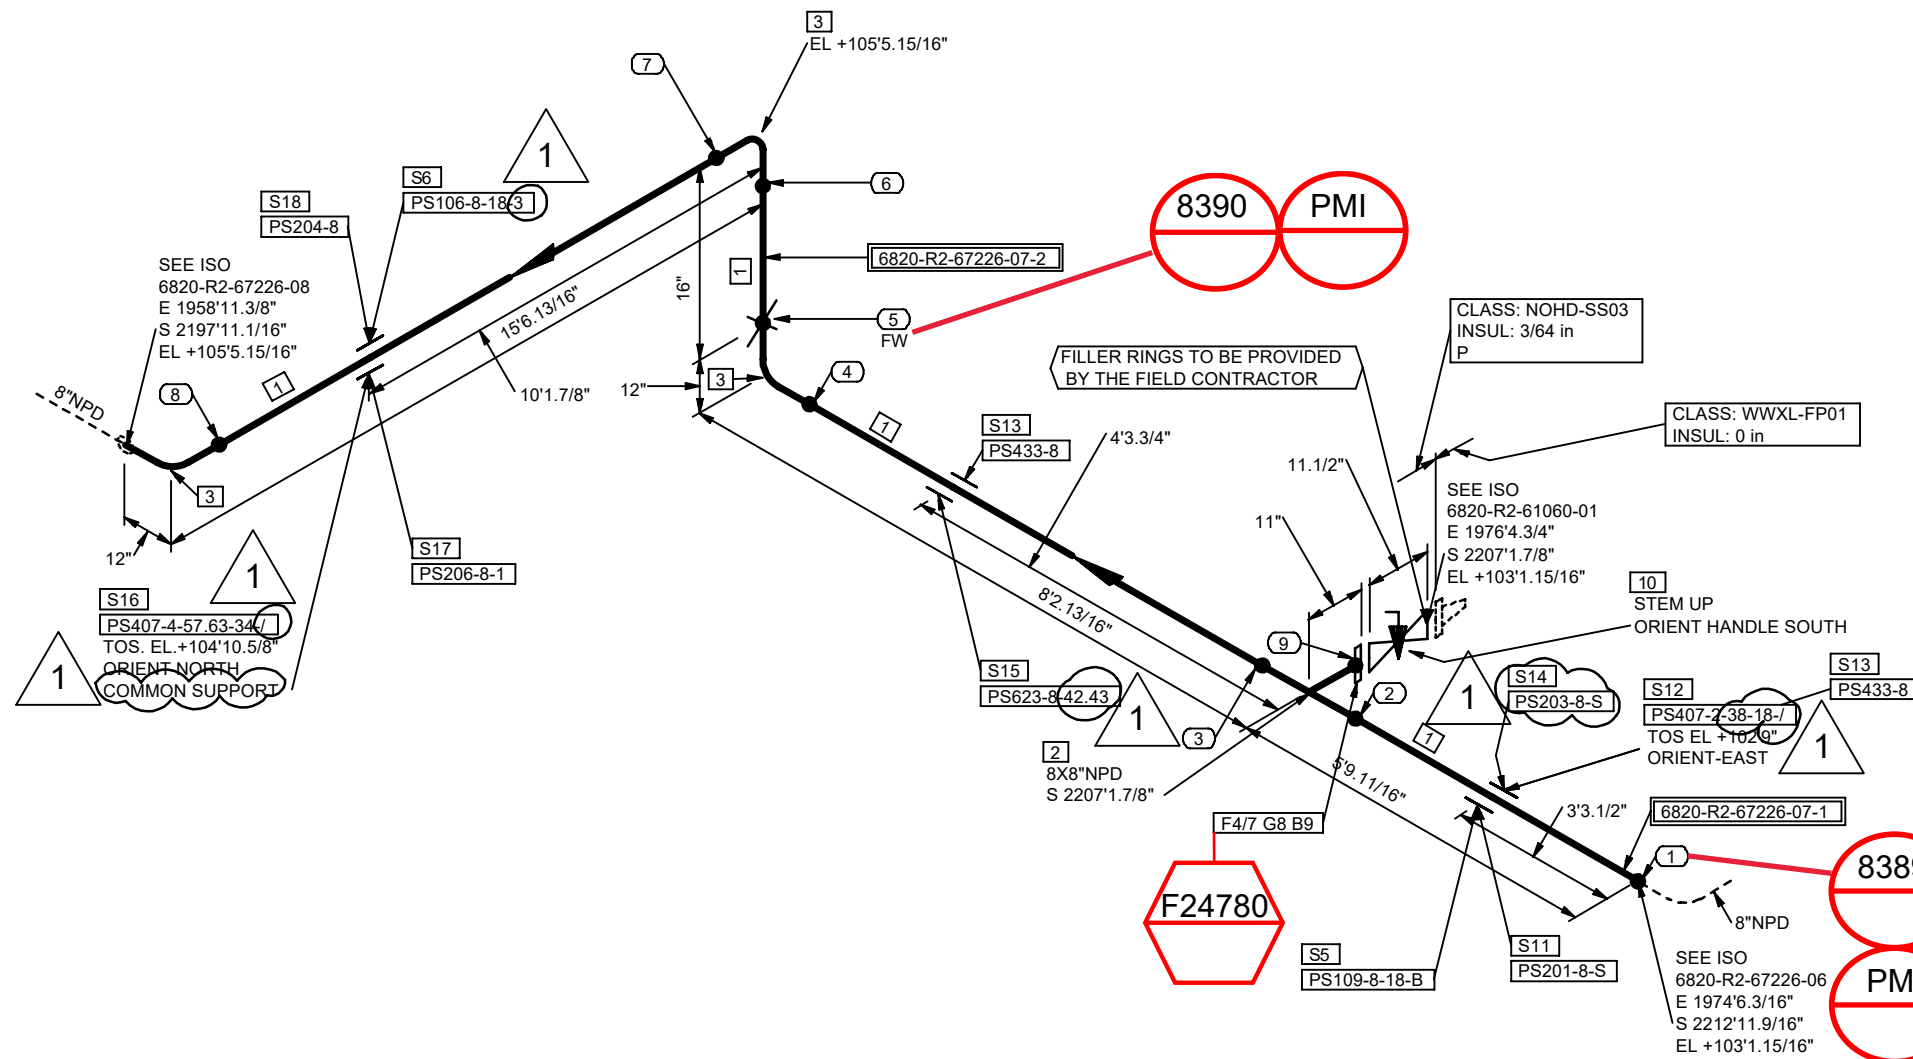

Filler Material Requisition
Date: 4-25-25
Line Class: NOHD-SS03
WPS: 802
Electrode: ER308L
Signature: *Glenn Sumrall Jr*

COORDINATE SYSTEM : PLANTCOORDINATES

NOTES:

- FOR LINE PRESSURES, TEMPERATURES, INSULATION TYPE AND THICKNESS, ETC. REFER TO LATEST REVISION OF LDT.
- FOR STANDARD PIPE SUPPORT DETAILS SEE PROJECT STANDARD.
- FIELD SHIM TO SUIT UNLESS OTHERWISE NOTED.
- FOR PWHT REQUIREMENTS REFER TO LINE CLASS SPECIFICATION.
- ALL THREADED PIPE LINE SYSTEMS, FIELD SHALL VERIFY DIMENSION PRIOR TO ERECTION.
- FFW DESIGNATION AT WELDS INDICATES FIELD FIT WELD, WHERE PIPE FABRICATOR IS TO ADD 9 INCH OF PIPE TO THE ISOMETRIC DIMENSION TO ENABLE THE FIELD TO CUT TO FIT AT SITE.
- REFER TO 202998C-000-W1-1300-0001 FOR FRP AND DUAL-LAM FABRICATION.




Information contained in this document is the work product of one or more legal entities of Technip Energies N.V. and embodies confidential and proprietary information of the applicable entity and/or its client. Use of this information is restricted in accordance with conditions specified by the contract. Technip Energies N.V. and its affiliates disclaim any and all liabilities for any changes or modifications to this document which are made by any person other than the entity that issued the document under the applicable client contract.

THIS DOCUMENT IS UNCONTROLLED WHEN REPRODUCED

REV	DATE	BY	DESCRIPTION	CHKD	MTD	STRESS	APRVD
1	2025-04-18	RVA	ISSUED FOR CONSTRUCTION	SAD	KJK	SMR	GR
0	2024-11-08	RVA	ISSUED FOR CONSTRUCTION	SAD	KJK	SMR	GR

SHOP MATERIALS				
NO	NPD	DESCRIPTION	IDENT	QTY
1	8	Pipes, Seamless, ASME B36.19/B36.10, ASTM A312 Gr.TP304L, BE, -, -, S-10S	C7FCT25	25.8
2	8X8	Eq Te, Seamless, ASME B16.9, ASTM A403 Gr.WP304L, BW Ends, -,Annealed, S-10S	C6SEUJ1B	1
3	8	90° Elb LR, Seamless, ASME B16.9, ASTM A403 Gr.WP304L, BW Ends, -,Annealed, S-10S	C6SEUJRF	3
4	8	LJ Flg, ASME B16.5, ASTM A105 Galv. as per ASTM A153, 150 Lbs, FF, -,	C26WFFFR	1
PIPE SUPPORTS				
5	8	PS109-8-18-B	PS109	1
6	8	PS106-8-18-B	PS106	1
MISCELLANEOUS COMPONENTS				
7	8	Stub SP, Seamless, ASME B16.9, ASTM A403 Gr.WP304L, BW Ends, -,Annealed, x S-10S	C8A5BL7M	1
OTHER THAN SHOP MATERIALS				
NO	NPD	DESCRIPTION	IDENT	QTY
8	8	NM Flat Gk, Barium Sulfate filled PTFE, 150 Lbs, RF as per ASME B16.5, -, Thk=1/8in, -,	C6SBWZF4	1
9	3/4	SBlt 2 HHx N, A193 Gr.B7/A194 Gr.2H, -, Xylan PTFE Coated, - 4.75 in. Length	C6S4K8BE	8
10	8	Plug Flg,SP, Tapered Plug, Non Lubricated, API 599, ASTM A351 Gr.CF8M, 150 Lbs, RF, Ends as per ASME B16.5, -, GO,-, -, Valve Tag: PL-0548	C6SDVYKY	1
PIPE SUPPORTS				
11	8	PS201-8-S	PS201	1
12	8	PS407-2-38-18-B	PS407	1
13	8	PS433-8	PS433	2
14	8	PS203-8-S	PS203	1
15	8	PS623-8-42.43	PS623	1
16	8	PS407-4-57.63-34-L	PS407	1
17	8	PS206-8-1	PS206	1
18	8	PS204-8	PS204	1
PIECE MARKS				
6820-R2-67226-07-1 6820-R2-67226-07-2				

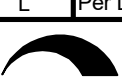

SERVICE:	VAPOR/LIQUID:	INSUL TYPE:	INSUL THK:	SHOP:	FIELD:	PAINT CODE:	MODULE:	
R2	L	Per LDT	Per LDT	Y	Y	Per LDT	-	
				P&ID:				
				202998C-001-PID-0021-0338				
				UNIT#:	EWPA AREA:	SPEC:	STRESS CALC #:	
				6800	6820	NOHD-SS03	CN-0129	
				LINE No.				
OxyChem Redstone Battleground PROJECT				8"-R2-67226-NOHD-SS03-P				
				DRAWING NUMBER				
				6820-R2-67226-07				
				REV. 1				

