


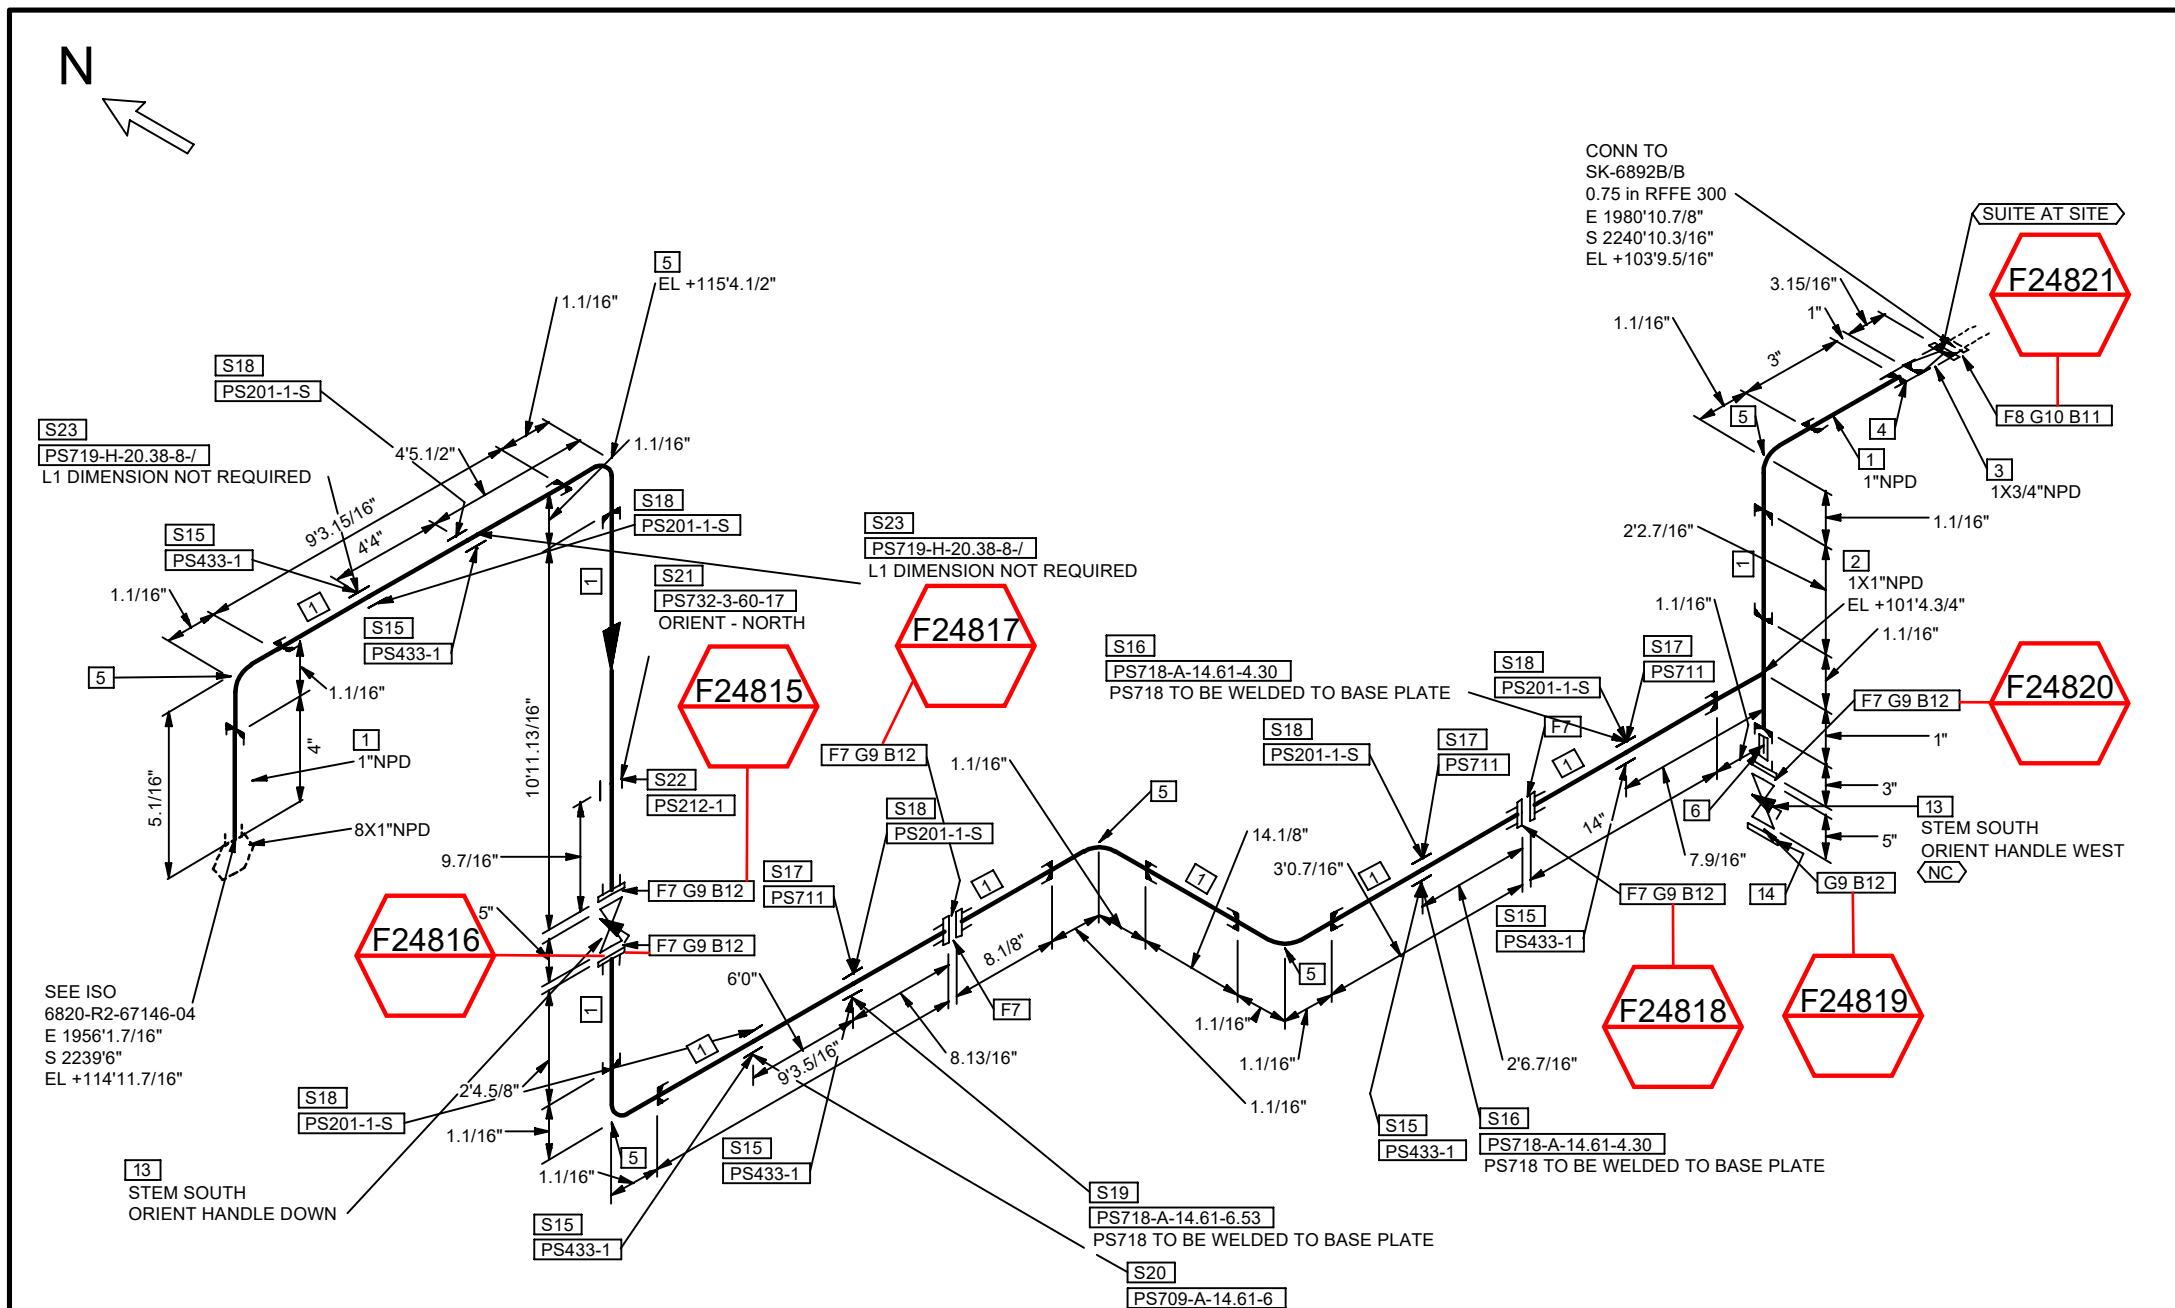

SERVICE: R2	VAPOR/LIQUID: L	INSUL TYPE: Per LDT	INSUL THK: Per LDT	SHOP: N	FIELD: Y	PAINT CODE: Per LDT	MODULE: -
				P&ID: 202998C-001-PID-0021-0331			
				UNIT#: 6800	EWP AREA: 6820	SPEC: EPCL-SS01	STRESS CALC #: -
				LINE No. 1"-R2-67263-EPCL-SS01-P			
				DRAWING NUMBER 6820-R2-67263-01			REV. 0
				OxyChem Redstone Battleground PROJECT			