


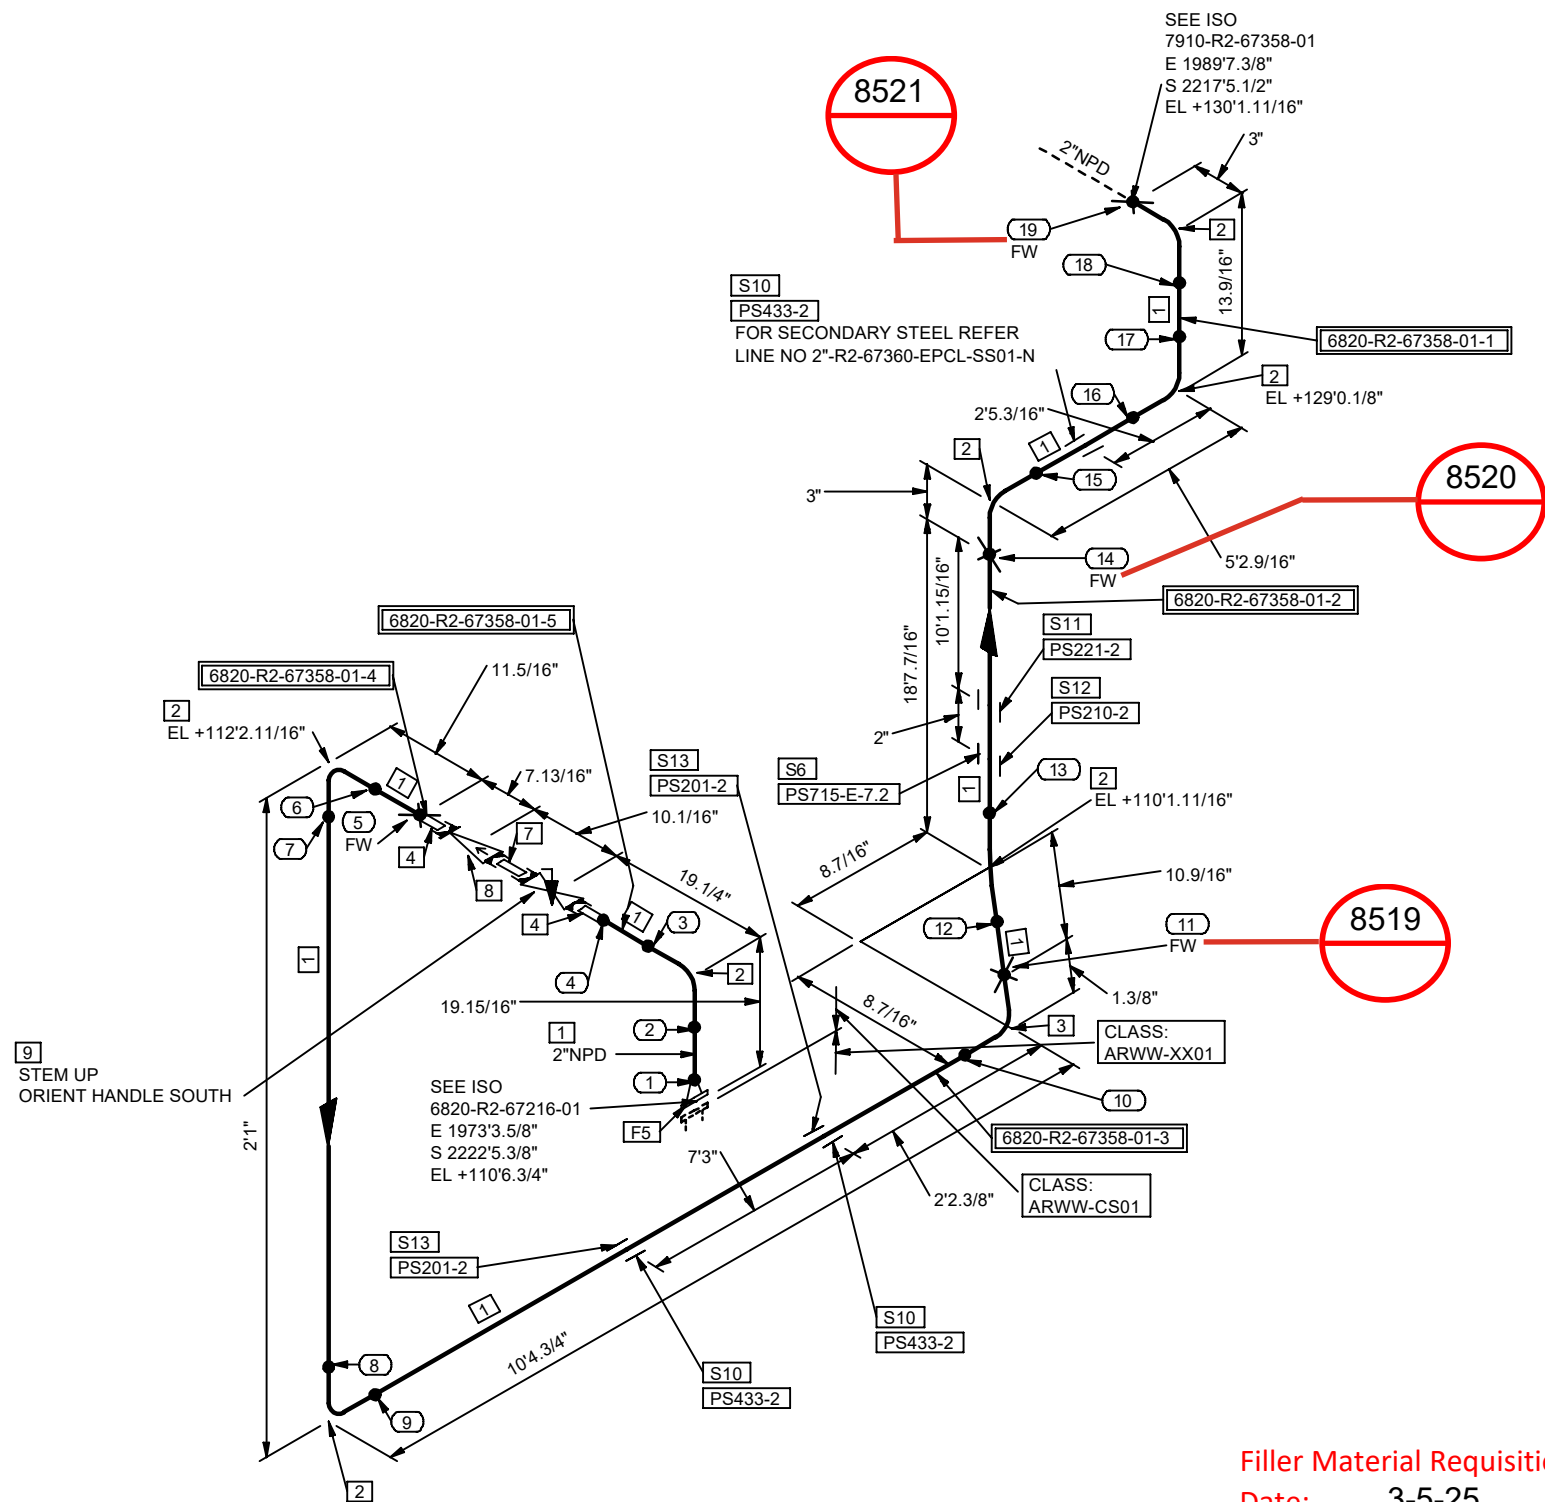

Filler Material Requisition

Date: 3-5-25
Line Class: ARWW-CS01
WPS: 10245
Electrode: ER70S-2
Signature: *Glenn Sumrall, Jr.*

SHOP MATERIALS

NO	NPD	DESCRIPTION	IDENT	QTY
1	2	Pipes, Seamless, ASME B36.10, ASTM A106 Gr.B, BE, -, -, S-XS	CPP0AAUB	38.6
2	2	90° Elb LR, Seamless, ASME B16.9, ASTM A234 Gr.WPB, BW Ends, -, -, S-XS	CDB66GD6	7
3	2	45° Elb LR, Seamless, ASME B16.9, ASTM A234 Gr.WPB, BW Ends, -, -, S-XS	CDB66FGD	1
4	2	Nipple, ASTM A106 Gr.B, BE/NPTM End, L = 6in, -, S-XS	C58PVZ7V	2
5	2	WN Flg, ASME B16.5, ASTM A105N, 150 Lbs, RF/BW End, -, S-XS	CFG6WJ8W	1

PIPE SUPPORTS

6	2	PS715-E-7.2	PS715	1
---	---	-------------	-------	---

OTHER THAN SHOP MATERIALS

NO	NPD	DESCRIPTION	IDENT	QTY
7	2	Nipple, ASTM A106 Gr.B, BE/NPTM End, L = 6in, -, S-XS	C58PVZ7V	1
8	2	SwgChk Y Fem,MSS SP-80,ASTM B61 UNS C92200,NPTF Ends,200 Lbs, Valve Tag: CH-0171	C766B01H	1
9	2	Plug Fem,RgP, Tapered Plug, Non Lubricated, API 599, ASTM A395 Gr.60-40-18, 300 Lbs, NPTF Ends, Ends as per ASME B16.11,-, LO, -, Valve Tag: PL-0545	C76S9AH4	1

PIPE SUPPORTS

10	2	PS433-2	PS433	3
11	2	PS221-2	PS221	1
12	2	PS210-2	PS210	1
13	2	PS201-2	PS201	2

PIECE MARKS

6820-R2-67358-01-1 6820-R2-67358-01-2 6820-R2-67358-01-3
6820-R2-67358-01-4 6820-R2-67358-01-5

COORDINATE SYSTEM : PLANTCOORDINATES

NOTES:

- FOR LINE PRESSURES, TEMPERATURES, INSULATION TYPE AND THICKNESS, ETC. REFER TO LATEST REVISION OF LDT.
- FOR STANDARD PIPE SUPPORT DETAILS SEE PROJECT STANDARD.
- FIELD SHIM TO SUIT UNLESS OTHERWISE NOTED.
- FOR PWHT REQUIREMENTS REFER TO LINE CLASS SPECIFICATION.
- ALL THREADED PIPE LINE SYSTEMS, FIELD SHALL VERIFY DIMENSION PRIOR TO ERECTION.
- FFW DESIGNATION AT WELDS INDICATES FIELD FIT WELD, WHERE PIPE FABRICATOR IS TO ADD 9 INCH OF PIPE TO THE ISOMETRIC DIMENSION TO ENABLE THE FIELD TO CUT TO FIT AT SITE.
- REFER TO 202998C-000-W1-1300-0001 FOR FRP AND DUAL-LAM FABRICATION.



Information contained in this document is the work product of one or more legal entities of Technip Energies N.V. and embodies confidential and proprietary information of the applicable entity and/or its client. Use of this information is restricted in accordance with conditions specified by the contract. Technip Energies N.V. and its affiliates disclaim any and all liabilities for any changes or modifications to this document which are made by any person other than the entity that issued the document under the applicable client contract.

THIS DOCUMENT IS UNCONTROLLED WHEN REPRODUCED

REV	DATE	BY	DESCRIPTION	CHKD	MTO	STRESS	APRVD
0	2025-02-28	RVA	ISSUED FOR CONSTRUCTION	SAD	KJK	SMR	GR

SERVICE: R2	VAPOR/LIQUID: V	INSUL TYPE: Per LDT	INSUL THK: Per LDT	SHOP: Y	FIELD: Y	PAINT CODE: Per LDT	MODULE: -	
 OxyChem Redstone Battleground PROJECT				P&ID: 202998C-001-PID-0021-0337				
				UNIT#: 6800	EWP AREA: 6820	SPEC: ARWW-CS01	STRESS CALC #: -	
				LINE No. 2"-R2-67358-ARWW-CS01-N				
				DRAWING NUMBER 6820-R2-67358-01				
				REV. 0				

OxyChem Redstone Battleground PROJECT

