


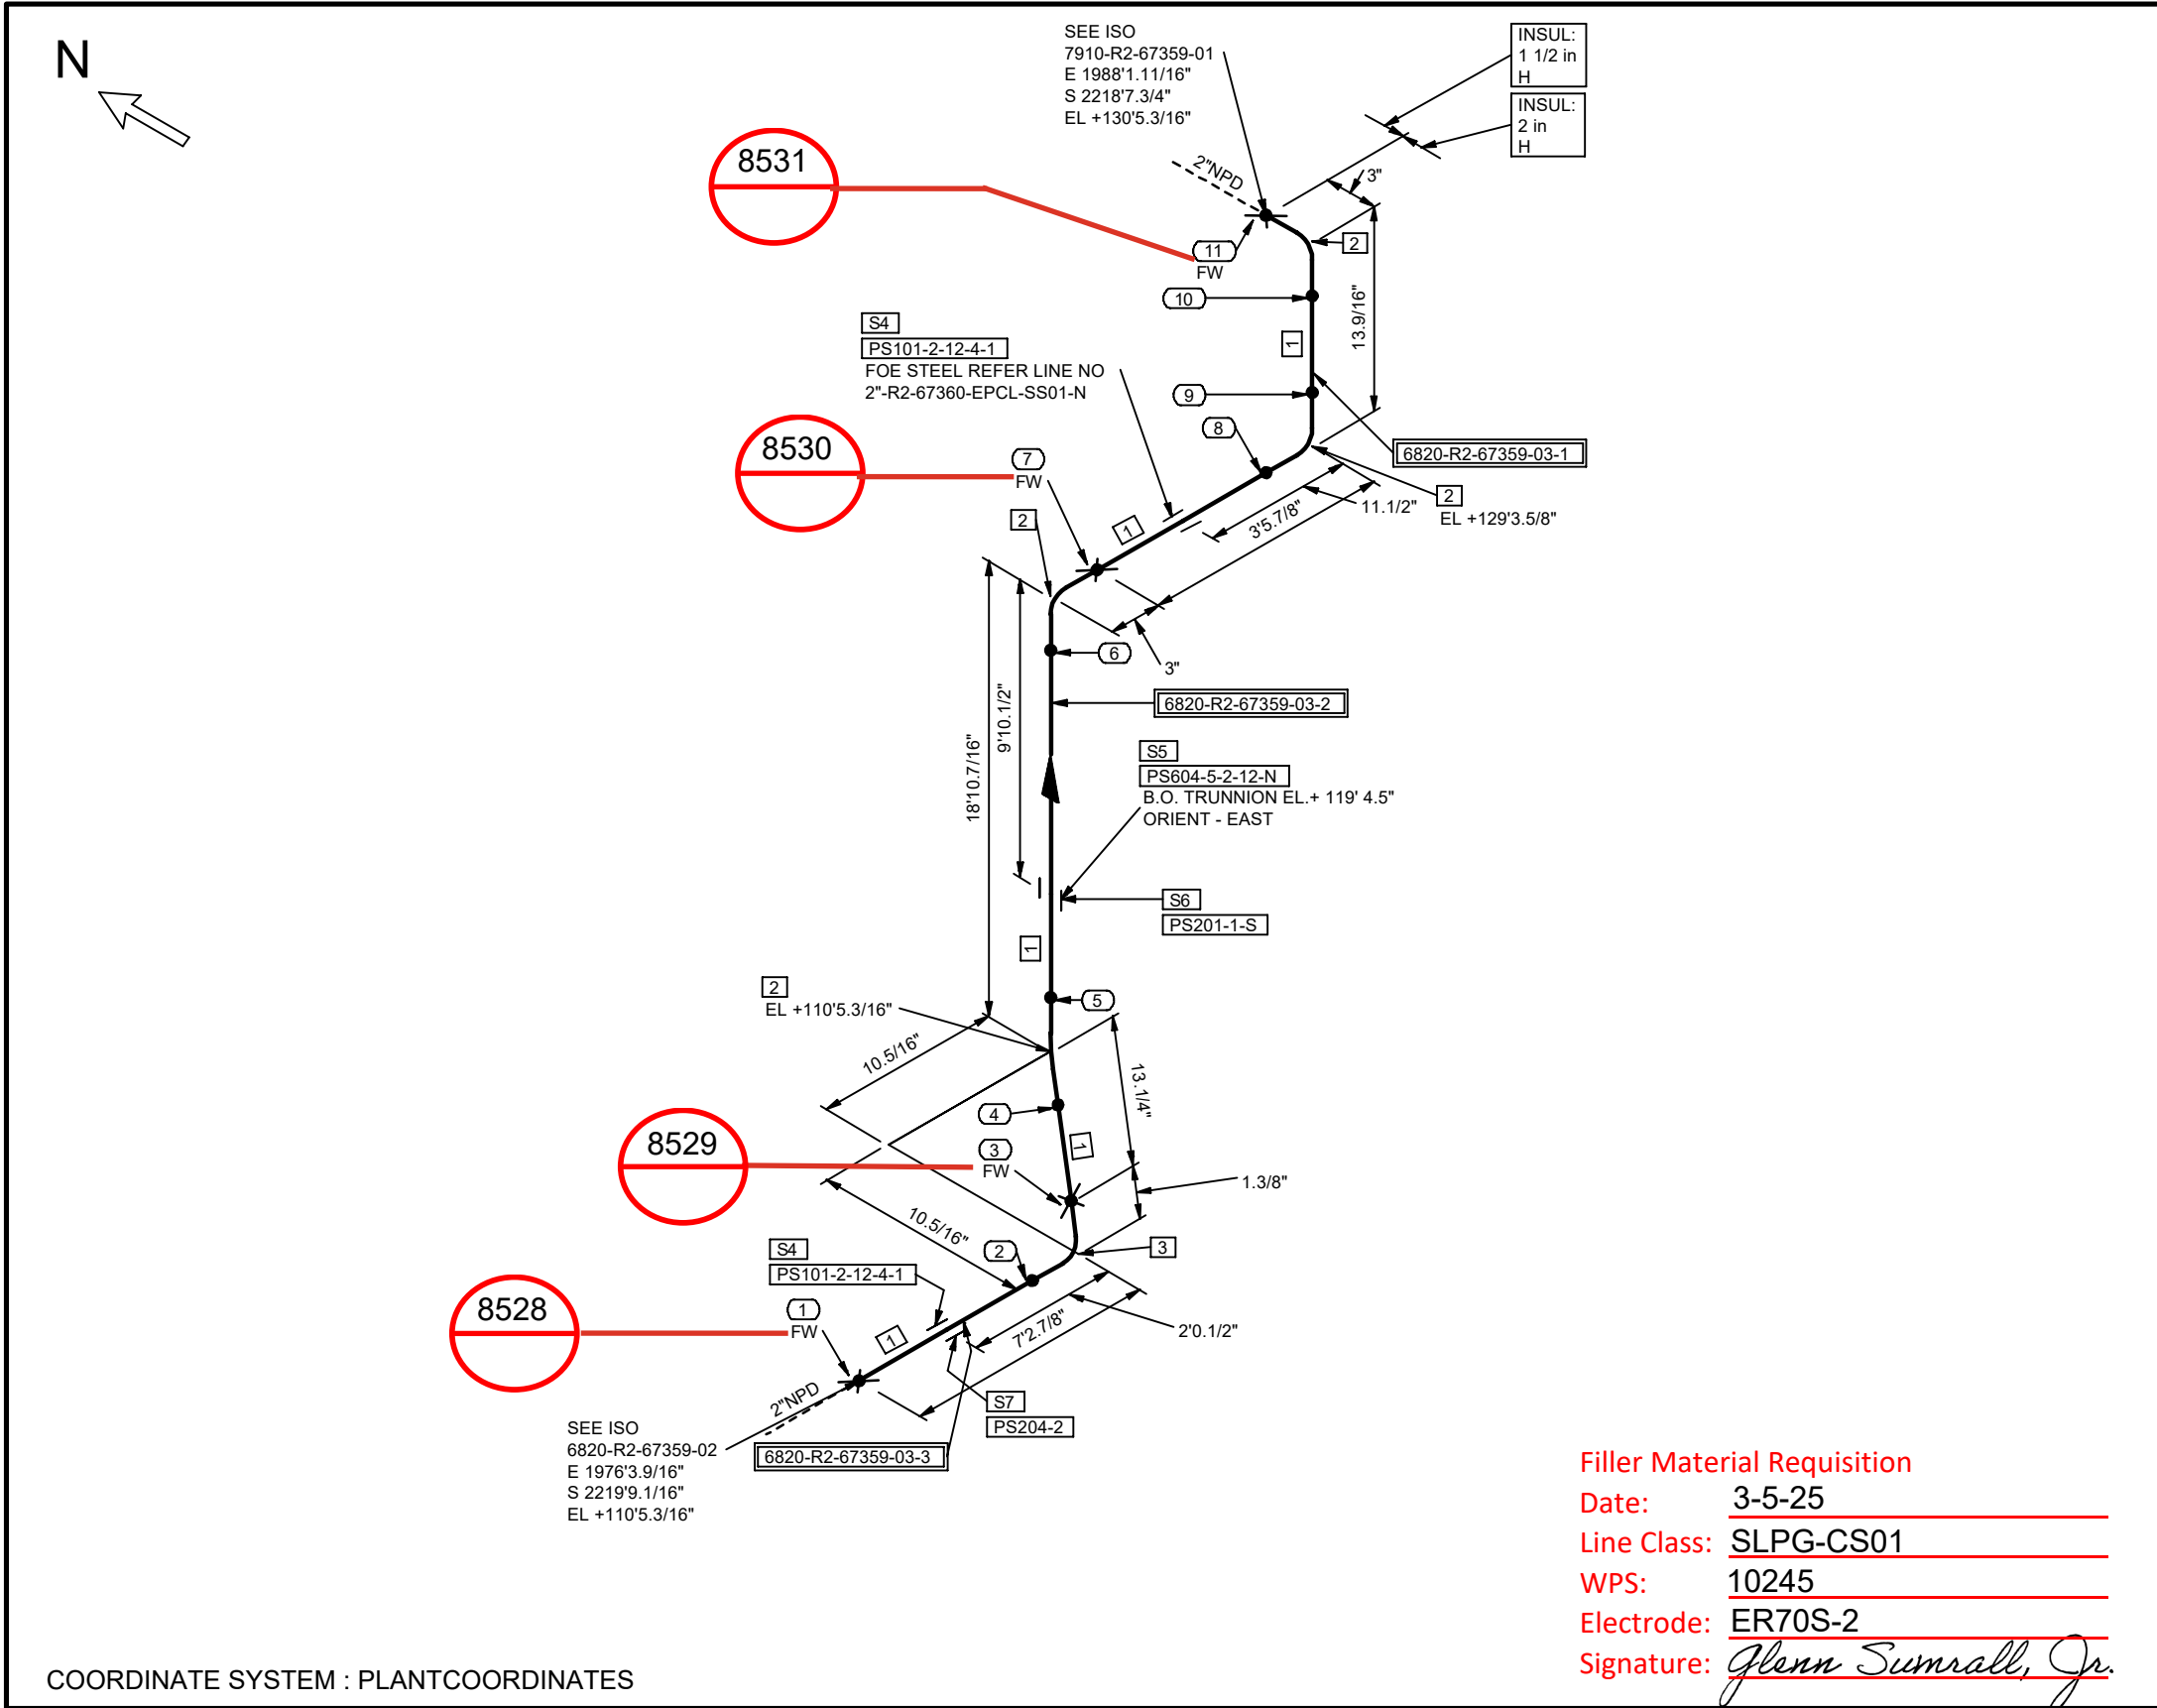

COORDINATE SYSTEM : PLANTCOORDINATES

NOTES:

- FOR LINE PRESSURES, TEMPERATURES, INSULATION TYPE AND THICKNESS, ETC. REFER TO LATEST REVISION OF LDT.
- FOR STANDARD PIPE SUPPORT DETAILS SEE PROJECT STANDARD.
- FIELD SHIM TO SUIT UNLESS OTHERWISE NOTED.
- FOR PWHT REQUIREMENTS REFER TO LINE CLASS SPECIFICATION.
- ALL THREADED PIPE LINE SYSTEMS, FIELD SHALL VERIFY DIMENSION PRIOR TO ERECTION.
- FFW DESIGNATION AT WELDS INDICATES FIELD FIT WELD, WHERE PIPE FABRICATOR IS TO ADD 9 INCH OF PIPE TO THE ISOMETRIC DIMENSION TO ENABLE THE FIELD TO CUT TO FIT AT SITE.
- REFER TO 202998C-000-W1-1300-0001 FOR FRP AND DUAL-LAM FABRICATION.



Information contained in this document is the work product of one or more legal entities of Technip Energies N.V. and embodies confidential and proprietary information of the applicable entity and/or its client. Use of this information is restricted in accordance with conditions specified by the contract. Technip Energies N.V. and its affiliates disclaim any and all liabilities for any changes or modifications to this document which are made by any person other than the entity that issued the document under the applicable client contract.

THIS DOCUMENT IS UNCONTROLLED WHEN REPRODUCED

Filler Material Requisition

Date: 3-5-25
Line Class: SLPG-CS01
WPS: 10245
Electrode: ER70S-2
Signature: *Glenn Sumrall, Jr.*

SHOP MATERIALS

NO	NPD	DESCRIPTION	IDENT	QTY
1	2	Pipes, Seamless, ASME B36.10, ASTM A106 Gr.B, BE, -, -, S-XS	CPP0AAUB	30.3
2	2	90° Elb LR, Seamless, ASME B16.9, ASTM A234 Gr.WPB, BW Ends, -, -, S-XS	CDB66GD6	4
3	2	45° Elb LR, Seamless, ASME B16.9, ASTM A234 Gr.WPB, BW Ends, -, -, S-XS	CDB66FGD	1

PIPE SUPPORTS

4	2	PS101-2-12-4-1	PS101	2
5	2	PS604-5-2-12-N	PS604	1

OTHER THAN SHOP MATERIALS

NO	NPD	DESCRIPTION	IDENT	QTY
6	2	PS201-1-S	PS201	1
7	2	PS204-2	PS204	1

PIECE MARKS

6820-R2-67359-03-1 6820-R2-67359-03-2 6820-R2-67359-03-3



SERVICE: R2	VAPOR/LIQUID: V	INSUL TYPE: Per LDT	INSUL THK: Per LDT	SHOP: Y	FIELD: Y	PAINT CODE: Per LDT	MODULE: -												
 OxyChem Redstone Battleground PROJECT P&ID: 202998C-001-PID-0021-0335 <table><tr><td>UNIT#: 6800</td><td>EWPA AREA: 6820</td><td>SPEC: SLPG-CS01</td><td>STRESS CALC #: -</td></tr><tr><td colspan="4">LINE No. 2"-R2-67359-SLPG-CS01-H</td></tr><tr><td colspan="3">DRAWING NUMBER 6820-R2-67359-03</td><td>REV. 0</td></tr></table>								UNIT#: 6800	EWPA AREA: 6820	SPEC: SLPG-CS01	STRESS CALC #: -	LINE No. 2"-R2-67359-SLPG-CS01-H				DRAWING NUMBER 6820-R2-67359-03			REV. 0
UNIT#: 6800	EWPA AREA: 6820	SPEC: SLPG-CS01	STRESS CALC #: -																
LINE No. 2"-R2-67359-SLPG-CS01-H																			
DRAWING NUMBER 6820-R2-67359-03			REV. 0																

OxyChem Redstone Battleground PROJECT

