



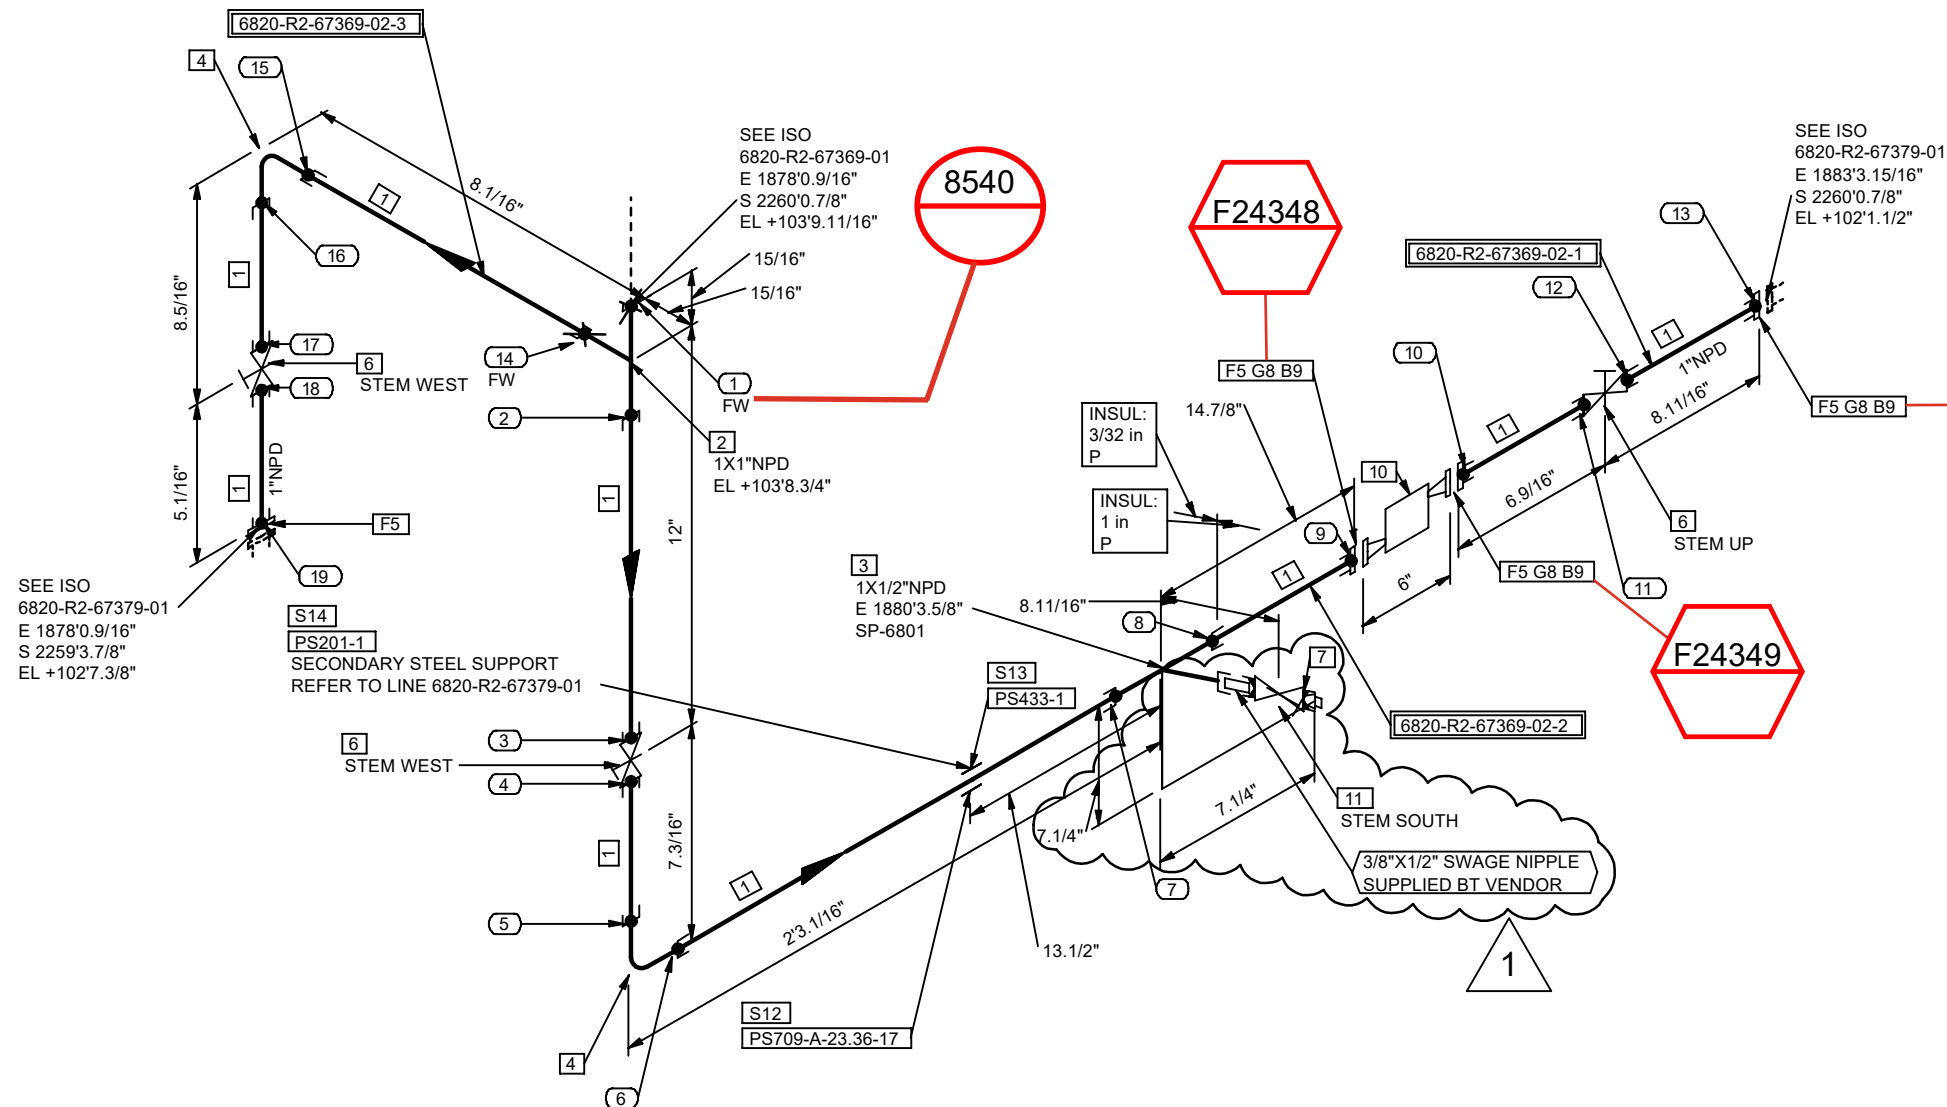

Filler Material Requisition
Date: 4-3-25
Line Class: SCXL-CS01
WPS: 10245
Electrode: ER70S-2
Signature: *Glenn Sumrall Jr*

COORDINATE SYSTEM : PLANTCOORDINATES

- NOTES:
- FOR LINE PRESSURES, TEMPERATURES, INSULATION TYPE AND THICKNESS, ETC. REFER TO LATEST REVISION OF LDT.
 - FOR STANDARD PIPE SUPPORT DETAILS SEE PROJECT STANDARD.
 - FIELD SHIM TO SUIT UNLESS OTHERWISE NOTED.
 - FOR PWHT REQUIREMENTS REFER TO LINE CLASS SPECIFICATION.
 - ALL THREADED PIPE LINE SYSTEMS, FIELD SHALL VERIFY DIMENSION PRIOR TO ERECTION.
 - FFW DESIGNATION AT WELDS INDICATES FIELD FIT WELD, WHERE PIPE FABRICATOR IS TO ADD 9 INCH OF PIPE TO THE ISOMETRIC DIMENSION TO ENABLE THE FIELD TO CUT TO FIT AT SITE.
 - REFER TO 202998C-000-W1-1300-0001 FOR FRP AND DUAL-LAM FABRICATION.

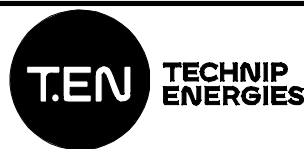

Information contained in this document is the work product of one or more legal entities of Technip Energies N.V. and embodies confidential and proprietary information of the applicable entity and/or its client. Use of this information is restricted in accordance with conditions specified by the contract. Technip Energies N.V. and its affiliates disclaim any and all liabilities for any changes or modifications to this document which are made by any person other than the entity that issued the document under the applicable client contract.

THIS DOCUMENT IS UNCONTROLLED WHEN REPRODUCED

REV	DATE	BY	DESCRIPTION	CHKD	MTO	STRESS	APRVD
1	2025-03-28	RVA	ISSUED FOR CONSTRUCTION	SAD	KJK	SMR	GR
0	2025-02-28	RVA	ISSUED FOR CONSTRUCTION	SAD	KJK	SMR	GR

SERVICE: R2	VAPOR/LIQUID: V	INSUL TYPE: Per LDT	INSUL THK: Per LDT	SHOP: Y	FIELD: Y	PAINT CODE: Per LDT	MODULE: -
P&ID: 202998C-001-PID-0021-0335				UNIT#: 6800	SWP AREA: 6820	SPEC: SCXL-CS01	STRESS CALC #: -
LINE No. 1"-R2-67369-SCXL-CS01-P				DRAWING NUMBER 6820-R2-67369-02			REV. 1

OxyChem Redstone Battleground PROJECT

SHOP MATERIALS

NO	NPD	DESCRIPTION	IDENT	QTY
1	1	Pipes, Seamless, ASME B36.10, ASTM A106 Gr.B, PE, -, -, S-XS	CPP0AMKL	6.6
2	1X1	Eq Te, ASME B16.11, ASTM A105N, 3000 Lbs, SW Ends, -,	CDF6FZ11	1
3	1X1/2	SP-6801	SP-6801	1
4	1	90° Elb, ASME B16.11, ASTM A105N, 3000 Lbs, SW Ends, -,	CDF66G5D	2
5	1	SW Flg, ASME B16.5, ASTM A105N, 150 Lbs, RF/SW End, -, x S-XS	CFG70G8J	4
6	1	Gat Fem, API 602, ASTM A105N, 800 Lbs, SW Ends, HO, -, Valve Tag: GA-0126	C76SPABF	3

OTHER THAN SHOP MATERIALS

NO	NPD	DESCRIPTION	IDENT	QTY
7	1/2	Plug, Solid Round Head Type, ASME B16.11, ASTM A105N, NPTM End, -,	CBBPLK2	1
8	1	NM Flat Gk, Barium Sulfate filled PTFE, 150 Lbs, RF as per ASME B16.5, Full Face, Thk=1/8in, -,	C7CT1ZFH	3
9	1/2	SBlT 2 HHx N, A193 Gr.B7/A194 Gr.2H, -, Xylan PTFE Coated, - 2.75 in. Length	C6S4K87U	12
10	1	SP-6802	SP-6802	1
11	1/2	Gat Fem, API 602, ASTM A105N, 800 Lbs, NPTF Ends, HO, -, Valve Tag: GA-0120	C76SPABT	1

PIPE SUPPORTS

12	1	PS709-A-23.36-17	PS709	1
13	1	PS433-1	PS433	1
14	1	PS201-1	PS201	1

PIECE MARKS

6820-R2-67369-02-1 6820-R2-67369-02-2 6820-R2-67369-02-3

