


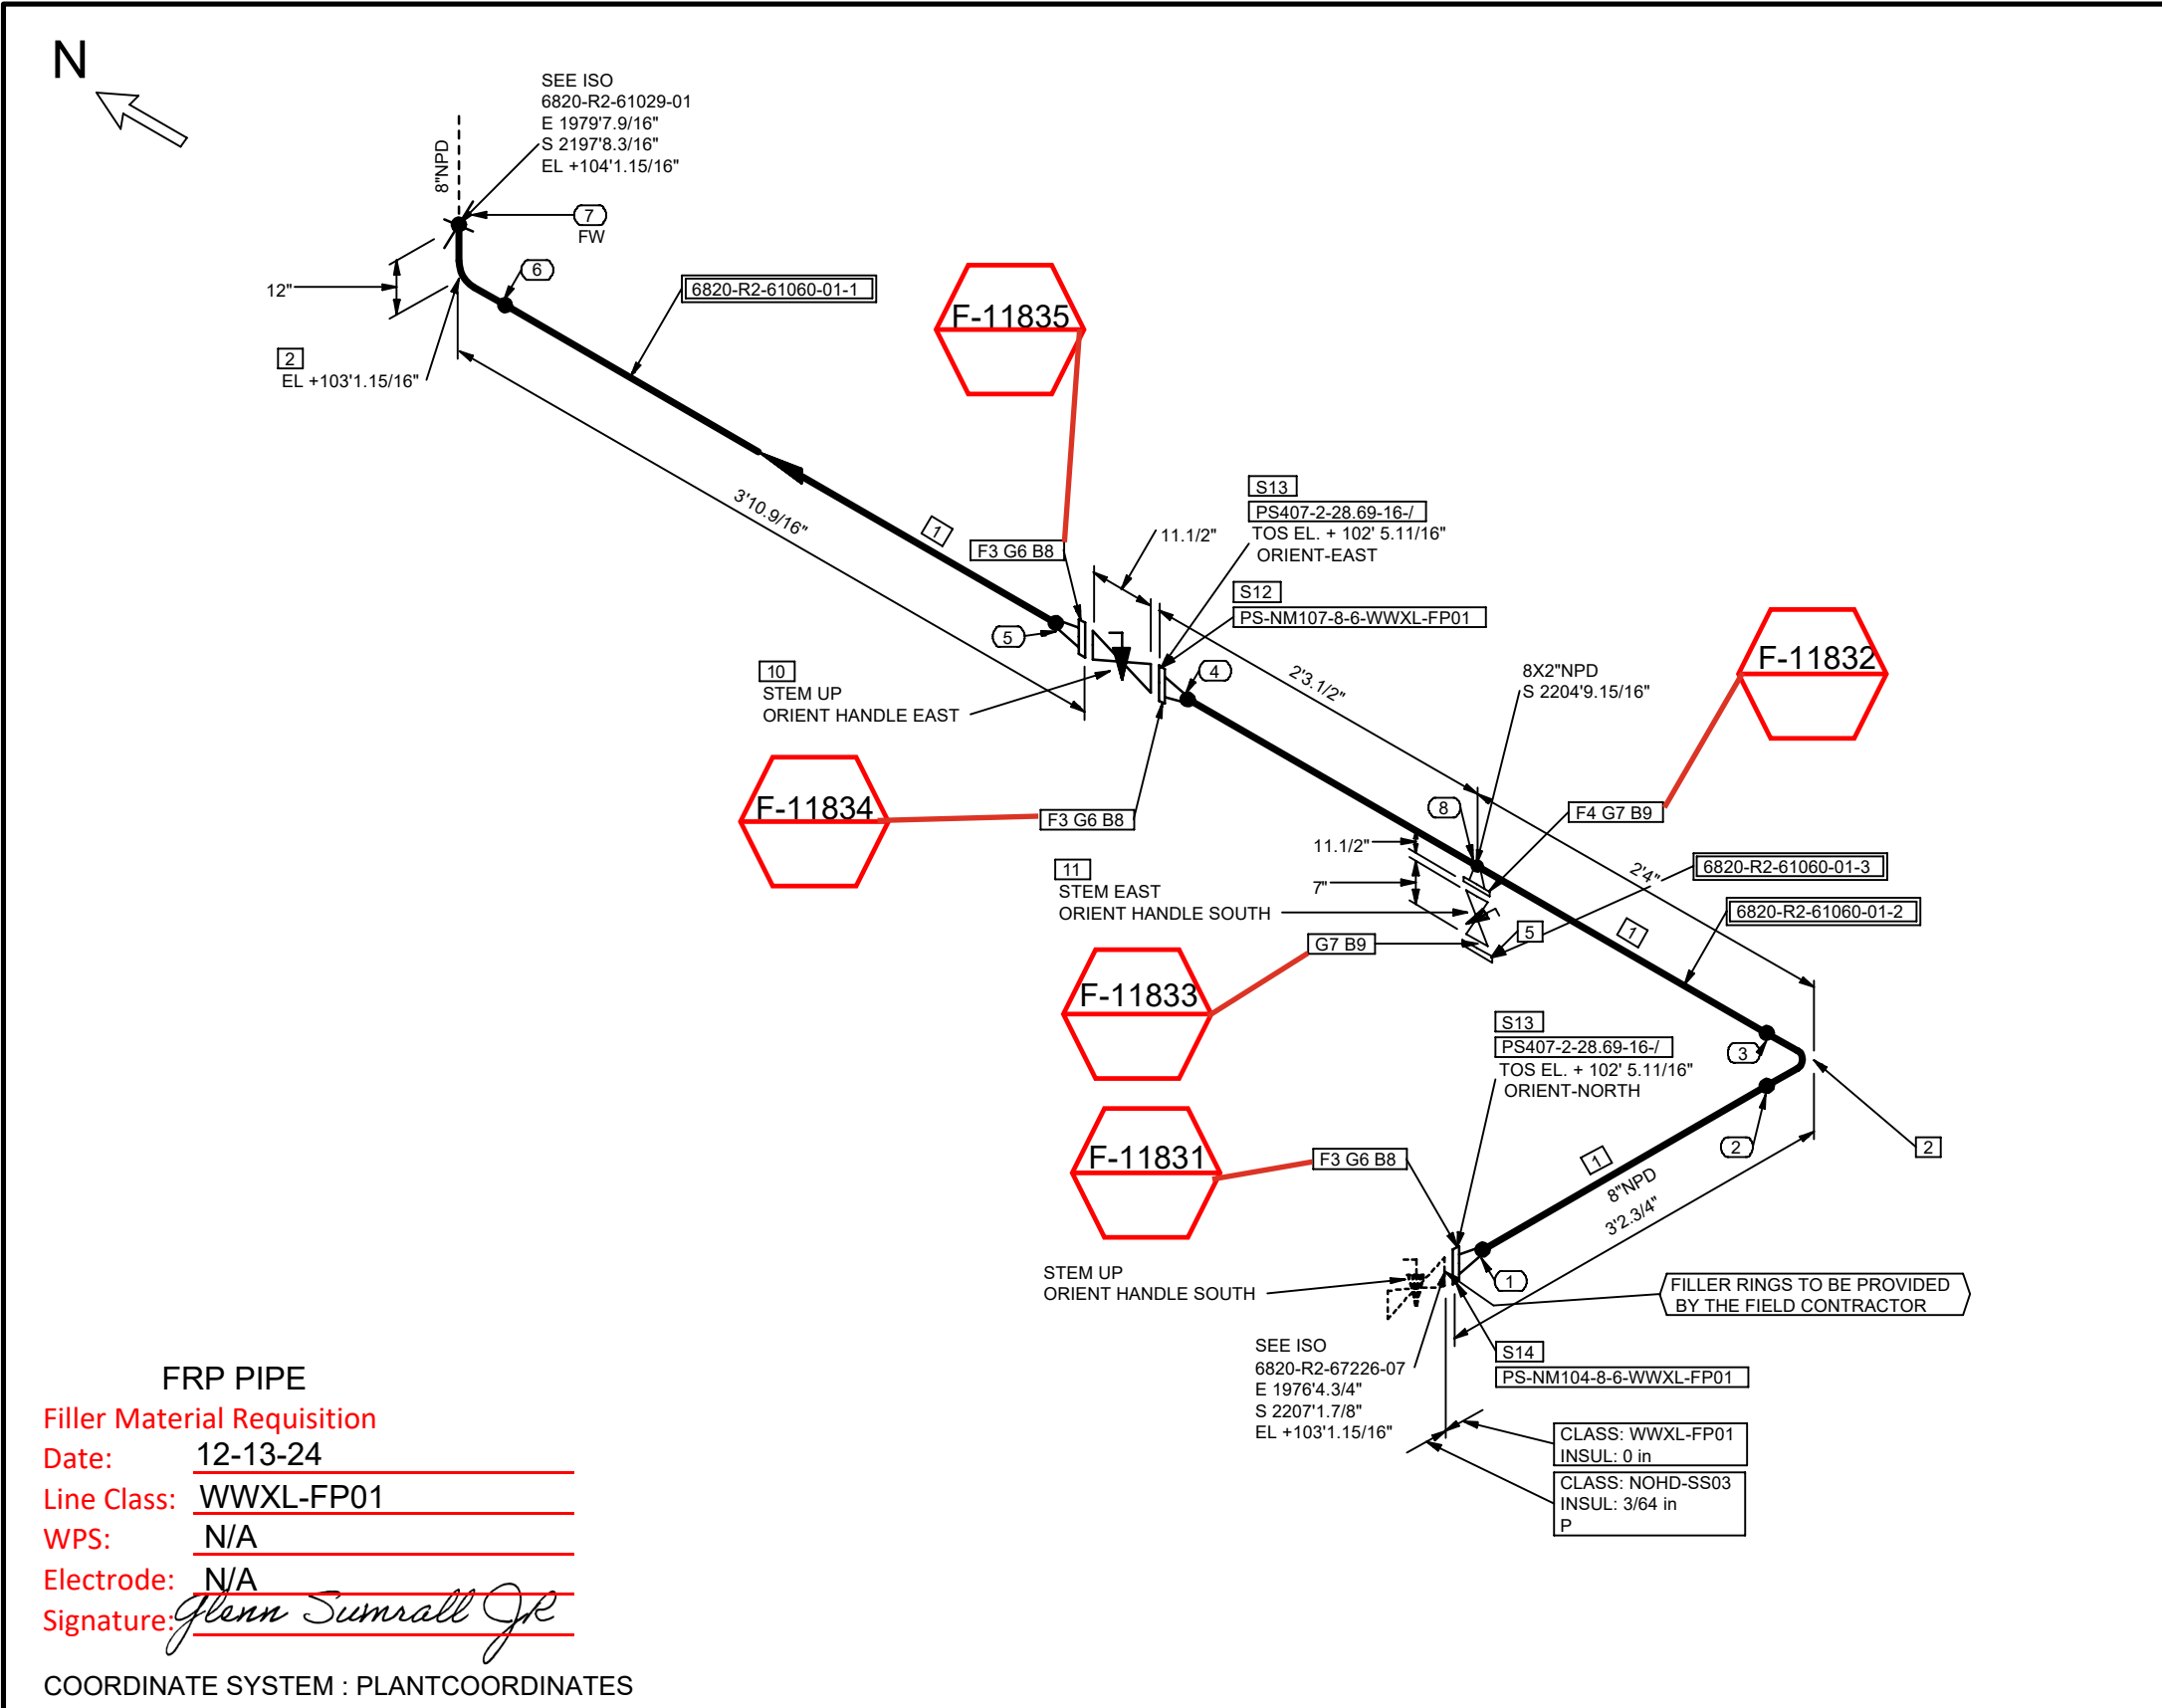

SHOP MATERIALS				
NO	NPD	DESCRIPTION	IDENT	QTY
1	8	Pipes, -, Prj Std, FRP, PE, -, -, .592"	C8GYAA87	5.9
2	8	90° Elb LR, Prj Std, FRP, PE, Prj Std, -, .592"	C8GYATLX	2
3	8	Neck Flg, ASTM D5421, FRP, 150 PSI, FF/PE - Butt & Wrap Type, -, .592"	C8M6VYS2	3
4	2	Neck Flg, ASTM D5421, FRP, 150 PSI, FF/PE - Butt & Wrap Type, -, .321"	C8M6VY24	1
5	2	Bld Flg, ASTM D5421, FRP, 150 PSI, FF, -,	C8JWWH94	1
OTHER THAN SHOP MATERIALS				
NO	NPD	DESCRIPTION	IDENT	QTY
6	8	NM Flat Gk, EPDM, 150 Lbs, FF as per ASME B16.5, Full Face, Thk=1/8in, -,	C7V61SEE	3
7	2	NM Flat Gk, EPDM, 150 Lbs, FF as per ASME B16.5, Full Face, Thk=1/8in, -,	C7V61SE4	2
8	3/4	SBlt 2 HHx N&2W, A193 Gr.B7/A194 Gr.2H, -, Xylan PTFE Coated, Typ B wsh, - 6 in. Length	C7CT0CKJ	24
9	5/8	SBlt 2 HHx N&2W, A193 Gr.B7/A194 Gr.2H, -, Xylan PTFE Coated, Typ B wsh, - 4.75 in. Length	C7CT0CGV	8
10	8	Plug Flg,SP, Inverted Tapered Plug, Non Lubricated, API 599, ASTM A395 Gr.60-40-18 PFA Lined, 150 Lbs, RF, Ends as per ASME B16.5, -, GO,-, -, Valve Tag: PL-0618	C6SWL10L	1
11	2	Plug Flg,SP, Inverted Tapered Plug, Non Lubricated, API 599, ASTM A395 Gr.60-40-18 PFA Lined, 150 Lbs, RF, Ends as per ASME B16.5, -, LO,-, -, Valve Tag: PL-0618	C6SWL10P	1
PIPE SUPPORTS				
12	8	PS-NM107-8-6-WWXL-FP01	PS-NM107	1
13	8	PS407-2-28.69-16-/-	PS407	2
14	8	PS-NM104-8-6-WWXL-FP01	PS-NM104	1
PIECE MARKS				
6820-R2-61060-01-1 6820-R2-61060-01-2 6820-R2-61060-01-3				

NOTES:

1. FOR LINE PRESSURES, TEMPERATURES, INSULATION TYPE AND THICKNESS, ETC. REFER TO LATEST REVISION OF LDT.

2. FOR STANDARD PIPE SUPPORT DETAILS SEE PROJECT STANDARD.

3. FIELD SHIM TO SUIT UNLESS OTHERWISE NOTED.

4. FOR PWHT REQUIREMENTS REFER TO LINE CLASS SPECIFICATION.

5. ALL THREADED PIPE LINE SYSTEMS, FIELD SHALL VERIFY DIMENSION PRIOR TO ERECTION.

6. FFW DESIGNATION AT WELDS INDICATES FIELD FIT WELD, WHERE PIPE FABRICATOR IS TO ADD 9 INCH OF PIPE TO THE ISOMETRIC DIMENSION TO ENABLE THE FIELD TO CUT TO FIT AT SITE.

7. REFER TO 202998C-000-W1-1300-0001 FOR FRP AND DUAL-LAM FABRICATION.

T.EN

TECHNIP ENERGIES

Information contained in this document is the work product of one or more legal entities of Technip Energies N.V. and embodies confidential and proprietary information of the applicable entity and/or its client. Use of this information is restricted in accordance with conditions specified by the contract. Technip Energies N.V. and its affiliates disclaim any and all liabilities for any changes or modifications to this document which are made by any person other than the entity that issued the document under the applicable client contract.

THIS DOCUMENT IS UNCONTROLLED WHEN REPRODUCED

0	2024-12-06	RVA	ISSUED FOR CONSTRUCTION	SAD	KJK	SMR	GR
REV	DATE	BY	DESCRIPTION	CHKD	MTO	STRESS	APRVD

SERVICE: R2

VAPOR/LIQUID: L

INSUL TYPE: Per LDT

INSUL THK: Per LDT

SHOP: Y

FIELD: Y

PAINT CODE: Per LDT

MODULE: -

P&ID: 202998C-001-PID-0021-0305

UNIT#: 6800

EWPA AREA: 6820

SPEC: WWXL-FP01

STRESS CALC #: CN-0255

LINE No: 8"-R2-61060-WWXL-FP01-N

DRAWING NUMBER: 6820-R2-61060-01

REV: 0

OxyChem Redstone Battleground PROJECT