


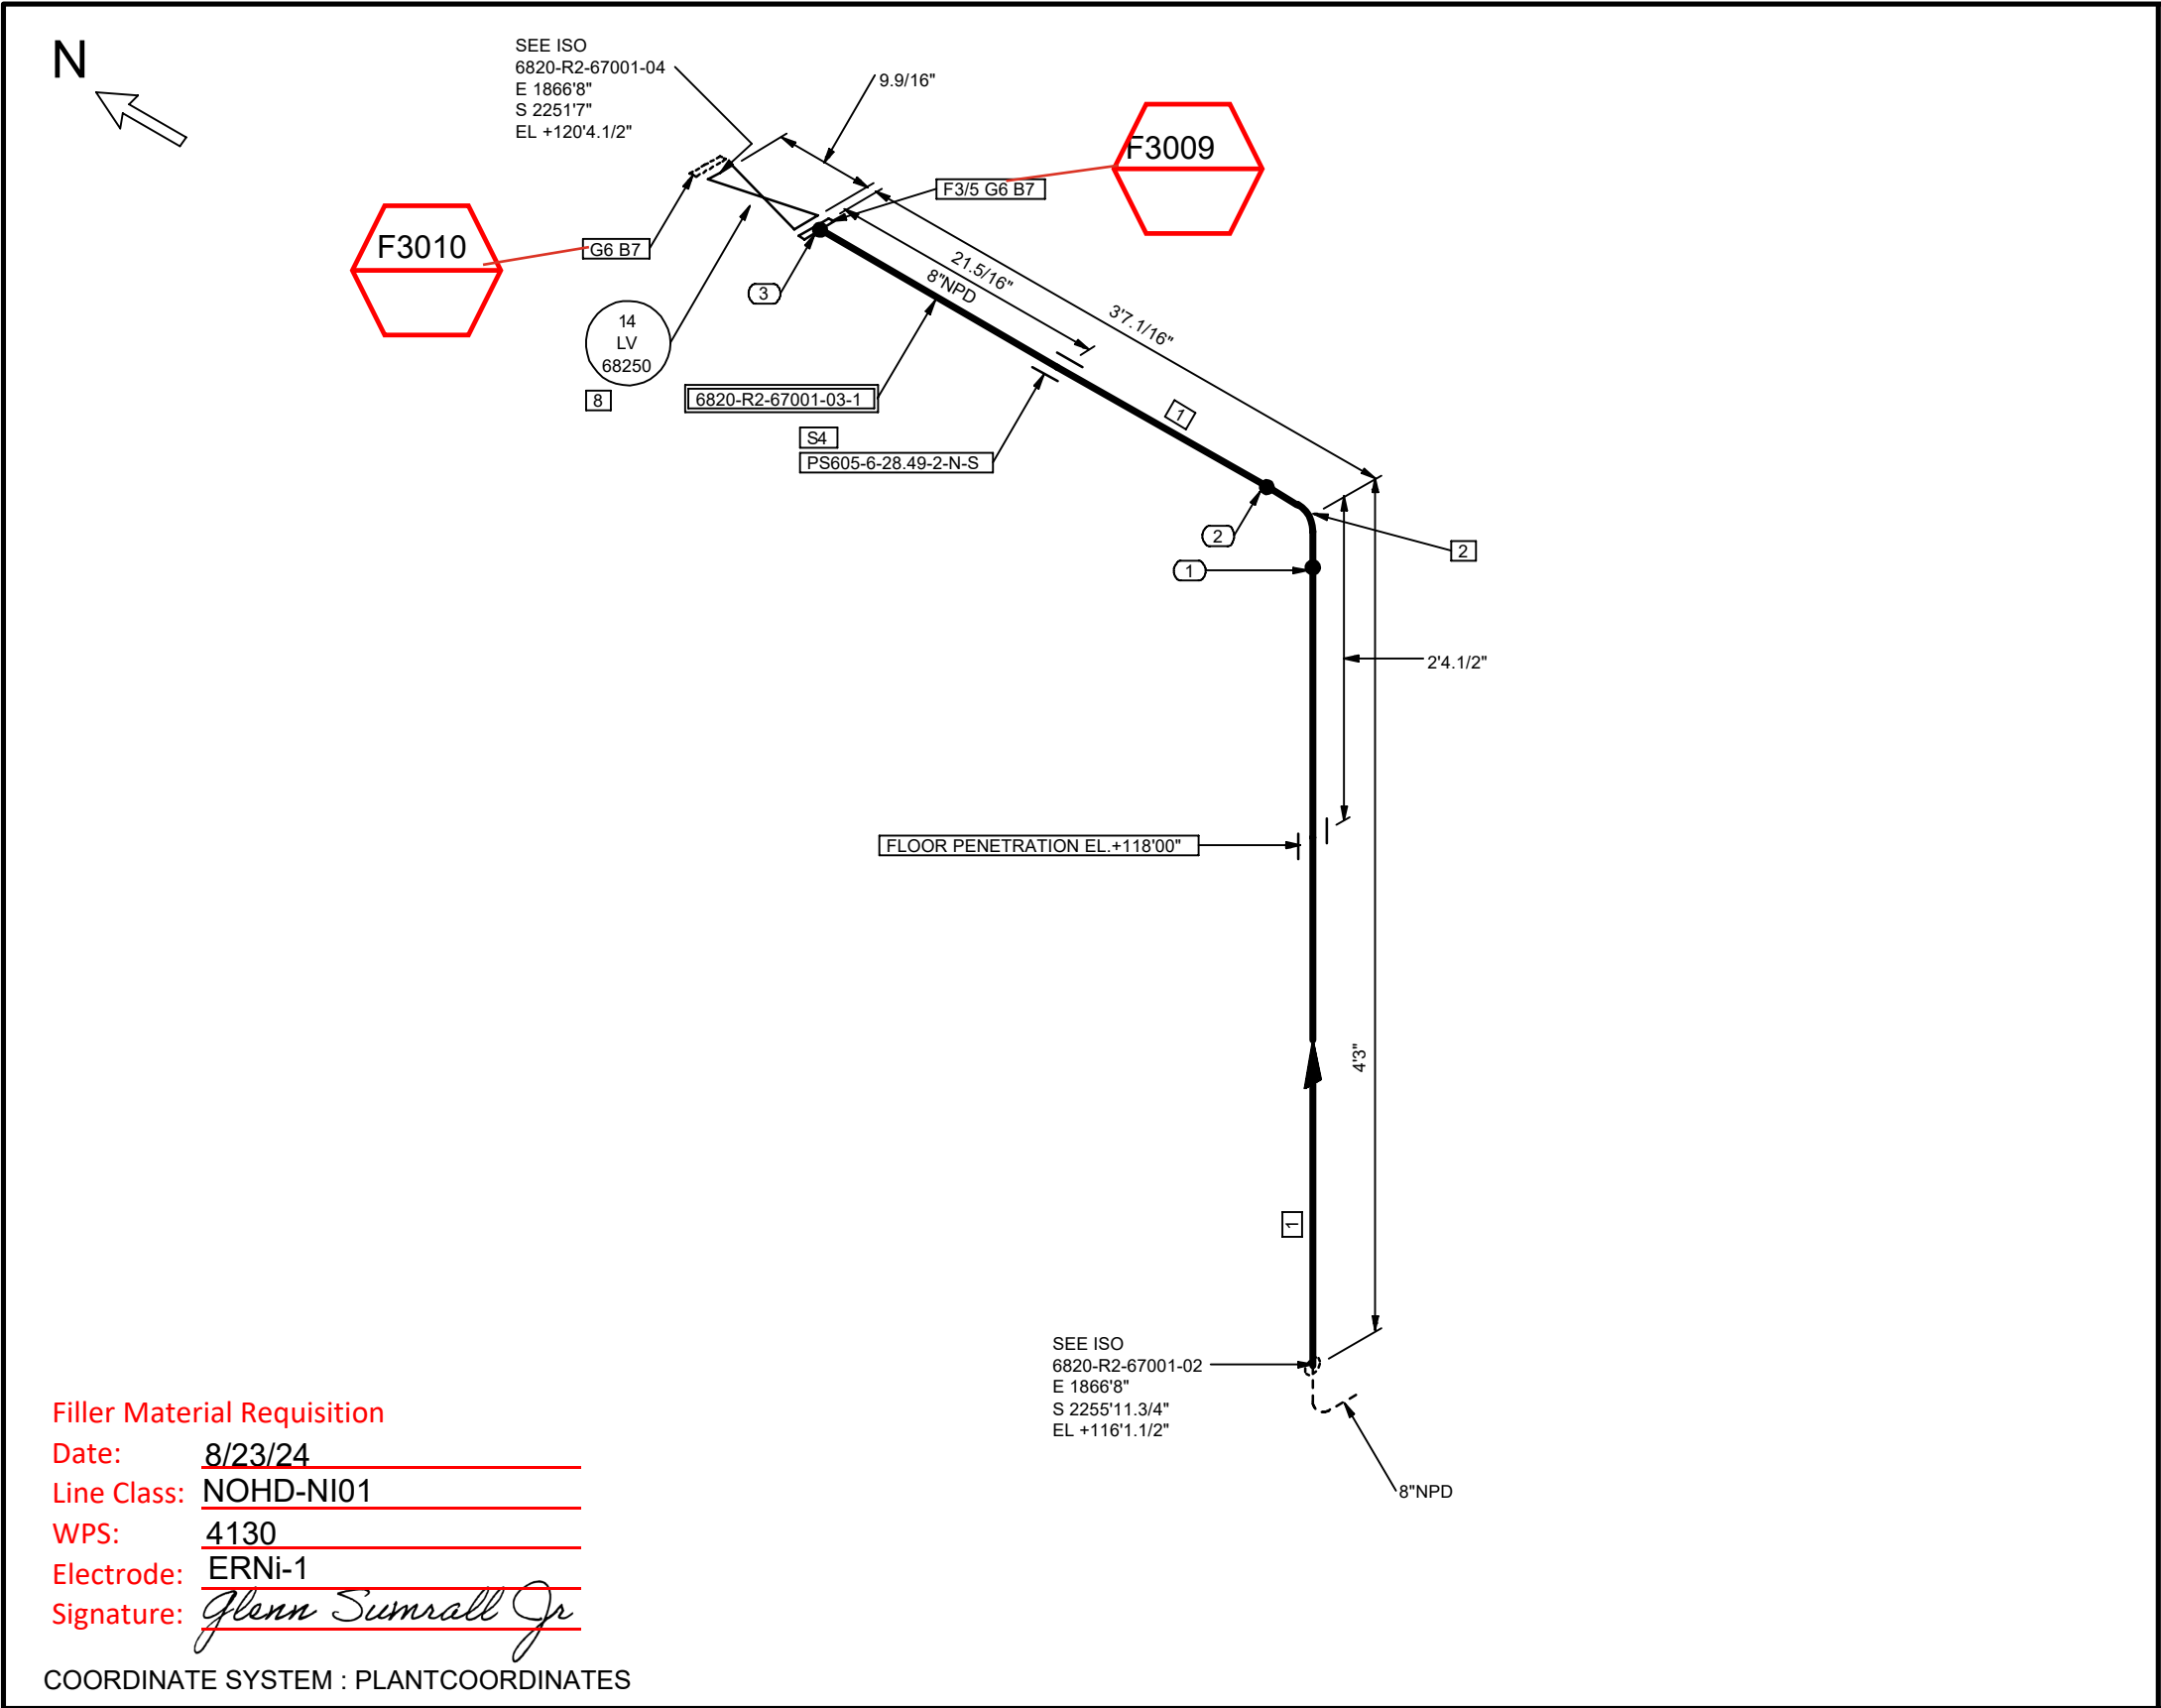

Filler Material Requisition
Date: 8/23/24
Line Class: NOHD-NI01
WPS: 4130
Electrode: ERNi-1
Signature: Glenn Sumrall Jr

SHOP MATERIALS				
NO	NPD	DESCRIPTION	IDENT	QTY
1	8	Pipes, EFW, ASME B36.19/B36.10, ASTM B725 UNS N02200 annealed, BE, -, -, S-10S	C7ZWWML7	5.6
2	8	90° Elb LR, Seamless, ASME B16.9, ASTM B366 Gr.WPN, BW Ends, -,Annealed, S-10S	C7ZWX04P	1
3	8	LJ Flg, ASME B16.5, ASTM A105 Galv. as per ASTM A153, 150 Lbs, FF, -,	C26WFFFR	1
PIPE SUPPORTS				
4	8	PS605-6-28.49-2-N-S	PS605	1
MISCELLANEOUS COMPONENTS				
5	8	Stub SP, Seamless, ASME B16.9, ASTM B366 Gr.WPN, BW Ends, -,Annealed, x S-10S	C8A5GY48	1
OTHER THAN SHOP MATERIALS				
NO	NPD	DESCRIPTION	IDENT	QTY
6	8	NM Flat Gk, Barium Sulfate filled PTFE, 150 Lbs, RF as per ASME B16.5, -, Thk=1/8in, -,	C6SBWZF4	2
7	3/4	SBlt 2 HHx N, A193 Gr.B7/A194 Gr.2H, -, Xylan PTFE Coated, - 4.5 in. Length	C6S4K8BD	16
INSTRUMENTS				
8	8	14-LV-68250	14-LV-68250	1
PIECE MARKS				
6820-R2-67001-03-1				

NOTES: 1. FOR LINE PRESSURES, TEMPERATURES, INSULATION TYPE AND THICKNESS, ETC. REFER TO LATEST REVISION OF LDT. 2. FOR STANDARD PIPE SUPPORT DETAILS SEE PROJECT STANDARD. 3. FIELD SHIM TO SUIT UNLESS OTHERWISE NOTED. 4. FOR PWHT REQUIREMENTS REFER TO LINE CLASS SPECIFICATION. 5. ALL THREADED PIPE LINE SYSTEMS, FIELD SHALL VERIFY DIMENSION PRIOR TO ERECTION. 6. FFW DESIGNATION AT WELDS INDICATES FIELD FIT WELD, WHERE PIPE FABRICATOR IS TO ADD 9 INCH OF PIPE TO THE ISOMETRIC DIMENSION TO ENABLE THE FIELD TO CUT TO FIT AT SITE. 7. REFER TO 202998C-000-W1-1300-0001 FOR FRP AND DUAL-LAM FABRICATION.		T.E.N TECHNIP ENERGIES Information contained in this document is the work product of one or more legal entities of Technip Energies N.V. and embodies confidential and proprietary information of the applicable entity and/or its client. Use of this information is restricted in accordance with conditions specified by the contract. Technip Energies N.V. and its affiliates disclaim any and all liabilities for any changes or modifications to this document which are made by any person other than the entity that issued the document under the applicable client contract. THIS DOCUMENT IS UNCONTROLLED WHEN REPRODUCED		<table><tr><td></td><td></td><td></td><td></td><td></td><td></td><td></td><td></td></tr><tr><td></td><td></td><td></td><td></td><td></td><td></td><td></td><td></td></tr><tr><td></td><td></td><td></td><td></td><td></td><td></td><td></td><td></td></tr><tr><td></td><td></td><td></td><td></td><td></td><td></td><td></td><td></td></tr><tr><td></td><td></td><td></td><td></td><td></td><td></td><td></td><td></td></tr><tr><td>0</td><td>2024-08-17</td><td>RVA</td><td>ISSUED FOR CONSTRUCTION</td><td>SAD</td><td>KJK</td><td>SMR</td><td>GR</td></tr><tr><td>REV</td><td>DATE</td><td>BY</td><td>DESCRIPTION</td><td>CHKD</td><td>MTO</td><td>STRESS</td><td>APRVD</td></tr></table>	0	2024-08-17	RVA	ISSUED FOR CONSTRUCTION	SAD	KJK	SMR	GR	REV	DATE	BY	DESCRIPTION	CHKD	MTO	STRESS	APRVD	<table><tr><td>SERVICE: R2</td><td>VAPOR/LIQUID: L</td><td>INSUL TYPE: Per LDT</td><td>INSUL THK: Per LDT</td><td>SHOP: Y</td><td>FIELD: Y</td><td>PAINT CODE: Per LDT</td><td>MODULE: -</td></tr><tr><td colspan="4"> OXY OxyChem Redstone Battleground PROJECT </td><td colspan="4"> P&ID: 202998C-001-PID-0021-0320 UNIT#: 6800 EWP AREA: 6820 SPEC: NOHD-NI01 STRESS CALC #: CN-0382 LINE No: 8"-R2-67001-NOHD-NI01-H DRAWING NUMBER 6820-R2-67001-03 REV. 0 </td></tr></table>				SERVICE: R2	VAPOR/LIQUID: L	INSUL TYPE: Per LDT	INSUL THK: Per LDT	SHOP: Y	FIELD: Y	PAINT CODE: Per LDT	MODULE: -	OXY OxyChem Redstone Battleground PROJECT				P&ID: 202998C-001-PID-0021-0320 UNIT#: 6800 EWP AREA: 6820 SPEC: NOHD-NI01 STRESS CALC #: CN-0382 LINE No: 8"-R2-67001-NOHD-NI01-H DRAWING NUMBER 6820-R2-67001-03 REV. 0			
0	2024-08-17	RVA	ISSUED FOR CONSTRUCTION	SAD	KJK	SMR	GR	
REV	DATE	BY	DESCRIPTION	CHKD	MTO	STRESS	APRVD	
SERVICE: R2	VAPOR/LIQUID: L	INSUL TYPE: Per LDT	INSUL THK: Per LDT	SHOP: Y	FIELD: Y	PAINT CODE: Per LDT	MODULE: -	
OXY OxyChem Redstone Battleground PROJECT				P&ID: 202998C-001-PID-0021-0320 UNIT#: 6800 EWP AREA: 6820 SPEC: NOHD-NI01 STRESS CALC #: CN-0382 LINE No: 8"-R2-67001-NOHD-NI01-H DRAWING NUMBER 6820-R2-67001-03 REV. 0	

