


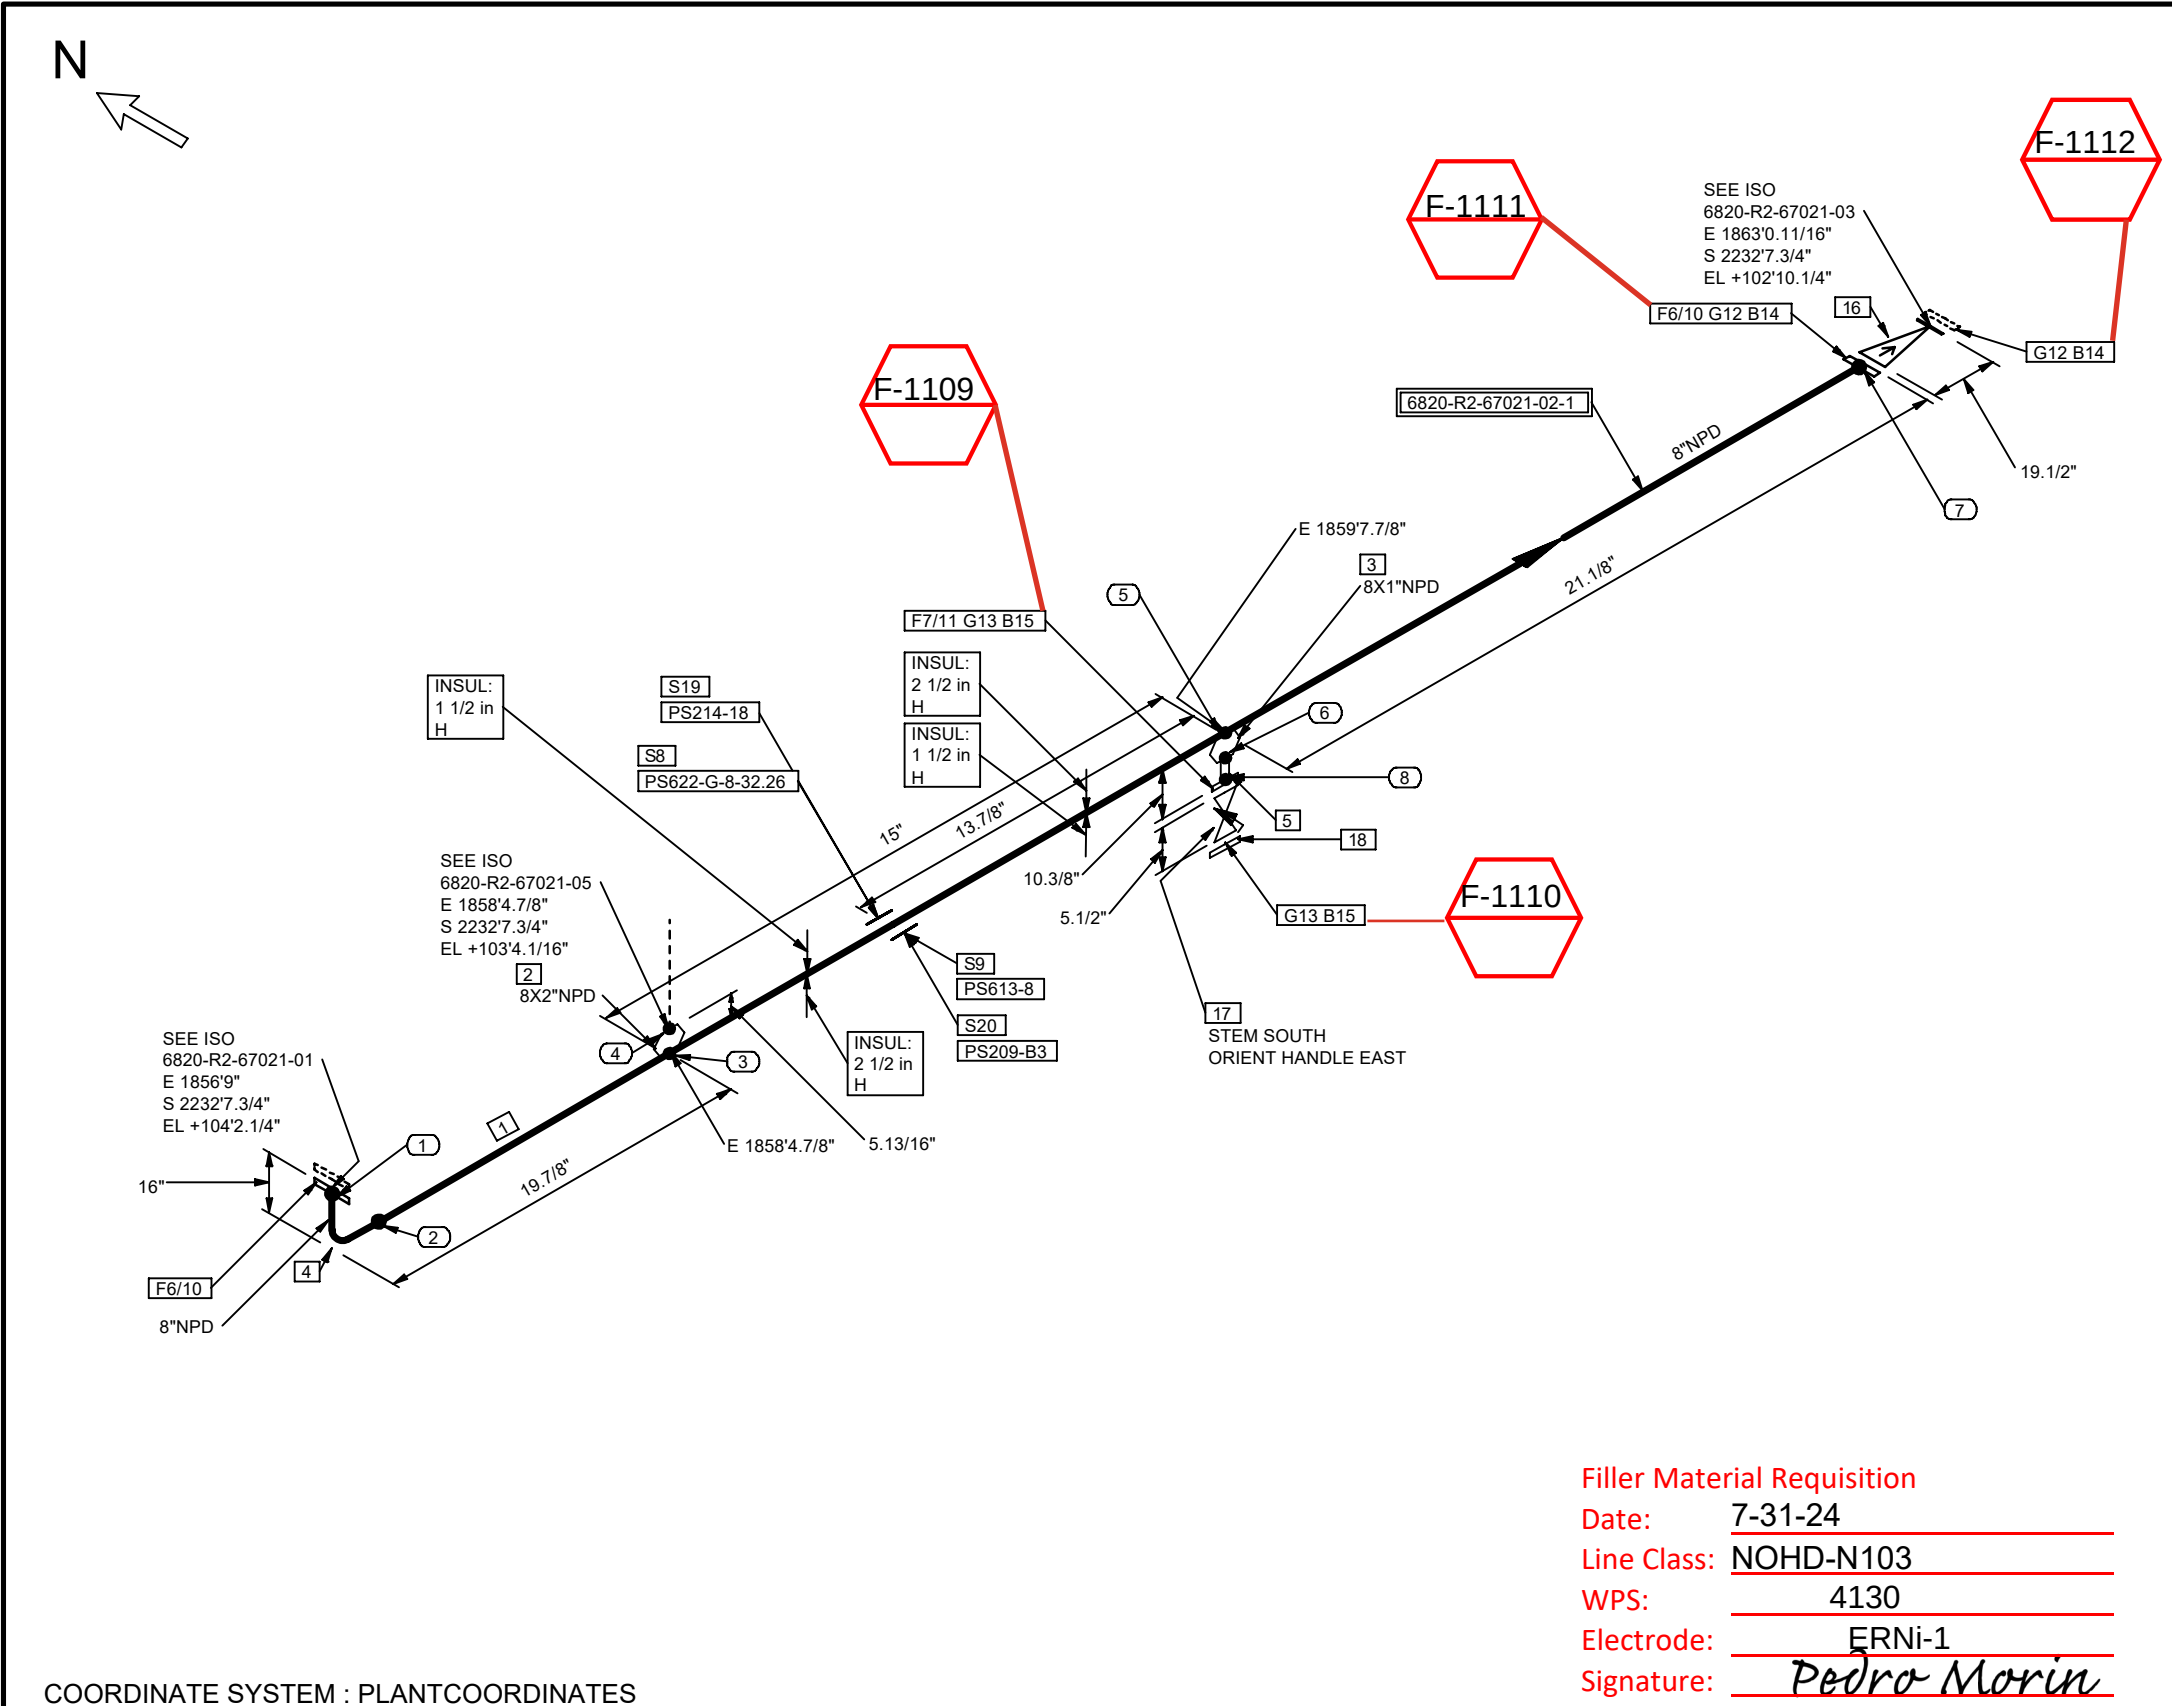

Filler Material Requisition
Date: 7-31-24
Line Class: NOHD-N103
WPS: 4130
Electrode: ERNi-1
Signature: Pedro Morin

SHOP MATERIALS				
NO	NPD	DESCRIPTION	IDENT	QTY
1	8	Pipes, EFW, ASME B36.19/B36.10, ASTM B725 UNS N02200 annealed, BE, -, -, S-10S	C7ZWWML7	3.4
2	8X2	Weldolet, MSS SP-97, ASTM B366 Gr.WPN, BW Ends, Annealed, S-10S	C7ZX07AS	1
3	8X1	Weldolet, MSS SP-97, ASTM B366 Gr.WPN, BW Ends, Annealed, S-10S	C7ZX02D9	1
4	8	90° Elb LR, Seamless, ASME B16.9, ASTM B366 Gr.WPN, BW Ends, -, Annealed, S-10S	C7ZWX04P	1
5	1	Nipple, ASTM B161 UNS N02200, BE, L = 3in, -, S-10S	C7ZWWN3N	1
6	8	LJ Flg, ASME B16.5, ASTM A182 Gr.F316/316L, 150 Lbs, FF, -,	C15RCMM6	2
7	1	LJ Flg, ASME B16.5, ASTM A182 Gr.F316/316L, 150 Lbs, FF, -,	C15RCMLV	1
PIPE SUPPORTS				
8	8	PS622-G-8-32.26	PS622	1
9	8	PS613-8	PS613	1
MISCELLANEOUS COMPONENTS				
10	8	Stub SP, Seamless, ASME B16.9, ASTM B366 Gr.WPN, BW Ends, -, x S-10S	C98MYDV5	2
11	1	Stub SP, Seamless, ASME B16.9, ASTM B366 Gr.WPN, BW Ends, -, x S-10S	C98MYD7N	1
OTHER THAN SHOP MATERIALS				
NO	NPD	DESCRIPTION	IDENT	QTY
12	8	NM Flat Gk, Barium Sulfate filled PTFE, 150 Lbs, RF as per ASME B16.5, -, Thk=1/8in, -,	C6SBWZF4	2
13	1	NM Flat Gk, Barium Sulfate filled PTFE, 150 Lbs, RF as per ASME B16.5, -, Thk=1/8in, -,	C6S4K87F	2
14	3/4	SBlit 2 HHx N, A193 Gr.B7/A194 Gr.2H, -, Xylan PTFE Coated, - 4.75 in. Length	C6S4K8BE	16
15	1/2	SBlit 2 HHx N, A193 Gr.B7/A194 Gr.2H, -, Xylan PTFE Coated, - 2.75 in. Length	C6S4K87U	8
16	8	SwgChk Flg, ASME B16.34, ASTM A494 Gr.CZ100, 150 Lbs, RF, Ends as per ASME B16.5, -, Valve Tag: CH-0529	C8YJLYLU	1
17	1	Plug Flg, SP, Inverted Tapered Plug, Non Lubricated, API 599, ASTM B564 UNS N02200, 150 Lbs, RF, Ends as per ASME B16.5, -, LO, -, -, Valve Tag: PL-1194	C99ZZ9D2	1
18	1	Bld Flg, ASME B16.5, ASTM B564 UNS N02200, 150 Lbs, RF, -,	C7T63YAU	1
PIPE SUPPORTS				
19	8	PS214-18	PS214	1
20	8	PS209-B3	PS209	1
PIECE MARKS				
6820-R2-67021-02-1				
Turner Industries Group, LLC Received July 31, 2024 DOCUMENT CONTROL				
SERVICE: R2 VAPOR/LIQUID: L INSUL TYPE: Per LDT INSUL THK: Per LDT SHOP: Y FIELD: Y PAINT CODE: Per LDT MODULE: -				
P&ID: 202998C-001-PID-0021-0322				
UNIT#: 6800 EWP AREA: 6820 SPEC: NOHD-NI03 STRESS CALC #: CN-0388				
LINE No: 8"-R2-67021-NOHD-NI03-H				
DRAWING NUMBER 6820-R2-67021-02				REV. 0
OxyChem Redstone Battleground PROJECT				

NOTES:
1. FOR LINE PRESSURES, TEMPERATURES, INSULATION TYPE AND THICKNESS, ETC. REFER TO LATEST REVISION OF LDT.
2. FOR STANDARD PIPE SUPPORT DETAILS SEE PROJECT STANDARD.
3. FIELD SHIM TO SUIT UNLESS OTHERWISE NOTED.
4. FOR PWHT REQUIREMENTS REFER TO LINE CLASS SPECIFICATION.
5. ALL THREADED PIPE LINE SYSTEMS, FIELD SHALL VERIFY DIMENSION PRIOR TO ERECTION.
6. FFW DESIGNATION AT WELDS INDICATES FIELD FIT WELD, WHERE PIPE FABRICATOR IS TO ADD 9 INCH OF PIPE TO THE ISOMETRIC DIMENSION TO ENABLE THE FIELD TO CUT TO FIT AT SITE.
7. REFER TO 202998C-000-W1-1300-0001 FOR FRP AND DUAL-LAM FABRICATION.

T.EN

TECHNIP ENERGIES

Information contained in this document is the work product of one or more legal entities of Technip Energies N.V. and embodies confidential and proprietary information of the applicable entity and/or its client. Use of this information is restricted in accordance with conditions specified by the contract. Technip Energies N.V. and its affiliates disclaim any and all liabilities for any changes or modifications to this document which are made by any person other than the entity that issued the document under the applicable client contract.

THIS DOCUMENT IS UNCONTROLLED WHEN REPRODUCED

0	2024-07-18	RVA	ISSUED FOR CONSTRUCTION	SAD	KJK	BRD	GR
REV	DATE	BY	DESCRIPTION	CHKD	MTO	STRESS	APRVD

