


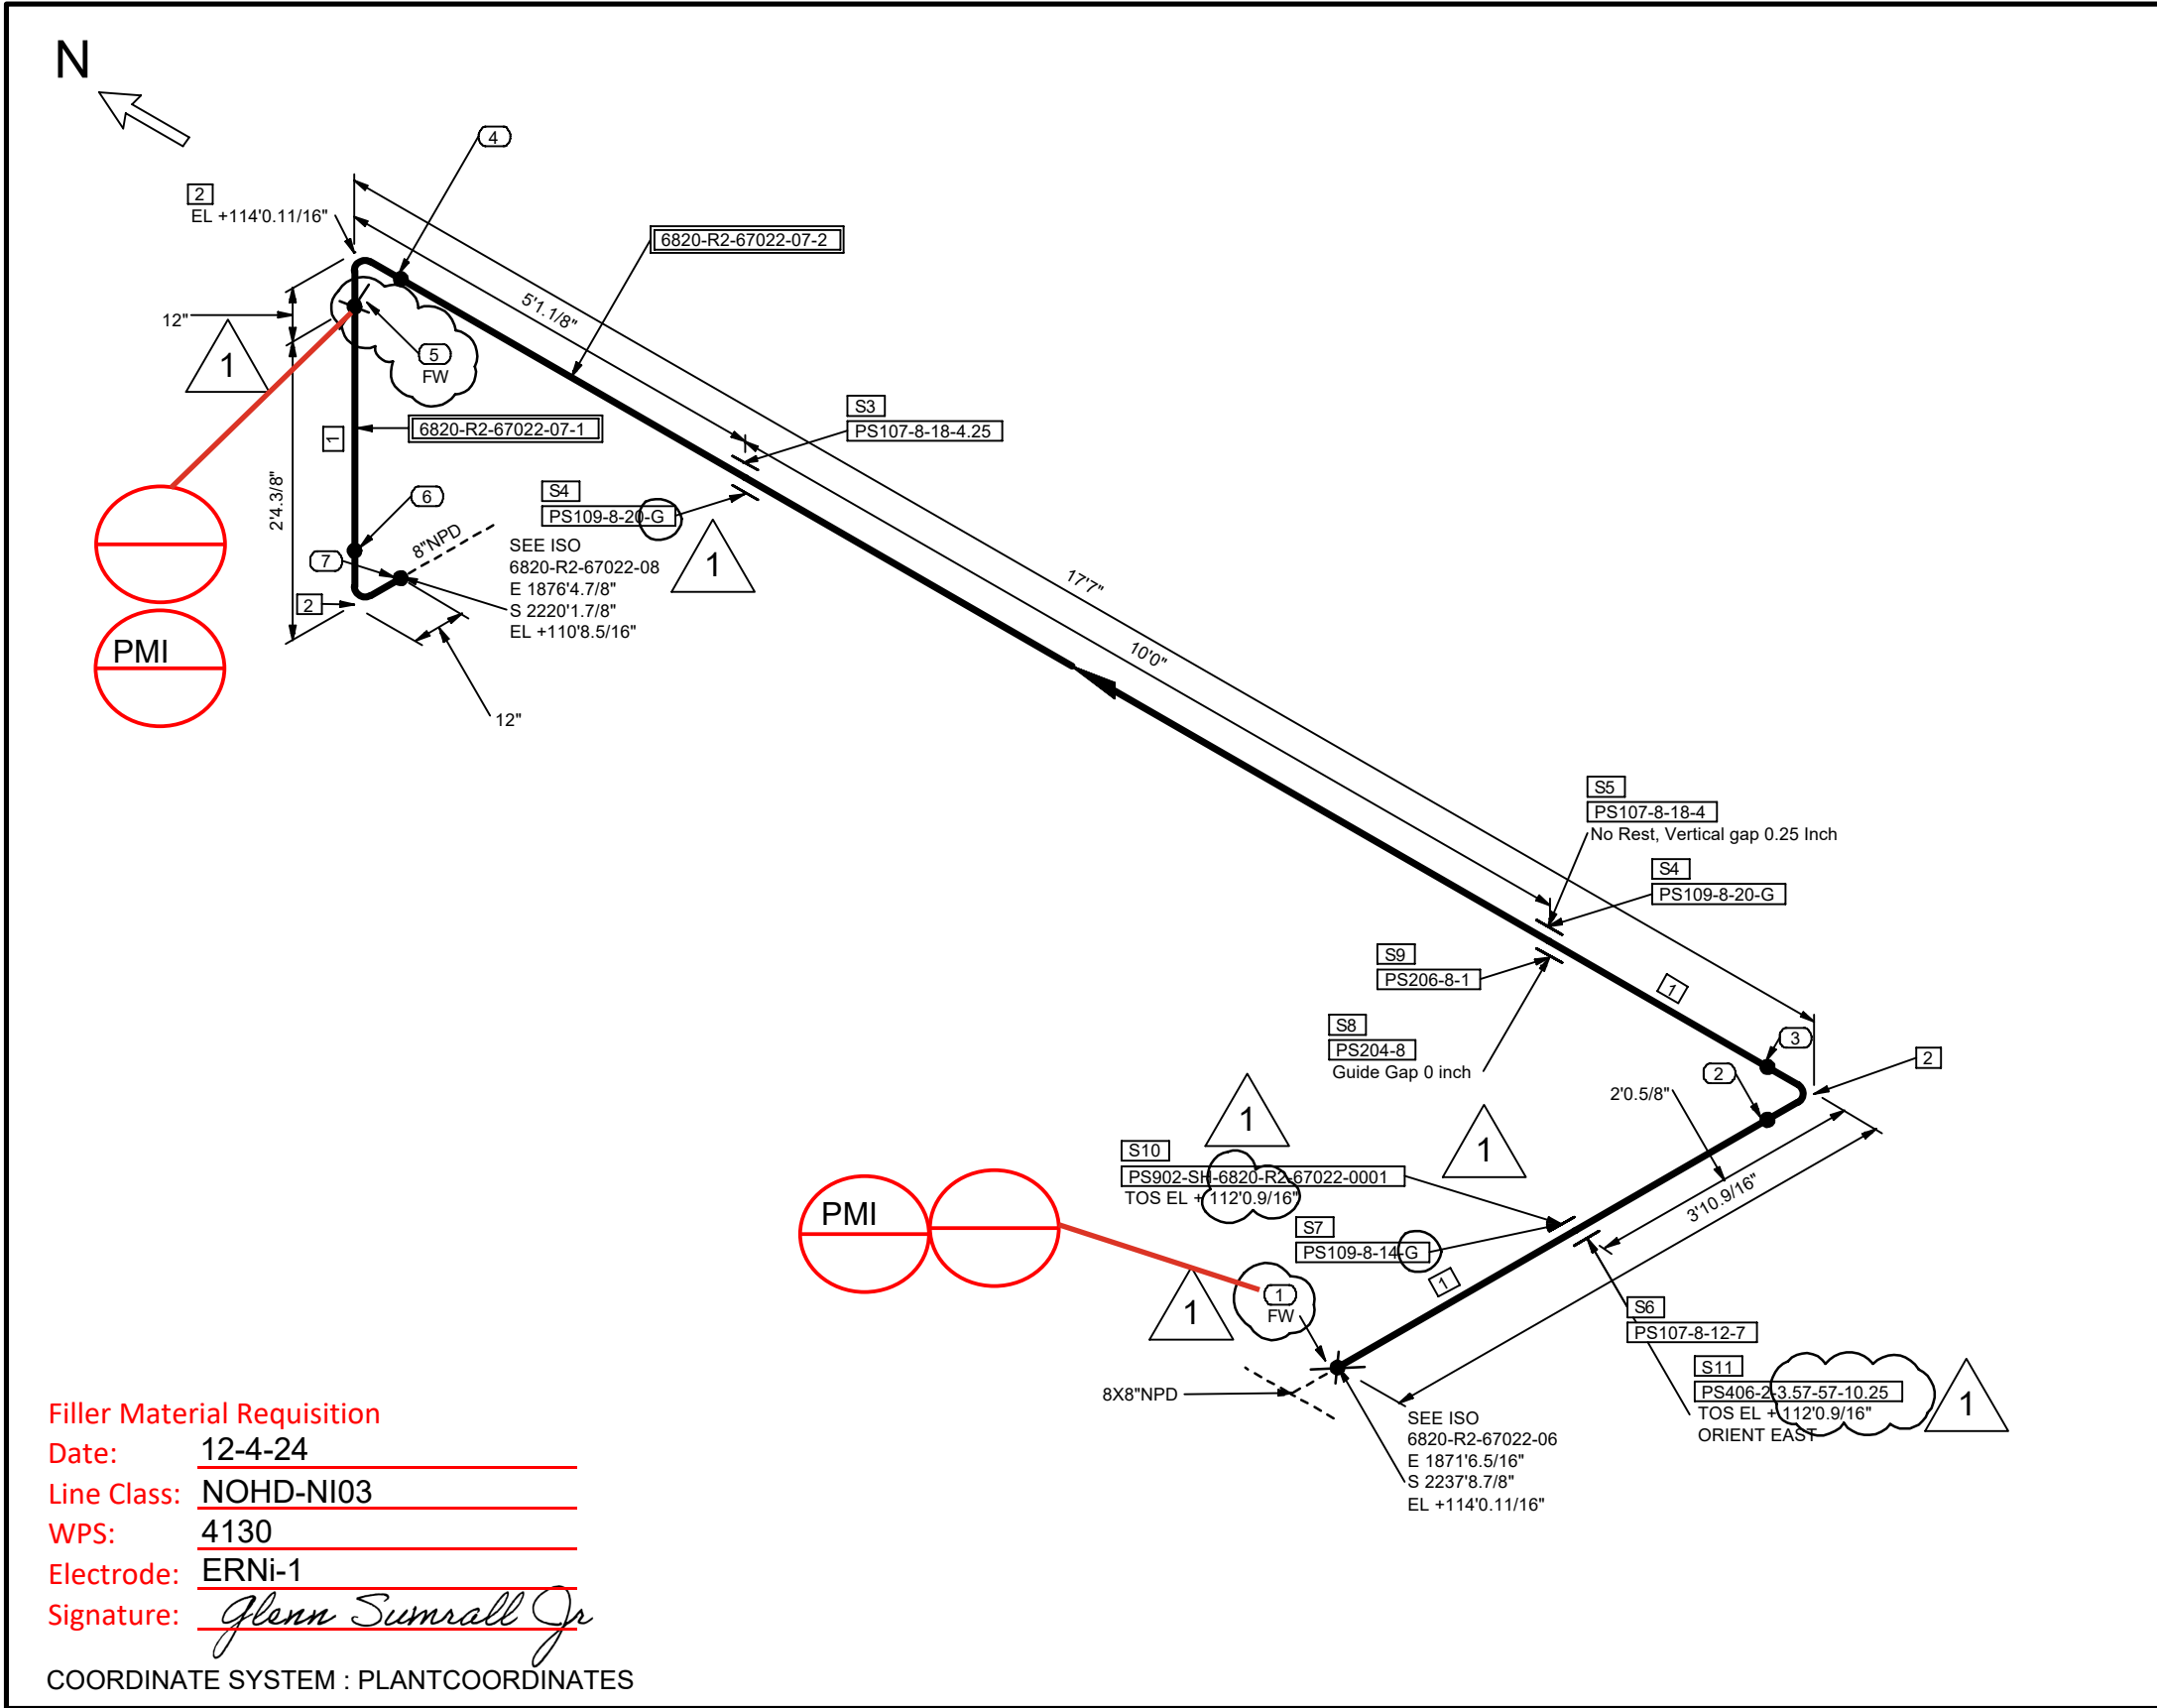

SHOP MATERIALS				
NO	NPD	DESCRIPTION	IDENT	QTY
1	8	Pipes, EFW, ASME B36.19/B36.10, ASTM B725 UNS N02200 annealed, BE, -, -, S-10S	C7ZWWML7	19.9
2	8	90° Elb LR, Seamless, ASME B16.9, ASTM B366 Gr.WPN, BW Ends, -,Annealed, S-10S	C7ZWX04P	3
PIPE SUPPORTS				
3	8	PS107-8-18-4.25	PS107	1
4	8	PS109-8-20-G	PS109	2
5	8	PS107-8-18-4	PS107	1
6	8	PS107-8-12-7	PS107	1
7	8	PS109-8-14-G	PS109	1
OTHER THAN SHOP MATERIALS				
NO	NPD	DESCRIPTION	IDENT	QTY
PIPE SUPPORTS				
8	8	PS204-8	PS204	1
9	8	PS206-8-1	PS206	1
10	8	PS902-SH-6820-R2-67022-0001	PS902	1
11	8	PS406-2-3.57-57-10.25	PS406	1
PIECE MARKS				
6820-R2-67022-07-1 6820-R2-67022-07-2				

NOTES: 1. FOR LINE PRESSURES, TEMPERATURES, INSULATION TYPE AND THICKNESS, ETC. REFER TO LATEST REVISION OF LDT. 2. FOR STANDARD PIPE SUPPORT DETAILS SEE PROJECT STANDARD. 3. FIELD SHIM TO SUIT UNLESS OTHERWISE NOTED. 4. FOR PWHT REQUIREMENTS REFER TO LINE CLASS SPECIFICATION. 5. ALL THREADED PIPE LINE SYSTEMS, FIELD SHALL VERIFY DIMENSION PRIOR TO ERECTION. 6. FFW DESIGNATION AT WELDS INDICATES FIELD FIT WELD, WHERE PIPE FABRICATOR IS TO ADD 9 INCH OF PIPE TO THE ISOMETRIC DIMENSION TO ENABLE THE FIELD TO CUT TO FIT AT SITE. 7. REFER TO 202998C-000-W1-1300-0001 FOR FRP AND DUAL-LAM FABRICATION.				T.E.N TECHNIP ENERGIES information contained in this document is the work product of one or more legal entities of Technip Energies N.V. and embodies confidential and proprietary information of the applicable entity and/or its client. Use of this information is restricted in accordance with conditions specified by the contract. Technip Energies N.V. and its affiliates disclaim any and all liabilities for any changes or modifications to this document which are made by any person other than the entity that issued the document under the applicable client contract. THIS DOCUMENT IS UNCONTROLLED WHEN REPRODUCED				<table><tr><td></td><td></td><td></td><td></td><td></td><td></td><td></td><td></td></tr><tr><td></td><td></td><td></td><td></td><td></td><td></td><td></td><td></td></tr><tr><td></td><td></td><td></td><td></td><td></td><td></td><td></td><td></td></tr><tr><td></td><td></td><td></td><td></td><td></td><td></td><td></td><td></td></tr><tr><td>1</td><td>2024-11-26</td><td>RVA</td><td>ISSUED FOR CONSTRUCTION</td><td>SAD</td><td>KJK</td><td>SMR</td><td>GR</td></tr><tr><td>0</td><td>2024-07-18</td><td>RVA</td><td>ISSUED FOR CONSTRUCTION</td><td>SAD</td><td>KJK</td><td>BRD</td><td>GR</td></tr><tr><td>REV</td><td>DATE</td><td>BY</td><td>DESCRIPTION</td><td>CHKD</td><td>MTO</td><td>STRESS</td><td>APRVD</td></tr></table>																																				1	2024-11-26	RVA	ISSUED FOR CONSTRUCTION	SAD	KJK	SMR	GR	0	2024-07-18	RVA	ISSUED FOR CONSTRUCTION	SAD	KJK	BRD	GR	REV	DATE	BY	DESCRIPTION	CHKD	MTO	STRESS	APRVD	<table><tr><td>SERVICE: R2</td><td>VAPOR/LIQUID: L</td><td>INSUL TYPE: Per LDT</td><td>INSUL THK: Per LDT</td><td>SHOP: Y</td><td>FIELD: Y</td><td>PAINT CODE: Per LDT</td><td>MODULE: -</td></tr><tr><td colspan="4" rowspan="4"> OXY OxyChem Redstone Battleground PROJECT </td><td colspan="4">P&ID: 202998C-001-PID-0021-0322</td></tr><tr><td>UNIT#: 6800</td><td>EWP AREA: 6820</td><td>SPEC: NOHD-NI03</td><td colspan="2">STRESS CALC #: CN-0388/0392</td></tr><tr><td colspan="4">LINE No: 8"-R2-67022-NOHD-NI03-H</td></tr><tr><td colspan="3">DRAWING NUMBER 6820-R2-67022-07</td><td>REV. 1</td></tr></table>				SERVICE: R2	VAPOR/LIQUID: L	INSUL TYPE: Per LDT	INSUL THK: Per LDT	SHOP: Y	FIELD: Y	PAINT CODE: Per LDT	MODULE: -	OXY OxyChem Redstone Battleground PROJECT				P&ID: 202998C-001-PID-0021-0322				UNIT#: 6800	EWP AREA: 6820	SPEC: NOHD-NI03	STRESS CALC #: CN-0388/0392		LINE No: 8"-R2-67022-NOHD-NI03-H				DRAWING NUMBER 6820-R2-67022-07			REV. 1
1	2024-11-26	RVA	ISSUED FOR CONSTRUCTION	SAD	KJK	SMR	GR	
0	2024-07-18	RVA	ISSUED FOR CONSTRUCTION	SAD	KJK	BRD	GR	
REV	DATE	BY	DESCRIPTION	CHKD	MTO	STRESS	APRVD	
SERVICE: R2	VAPOR/LIQUID: L	INSUL TYPE: Per LDT	INSUL THK: Per LDT	SHOP: Y	FIELD: Y	PAINT CODE: Per LDT	MODULE: -	
OXY OxyChem Redstone Battleground PROJECT				P&ID: 202998C-001-PID-0021-0322	
				UNIT#: 6800	EWP AREA: 6820	SPEC: NOHD-NI03	STRESS CALC #: CN-0388/0392	
				LINE No: 8"-R2-67022-NOHD-NI03-H	
				DRAWING NUMBER 6820-R2-67022-07			REV. 1	

