


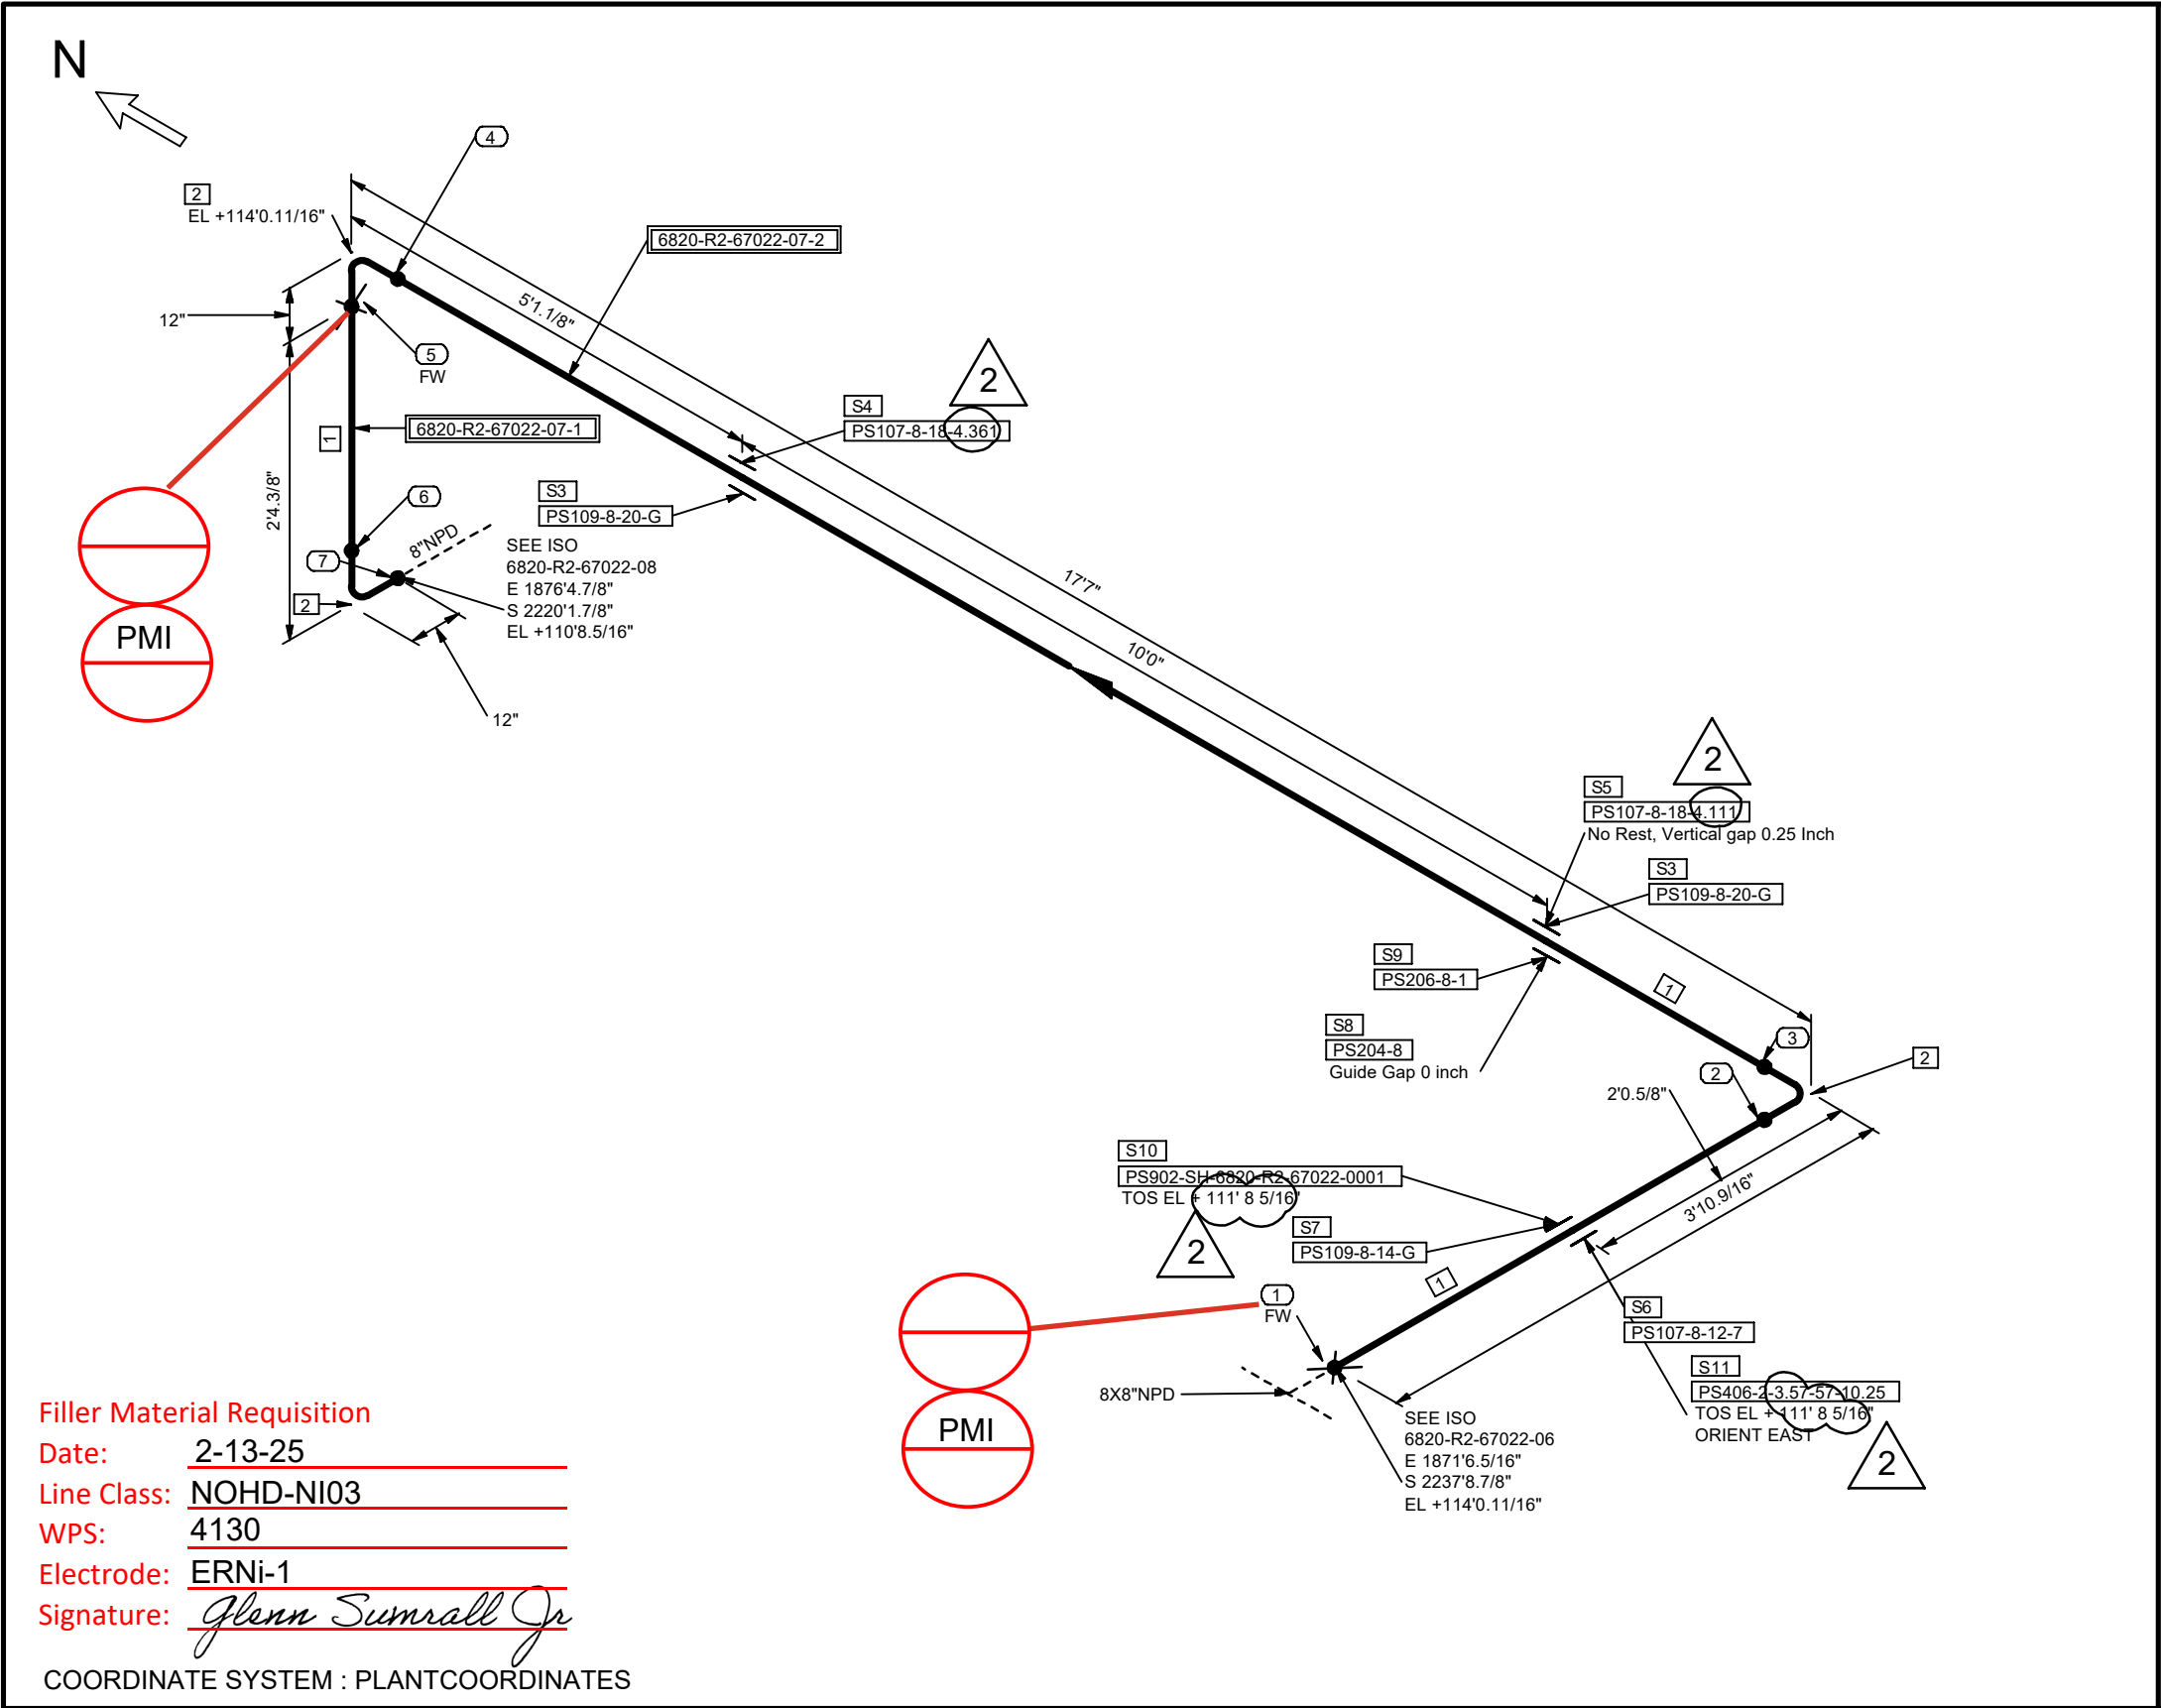

Filler Material Requisition
Date: 2-13-25
Line Class: NOHD-NI03
WPS: 4130
Electrode: ERNi-1
Signature: *Glenn Sumrall Jr*

COORDINATE SYSTEM : PLANTCOORDINATES

NOTES:

- FOR LINE PRESSURES, TEMPERATURES, INSULATION TYPE AND THICKNESS, ETC. REFER TO LATEST REVISION OF LDT.
- FOR STANDARD PIPE SUPPORT DETAILS SEE PROJECT STANDARD.
- FIELD SHIM TO SUIT UNLESS OTHERWISE NOTED.
- FOR PWHT REQUIREMENTS REFER TO LINE CLASS SPECIFICATION.
- ALL THREADED PIPE LINE SYSTEMS, FIELD SHALL VERIFY DIMENSION PRIOR TO ERECTION.
- FFW DESIGNATION AT WELDS INDICATES FIELD FIT WELD, WHERE PIPE FABRICATOR IS TO ADD 9 INCH OF PIPE TO THE ISOMETRIC DIMENSION TO ENABLE THE FIELD TO CUT TO FIT AT SITE.
- REFER TO 202998C-000-W1-1300-0001 FOR FRP AND DUAL-LAM FABRICATION.



TECHNIP
ENERGIES

Information contained in this document is the work product of one or more legal entities of Technip Energies N.V. and embodies confidential and proprietary information of the applicable entity and/or its client. Use of this information is restricted in accordance with conditions specified by the contract. Technip Energies N.V. and its affiliates disclaim any and all liabilities for any changes or modifications to this document which are made by any person other than the entity that issued the document under the applicable client contract.

THIS DOCUMENT IS UNCONTROLLED WHEN REPRODUCED

REV	DATE	BY	DESCRIPTION	CHKD	MTO	STRESS	APRVD
2	2025-01-31	RVA	ISSUED FOR CONSTRUCTION	SAD	KJK	SMR	GR
1	2024-11-24	RVA	ISSUED FOR CONSTRUCTION	SAD	KJK	SMR	GR
0	2024-07-18	RVA	ISSUED FOR CONSTRUCTION	SAD	KJK	BRD	GR

SHOP MATERIALS

NO	NPD	DESCRIPTION	IDENT	QTY
1	8	Pipes, EFW, ASME B36.19/B36.10, ASTM B725 UNS N02200 annealed, BE, -, -, S-10S	C7ZWWML7	19.9
2	8	90° Elb LR, Seamless, ASME B16.9, ASTM B366 Gr.WPN, BW Ends, -,Annealed, S-10S	C7ZWX04P	3

PIPE SUPPORTS

3	8	PS109-8-20-G	PS109	2
4	8	PS107-8-18-4.361	PS107	1
5	8	PS107-8-18-4.111	PS107	1
6	8	PS107-8-12-7	PS107	1
7	8	PS109-8-14-G	PS109	1

OTHER THAN SHOP MATERIALS

NO	NPD	DESCRIPTION	IDENT	QTY
8	8	PS204-8	PS204	1
9	8	PS206-8-1	PS206	1
10	8	PS902-SH-6820-R2-67022-0001	PS902	1
11	8	PS406-2-3.57-57-10.25	PS406	1

PIECE MARKS

6820-R2-67022-07-1 6820-R2-67022-07-2

Turner Industries Group, LLC
Received
FEBRUARY 13, 2025
DOCUMENT CONTROL



OxyChem Redstone Battleground
PROJECT

P&ID:
202998C-001-PID-0021-0322

UNIT#: 6800 EWP AREA: 6820 SPEC: NOHD-NI03 STRESS CALC #: CN-0388/0392

LINE No:
8"-R2-67022-NOHD-NI03-H

DRAWING NUMBER
6820-R2-67022-07

REV.
2

