


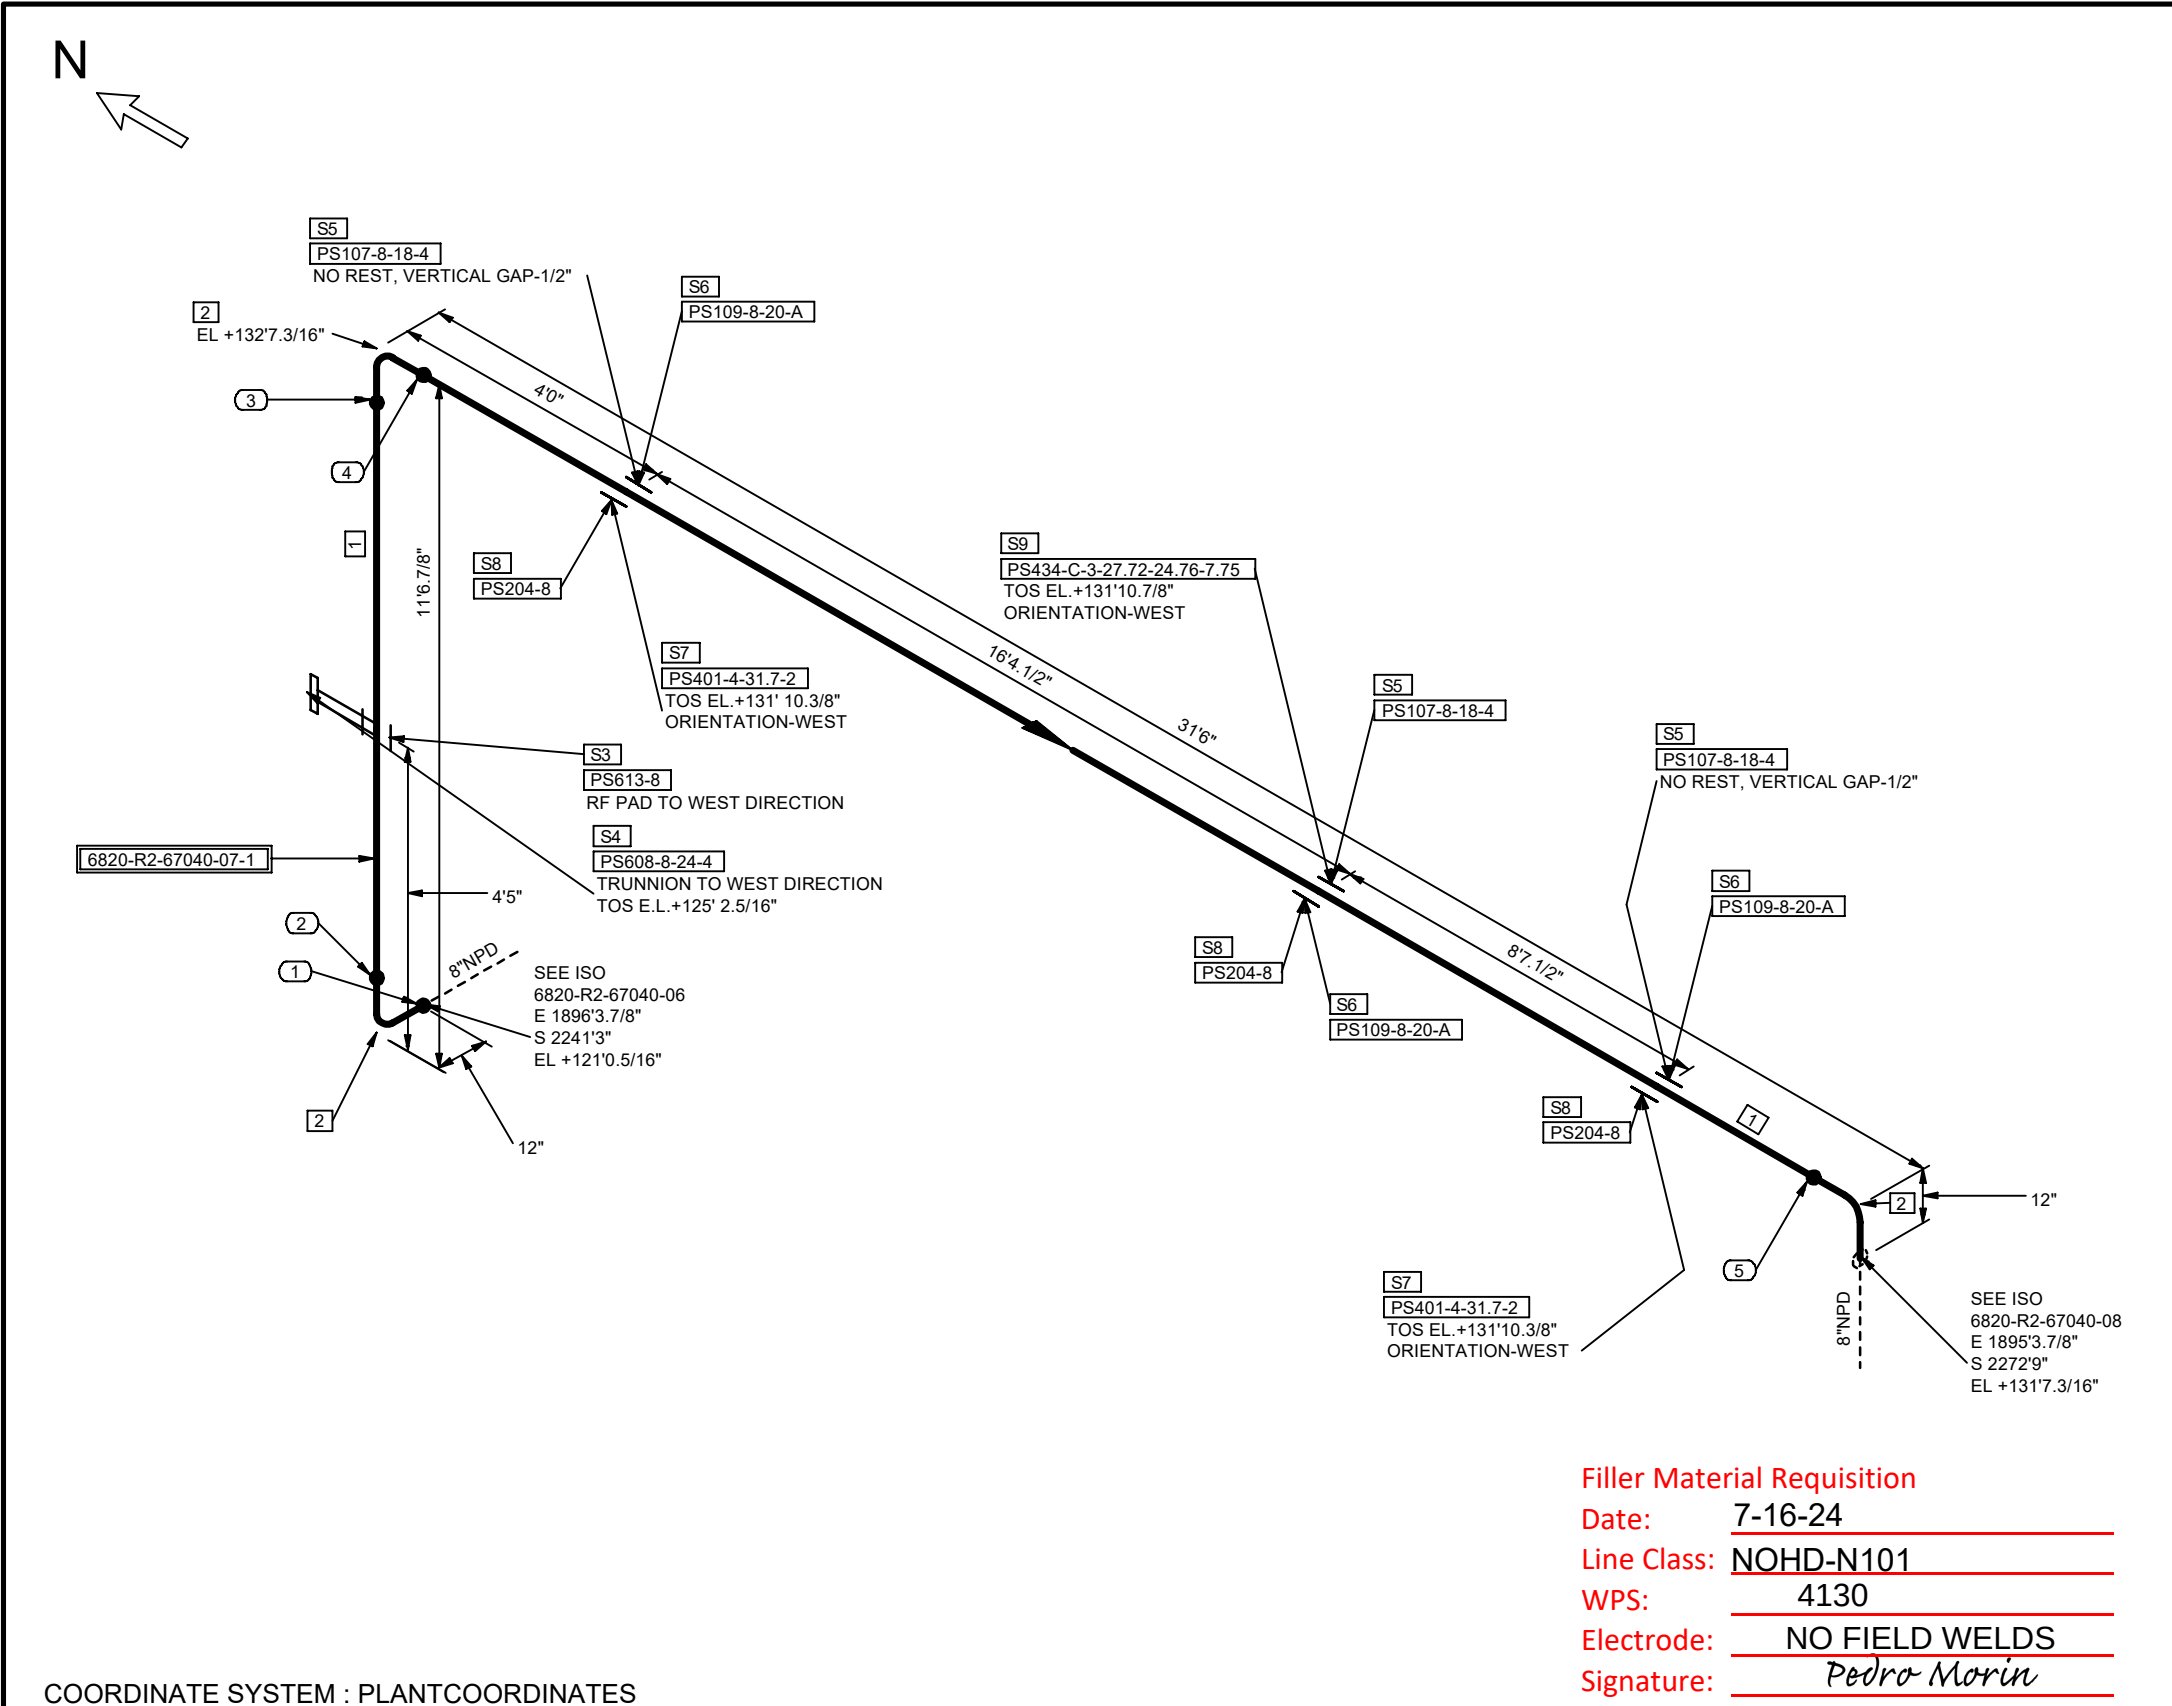

Filler Material Requisition
Date: 7-16-24
Line Class: NOHD-N101
WPS: 4130
Electrode: NO FIELD WELDS
Signature: Pedro Morin

SHOP MATERIALS				
NO	NPD	DESCRIPTION	IDENT	QTY
1	8	Pipes, EFW, ASME B36.19/B36.10, ASTM B725 UNS N02200 annealed, BE, -, -, S-10S	C7ZWWML7	39.1'
2	8	90° Elb LR, Seamless, ASME B16.9, ASTM B366 Gr.WPN, BW Ends, -,Annealed, S-10S	C7ZWX04P	3
PIPE SUPPORTS				
3	8	PS613-8	PS613	1
4	8	PS608-8-24-4	PS608	1
5	8	PS107-8-18-4	PS107	3
6	8	PS109-8-20-A	PS109	3
OTHER THAN SHOP MATERIALS				
NO	NPD	DESCRIPTION	IDENT	QTY
PIPE SUPPORTS				
7	8	PS401-4-31.7-2	PS401	2
8	8	PS204-8	PS204	3
9	8	PS434-C-3-27.72-24.76-7.75	PS434	1
PIECE MARKS				
6820-R2-67040-07-1				

COORDINATE SYSTEM : PLANTCOORDINATES

- NOTES:
- FOR LINE PRESSURES, TEMPERATURES, INSULATION TYPE AND THICKNESS, ETC. REFER TO LATEST REVISION OF LDT.
 - FOR STANDARD PIPE SUPPORT DETAILS SEE PROJECT STANDARD.
 - FIELD SHIM TO SUIT UNLESS OTHERWISE NOTED.
 - FOR PWHT REQUIREMENTS REFER TO LINE CLASS SPECIFICATION.
 - ALL THREADED PIPE LINE SYSTEMS, FIELD SHALL VERIFY DIMENSION PRIOR TO ERECTION.
 - FFW DESIGNATION AT WELDS INDICATES FIELD FIT WELD, WHERE PIPE FABRICATOR IS TO ADD 9 INCH OF PIPE TO THE ISOMETRIC DIMENSION TO ENABLE THE FIELD TO CUT TO FIT AT SITE.
 - REFER TO 202998C-000-W1-1300-0001 FOR FRP AND DUAL-LAM FABRICATION.

T.EN

TECHNIP ENERGIES

Information contained in this document is the work product of one or more legal entities of Technip Energies N.V. and embodies confidential and proprietary information of the applicable entity and/or its client. Use of this information is restricted in accordance with conditions specified by the contract. Technip Energies N.V. and its affiliates disclaim any and all liabilities for any changes or modifications to this document which are made by any person other than the entity that issued the document under the applicable client contract.

THIS DOCUMENT IS UNCONTROLLED WHEN REPRODUCED

0	2024-07-12	RVA	ISSUED FOR CONSTRUCTION	SAD	KJK	SAD	GR		
REV	DATE	BY	DESCRIPTION	CHKD	MTO	STRESS	APRVD		



SERVICE:	VAPOR/LIQUID:	INSUL TYPE:	INSUL THK:	SHOP:	FIELD:	PAINT CODE:	MODULE:	
R2	L	Per LDT	Per LDT	Y	Y	Per LDT	-	
				P&ID:				
				202998C-001-PID-0021-0323				
				UNIT#:	EWPA AREA:	SPEC:	STRESS CALC #:	
				6800	6820	NOHD-NI01	CN-0379	
				LINE No.				
OxyChem Redstone Battleground PROJECT				8"-R2-67040-NOHD-NI01-H				
				DRAWING NUMBER				
				6820-R2-67040-07				
						REV.	0	

