



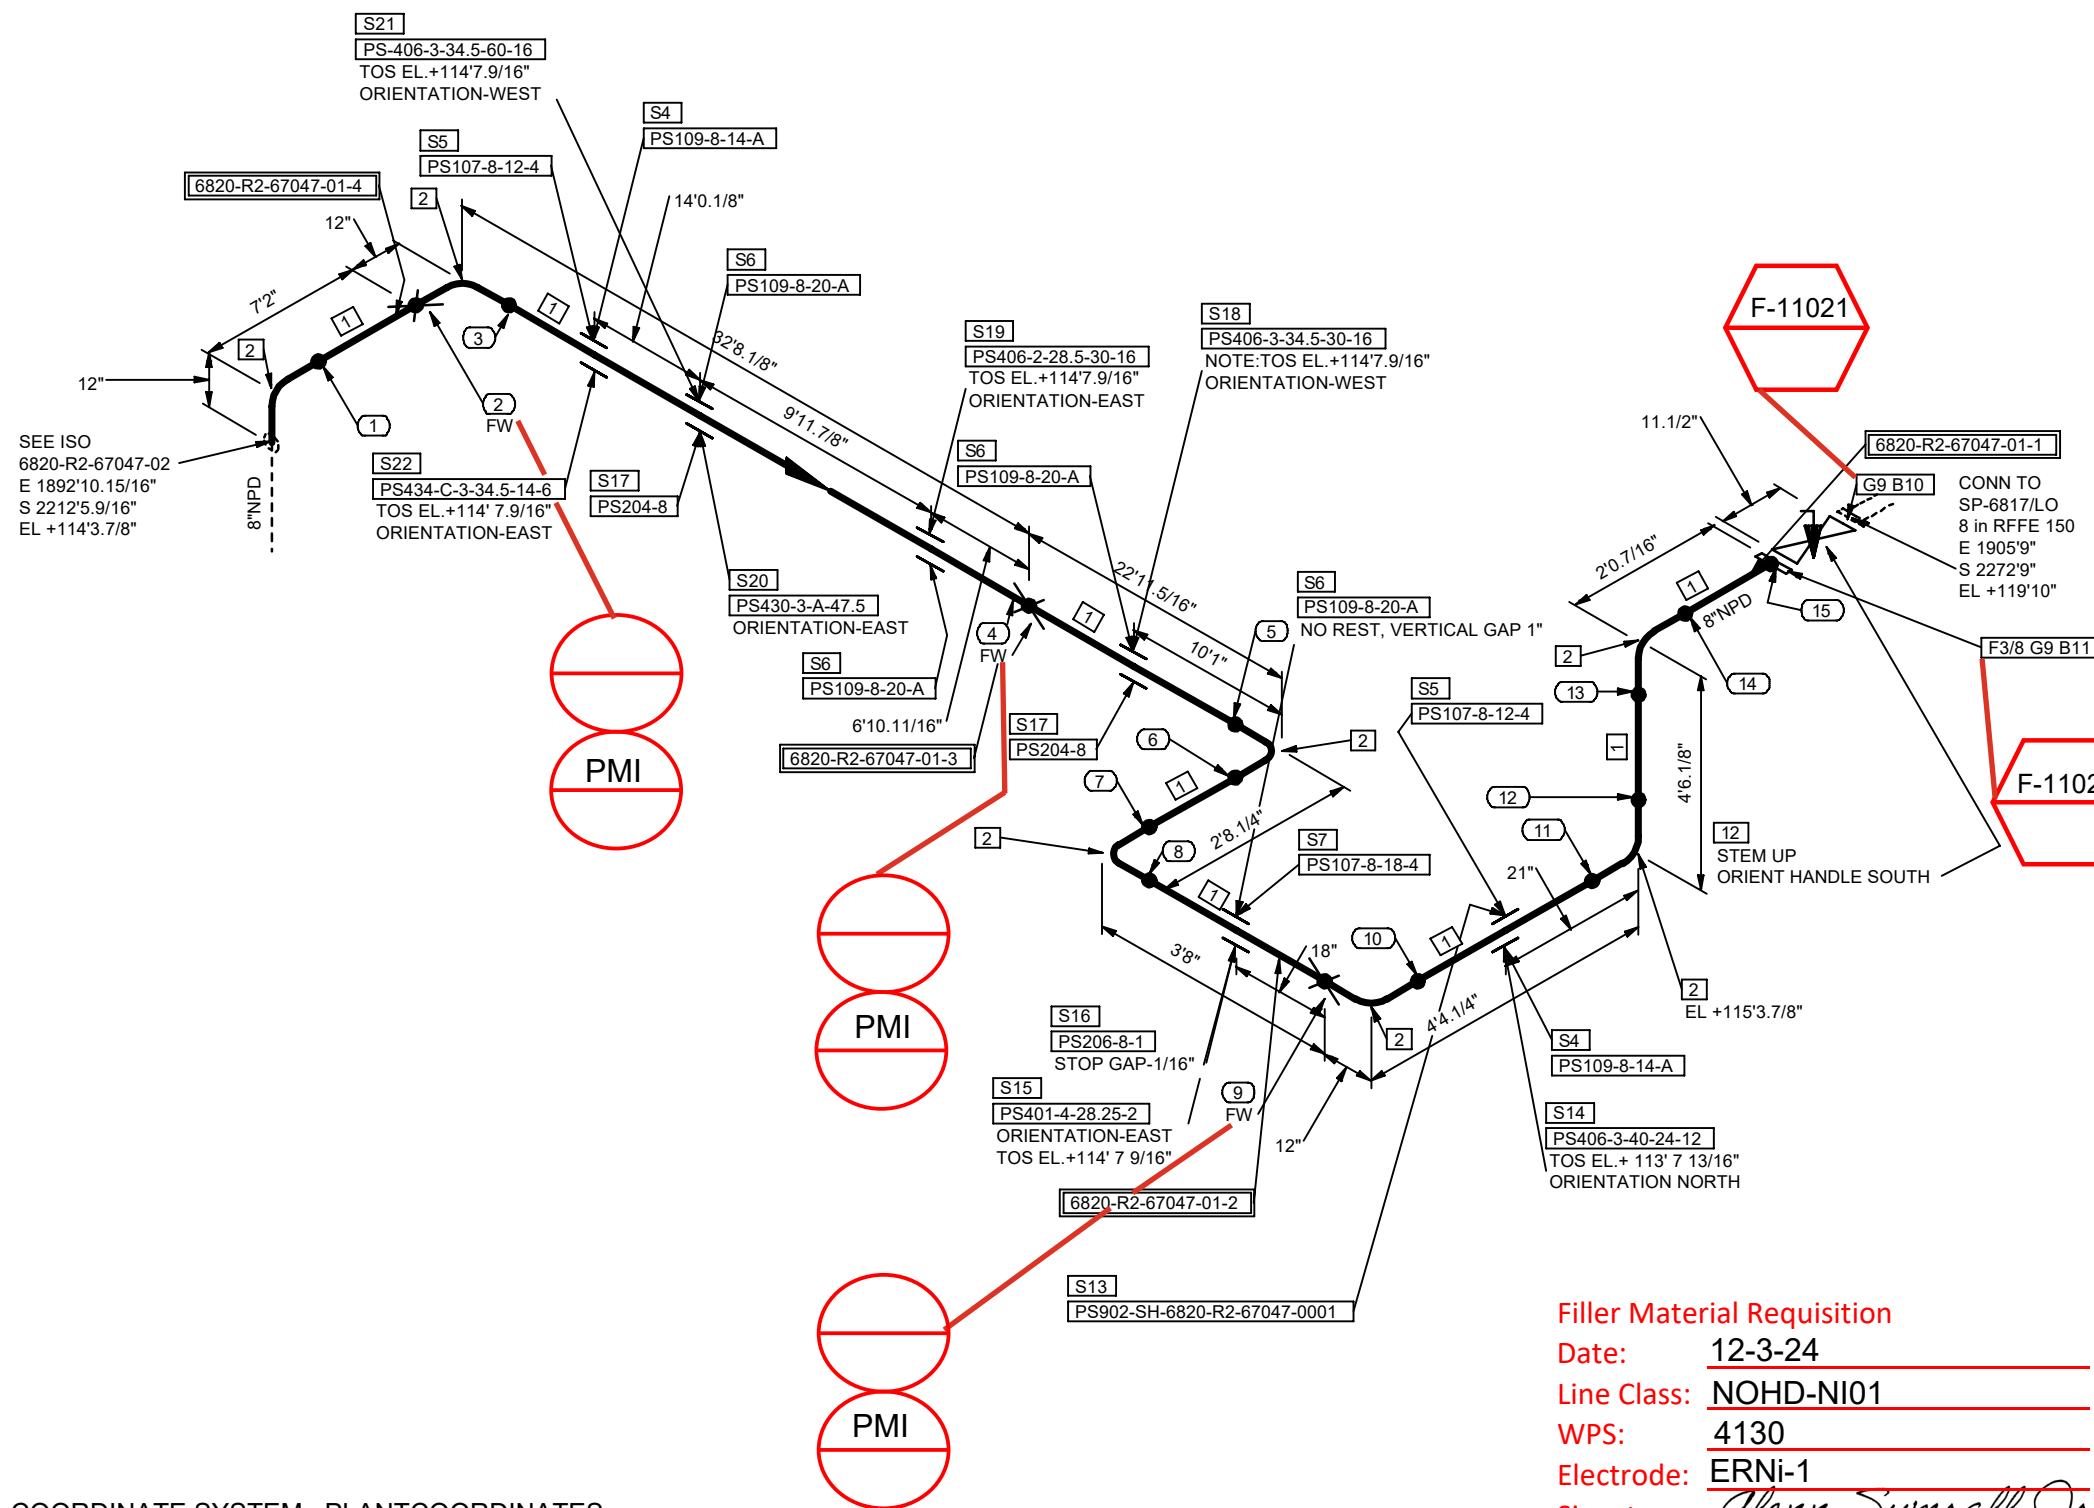

NOTES:

1. FOR LINE PRESSURES, TEMPERATURES, INSULATION TYPE AND THICKNESS, ETC. REFER TO LATEST REVISION OF LDT.
2. FOR STANDARD PIPE SUPPORT DETAILS SEE PROJECT STANDARD.
3. FIELD SHIM TO SUIT UNLESS OTHERWISE NOTED.
4. FOR PWHT REQUIREMENTS REFER TO LINE CLASS SPECIFICATION.
5. ALL THREADED PIPE LINE SYSTEMS, FIELD SHALL VERIFY DIMENSION PRIOR TO ERECTION.
6. FFW DESIGNATION AT WELDS INDICATES FIELD FIT WELD, WHERE PIPE FABRICATOR IS TO ADD 9 INCH OF PIPE TO THE ISOMETRIC DIMENSION TO ENABLE THE FIELD TO CUT TO FIT AT SITE.
7. REFER TO 202998C-000-W1-1300-0001 FOR FRP AND DUAL-LAM FABRICATION.

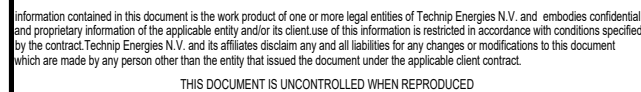

0	2024-11-22	RVA	ISSUED FOR CONSTRUCTION		SAD	KJK	SMR	GR	
REV	DATE	BY	DESCRIPTION		CHKD	MTO	STRESS	APRVD	

Date: 12-3-24

Line Class: NOHD-NI01

WPS: 4130

Electrode: ERNi-1

Signature: *Glenn Sumrall*

SHOP MATERIALS				
NO	NPD	DESCRIPTION	IDENT	QTY
1	8	Pipes, EFW, ASME B36.19/B36.10, ASTM B725 UNS N02200 annealed, BE, -, -, S-10S	C7ZWWML7	68.8
2	8	90° Elb LR, Seamless, ASME B16.9, ASTM B366 Gr.WPN, BW Ends, -,Annealed, S-10S	C7ZWX04P	7
3	8	LJ Flg, ASME B16.5, ASTM A105 Galv. as per ASTM A153, 150 Lbs, FF, -,	C26WFFFR	1
<u>PIPE SUPPORTS</u>				
4	8	PS109-8-14-A	PS109	2
5	8	PS107-8-12-4	PS107	2
6	8	PS109-8-20-A	PS109	4
7	8	PS107-8-18-4	PS107	1
<u>MISCELLANEOUS COMPONENTS</u>				
8	8	Stub SP, Seamless, ASME B16.9, ASTM B366 Gr.WPN, BW Ends, -,Annealed, x S-10S	C8A5GY48	1
<u>OTHER THAN SHOP MATERIALS</u>				
NO	NPD	DESCRIPTION	IDENT	QTY
9	8	NM Flat Gk, Barium Sulfate filled PTFE, 150 Lbs, RF as per ASME B16.5, -, Thk=1/8in, -,	C6SBWZF4	2
10	3/4	SBlt 2 HHx N, A193 Gr.B7/A194 Gr.2H, -, Xylan PTFE Coated, - 4.5 in. Length	C6S4K8BD	8
11	3/4	SBlt 2 HHx N, A193 Gr.B7/A194 Gr.2H, -, Xylan PTFE Coated, - 4.75 in. Length	C6S4K8BE	8
12	8	Plug Flg,SP, Inverted Tapered Plug, Non Lubricated, API 599, ASTM A494 Gr.CZ100, 150 Lbs, RF, Ends as per ASME B16.5, -, GO,-, -, Valve Tag: PL-0503	C8P7NJK0	1
<u>PIPE SUPPORTS</u>				
13	8	PS902-SH-6820-R2-67047-0001	PS902	1
14	8	PS406-3-40-24-12	PS406	1
15	8	PS401-4-28-25-2	PS401	1
16	8	PS206-8-1	PS206	1
17	8	PS204-8	PS204	2
18	8	PS406-3-34.5-30-16	PS406	1
19	8	PS406-2-28.5-30-16	PS406	1
20	8	PS430-3-A-47.5	PS430	1
21	8	PS-406-3-34.5-60-16	PS	1
22	8	PS434-C-3-34.5-14-6	PS434	1

6820-R2-67047-01-1 6820-R2-67047-01-2 6820-R2-67047-01-3
6820-R2-67047-01-4



SERVICE: R2	VAPOR/LIQUID: L	INSUL TYPE: Per LDT	INSUL THK: Per LDT	SHOP: Y	FIELD: Y	PAINT CODE: Per LDT	MODULE: -
				P&ID: 202998C-001-PID-0021-0324			
				UNIT#: 6800	LEWP AREA: 6820	SPEC: NOHD-NI01	STRESS CALC #: CN-0379
				LINE No. 8"-R2-67047-NOHD-NI01-H			
				DRAWING NUMBER 6820-R2-67047-01			
OxyChem Redstone Battleground PROJECT				REV.		0	

