


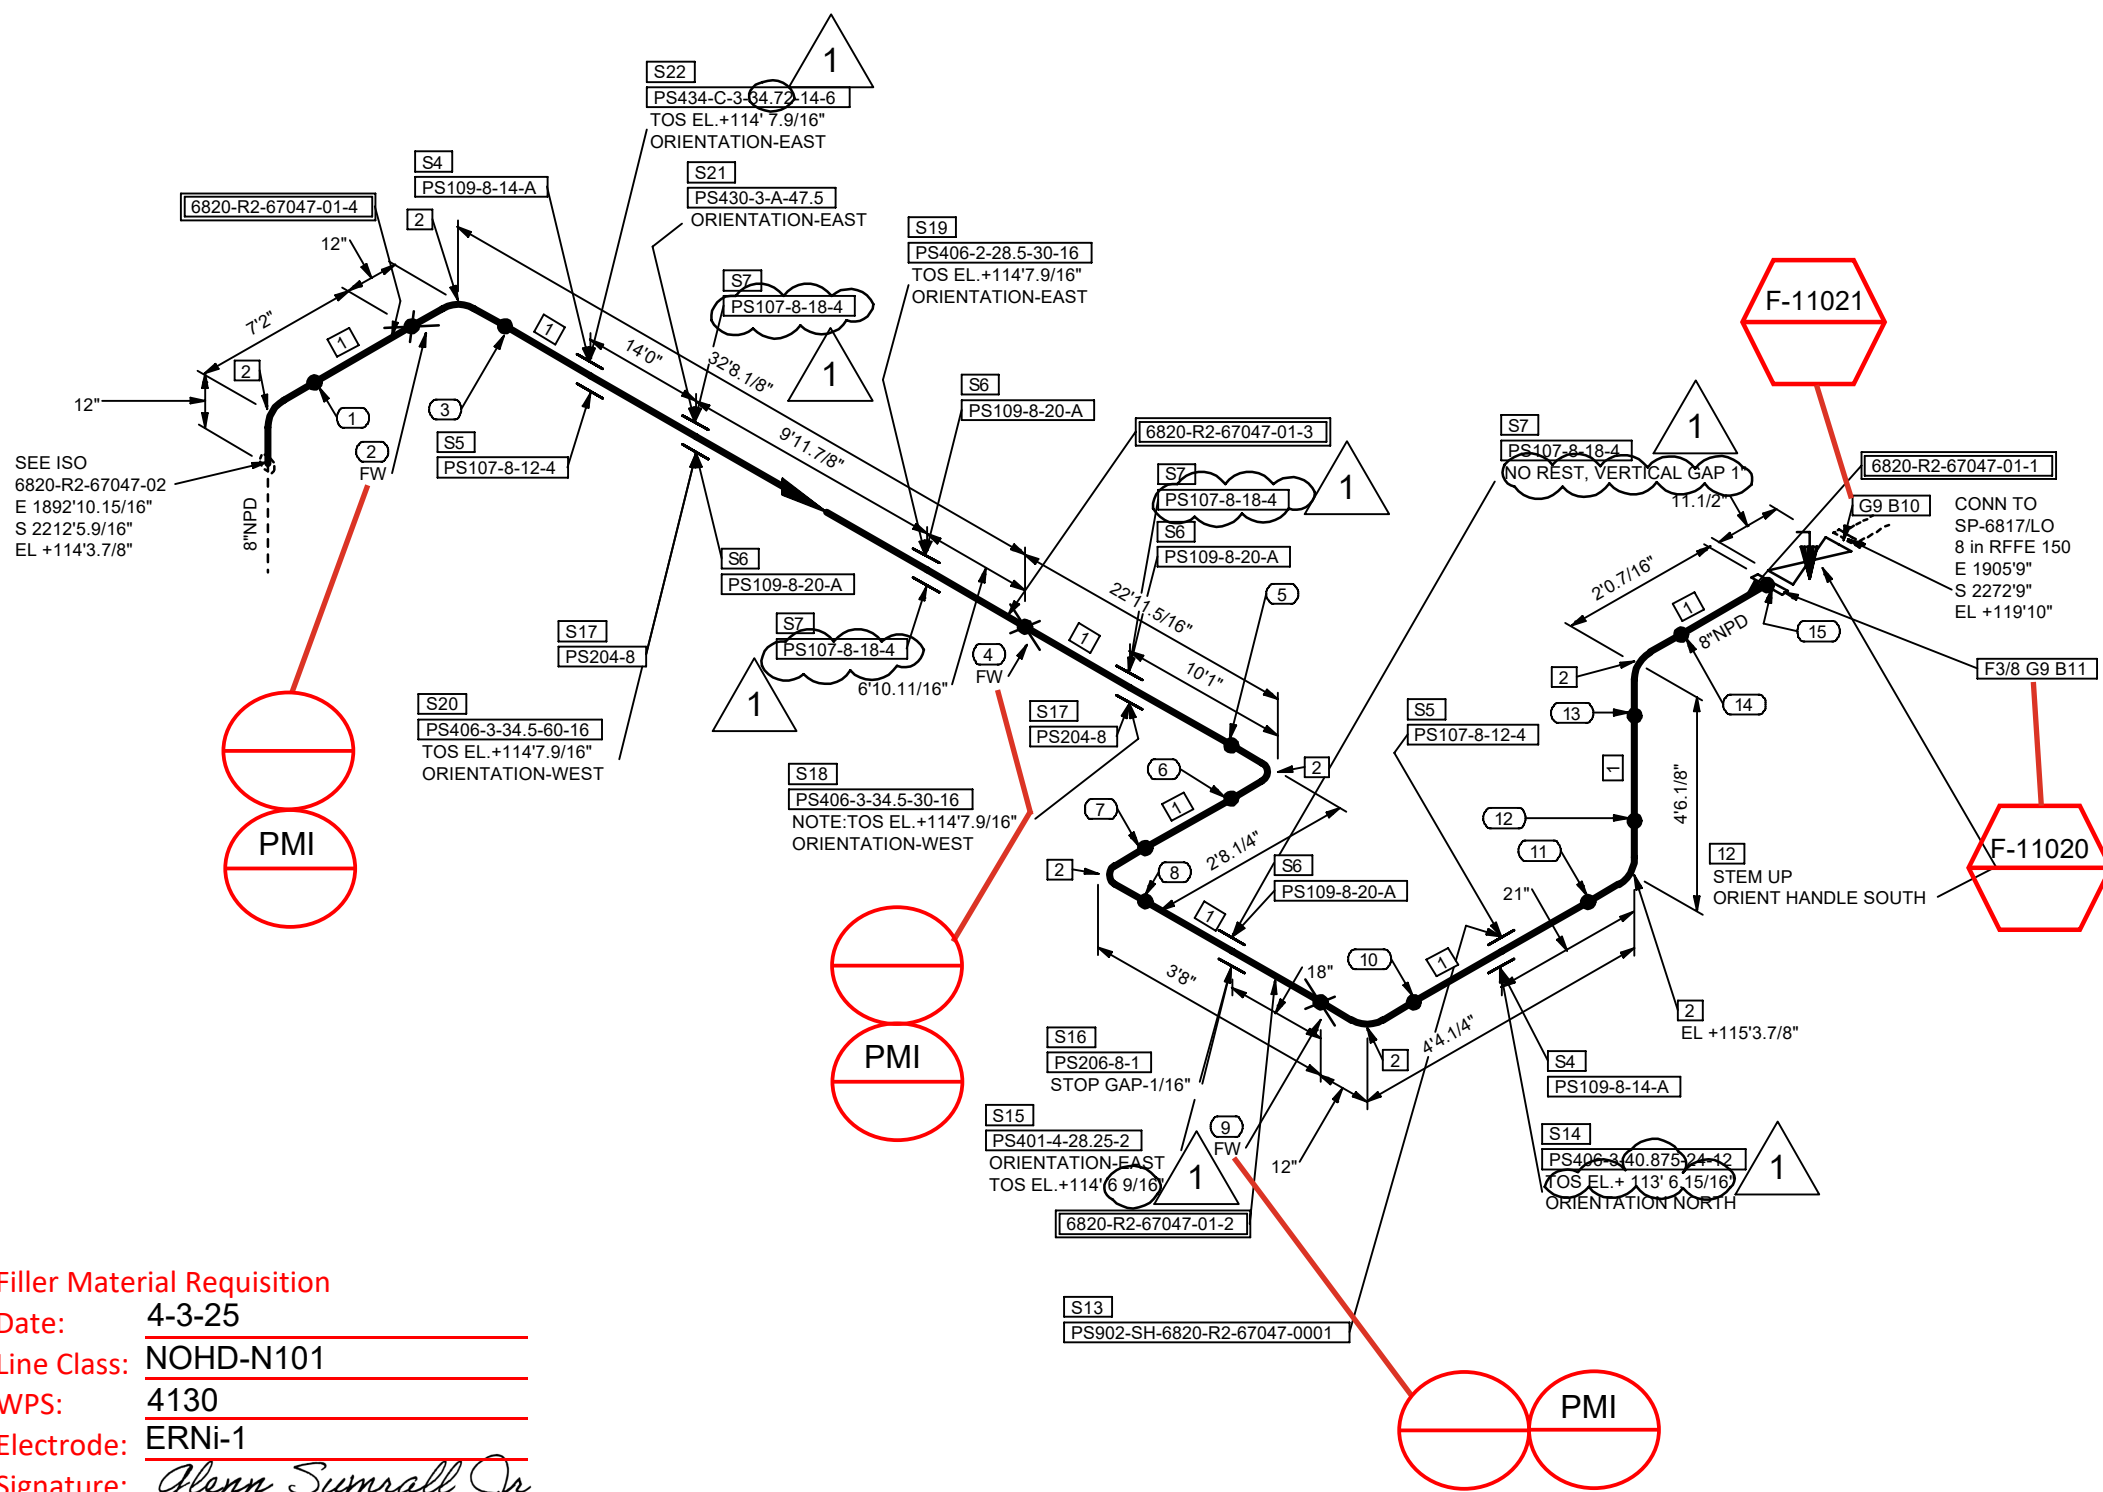

Date: 4-3-25
Line Class: NOHD-N101
WPS: 4130
Electrode: ERNi-1
Signature: *Glenn S*

NOTES:

FOR LINE PRESSURES, TEMPERATURES, INSULATION TYPE AND THICKNESS, ETC.
REFER TO LATEST REVISION OF LDT.

FOR STANDARD PIPE SUPPORT DETAILS SEE PROJECT STANDARD.


FIELD SHIM TO SUIT UNLESS OTHERWISE NOTED.

FOR PWHT REQUIREMENTS REFER TO LINE CLASS SPECIFICATION.

ALL THREADED PIPE LINE SYSTEMS, FIELD SHALL VERIFY DIMENSION PRIOR TO ERECTION.

FWF DESIGNATION AT WELDS INDICATES FIELD FIT WELD, WHERE PIPE FABRICATOR IS TO ADD 1/8 INCH OF PIPE TO THE ISOMETRIC DIMENSION TO ENABLE THE FIELD TO CUT TO FIT AT SITE.

REFER TO 202998C-000-W1-1300-0001 FOR FRP AND DUAL-LAM FABRICATION.

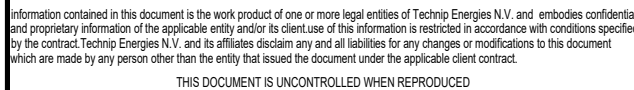

SERVICE: R2	VAPOR/LIQUID: L	INSUL TYPE: Per LDT	INSUL THK: Per LDT	SHOP: Y	FIELD: Y	PAINT CODE: Per LDT	MODULE: -	
 OxyChem Redstone Battleground PROJECT				P&ID: 202998C-001-PID-0021-0324				
				UNIT#: 6800	EWP AREA: 6820	SPEC: NOHD-NI01	STRESS CALC #: CN-0379	
				LINE No. 8"-R2-67047-NOHD-NI01-H				
				DRAWING NUMBER 6820-R2-67047-01				REV. 1

PIECE MARKS	
6820-R2-67047-01-1	6820-R2-67047-01-2
6820-R2-67047-01-3	6820-R2-67047-01-4

SERVICE: R2	VAPOR/LIQUID: L	INSUL TYPE: Per LDT	INSUL THK: Per LDT	SHOP: Y	FIELD: Y	PAINT CODE: Per LDT	MODULE: -
				P&ID: 202998C-001-PID-0021-0324			
				UNIT#: 6800	EWP AREA: 6820	SPEC: NOHD-NI01	STRESS CALC #: CN-0379
				LINE No. 8"-R2-67047-NOHD-NI01-H			
				DRAWING NUMBER 6820-R2-67047-01			
OxyChem Redstone Battleground PROJECT							