


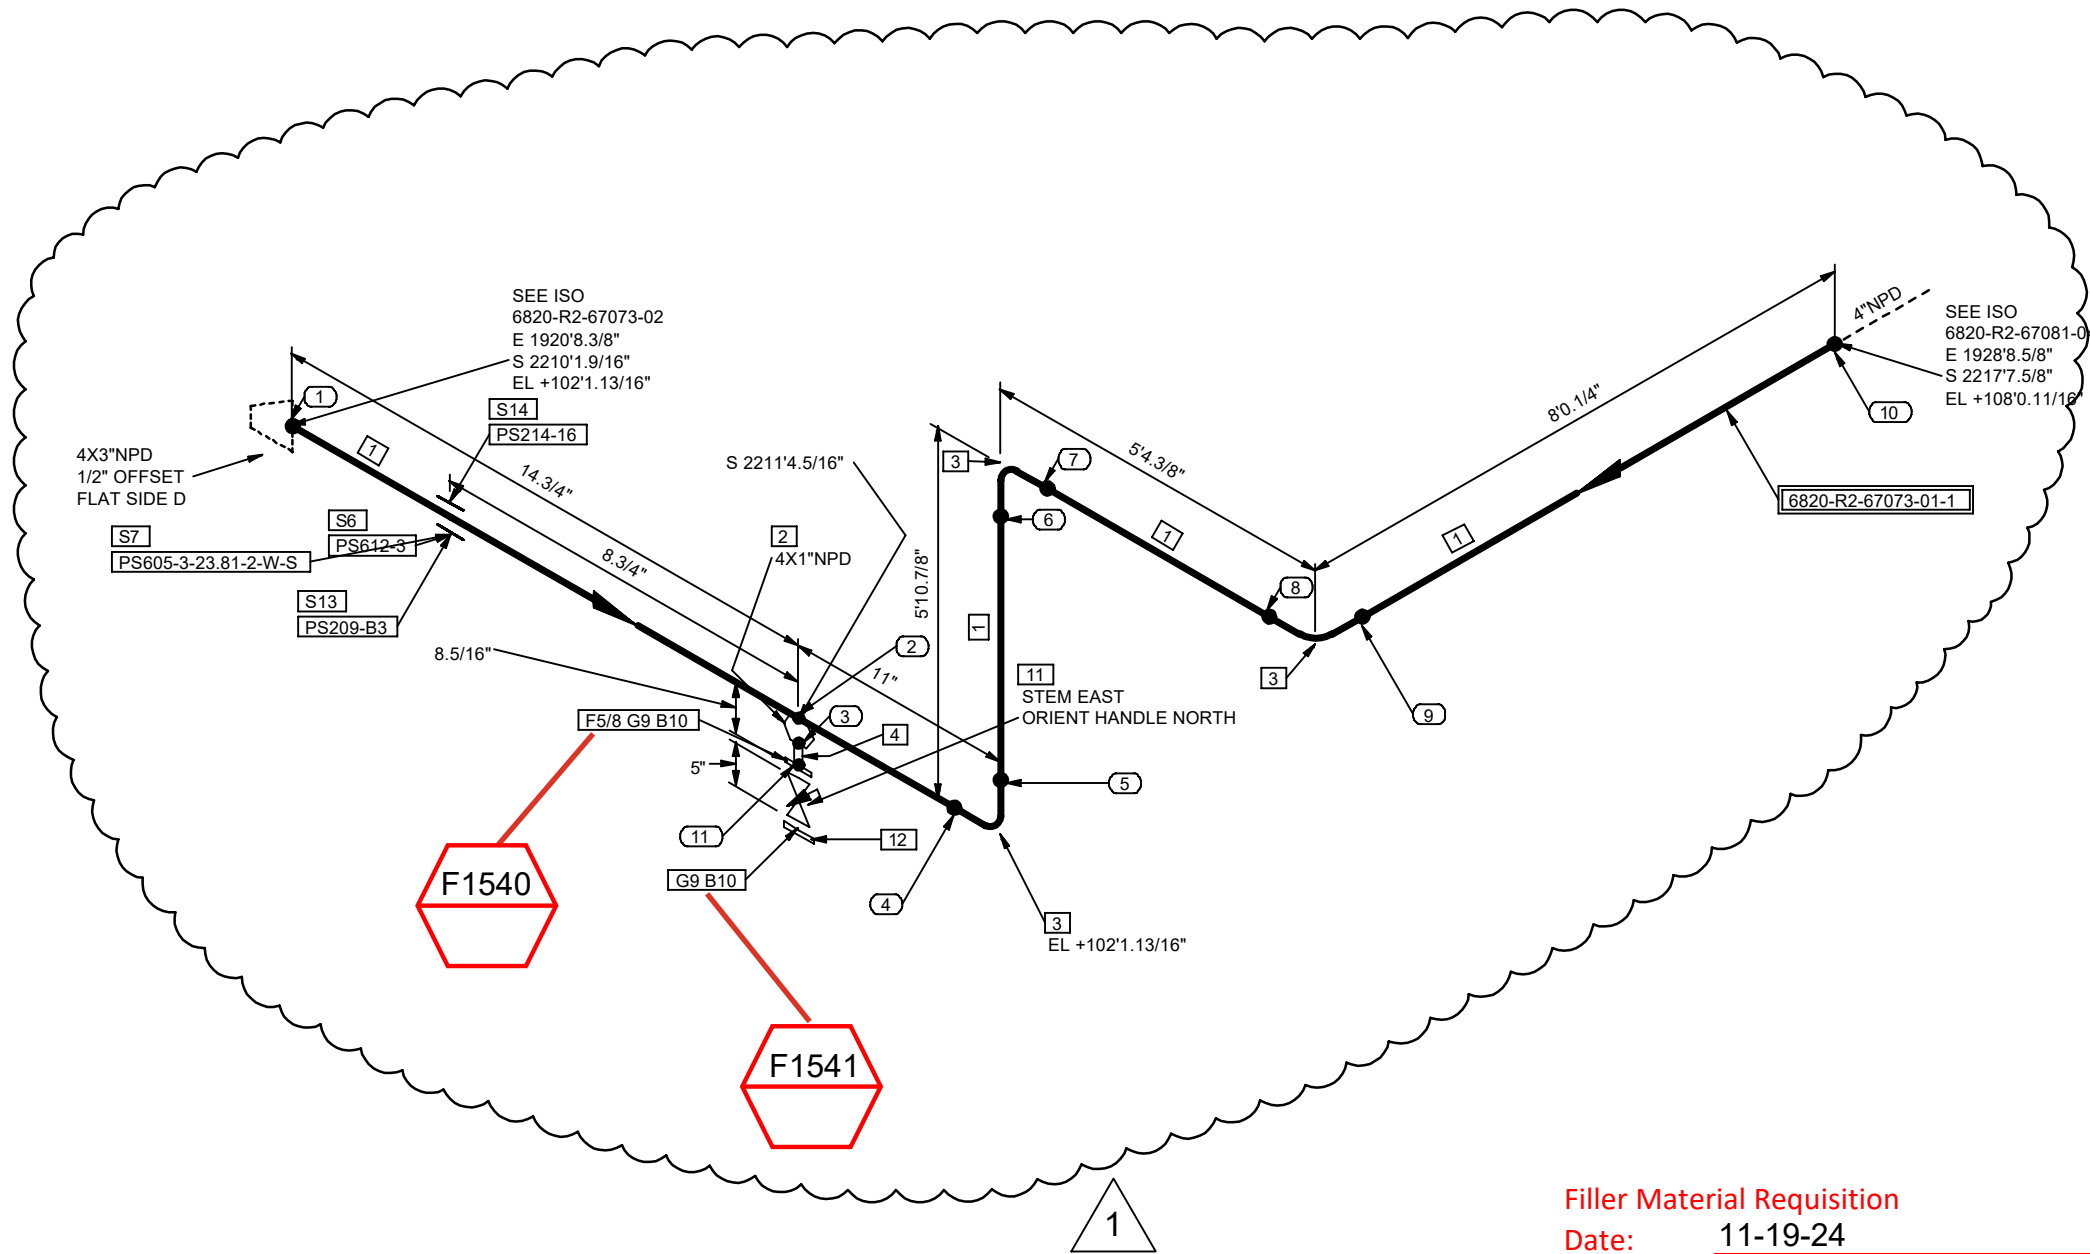

COORDINATE SYSTEM : PLANTCOORDINATES

Filler Material Requisition

Date: 11-19-24
Line Class: NOHD-SS01
WPS: 802
Electrode: ER316L
Signature: *Glenn Sumrall Jr*

SHOP MATERIALS

NO	NPD	DESCRIPTION	IDENT	QTY
1	4	Pipes, Seamless, ASME B36.19/B36.10, ASTM A312 Gr.TP316L, BE, -, -, S-10S	CPP5F90U	18.5'
2	4X1	Weldolet, MSS SP-97, ASTM A182 Gr.F316L, BW Ends, Annealed, S-10S x S-40S	C80R6A72	1
3	4	90° Elb LR, Seamless, ASME B16.9, ASTM A403 Gr.WP316L, BW Ends, -,Annealed, S-10S	C6SDP2PZ	3
4	1	Nipple, ASTM A312 Gr.TP316L, BE, L = 3in, -, S-40S	C80R1V84	1
5	1	LJ Flg, ASME B16.5, ASTM A105 Galv. as per ASTM A153, 150 Lbs, FF, -,	C26WFFF7	1

PIPE SUPPORTS

6	4	PS612-3	PS612	1
7	4	PS605-3-23.81-2-W-S	PS605	1

MISCELLANEOUS COMPONENTS

8	1	Stub SP, Seamless, ASME B16.9, ASTM A403 Gr.WP316L, BW Ends, -,Annealed, x S-40S	C8A57RN3	1
---	---	--	----------	---

OTHER THAN SHOP MATERIALS

NO	NPD	DESCRIPTION	IDENT	QTY
9	1	NM Flat Gk, Barium Sulfate filled PTFE, 150 Lbs, RF as per ASME B16.5, -, Thk=1/8in, -,	C6S4K87F	2
10	1/2	SBlt 2 HHx N, A193 Gr.B7/A194 Gr.2H, -, Xylan PTFE Coated, - 2.75 in. Length	C6S4K87U	8
11	1	Plug Flg,SP, Tapered Plug, Non Lubricated, API 599, ASTM A351 Gr.CF8M, 150 Lbs, RF, Ends as per ASME B16.5, -, LO,-, -, Valve Tag: PL-0548	C76KHSRR	1
12	1	Bld Flg, ASME B16.5, ASTM A182 Gr.F316L, 150 Lbs, RF, Annealed,	C80R6Y1H	1

PIPE SUPPORTS

13	4	PS209-B3	PS209	1
14	4	PS214-16	PS214	1

PIECE MARKS

6820-R2-67073-01-1



- NOTES:
- FOR LINE PRESSURES, TEMPERATURES, INSULATION TYPE AND THICKNESS, ETC. REFER TO LATEST REVISION OF LDT.
 - FOR STANDARD PIPE SUPPORT DETAILS SEE PROJECT STANDARD.
 - FIELD SHIM TO SUIT UNLESS OTHERWISE NOTED.
 - FOR PWHT REQUIREMENTS REFER TO LINE CLASS SPECIFICATION.
 - ALL THREADED PIPE LINE SYSTEMS, FIELD SHALL VERIFY DIMENSION PRIOR TO ERECTION.
 - FFW DESIGNATION AT WELDS INDICATES FIELD FIT WELD, WHERE PIPE FABRICATOR IS TO ADD 9 INCH OF PIPE TO THE ISOMETRIC DIMENSION TO ENABLE THE FIELD TO CUT TO FIT AT SITE.
 - REFER TO 202998C-000-W1-1300-0001 FOR FRP AND DUAL-LAM FABRICATION.



Information contained in this document is the work product of one or more legal entities of Technip Energies N.V. and embodies confidential and proprietary information of the applicable entity and/or its client. Use of this information is restricted in accordance with conditions specified by the contract. Technip Energies N.V. and its affiliates disclaim any and all liabilities for any changes or modifications to this document which are made by any person other than the entity that issued the document under the applicable client contract.

THIS DOCUMENT IS UNCONTROLLED WHEN REPRODUCED

REV	DATE	BY	DESCRIPTION	CHKD	MTO	STRESS	APRVD
1	2024-11-08	RVA	ISSUED FOR CONSTRUCTION	SAD	KJK	SMR	GR
0	2024-08-02	RVA	ISSUED FOR CONSTRUCTION	SAD	KJK	BRD	GR

SERVICE: R2	VAPOR/LIQUID: L	INSUL TYPE: Per LDT	INSUL THK: Per LDT	SHOP: Y	FIELD: Y	PAINT CODE: Per LDT	MODULE: -
P&ID: 202998C-001-PID-0021-0325				UNIT#: 6800	EWPA AREA: 6820	SPEC: NOHD-SS01	STRESS CALC #: CN-0393
LINE No: 4"-R2-67073-NOHD-SS01-H				DRAWING NUMBER: 6820-R2-67073-01			
OxyChem Redstone Battleground PROJECT							REV: 1

