



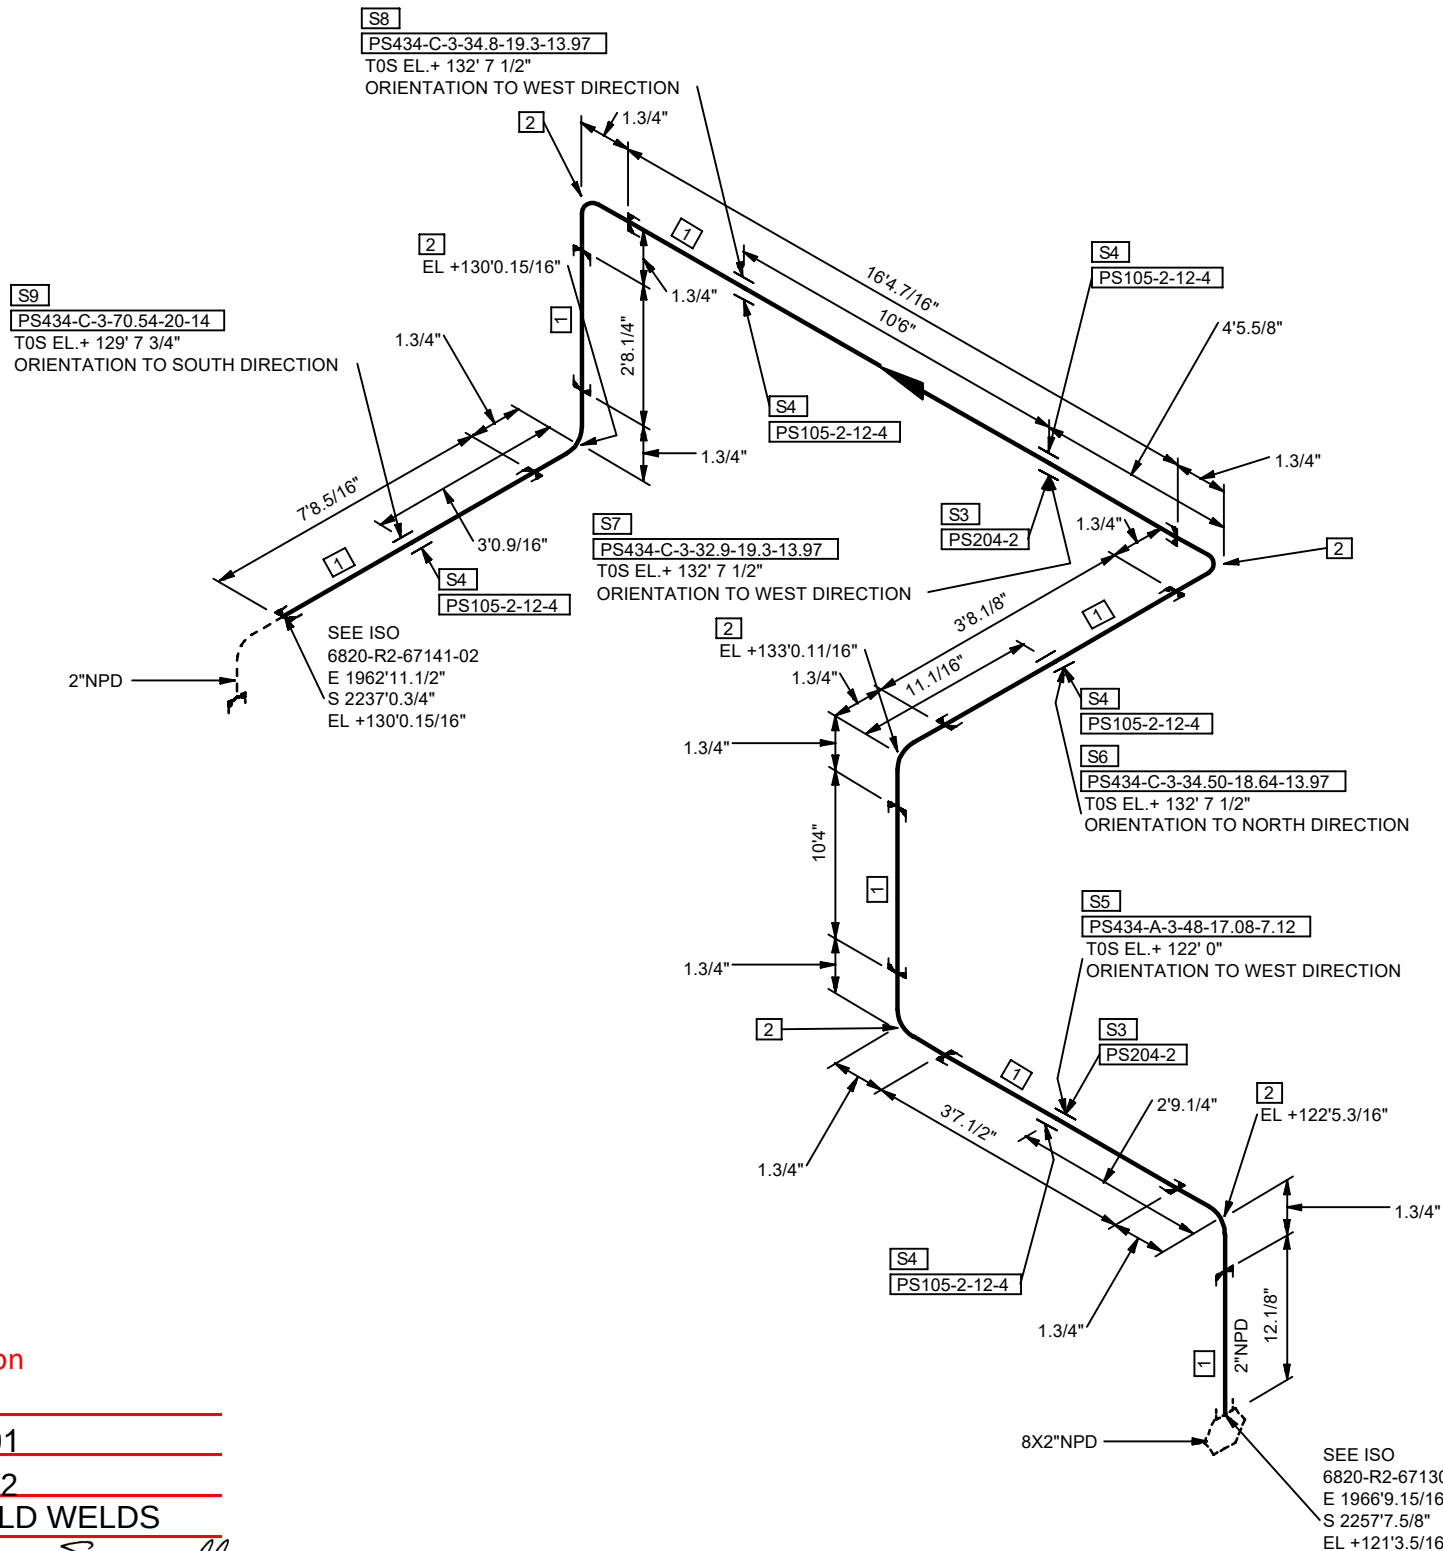

Filler Material Requisition
Date: 7-1-24
Line Class: EPCL-SS01
WPS: 802
Electrode: NO FIELD WELDS
Signature: Glenn Sumrall

COORDINATE SYSTEM : PLANTCOORDINATES

- NOTES:
- FOR LINE PRESSURES, TEMPERATURES, INSULATION TYPE AND THICKNESS, ETC. REFER TO LATEST REVISION OF LDT.
 - FOR STANDARD PIPE SUPPORT DETAILS SEE PROJECT STANDARD.
 - FIELD SHIM TO SUIT UNLESS OTHERWISE NOTED.
 - FOR PWHT REQUIREMENTS REFER TO LINE CLASS SPECIFICATION.
 - ALL THREADED PIPE LINE SYSTEMS, FIELD SHALL VERIFY DIMENSION PRIOR TO ERECTION.
 - FFW DESIGNATION AT WELDS INDICATES FIELD FIT WELD, WHERE PIPE FABRICATOR IS TO ADD 9 INCH OF PIPE TO THE ISOMETRIC DIMENSION TO ENABLE THE FIELD TO CUT TO FIT AT SITE.

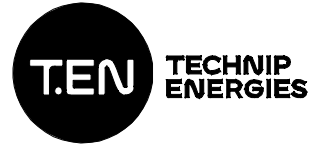

Information contained in this document is the work product of one or more legal entities of Technip Energies N.V. and embodies confidential and proprietary information of the applicable entity and/or its client. Use of this information is restricted in accordance with conditions specified by the contract. Technip Energies N.V. and its affiliates disclaim any and all liabilities for any changes or modifications to this document which are made by any person other than the entity that issued the document under the applicable client contract.

THIS DOCUMENT IS UNCONTROLLED WHEN REPRODUCED

REV	DATE	BY	DESCRIPTION	CHKD	MTO	STRESS	APRVD
0	2024-06-28	RVA	ISSUE FOR CONSTRUCTION	SAD	KJK	BRD	GR

OTHER THAN SHOP MATERIALS				
NO	NPD	DESCRIPTION	IDENT	QTY
1	2	Pipes, Seamless, ASME B36.19/B36.10, ASTM A312 Gr. TP304L, NPTM Ends, w/ coupling, -, S-80S	C76KFFWK	45.4
2	2	90° Elb, ASME B16.11, ASTM A182 Gr. F304L, 3000 Lbs, NPTF Ends, Annealed,	C7BP5GGZ	6
PIPE SUPPORTS				
3	2	PS204-2	PS204	2
4	2	PS105-2-12-4	PS105	5
5	2	PS434-A-3-48-17.08-7.12	PS434	1
6	2	PS434-C-3-34.50-18.64-13.97	PS434	1
7	2	PS434-C-3-32.9-19.3-13.97	PS434	1
8	2	PS434-C-3-34.8-19.3-13.97	PS434	1
9	2	PS434-C-3-70.54-20-14	PS434	1





OxyChem Redstone Battleground PROJECT

SERVICE: R2	VAPOR/LIQUID: L	INSUL TYPE: Per LDT	INSUL THK: Per LDT	SHOP: N	FIELD: Y	PAINT CODE: Per LDT	MODULE: -
P&ID: 202998C-001-PID-0021-0329							
UNIT#: 6800	EWPA AREA: 6820	SPEC: EPCL-SS01	STRESS CALC #: NC				
LINE No. 2"-R2-67141-EPCL-SS01-H							
DRAWING NUMBER 6820-R2-67141-01							REV. 0

