


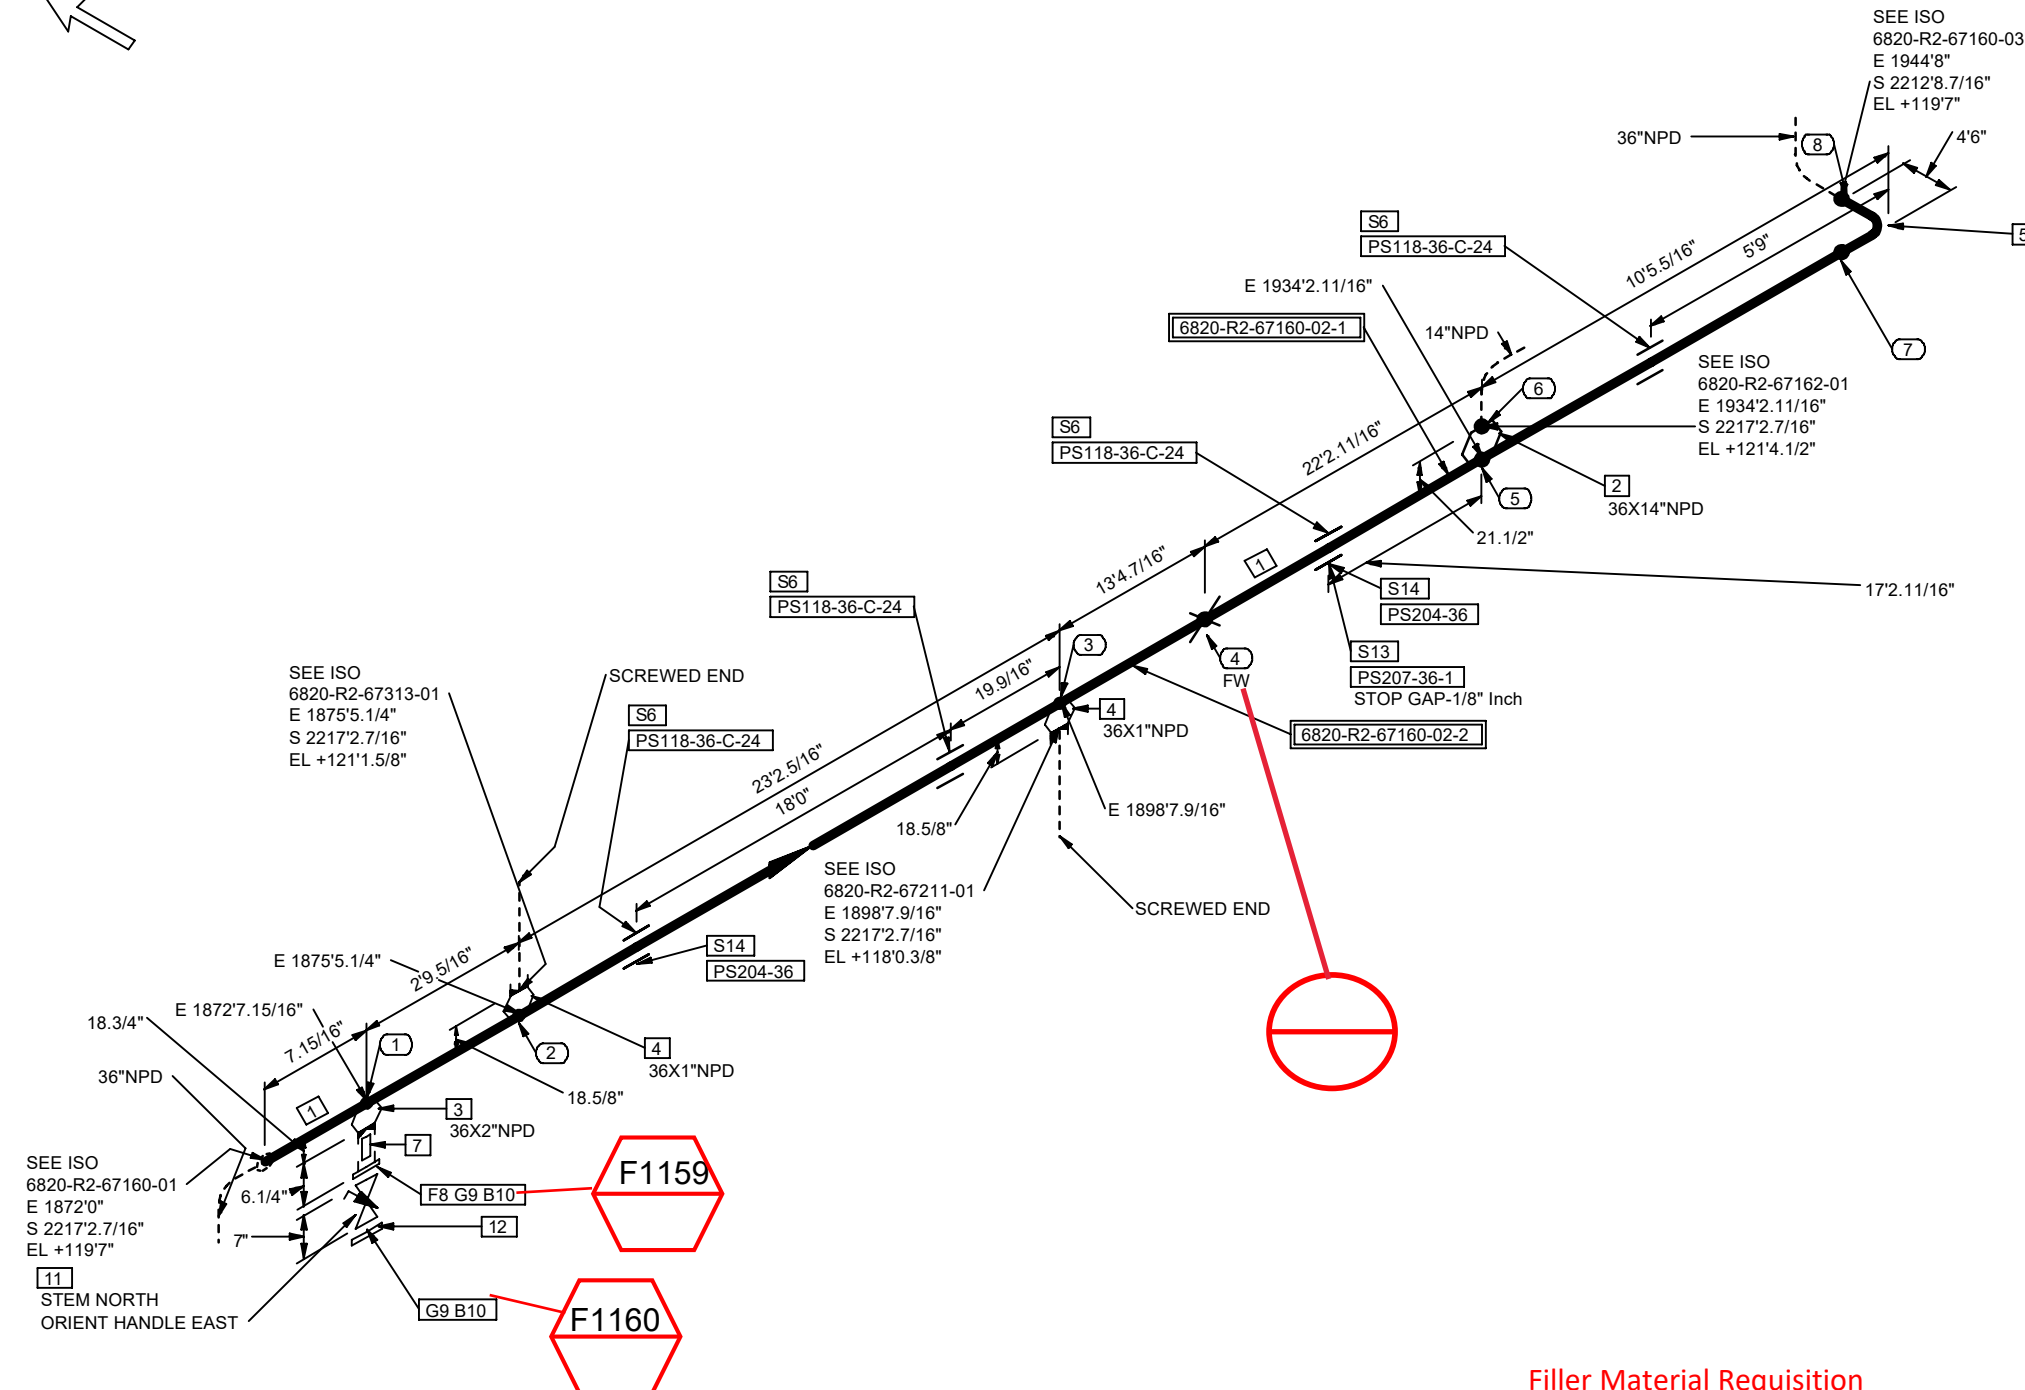

COORDINATE SYSTEM : PLANTCOORDINATES

NOTES:

1. FOR LINE PRESSURES, TEMPERATURES, INSULATION TYPE AND THICKNESS, ETC.
REFER TO LATEST REVISION OF LDT.
2. FOR STANDARD PIPE SUPPORT DETAILS SEE PROJECT STANDARD.
3. FIELD SHIM TO SUIT UNLESS OTHERWISE NOTED.
4. FOR PWHT REQUIREMENTS REFER TO LINE CLASS SPECIFICATION.
5. ALL THREADED PIPE LINE SYSTEMS, FIELD SHALL VERIFY DIMENSION PRIOR TO ERECTION.
6. FFW DESIGNATION AT WELDS INDICATES FIELD FIT WELD, WHERE PIPE FABRICATOR IS TO ADD
9 INCH OF PIPE TO THE ISOMETRIC DIMENSION TO ENABLE THE FIELD TO CUT TO FIT AT SITE.
7. REFER TO 202998C-000-W1-1300-0001 FOR FRP AND DUAL-LAM FABRICATION.



Information contained in this document is the work product of one or more legal entities of Technip Energies N.V. and embodies confidential and proprietary information of the applicable entity and/or its client; use of this information is restricted in accordance with conditions specified by the contract. Technip Energies N.V. and its affiliates disclaim any and all liabilities for any changes or modifications to this document which are made by any person other than the entity that issued the document under the applicable client contract.

THIS DOCUMENT IS UNCONTROLLED WHEN REPRODUCED

0	2024-07-26	RVA	ISSUED FOR CONSTRUCTION	SAD	KJK	BRD	GR
REV	DATE	BY	DESCRIPTION	CHKD	MTO	STRESS	APRVD

Filler Material Requisition

Date: 8-2-24

Line Class: CTWL-CS01

WPS: 10245

Electrode: ER70S-2

Signature: Glenn Sumrall Jr

SHOP MATERIALS				
NO	NPD	DESCRIPTION	IDENT	QTY
1	36	Pipes, DSAW, ASME B36.10, API 5L Gr.B PSL1, BE, -, -, .375"	C7SN25MV	68.2
2	36X14	Weldolet, MSS SP-97, ASTM A105N, BW Ends, -, .375" x S-STD	C56W17FS	1
3	36X2	Thredolet, ASTM A105N Galv. as per ASTM A153, 3000 Lbs, NPTF Ends, -, -,	C5N67YV5	1
4	36X1	Thredolet, ASTM A105N Galv. as per ASTM A153, 3000 Lbs, NPTF Ends, -, -,	C5MYLG8B	2
5	36	90° Elb LR, Welded + 100% RT, ASME B16.9, ASTM A234 Gr.WPB, BW Ends, -, -, .375"	CE79U10	1
PIPE SUPPORTS				
6	36	PS118-36-C-24	PS118	4
OTHER THAN SHOP MATERIALS				
NO	NPD	DESCRIPTION	IDENT	QTY
7	2	Nipple, ASTM A106 Gr.B Galv. as per ASTM A153, NPTM Ends, L = 6in, -, S-XS	C76KHZKZ	1
8	2	THD Flg, ASME B16.5, ASTM A105N Galv. as per ASTM A153, 150 Lbs, RF/NPTF End, -,	C1DR2JR	1
9	2	NM Flat Gk, Aramid Fiber Reinforced SBR, 150 Lbs, RF as per ASME B16.5, Full Face, Thk=1/8in, -,	C76KHSS3	2
10	5/8	SBlT 2 HHx N, A193 Gr.B7/A194 Gr.2H, -, Xylan PTFE Coated, - 3.5 in. Length	C6S4K88R	8
11	2	Plug Flg.SP, Inverted Tapered Plug, Non Lubricated, API 599, ASTM A395 Gr.60-40-18, 150 Lbs, RF, Ends as per ASME B16.5, -, LO,-, -, Valve Tag: PL-0546	C76RJXHX	1
12	2	Bld Flg, ASME B16.5, ASTM A105N Galv. as per ASTM A153, 150 Lbs, RF, -,	C1DR2JY	1
PIPE SUPPORTS				
13	36	PS207-36-1	PS207	1
14	36	PS204-36	PS204	2
PIECE MARKS				
6820-R2-67160-02-1 6820-R2-67160-02-2				



SERVICE: R2	VAPOR/LIQUID: L	INSUL TYPE: Per LDT	INSUL THK: Per LDT	SHOP: Y	FIELD: Y	PAINT CODE: Per LDT	MODULE: -	
 OxyChem Redstone Battleground PROJECT				PID: 202998C-001-PID-0021-0333				
				UNIT#: 6800	LEW AREA: 6820	SPEC: CTWL-CS01	STRESS CALC #: CN-0407	
				LINE No. 36"-R2-67160-CTWL-CS01-N				
				DRAWING NUMBER 6820-R2-67160-02			REV. 0	

