


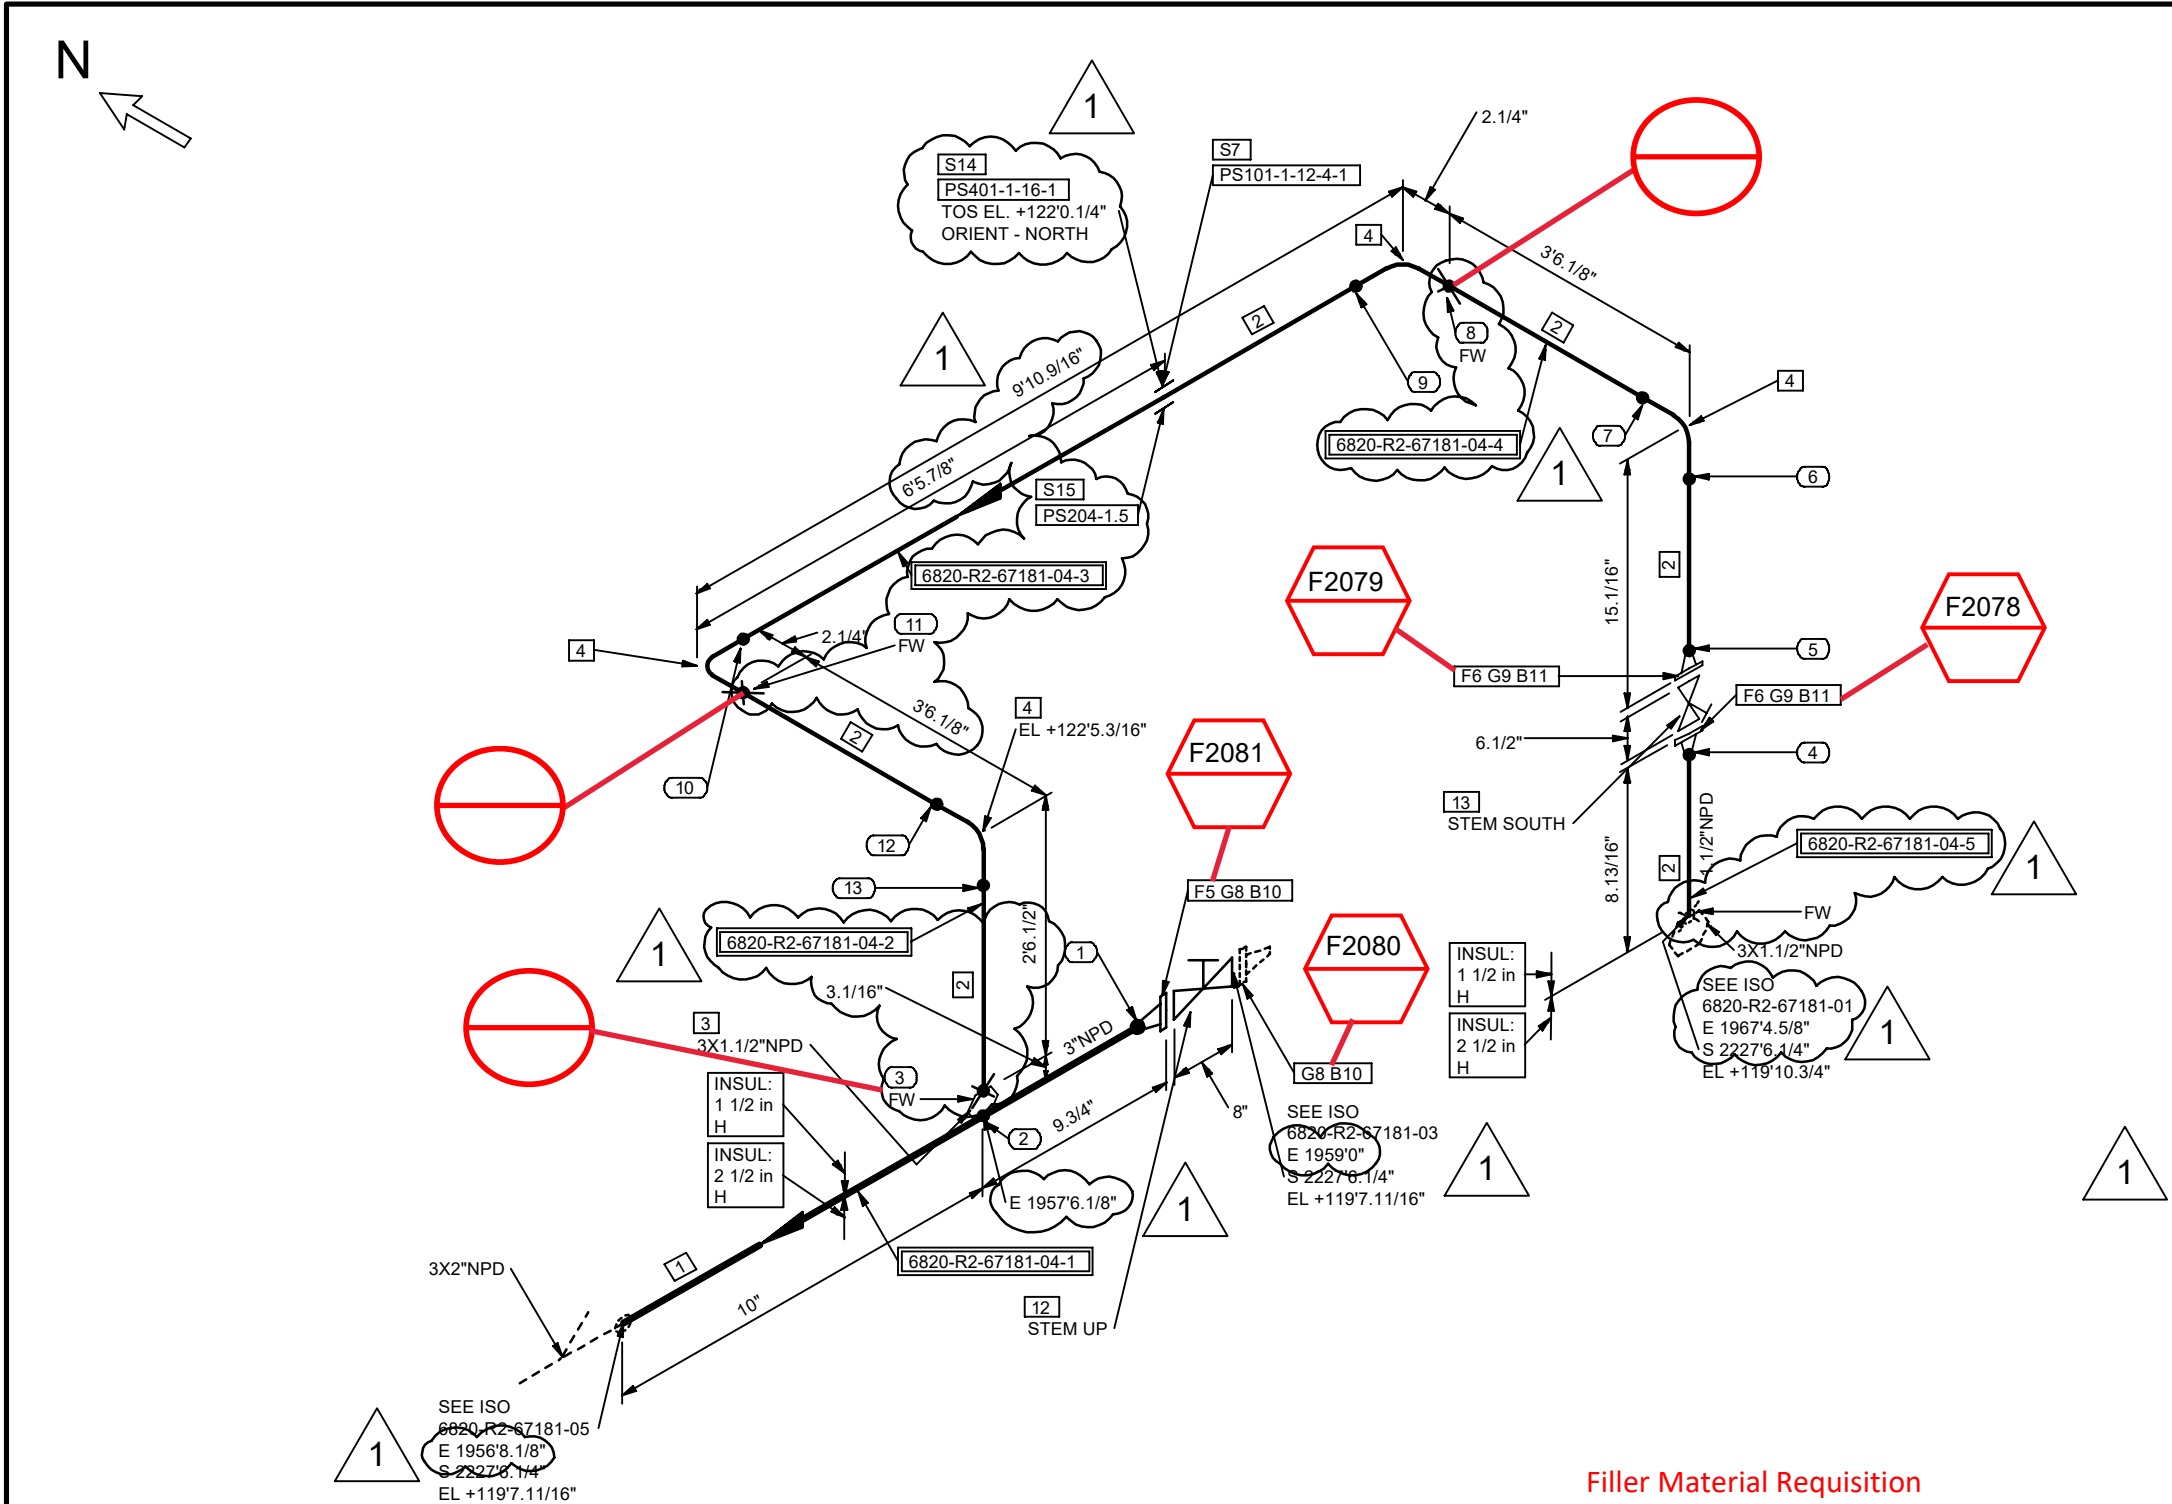

Filler Material Requisition

Date: 1-3-25
Line Class: SLPG-CS01
WPS: 10245
Electrode: ER70S-2
Signature: Pedro Morin

COORDINATE SYSTEM : PLANTCOORDINATES

- NOTES:
- FOR LINE PRESSURES, TEMPERATURES, INSULATION TYPE AND THICKNESS, ETC. REFER TO LATEST REVISION OF LDT.
 - FOR STANDARD PIPE SUPPORT DETAILS SEE PROJECT STANDARD.
 - FIELD SHIM TO SUIT UNLESS OTHERWISE NOTED.
 - FOR PWHT REQUIREMENTS REFER TO LINE CLASS SPECIFICATION.
 - ALL THREADED PIPE LINE SYSTEMS, FIELD SHALL VERIFY DIMENSION PRIOR TO ERECTION.
 - FFW DESIGNATION AT WELDS INDICATES FIELD FIT WELD, WHERE PIPE FABRICATOR IS TO ADD 9 INCH OF PIPE TO THE ISOMETRIC DIMENSION TO ENABLE THE FIELD TO CUT TO FIT AT SITE.
 - REFER TO 202998C-000-W1-1300-0001 FOR FRP AND DUAL-LAM FABRICATION.



Information contained in this document is the work product of one or more legal entities of Technip Energies N.V. and embodies confidential and proprietary information of the applicable entity and/or its client. Use of this information is restricted in accordance with conditions specified by the contract. Technip Energies N.V. and its affiliates disclaim any and all liabilities for any changes or modifications to this document which are made by any person other than the entity that issued the document under the applicable client contract.

THIS DOCUMENT IS UNCONTROLLED WHEN REPRODUCED

REV	DATE	BY	DESCRIPTION	CHKD	MTO	STRESS	APRVD
1	2024-12-20	RVA	ISSUED FOR CONSTRUCTION	SAD	KJK	SMR	GR
0	2024-08-09	RVA	ISSUED FOR CONSTRUCTION	SAD	KJK	SMR	GR

SHOP MATERIALS				
NO	NPD	DESCRIPTION	IDENT	QTY
1	3	Pipes, Seamless, ASME B36.10, ASTM A106 Gr.B, BE, -, -, S-STD	CPP002ZK	1.5'
2	1.1/2	Pipes, Seamless, ASME B36.10, ASTM A106 Gr.B, BE, -, -, S-XS	C2UE2CJ	20.0'
3	3X1.1/2	Weldolet, MSS SP-97, ASTM A105N, BW Ends, -, S-STD x S-XS	CTE2DXS	1
4	1.1/2	90° Elb LR, Seamless, ASME B16.9, ASTM A234 Gr.WPB, BW Ends, -, -, S-XS	C2UE494	4
5	3	WN Flg, ASME B16.5, ASTM A105N, 150 Lbs, RF/BW End, -, S-STD	CFG6WJDF	1
6	1.1/2	WN Flg, ASME B16.5, ASTM A105N, 150 Lbs, RF/BW End, -, S-XS	CFG6WJ14	2
PIPE SUPPORTS				
7	1.1/2	PS101-1-12-4-1	PS101	1
OTHER THAN SHOP MATERIALS				
NO	NPD	DESCRIPTION	IDENT	QTY
8	3	NM Flat Gk, Aramid Fiber Reinforced SBR, 150 Lbs, RF as per ASME B16.5, -, Thk=1/8in, -,	C7SM1YGT	2
9	1.1/2	NM Flat Gk, Aramid Fiber Reinforced SBR, 150 Lbs, RF as per ASME B16.5, -, Thk=1/8in, -,	C7SM1YGP	2
10	5/8	SBlt 2 HHx N, A193 Gr.B7/A194 Gr.2H, -, Xylan PTFE Coated, - 3.75 in. Length	C6S4K88S	8
11	1/2	SBlt 2 HHx N, A193 Gr.B7/A194 Gr.2H, -, Xylan PTFE Coated, - 3 in. Length	C6S4K87V	8
12	3	Gat Flg, -, API 600, ASTM A216 Gr.WCB, 150 Lbs, RF, Ends as per ASME B16.5, HO, -, Valve Tag: GA-0215	C76SPAB8	1
13	1.1/2	Gat Flg, -, API 600, ASTM A216 Gr.WCB, 150 Lbs, RF, Ends as per ASME B16.5, HO, -, Valve Tag: GA-0215	C7SNM2BC	1
PIPE SUPPORTS				
14	1.1/2	PS401-1-16-1	PS401	1
15	1.1/2	PS204-1.5	PS204	1
PIECE MARKS				
6820-R2-67181-04-1 6820-R2-67181-04-2 6820-R2-67181-04-3 6820-R2-67181-04-4 6820-R2-67181-04-5				



SERVICE:	VAPOR/LIQUID:	INSUL TYPE:	INSUL THK:	SHOP:	FIELD:	PAINT CODE:	MODULE:
R2	V	Per LDT	Per LDT	Y	Y	Per LDT	-
P&ID: 202998C-001-PID-0031-0995				UNIT#: 6800 EWP AREA: 6820 SPEC: SLPG-CS01 STRESS CALC #: CN-0479/CN-0493			
LINE No: 3"-R2-67181-SLPG-CS01-H				DRAWING NUMBER: 6820-R2-67181-04 REV: 1			

