



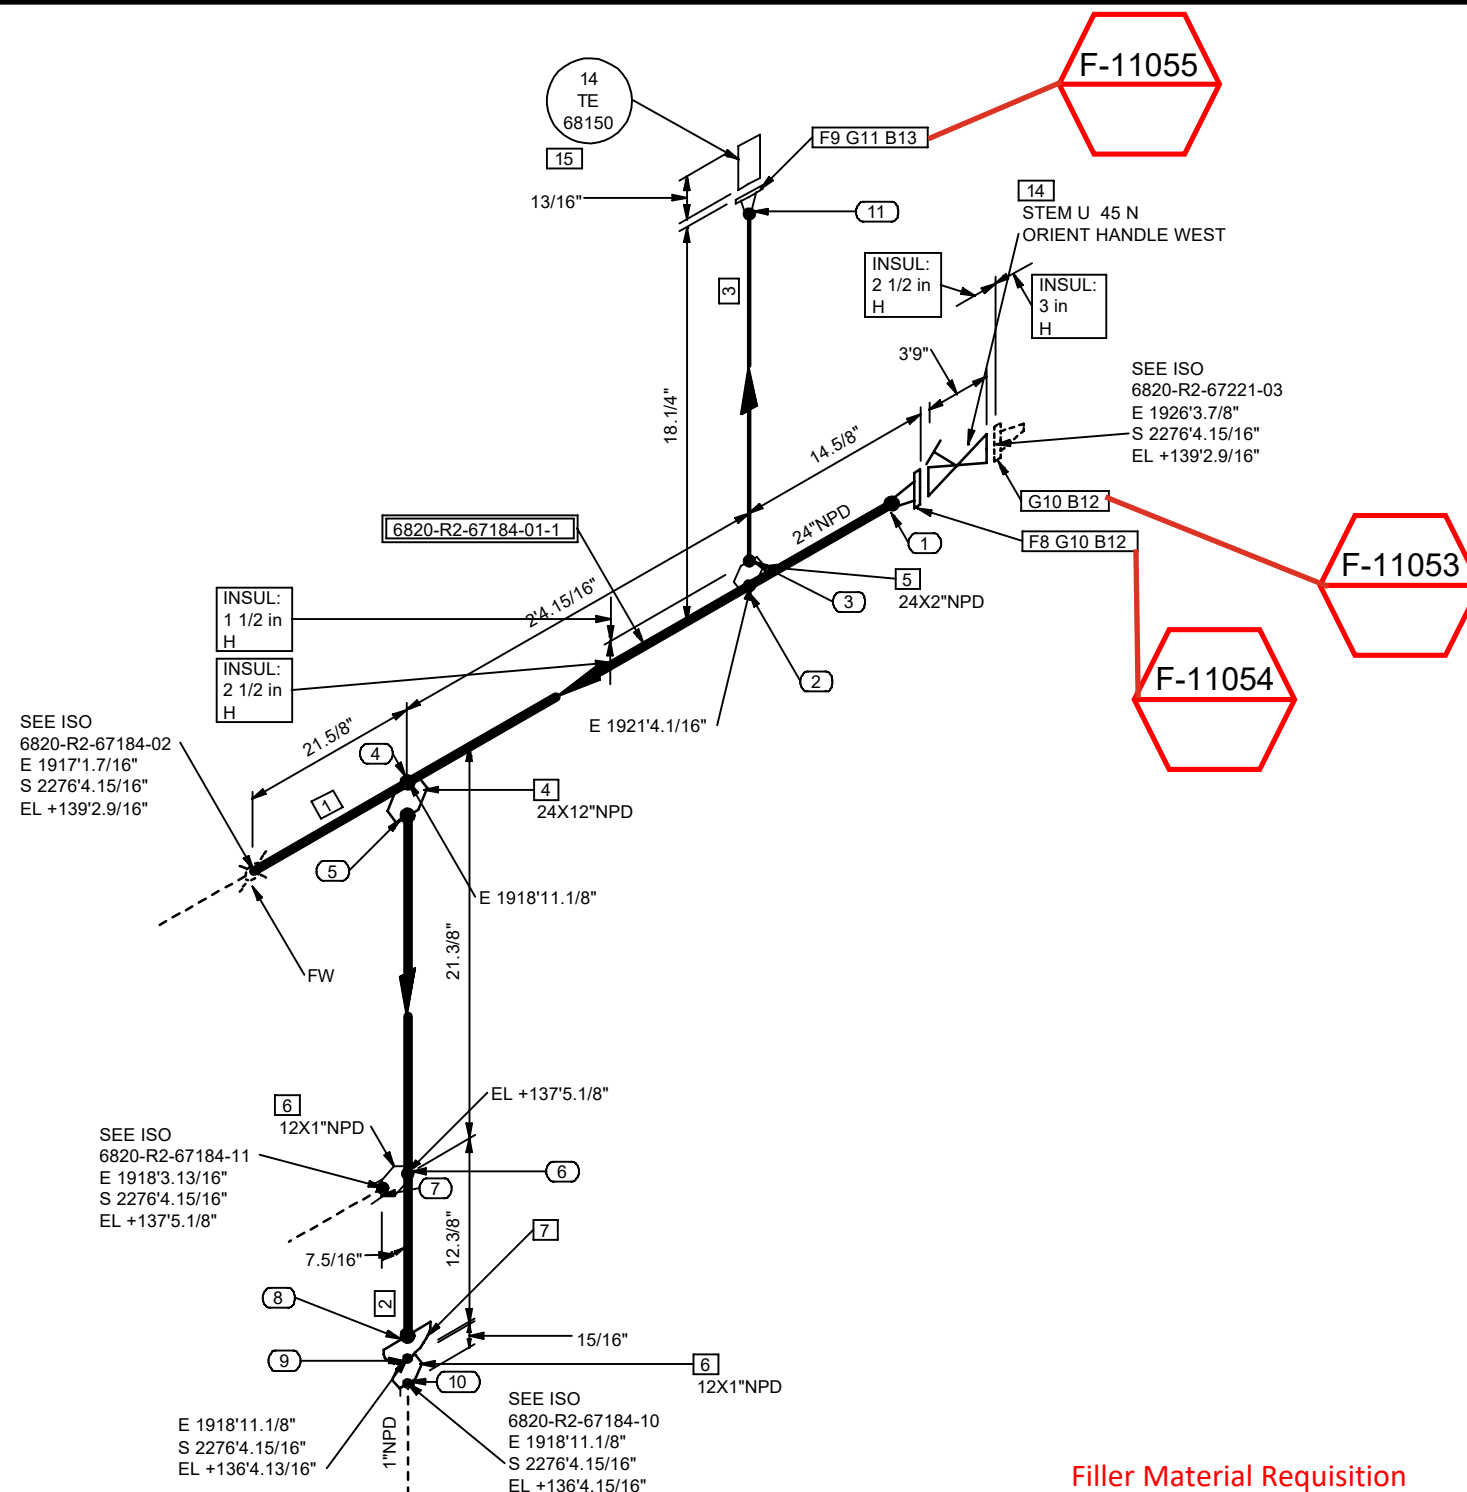

Date: 12-3-24  
Line Class: SIPG-CS01  
WPS: 10245  
Electrode: ER70S-2  
Signature: *Glenn Sumrall*

**NOTES:**

1. FOR LINE PRESSURES, TEMPERATURES, INSULATION TYPE AND THICKNESS, ETC. REFER TO LATEST REVISION OF LDT.
2. FOR STANDARD PIPE SUPPORT DETAILS SEE PROJECT STANDARD.
3. FIELD SHIM TO SUIT UNLESS OTHERWISE NOTED.
4. FOR PWHT REQUIREMENTS REFER TO LINE CLASS SPECIFICATION.
5. ALL THREADED PIPE LINE SYSTEMS, FIELD SHALL VERIFY DIMENSION PRIOR TO ERECTION.
6. FFW DESIGNATION AT WELDS INDICATES FIELD FIT WELD, WHERE PIPE FABRICATOR IS TO ADD 9 INCH OF PIPE TO THE ISOMETRIC DIMENSION TO ENABLE THE FIELD TO CUT TO FIT AT SITE.
7. REFER TO 202998C-000-W1-1300-0001 FOR FRP AND DUAL-LAM FABRICATION.

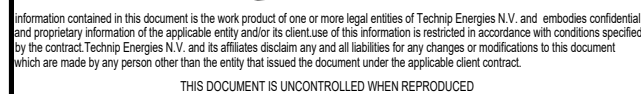

|     |            |     |                         |      |     |        |       |  |
|-----|------------|-----|-------------------------|------|-----|--------|-------|--|
|     |            |     |                         |      |     |        |       |  |
|     |            |     |                         |      |     |        |       |  |
| 0   | 2024-11-22 | RVA | ISSUED FOR CONSTRUCTION | SAD  | KJK | SMR    | GR    |  |
| REV | DATE       | BY  | DESCRIPTION             | CHKD | MTO | STRESS | APRVL |  |

PIECE MARKS  
6820-R2-67184-01-1

Turner Industries Group, LLC  
Received  
DECEMBER 03, 2024  
DOCUMENT CONTROL

|   |                    |                        |                       |                                      |                   |                        |                           |  |
|---|--------------------|------------------------|-----------------------|--------------------------------------|-------------------|------------------------|---------------------------|--|
| SERVICE:<br>R2   | VAPOR/LIQUID:<br>V | INSUL TYPE:<br>Per LDT | INSUL THK:<br>Per LDT | SHOP:<br>Y                           | FIELD:<br>Y       | PAINT CODE:<br>Per LDT | MODULE:<br>-              |  |
| <div></div> <div>OxyChem Redstone Battleground<br/>PROJECT</div> |                    |                        |                       | P&ID:<br>202998C-001-PID-0021-0320   |                   |                        |                           |  |
|   |                    |                        |                       | UNIT#:<br>6800                       | SWP AREA:<br>6820 | SPEC:<br>SIPG-CS01     | STRESS CALC #:<br>CN-0023 |  |
|   |                    |                        |                       | LINE No.<br>24"-R2-67184-SIPG-CS01-H |                   |                        |                           |  |
|   |                    |                        |                       | DRAWING NUMBER<br>6820-R2-67184-01   |                   |                        | REV.<br>0                 |  |
|   |                    |                        |                       |                                      |                   |                        |                           |  |