



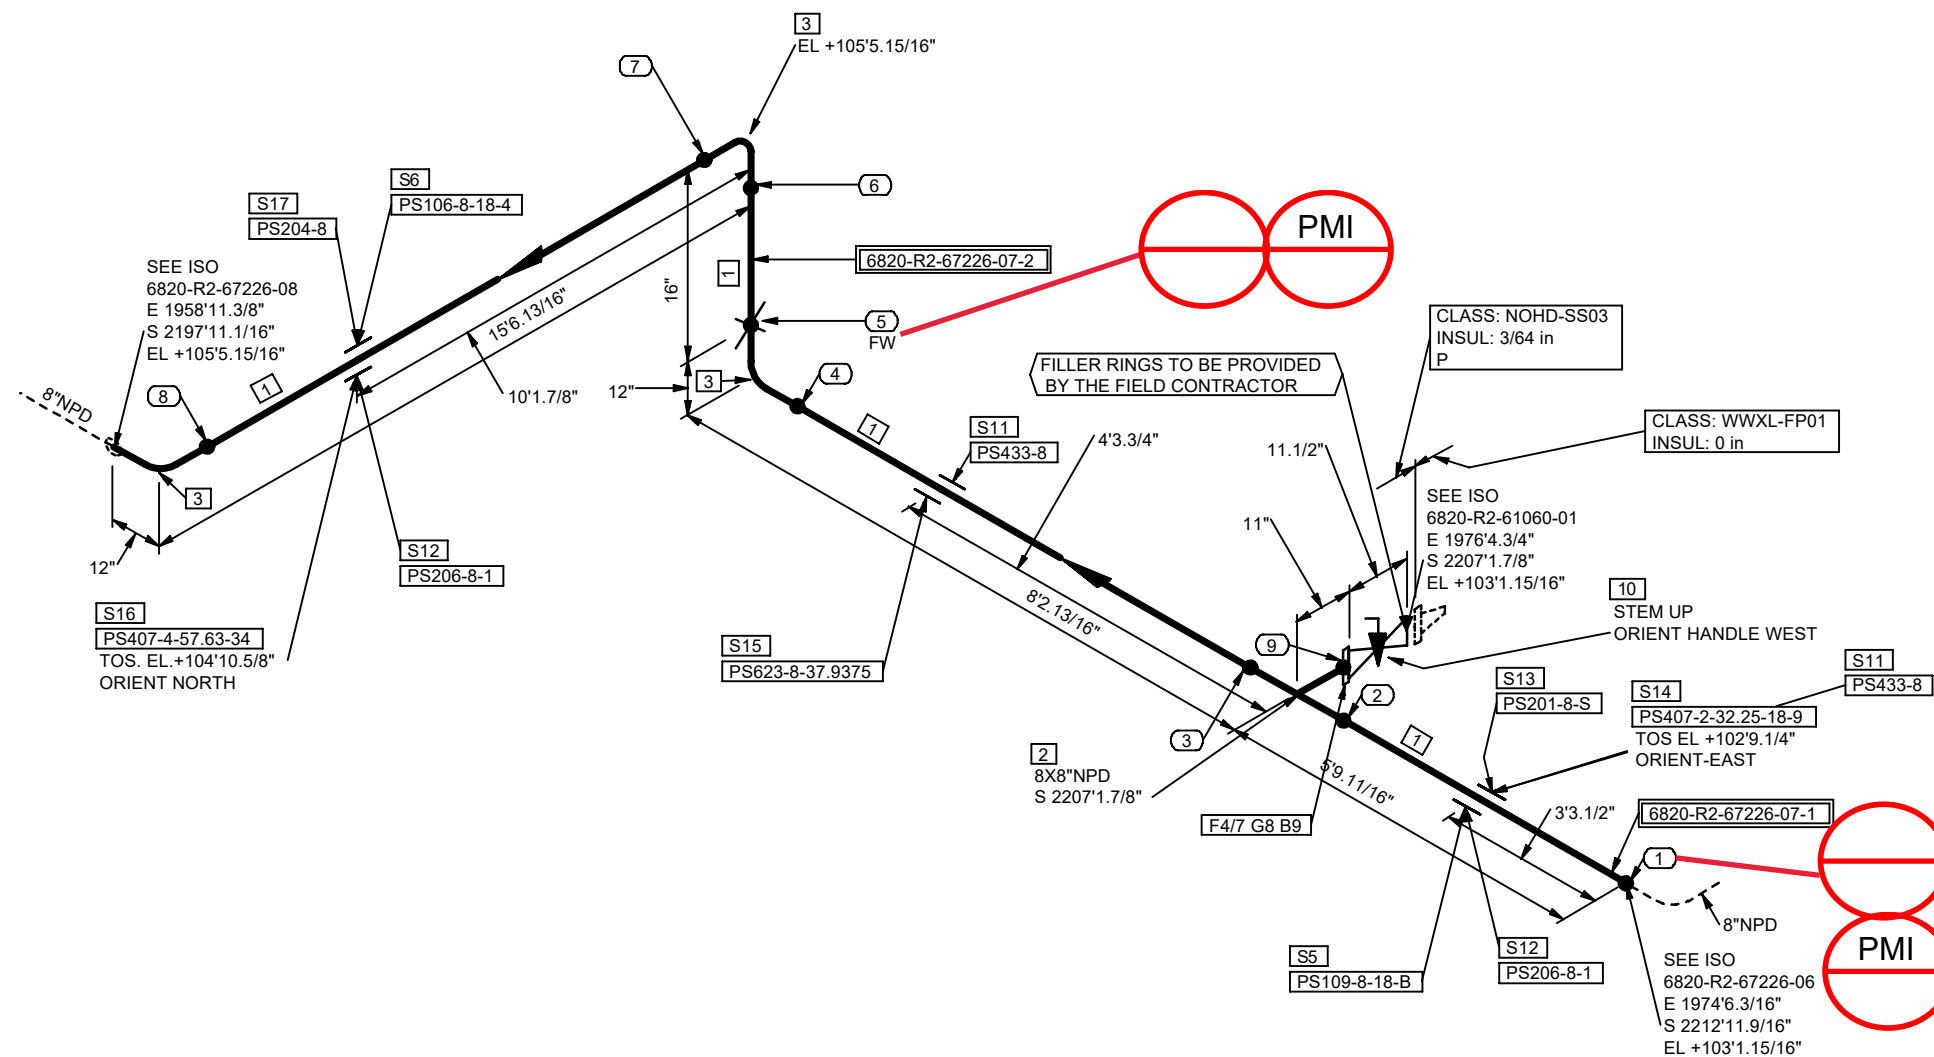

NOTES:

1. FOR LINE PRESSURES, TEMPERATURES, INSULATION TYPE AND THICKNESS, ETC. REFER TO LATEST REVISION OF LDT.
2. FOR STANDARD PIPE SUPPORT DETAILS SEE PROJECT STANDARD.
3. FIELD SHIM TO SUIT UNLESS OTHERWISE NOTED.
4. FOR PWHT REQUIREMENTS REFER TO LINE CLASS SPECIFICATION.
5. ALL THREADED PIPE LINE SYSTEMS, FIELD SHALL VERIFY DIMENSION PRIOR TO ERECTION.
6. FFW DESIGNATION AT WELDS INDICATES FIELD FIT WELD, WHERE PIPE FABRICATOR IS TO ADD 9 INCH OF PIPE TO THE ISOMETRIC DIMENSION TO ENABLE THE FIELD TO CUT TO FIT AT SITE.
7. REFER TO 202998C-000-W1-1300-0001 FOR FRP AND DUAL-LAM FABRICATION.

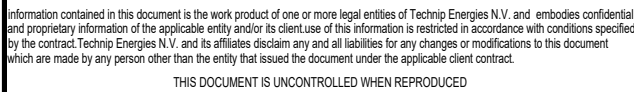

0	2024-11-08	RVA	ISSUED FOR CONSTRUCTION	SAD	KJK	SMR	GR
REV	DATE	BY	DESCRIPTION	CHKD	MTO	STRESS	APRVD

Date: 11-12-24

Line Class: NOHD-SS03

WPS: 802

Electrode: ER308L

Signature: *Glenn Sumrall*

PIPE SUPPORTS				
11	8	PS433-8	PS433	2
12	8	PS206-8-1	PS206	2
13	8	PS201-8-S	PS201	1
14	8	PS407-2-32.25-18-9	PS407	1
15	8	PS623-8-37.9375	PS623	1
16	8	PS407-4-57.63-34	PS407	1
17	8	PS204-8	PS204	1

6820-R2-67226-07-1 6820-R2-67226-07-2

