


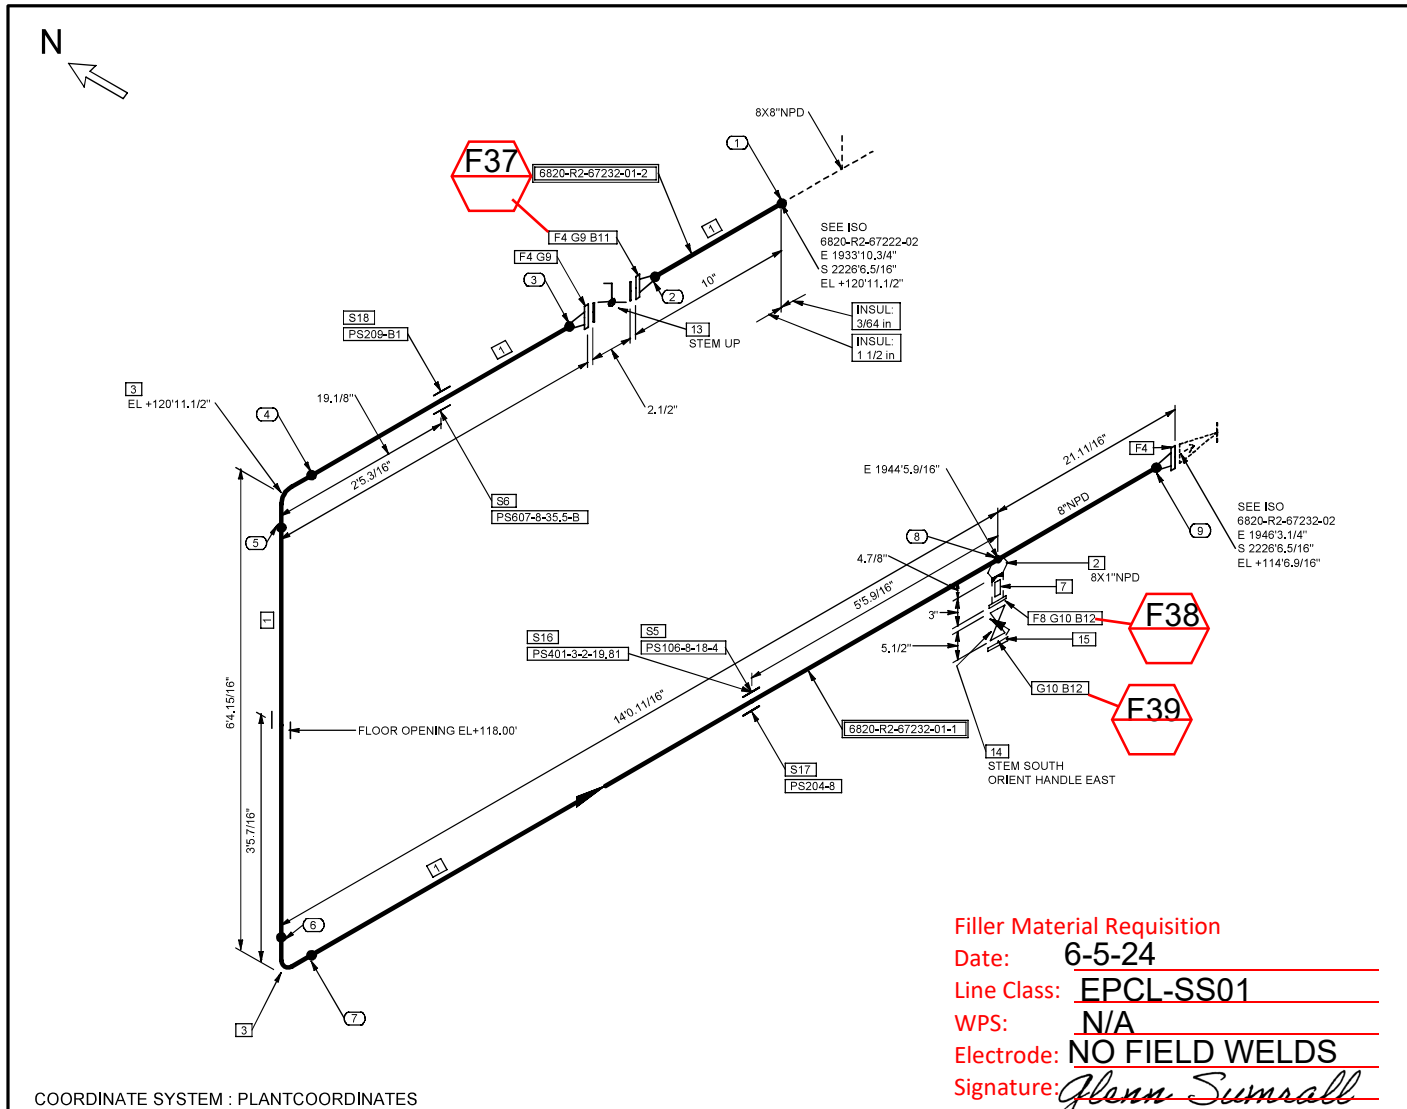

Filler Material Requisition
Date: 6-5-24
Line Class: EPCL-SS01
WPS: N/A
Electrode: NO FIELD WELDS
Signature: *Glenn Sumrall*

SHOP MATERIALS							
NO	NPD	DESCRIPTION	IDENT	QTY			
1	8	Pipes, Seamless, ASME B36,19/B36,10, ASTM A312 Gr,TP304L, BE, -, -, S-10S	C7FCT25	20.6			
2	8X1	Threadolet, ASTM A182 Gr,F304L, 3000 Lbs, NPTF Ends, -, Annealed,	C7BP7RN7	1			
3	8	90° Elb LR, Seamless, ASME B16.9, ASTM A403 Gr,WP304L, BW Ends, -, Annealed, S-10S	C6SEUJRF	2			
4	8	WN Flg, ASME B16.5, ASTM A182 Gr,F304L, 150 Lbs, RF/BW End, Annealed, S-10S	C7W2U6T4	3			
PIPE SUPPORTS							
5	8	PS106-8-18-4	PS106	1			
6	8	PS607-8-35.5-B	PS607	1			
OTHER THAN SHOP MATERIALS							
NO	NPD	DESCRIPTION	IDENT	QTY			
7	1	Nipple, ASTM A312 Gr,TP304L, NPTM Ends, L = 3in, -, S-80S	CEZMKL0	1			
8	1	THD Flg, ASME B16.5, ASTM A182 Gr,F304L, 150 Lbs, RF/NPTF End, Annealed,	C7W2U48L	1			
9	8	NM Flat Gk, Barium Sulfate filled PTFE, 150 Lbs, RF as per ASME B16.5, Full Face, Thk=1/8in, -, Annealed,	C7CT1ZG2	2			
10	1	NM Flat Gk, Barium Sulfate filled PTFE, 150 Lbs, RF as per ASME B16.5, Full Face, Thk=1/8in, -, Annealed,	C7CT1ZFH	2			
11	3/4	SBH 2 Hhix N, A193 Gr,B7/A194 Gr,2H, -, Xylan PTFE Coated, -, 7.25 in, Length	C6S4K8BR	8			
12	1/2	SBH 2 Hhix N, A193 Gr,B7/A194 Gr,2H, -, Xylan PTFE Coated, -, 2.75 in, Length	C6S4K87U	8			
13	8	But Waf, API 609 Cat,B, ASTM A351 Gr,CF8M, 150 Lbs, Lug-type RF, Ends as per ASME B16.5, GO, -, Valve Tag: BU-1191	C8PLE444	1			
14	1	Plug Flg,SP, Tapered Plug, Non Lubricated, API 599, ASTM A351 Gr,CF8M, 150 Lbs, RF, Ends as per ASME B16.5, -, LO, -, Valve Tag: PL-0548	C76KHSRR	1			
15	1	Bld Flg, ASME B16.5, ASTM A182 Gr,F304L, 150 Lbs, RF, Annealed,	C7W2U478	1			
PIPE SUPPORTS							
16	8	PS401-3-2-19.81	PS401	1			
17	8	PS204-8	PS204	1			
18	8	PS209-B1	PS209	1			
PIECE MARKS							
6820-R2-67232-01-1 6820-R2-67232-01-2							
Turner Industries Group, LLC Received June 4, 2024 DOCUMENT CONTROL							
SERVICE	VAPOR/LIQUID	INSUL TYPE	INSUL THK	SHOP	FIELD	PAINT CODE	MODULE
R2	L	Per LDT	Per LDT	Y	N	Per LDT	-
202998C-001-PID-0021-0331							
UNIT#		WVP AREA		SPEC		STRESS CALC#	
6800		6820		EPCL-SS01		NC	
8"-R2-67232-EPCL-SS01-H							
DRAWMING NUMBER							
6820-R2-67232-01							
OxyChem Redstone Battleground PROJECT							
REV	DATE	BY	DESCRIPTION	CHKD	MTO	STRESS	APRVD
0	17/05/2024	RVA	ISSUED FOR CONSTRUCTION	SAD	KJK	BRD	GR
THIS DOCUMENT IS UNCONTROLLED WHEN REPRODUCED							

NOTES:
1. FOR LINE PRESSURES, TEMPERATURES, INSULATION TYPE AND THICKNESS, ETC. REFER TO LATEST REVISION OF LDT.
2. FOR STANDARD PIPE SUPPORT DETAILS SEE PROJECT STANDARD.
3. FIELD SHIM TO SUIT UNLESS OTHERWISE NOTED.
4. FOR PAINT REQUIREMENTS REFER TO LINE CLASS SPECIFICATION.
5. ALL THREADED PIPE LINE SYSTEMS, FIELD SHALL VERIFY DIMENSION PRIOR TO ERECTION.
6. FFW DESIGNATION AT WELDS INDICATES FIELD FIT WELD, WHERE PIPE FABRICATOR IS TO ADD 9 INCH OF PIPE TO THE ISOMETRIC DIMENSION TO ENABLE THE FIELD TO CUT TO FIT AT SITE.

TEN TECHNIP ENERGIES
Information contained in this document is the work product of one or more legal entities of Technip Energies N.V. and embodies confidential and proprietary information of the applicable entity and/or its client. Use of this information is restricted in accordance with conditions specified by the contract. Technip Energies N.V. and its affiliates disclaim any and all liabilities for any changes or modifications to this document which are made by any person other than the entity that issued the document under the applicable client contract.
THIS DOCUMENT IS UNCONTROLLED WHEN REPRODUCED

0	17/05/2024	RVA	ISSUED FOR CONSTRUCTION	SAD	KJK	BRD	GR
REV	DATE	BY	DESCRIPTION	CHKD	MTO	STRESS	APRVD

