


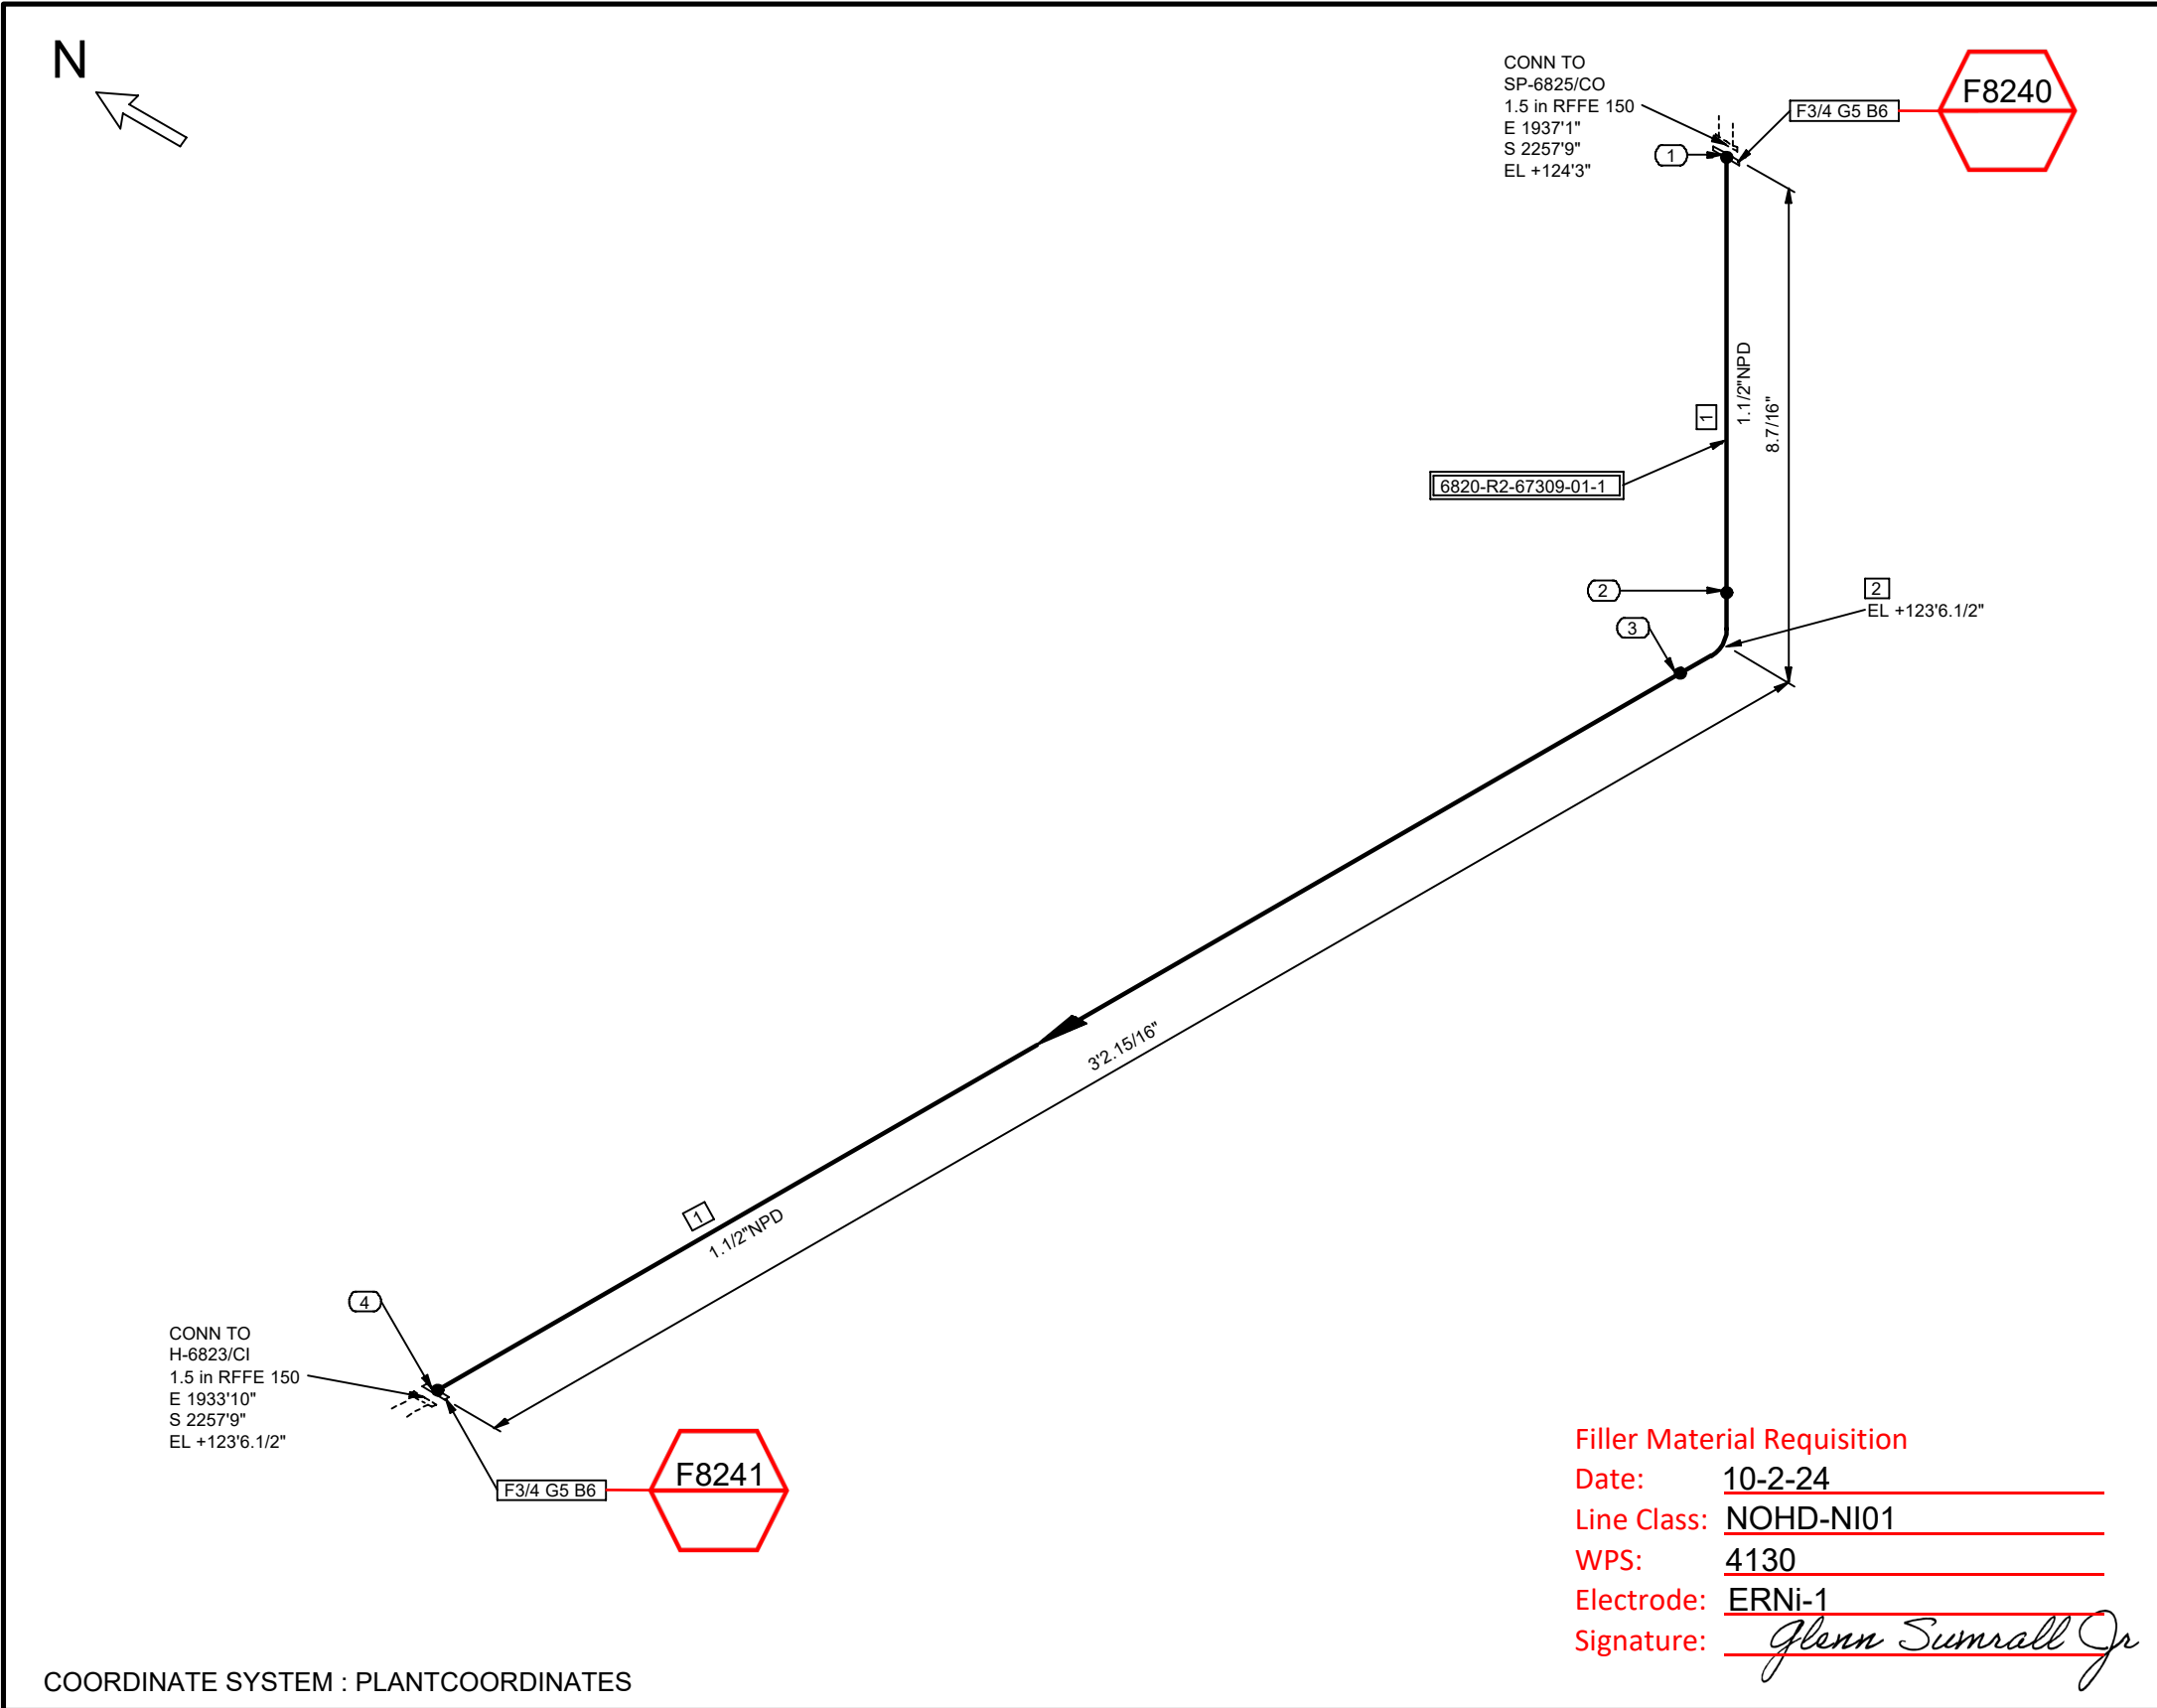

SHOP MATERIALS					
NO	NPD	DESCRIPTION	IDENT	QTY	
1	1.1/2	Pipes, Seamless, ASME B36.19/B36.10, ASTM B161 UNS N02200, BE, -, -, S-10S	C7ZWWMRJ	3.3	'
2	1.1/2	90° Elb LR, Seamless, ASME B16.9, ASTM B366 Gr.WPN, BW Ends, -,Annealed, S-10S	C7ZWWZKF	1	
3	1.1/2	LJ Flg, ASME B16.5, ASTM A105 Galv. as per ASTM A153, 150 Lbs, FF, -,	C26WFFF9	2	
MISCELLANEOUS COMPONENTS					
4	1.1/2	Stub SP, Seamless, ASME B16.9, ASTM B366 Gr.WPN, BW Ends, -,Annealed, x S-10S	C8A5GXPV	2	
OTHER THAN SHOP MATERIALS					
NO	NPD	DESCRIPTION	IDENT	QTY	
5	1.1/2	NM Flat Gk, Barium Sulfate filled PTFE, 150 Lbs, RF as per ASME B16.5, -, Thk=1/8in, -,	C6S4K87H	2	
6	1/2	SBlt 2 HHx N, A193 Gr.B7/A194 Gr.2H, -, Xylan PTFE Coated, - 3 in. Length	C6S4K87V	8	
PIECE MARKS					
6820-R2-67309-01-1					
Turner Industries Group, LLC Received OCTOBER 01, 2024 DOCUMENT CONTROL					

SERVICE:	VAPOR/LIQUID:	INSUL TYPE:	INSUL THK:	SHOP:	FIELD:	PAINT CODE:	MODULE:
R2	L	Per LDT	Per LDT	Y	Y	Per LDT	-

 OxyChem Redstone Battleground PROJECT		P&ID: 202998C-001-PID-0021-0326	
		UNIT#: 6800	STRESS CALC #: -
		EWPA AREA: 6820	SPEC: NOHD-NI01
		LINE No: 1.5"-R2-67309-NOHD-NI01-H	
DRAWING NUMBER 6820-R2-67309-01		REV. 0	

NOTES:

1. FOR LINE PRESSURES, TEMPERATURES, INSULATION TYPE AND THICKNESS, ETC. REFER TO LATEST REVISION OF LDT.

2. FOR STANDARD PIPE SUPPORT DETAILS SEE PROJECT STANDARD.

3. FIELD SHIM TO SUIT UNLESS OTHERWISE NOTED.

4. FOR PWHT REQUIREMENTS REFER TO LINE CLASS SPECIFICATION.

5. ALL THREADED PIPE LINE SYSTEMS, FIELD SHALL VERIFY DIMENSION PRIOR TO ERECTION.

6. FFW DESIGNATION AT WELDS INDICATES FIELD FIT WELD, WHERE PIPE FABRICATOR IS TO ADD 9 INCH OF PIPE TO THE ISOMETRIC DIMENSION TO ENABLE THE FIELD TO CUT TO FIT AT SITE.

7. REFER TO 202998C-000-W1-1300-0001 FOR FRP AND DUAL-LAM FABRICATION.



TECHNIP
ENERGIES

Information contained in this document is the work product of one or more legal entities of Technip Energies N.V. and embodies confidential and proprietary information of the applicable entity and/or its client. Use of this information is restricted in accordance with conditions specified by the contract. Technip Energies N.V. and its affiliates disclaim any and all liabilities for any changes or modifications to this document which are made by any person other than the entity that issued the document under the applicable client contract.

THIS DOCUMENT IS UNCONTROLLED WHEN REPRODUCED

0	2024-09-26	RVA	ISSUED FOR CONSTRUCTION	SAD	KJK	SMR	GR		
REV	DATE	BY	DESCRIPTION	CHKD	MTO	STRESS	APRVD		

