


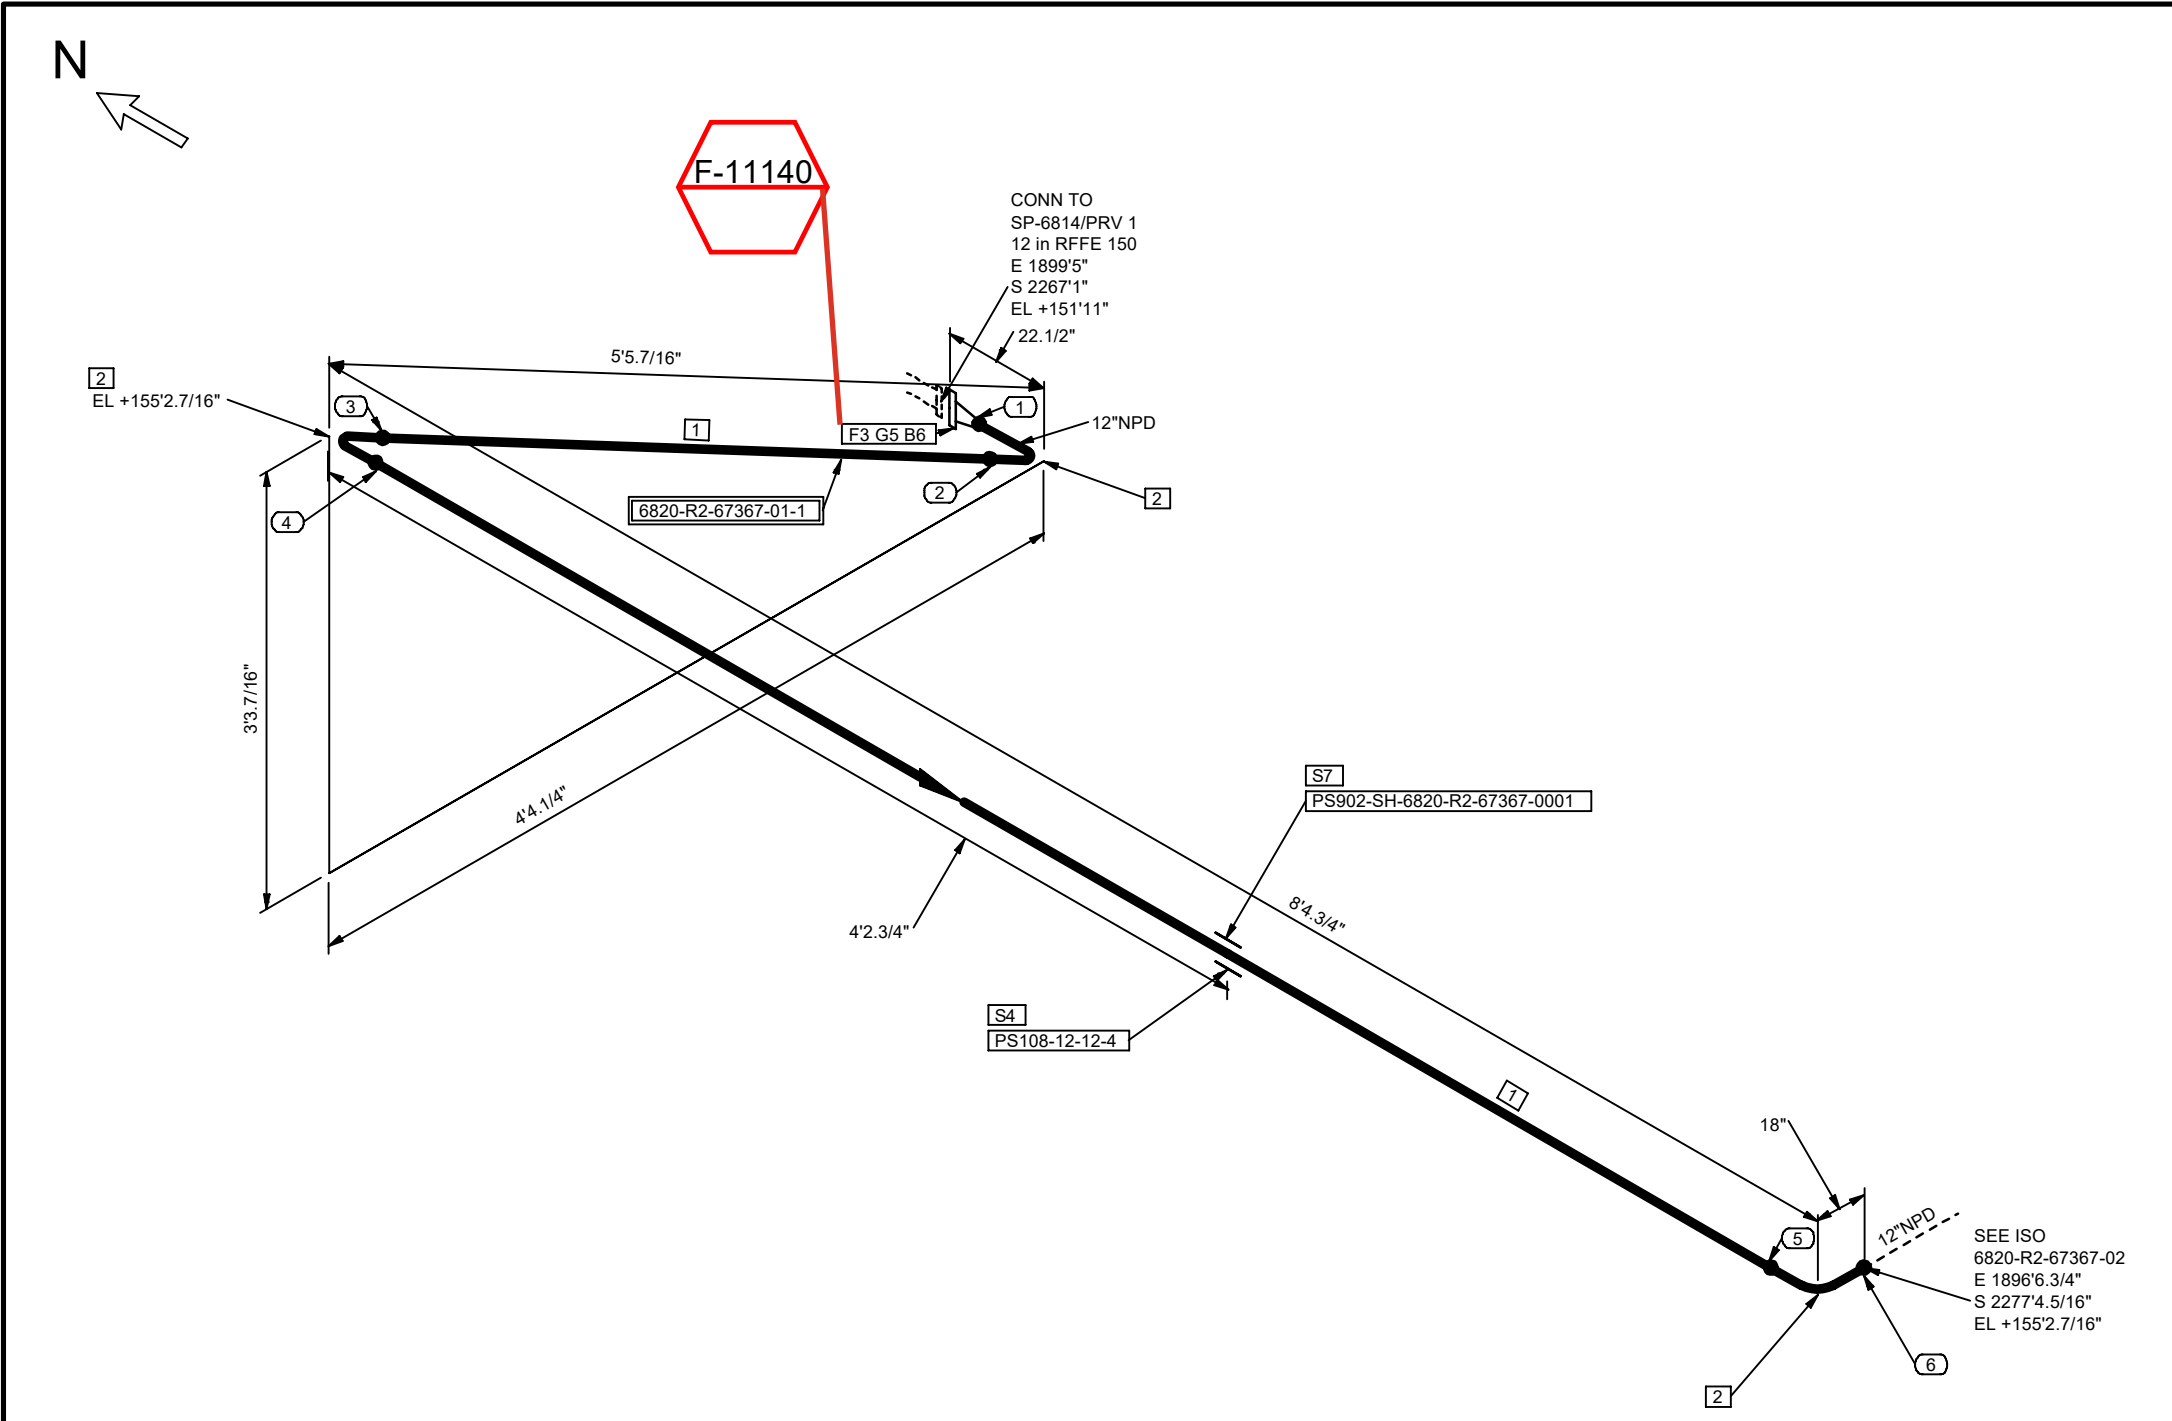

Filler Material Requisition

Date: 12-3-24  
Line Class: SLPG-CS01  
WPS: 10245  
Electrode: ER70S-2  
Signature: *Glenn Sumrall Jr*

SHOP MATERIALS

| NO | NPD | DESCRIPTION                                                              | IDENT    | QTY   |
|----|-----|--------------------------------------------------------------------------|----------|-------|
| 1  | 12  | Pipes, Seamless, ASME B36.10, ASTM A106 Gr.B, BE, -, -, S-STD            | CPP0AATK | 7.9 ' |
| 2  | 12  | 90° Elb LR, Seamless, ASME B16.9, ASTM A234 Gr.WPB, BW Ends, -, -, S-STD | CDB66G82 | 3     |
| 3  | 12  | WN Flg, ASME B16.5, ASTM A105N, 150 Lbs, RF/BW End, -, S-STD             | CFG6WJ3S | 1     |

PIPE SUPPORTS

|   |    |               |       |   |
|---|----|---------------|-------|---|
| 4 | 12 | PS108-12-12-4 | PS108 | 1 |
|---|----|---------------|-------|---|

OTHER THAN SHOP MATERIALS

| NO | NPD | DESCRIPTION                                                                              | IDENT    | QTY |
|----|-----|------------------------------------------------------------------------------------------|----------|-----|
| 5  | 12  | NM Flat Gk, Aramid Fiber Reinforced SBR, 150 Lbs, RF as per ASME B16.5, -, Thk=1/8in, -, | C7SMNYW5 | 1   |
| 6  | 7/8 | SBlt 2 HHx N, A193 Gr.B7/A194 Gr.2H, -, Xylan PTFE Coated, - 5 in. Length                | C6S4K8CU | 12  |

PIPE SUPPORTS

|   |    |                             |       |   |
|---|----|-----------------------------|-------|---|
| 7 | 12 | PS902-SH-6820-R2-67367-0001 | PS902 | 1 |
|---|----|-----------------------------|-------|---|

PIECE MARKS

6820-R2-67367-01-1

COORDINATE SYSTEM : PLANTCOORDINATES

|   |
|---|
| NOTES:   |
| 1. FOR LINE PRESSURES, TEMPERATURES, INSULATION TYPE AND THICKNESS, ETC. REFER TO LATEST REVISION OF LDT.                                                                  |
| 2. FOR STANDARD PIPE SUPPORT DETAILS SEE PROJECT STANDARD.   |
| 3. FIELD SHIM TO SUIT UNLESS OTHERWISE NOTED.   |
| 4. FOR PWHT REQUIREMENTS REFER TO LINE CLASS SPECIFICATION.   |
| 5. ALL THREADED PIPE LINE SYSTEMS, FIELD SHALL VERIFY DIMENSION PRIOR TO ERECTION.                                                                                         |
| 6. FFW DESIGNATION AT WELDS INDICATES FIELD FIT WELD, WHERE PIPE FABRICATOR IS TO ADD 9 INCH OF PIPE TO THE ISOMETRIC DIMENSION TO ENABLE THE FIELD TO CUT TO FIT AT SITE. |
| 7. REFER TO 202998C-000-W1-1300-0001 FOR FRP AND DUAL-LAM FABRICATION.   |

|                                               |   |
|-----------------------------------------------|---|
|                                               | Information contained in this document is the work product of one or more legal entities of Technip Energies N.V. and embodies confidential and proprietary information of the applicable entity and/or its client. Use of this information is restricted in accordance with conditions specified by the contract. Technip Energies N.V. and its affiliates disclaim any and all liabilities for any changes or modifications to this document which are made by any person other than the entity that issued the document under the applicable client contract. |
| THIS DOCUMENT IS UNCONTROLLED WHEN REPRODUCED |   |

| 0   | 2024-11-22 | RVA | ISSUED FOR CONSTRUCTION | SAD  | KJK | SMR    | GR    |
|-----|------------|-----|-------------------------|------|-----|--------|-------|
| REV | DATE       | BY  | DESCRIPTION             | CHKD | MTO | STRESS | APRVD |

|   |                    |                        |                       |                                       |                   |                        |                           |  |
|---|--------------------|------------------------|-----------------------|---------------------------------------|-------------------|------------------------|---------------------------|--|
| SERVICE:<br>R2   | VAPOR/LIQUID:<br>L | INSUL TYPE:<br>Per LDT | INSUL THK:<br>Per LDT | SHOP:<br>Y                            | FIELD:<br>Y       | PAINT CODE:<br>Per LDT | MODULE:<br>-              |  |
| <div></div> <div>OxyChem Redstone Battleground<br/>PROJECT</div> |                    |                        |                       | P&ID:<br>202998C-001-PID-0021-0324    |                   |                        |                           |  |
|   |                    |                        |                       | UNIT#:<br>6800                        | EWP AREA:<br>6820 | SPEC:<br>SLPG-CS01     | STRESS CALC #:<br>CN-0411 |  |
|   |                    |                        |                       | LINE No.<br>12"-R2-67367-S LPG-CS01-P |                   |                        |                           |  |
|   |                    |                        |                       | DRAWING NUMBER<br>6820-R2-67367-01    |                   |                        |                           |  |
|   |                    |                        |                       | REV.<br>0                             |                   |                        |                           |  |

