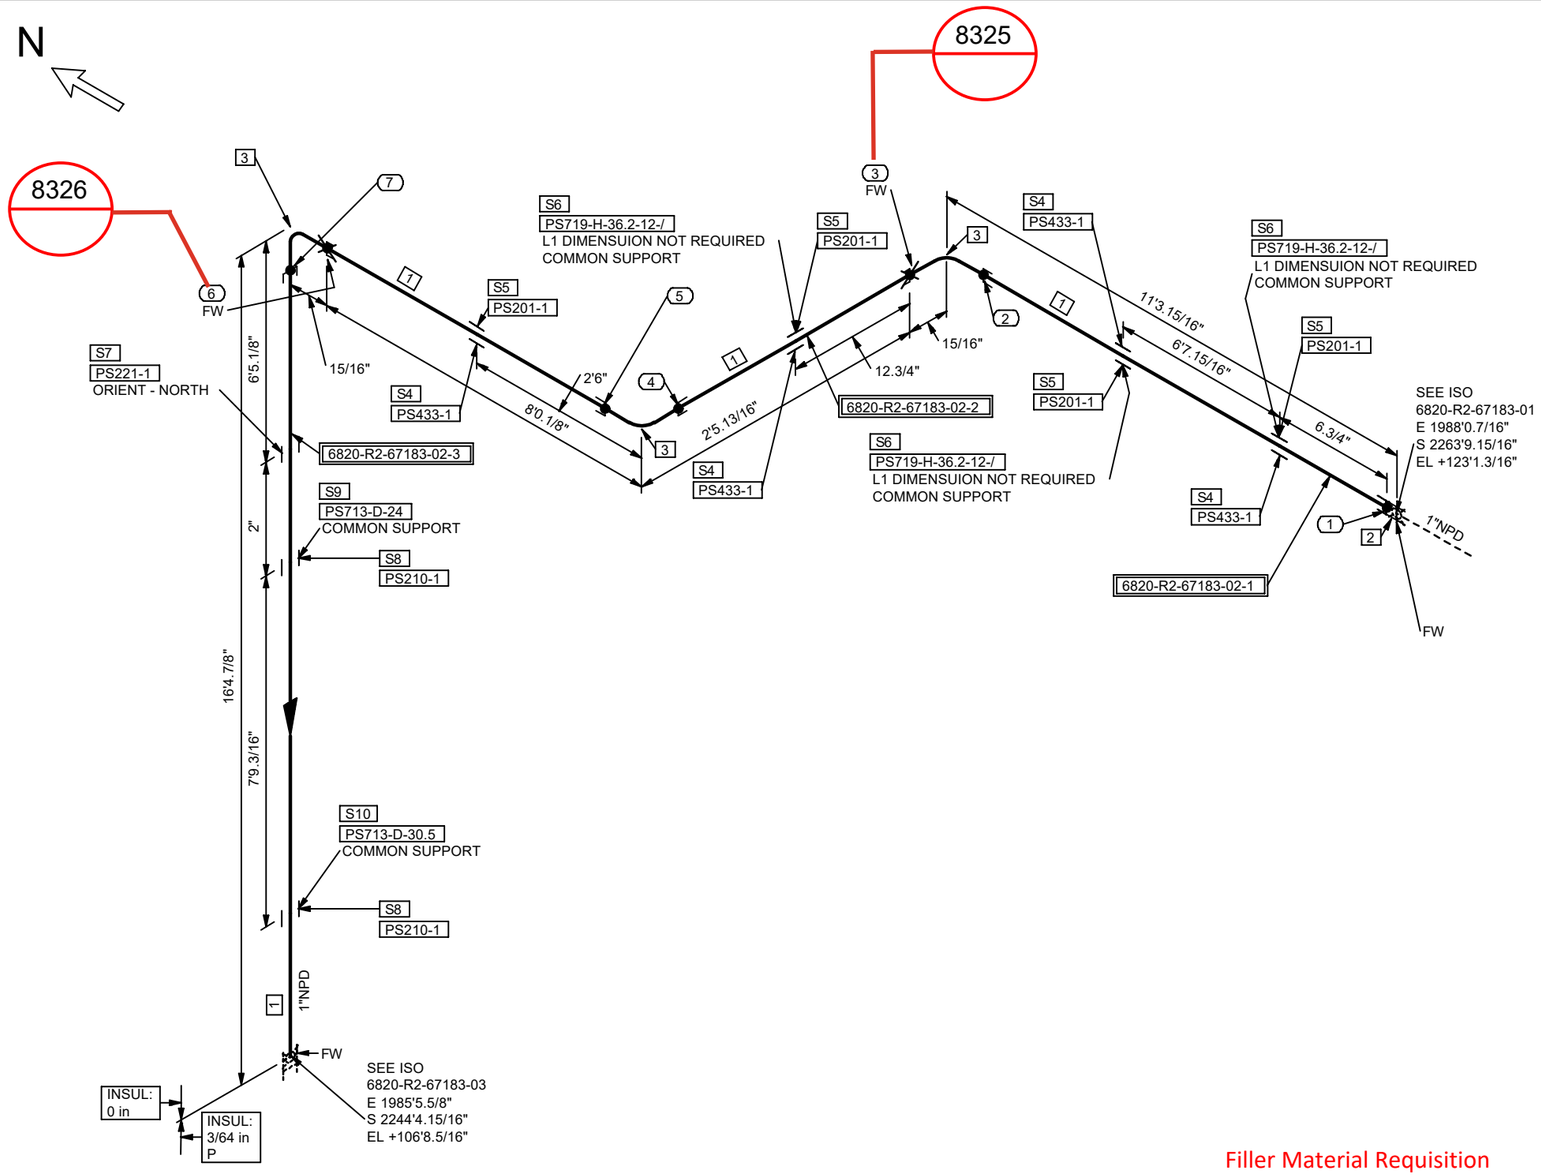


COORDINATE SYSTEM : PLANTCOORDINATES

SHOP MATERIALS

NO	NPD	DESCRIPTION	IDENT	QTY
1	1	Pipes, Seamless, ASME B36.10, ASTM A106 Gr.B, PE, -, -, S-XS	CPP0AMKL	37.9 '
2	1	Full Coup, ASME B16.11, ASTM A105N, 3000 Lbs, SW Ends, -,	CDF6FZ0N	1
3	1	90° Elb, ASME B16.11, ASTM A105N, 3000 Lbs, SW Ends, -,	CDF66G5D	3

OTHER THAN SHOP MATERIALS

NO	NPD	DESCRIPTION	IDENT	QTY
		PIPE SUPPORTS		
4	1	PS433-1	PS433	4
5	1	PS201-1	PS201	4
6	1	PS719-H-36.2-12-/	PS719	3
7	1	PS221-1	PS221	1
8	1	PS210-1	PS210	2
9	1	PS713-D-24	PS713	1
10	1	PS713-D-30.5	PS713	1

PIECE MARKS

6820-R2-67183-02-1 6820-R2-67183-02-2 6820-R2-67183-02-3

Filler Material Requisition
Date: 2-26-25
Line Class: SCXL-CS01
WPS: 10245
Electrode: ER70S-2
Signature: Glenn Sumrall Jr

Turner Industries Group, LLC
Received
FEBRUARY 26,2025
DOCUMENT CONTROL

NOTES:
1. FOR LINE PRESSURES, TEMPERATURES, INSULATION TYPE AND THICKNESS, ETC. REFER TO LATEST REVISION OF LDT.
2. FOR STANDARD PIPE SUPPORT DETAILS SEE PROJECT STANDARD.
3. FIELD SHIM TO SUIT UNLESS OTHERWISE NOTED.
4. FOR PWHT REQUIREMENTS REFER TO LINE CLASS SPECIFICATION.
5. ALL THREADED PIPE LINE SYSTEMS, FIELD SHALL VERIFY DIMENSION PRIOR TO ERECTION.
6. FFW DESIGNATION AT WELDS INDICATES FIELD FIT WELD, WHERE PIPE FABRICATOR IS TO ADD 9 INCH OF PIPE TO THE ISOMETRIC DIMENSION TO ENABLE THE FIELD TO CUT TO FIT AT SITE.
7. REFER TO 202998C-000-W1-1300-0001 FOR FRP AND DUAL-LAM FABRICATION.

TECHNIP ENERGIES

information contained in this document is the work product of one or more legal entities of Technip Energies N.V. and embodies confidential and proprietary information of the applicable entity and/or its client.use of this information is restricted in accordance with conditions specified by the contract.Technip Energies N.V. and its affiliates disclaim any and all liabilities for any changes or modifications to this document which are made by any person other than the entity that issued the document under the applicable client contract.
THIS DOCUMENT IS UNCONTROLLED WHEN REPRODUCED

REV	DATE	BY	DESCRIPTION	CHKD	MTO	STRESS	APRVD
0	2025-02-21	RVA	ISSUED FOR CONSTRUCTION	SAD	KJK	SMK	GR

SERVICE:	VAPOR/LIQUID:	INSUL TYPE:	INSUL THK:	SHOP:	FIELD:	PAINT CODE:	MODULE:
R2	L	Per LDT	Per LDT	Y	Y	Per LDT	-

OXY
OxyChem Redstone Battleground
PROJECT

P&ID: 202998C-001-PID-0021-0335
UNIT#: 6800 | EWP AREA: 6820 | SPEC: SCXL-CS01 | STRESS CALC #:
LINE No.: 1"-R2-67183-SCXL-CS01-N
DRAWING NUMBER: 6820-R2-67183-02
REV.: 0

21 FEB 2025 04:49